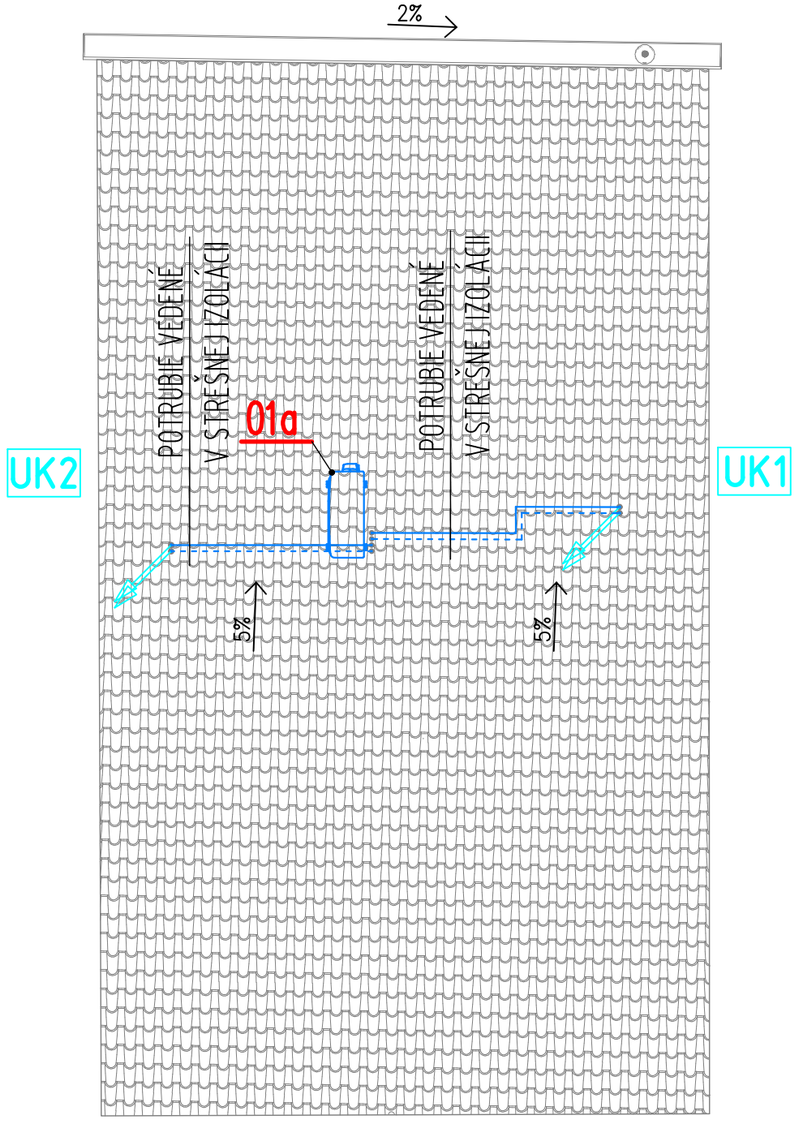


LEGENDA POTRUBIA:

PROJEKTOVANÉ MEDENÉ POTRUBIE

LEGENDA ZARIADENÍ A ARMATÚR:

01a	PROJEKTOVANÁ VONKJŠIA MULTI SPLIT JEDNOTKA, PRESNÝ TYP URČÍ ARCHITEKT MULTI SPLIT PRE NAPOJENIE 2 VNÚTORNÝCH JEDNOTIEK

POZNÁMKY:

- VŠETKY ROZMERY STAVEBNÝCH PRÁC KONTROLOVAŤ NA MIESTE STAVBY
- DOPORUČUJEM PREKÁBLOVANIE JEDNOTLIVÝCH TERMOSTATOV PODLAHOVÉHO VYKUROVANIA
- V PRÍPADE NEJASNOSTÍ VO VÝKRESOVEJ DOKUMENTÁCII KONTAKTOVAŤ ZODPOVEDNÉHO PROJEKTANTA S PRISLÚCHAJÚCOU REGULÁCIOU EŠTE PRED ZHOTOVENÍM OMIETOK
- DODÁVATEL STAVBY JE POVINNÝ REALIZOVAŤ VŠETKY PRÁCE V ZMYSLE PLATNÝCH STN EN S DODRŽANÍM TECHNOLOGICKÝCH A BEZPEČNOSTNÝCH POSTUPOV. ĎALEJ JE POVINNÝ REŠPEKTOVAŤ USTANOVENIA STN 730421 O PRÍSLUŠNÝCH ROZMEROVÝCH ODCHÝLKACH REALIZOVANÝCH KONŠTRUKCIÍ PROTI PROJEKTOVANÉMU STAVU. KAŽDÚ ODCHÝLKU OD PROJEKTU JE POTREBNÉ PREROKOVAŤ S GP.
- ±0,000 SA VZŤAHUJE K ÚROVNI FINÁLNEJ ÚPRAVY PODLAHY
- VÝBER VYKUROVACÍCH TELIES PODĽA INVESTORA

TABUĽKA REVÍZIÍ

ČÍSLO REVÍZIE	DÁTUM	POPIS ZMENY	VYPRACOVAL

0,000=256,300 m n. m.

AUTOR PROJEKTU:	Ing. arch. Ivor Mečiar, ArtD.
H.I.P.:	Ing. arch. Ivor Mečiar, ArtD.
ZODP. PROJEKTANT:	Ing. arch. Ivor Mečiar, ArtD.
VYPRACOVAL:	Bc. Viktor Labovský

GENERÁLNY PROJEKTANT:
Alla s.r.o.
Riazanská 70/683
831 02 Bratislava
tel.: +421 907 693 679
email: ateliar@alla.sk

INVESTOR: Haverčáková Viera r. Miznerová, Novohradská 1283/1, Bratislava

NÁZOV PROJEKTU: ZAHRADNA CHATKA ZLATÁ HORA

MIESTO STAVBY: Zlatá hora B, Stupava, p.č 5329/11

OBSAH VÝKRESU: **ÚK - Výkres strechy**

STAVEBNÝ OBJEKT: REKREAČNÁ ZÁHRADNÁ STAVBA

PEČIATKA:

PARÉ:

ČÍSLO VÝKRESU: 3

ID STAVBY:	STUPEŇ PD:	URČENIE STAVBY:	IDENTIFIK. : KÓD	ČLENENIE DOK.:	PROFESIE:	ČÍSLO VÝKRESU:	NÁZOV VÝKRESU:	REVÍZIA:

NÁZOV VÝKRESU V ELEKTRONICKEJ PODOBE:

DÁTUM: 05/2026

FORMÁT: 420 x 297mm

KÓD AKCIE:

MIERKA: 1:50