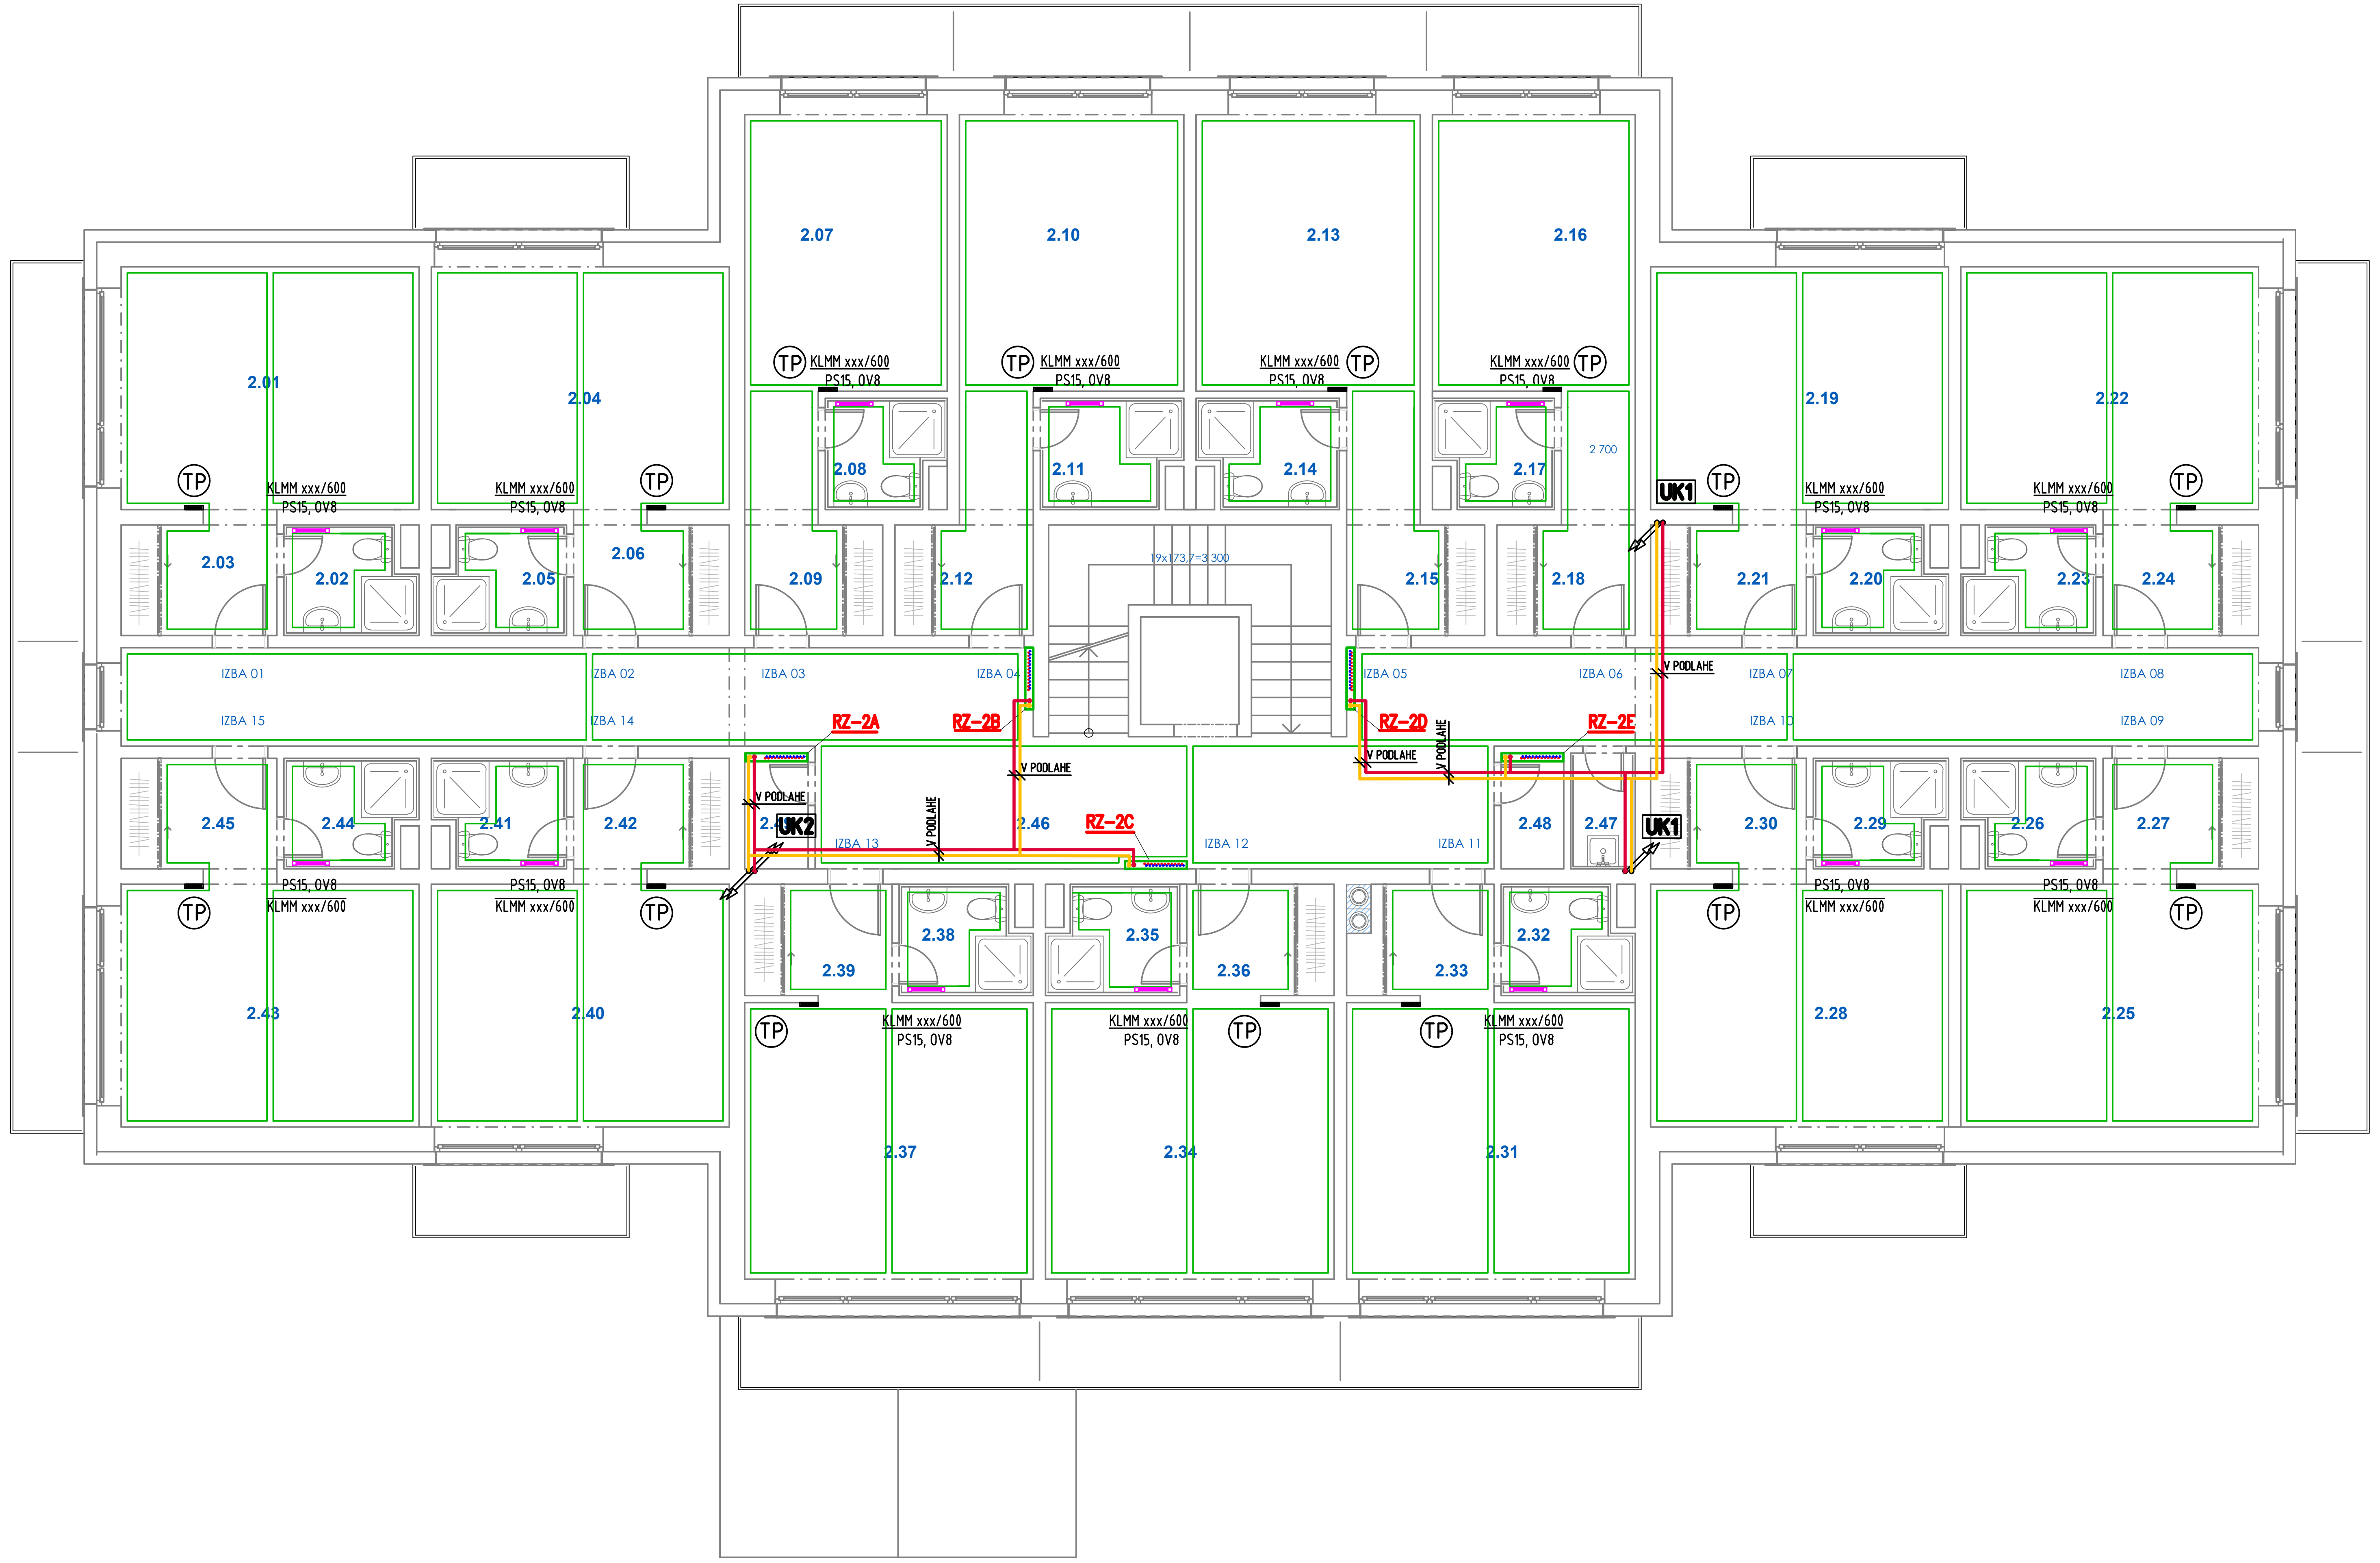

TABUĽKA MIESTNOSTÍ 2.NP			
Č.M.	NÁZOV MIESTNOSTI	PLOCHA (m2)	PODLAHA
2.01	IZBA	19,16	koberec
2.02	KÚPELŇA	3,64	ker. dlažba
2.03	PREDSIEŇ	4,56	koberec
2.04	IZBA	19,16	koberec
2.05	KÚPELŇA	3,64	ker. dlažba
2.06	PREDSIEŇ	4,56	koberec
2.07	IZBA	17,46	koberec
2.08	KÚPELŇA	3,27	ker. dlažba
2.09	PREDSIEŇ	4,05	koberec
2.10	IZBA	19,04	koberec
2.11	KÚPELŇA	3,91	ker. dlažba
2.12	PREDSIEŇ	4,05	koberec
2.13	IZBA	19,04	koberec
2.14	KÚPELŇA	3,91	ker. dlažba
2.15	PREDSIEŇ	4,05	koberec
2.16	IZBA	17,46	koberec
2.17	KÚPELŇA	3,27	ker. dlažba
2.18	PREDSIEŇ	4,05	koberec
2.19	IZBA	19,16	koberec
2.20	KÚPELŇA	3,64	ker. dlažba
2.21	PREDSIEŇ	4,56	koberec
2.22	IZBA	19,16	koberec
2.23	KÚPELŇA	3,64	ker. dlažba
2.24	PREDSIEŇ	4,56	koberec
2.25	IZBA	19,16	koberec
2.26	KÚPELŇA	3,64	ker. dlažba
2.27	PREDSIEŇ	4,56	koberec
2.28	IZBA	19,16	koberec
2.29	KÚPELŇA	3,64	ker. dlažba
2.30	PREDSIEŇ	4,56	koberec
2.31	IZBA	21,15	koberec
2.32	KÚPELŇA	3,63	ker. dlažba
2.33	PREDSIEŇ	4,02	koberec
2.34	IZBA	21,15	koberec
2.35	KÚPELŇA	3,63	ker. dlažba
2.36	PREDSIEŇ	4,34	koberec
2.37	IZBA	21,15	koberec
2.38	KÚPELŇA	3,63	ker. dlažba
2.39	PREDSIEŇ	4,34	koberec
2.40	IZBA	19,16	koberec
2.41	KÚPELŇA	3,64	ker. dlažba
2.42	PREDSIEŇ	4,56	koberec
2.43	IZBA	19,16	koberec
2.44	KÚPELŇA	3,64	ker. dlažba
2.45	PREDSIEŇ	4,56	koberec
2.46	CHODBA	70,54	koberec
2.47	EKONOMAT	1,98	ker. dlažba
2.48	SKLAD POUŽ. PRÁDLA	1,92	ker. dlažba
2.49	SKLAD ČISTÉHO PRÁDLA	1,95	ker. dlažba

DETAIL ZAPOJENIA VYKUROVACÍCH TELIES
REBRÍKOVÉ VYKUROVACIE TELESO

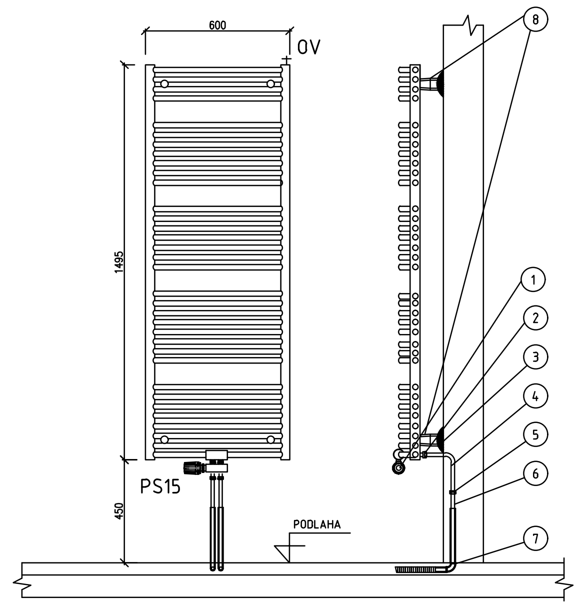

LEGENDA:

1. Stredové pripojenie vykurovacieho telesa, rozteč H=50mm rohové, farbia biela
2. Svorková spojka
3. Krycia rozeta
4. Pripojovacia garnitúra s upevňovacím
5. Násuvná objímka
6. Vykurovacia rúrka
7. Vodiaci oblúk 90°
8. Stenová konzola

LEGENDA PODLAHOVÉHO VYKUROVANIA:

▭

PODLAHOVÉ KÚRENIE REHAU

Rúrka RAUTHERM S 17x2,0	TYP VYKUROVACEJ RÚRKY
VARIONOVA	SYSTÉM PODLAHOVÉHO VYKUROVANIA

LEGENDA POTRUBIA:

POTRUBIE - PLASTHLINNÍKOVÁ RÚRKA NAPR. GEBERIT MEPLA
SPÁJANÉ LISOVANÍM, IZOLOVANÉ POTRUBIE, TEPLOTNÝ SPÁD 45/35°C
POTRUBIE VEDENÉ V PODLAHE, V ŠACHTE, PRE PODLAHOVÉ VYKUROVANIE, PRÍVOD A SPIATOČKA

PROJEKTOVANÉ POTRUBIE Z UŠĽACHTILEJ OCELE NAPR. GEBERIT MAPRESS
SPÁJANÉ LISOVANÍM, IZOLOVANÉ POTRUBIE, TEPLOTNÝ SPÁD 55/45°C
POTRUBIE VEDENÉ POD STROPOM, PRE OHREV VZT JEDNOTKY, PRÍVOD A SPIATOČKA

LEGENDA ZARIADENÍ A ARMATÚR :

PS	PRIPÁJACÍ BLOK S INTEGROVANÝM TERMOSTATICKÝM VENTILOM TYP BB PRE VYKUROVACIE TELESÁ SO STREDOVÝM PRIPOJENÍM, ROHOVÉ, DN15, PRIPOJENIE RADIÁTORA VONKAJŠÍ ZÁVIT 1/2", PRIPOJENIE DO STENY VONKAJŠÍ ZÁVIT 3/4" S TERMOSTATICKOU HLAVICOU NAPR. THERA-4 KLASIK S KVAPAL. SNÍMAČOM
GV	GUĽOVÝ VENTIL ZÁVITOVÝ
RV	PREDNASTAVITEĽNÝ REGULAČNÝ VENTIL PRIAMY - STAD
VK	VYPÚŠŤACÍ KOHÚT
OV	ODVZDUŠŇOVACÍ VENTIL
TP	PRIESTOROVÝ REGULÁTOR NEA SMART 2.0 PRE MERANIE TEPLOTY V MIESTNOSTI, FY. REHAU
UK1-5	STÚPAČKA VYKUROVANIA
UKVZT	STÚPAČKA VYKUROVANIA PRE OKRUH VZT ZARIADENÍ
RZ	ROZDELOVACIA STANICA PRE VYKUROVACIE TELESÁ A PODLAHOVĚ VYKUROVANIE

POZNÁMKA :

- V PRÍPADE NEJASNOSTÍ VO VÝKRESOVEJ DOKUMENTÁCIÍ KONTAKTOVAŤ ZODPOVEDNÉHO PROJEKTANTA
- VŠETKY ROZMERY STAVEBNÝCH PRÁC KONTROLOVAŤ NA MIESTE STAVBY
- PRED UVEDENÍM SYSTÉMU DO PREVÁDZKY JE POTREBNÉ VYKONAŤ DÔKLADNÝ PREPLACH SYSTÉMU S VYČISTENÍM VŠETKÝCH FILTROV NA ROZVODE
- PO NAPUSTENÍ SYSTÉMU JE POTREBNÉ VYKONAŤ JEHO ODVZDUŠNENIE
- DODÁVATEL STAVBY JE POVINNÝ REALIZOVAŤ VŠETKY PRÁCE V ZMYSLE PLATNÝCH STN EN S DODRŽANÍM TECHNOLOGICKÝCH A BEZPEČNOSTNÝCH POSTUPOV. ĎALEJ JE POVINNÝ REŠPEKTOVAŤ USTANOVENIÁ STN 730421 O PRÍSLUŠNÝCH ROZMEROVÝCH ODCHÝLKACH REALIZOVANÝCH KONŠTRUKCIÍ PROTI PROJEKTOVANÉMU STAVU. KAŽDÚ ODCHÝLKU OD PROJEKTU JE POTREBNÉ PREROKOVAŤ S GP.
- PRESTUPY INŽINIERSKYCH SIETÍ A ROZVODOV V OBJEKTE JE POTREBNÉ VYNECHAŤ PRI REALIZÁCII STAVBY.
- PROJEKTOVÁ DOKUMENTÁCIA JE SPRACOVANÁ PRE ÚČEL VYDANIA STAVEBNÉHO POVOLENIA A NENAHRÁDZA REALIZAČNÝ PROJEKT

OBJEDNÁV
O&L, s.r.o., Št
058 01 Poprac

STUPEŇ PD
DSP

DATUM SPR
03/2025