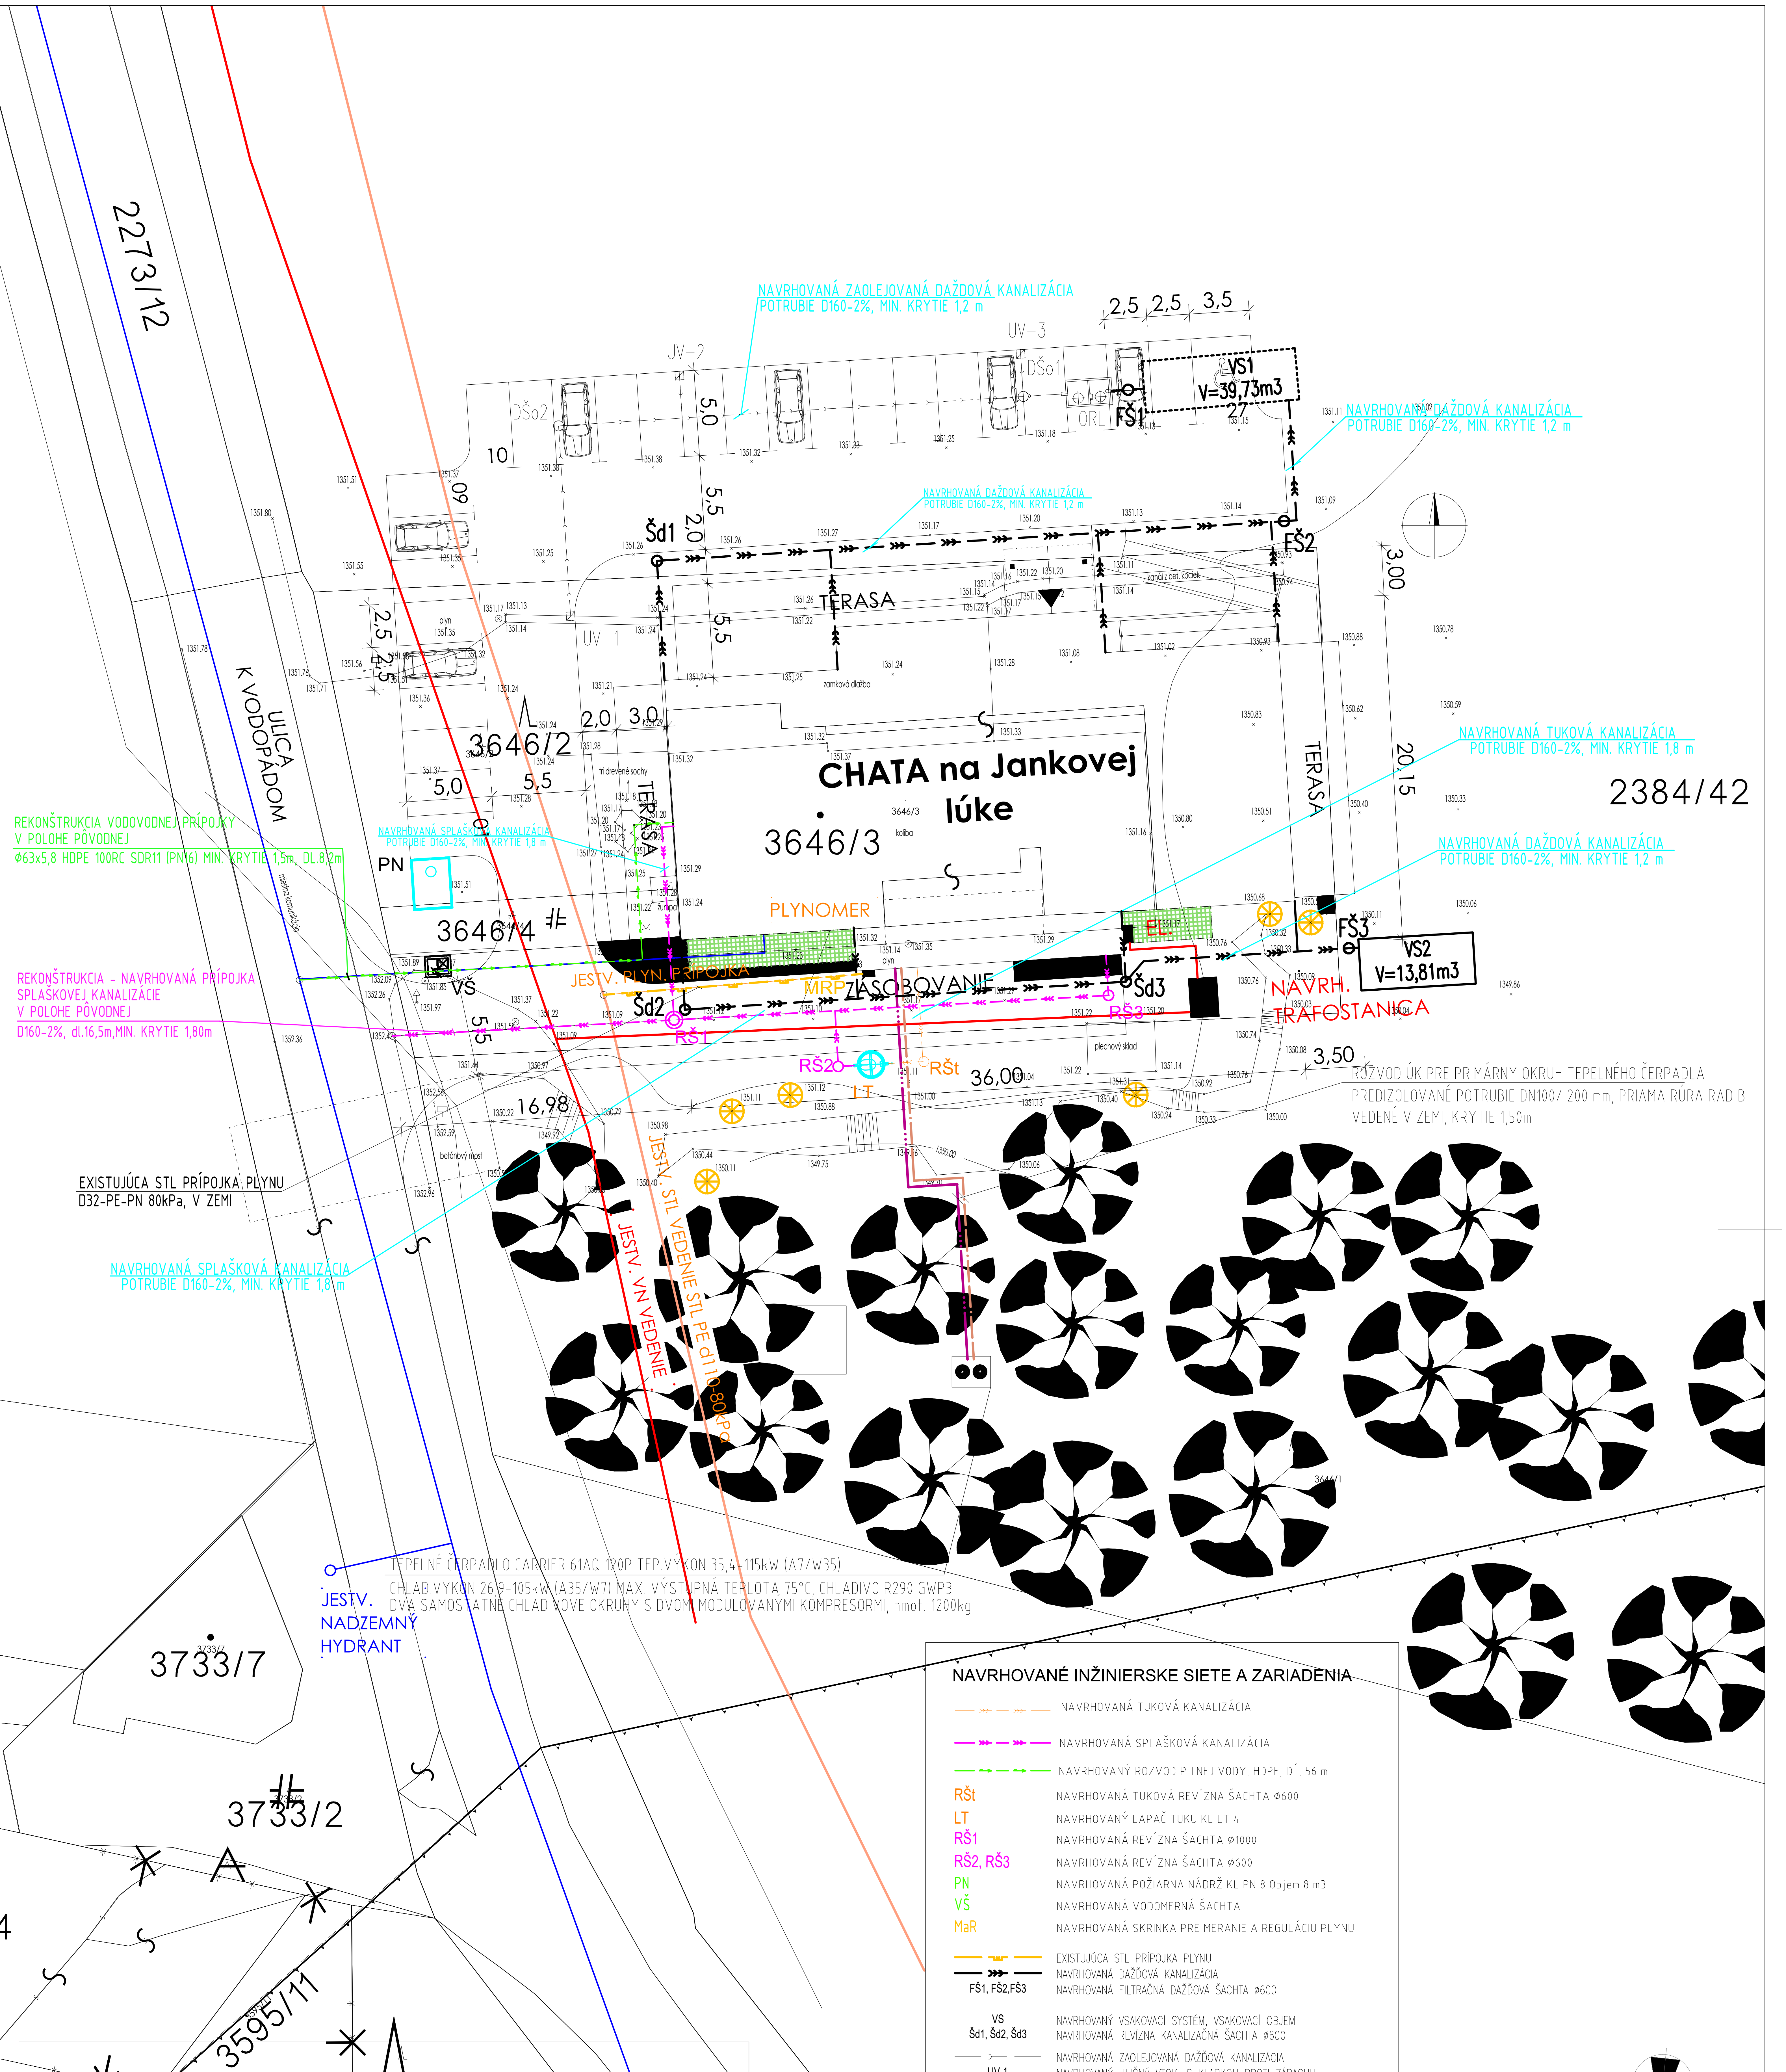
2273/12
NAVRHOVANÁ ZAOLEJOVANÁ DAŽDOVÁ KANALIZÁCIA
POTRUBIE D160-2%, MIN. KRYTIE 1,2 m
UV-2
UV-3
2,5
2,5
3,5
DŠo2
DŠo1
ORL
VS1
V=39,73m3
FŠ1
27
NAVRHOVANÁ DAŽDOVÁ KANALIZÁCIA
POTRUBIE D160-2%, MIN. KRYTIE 1,2 m
10
5,0
5,5
2,0
09
Šd1
NAVRHOVANÁ DAŽDOVÁ KANALIZÁCIA
POTRUBIE D160-2%, MIN. KRYTIE 1,2 m
FŠ2
3,00
TERASA
kanál z bet. kociek
UV-1
5,5
zamková dlažba
plyn
2,5
2,5
ULICA K VODOPÁDOM
miestna komunikácia
3646/2
2,0
3,0
5,0
5,5
tri drevené sochy
TERASA
CHATA na Jankovej lúke
3646/3
koliba
TERASA
20,15
2384/42
NAVRHOVANÁ TUKOVÁ KANALIZÁCIA
POTRUBIE D160-2%, MIN. KRYTIE 1,8 m
NAVRHOVANÁ DAŽDOVÁ KANALIZÁCIA
POTRUBIE D160-2%, MIN. KRYTIE 1,2 m
REKONŠTRUKCIA VODOVODNEJ PRÍPOJKY
V POLOHE PÔVODNEJ
Ø63x5,8 HDPE 100RC SDR11 (PN16) MIN. KRYTIE 1,5m, DL.8,2m
NAVRHOVANÁ SPLAŠKOVÁ KANALIZÁCIA
POTRUBIE D160-2%, MIN. KRYTIE 1,8 m
PN
žumpa
3646/4
PLYNOMER
EL.
FŠ3
VS2
V=13,81m3
REKONŠTRUKCIA - NAVRHOVANÁ PRÍPOJKA
SPLAŠKOVEJ KANALIZÁCIE
V POLOHE PÔVODNEJ
D160-2%, dl.16,5m,MIN. KRYTIE 1,80m
VŠ
JESTV. PLYN. PRÍPOJKA
MRP
ZÁSOBOVANIE
Šd3
Šd2
RŠ3
RŠ1
NAVRH. TRAFOSTANICA
plechový sklad
5,5
RŠ2
LT
RŠt
36,00
3,50
ROZVOD ÚK PRE PRIMÁRNY OKRUH TEPELNÉHO ČERPADLA
PREDIZOLOVANÉ POTRUBIE DN100/ 200 mm, PRIAMA RÚRA RAD B
VEDENÉ V ZEMI, KRYTIE 1,50m
16,98
betónový most
EXISTUJÚCA STL PRÍPOJKA PLYNU
D32-PE-PN 80kPa, V ZEMI
NAVRHOVANÁ SPLAŠKOVÁ KANALIZÁCIA
POTRUBIE D160-2%, MIN. KRYTIE 1,8 m
JESTV. STL VEDENIE STL PE d110 80kPa
JESTV. VN VEDENIE
TEPELNÉ ČERPADLO CARRIER 61AQ 120P TEP.VÝKON 35,4-115kW (A7/W35)
CHLAD.VÝKON 26,9-105kW (A35/W7) MAX. VÝSTUPNÁ TEPLOTA 75°C, CHLADIVO R290 GWP3
DVA SAMOSTATNÉ CHLADIVOVÉ OKRUHY S DVOMI MODULOVANÝMI KOMPRESORMI, hmot. 1200kg
JESTV. NADZEMNÝ HYDRANT
3733/7
3733/2
3595/11
3595/12
3646/1

NAVRHOVANÉ INŽINIERSKE SIETE A ZARIADENIA

—»»—»»—	NAVRHOVANÁ TUKOVÁ KANALIZÁCIA
—»»—»»—	NAVRHOVANÁ SPLAŠKOVÁ KANALIZÁCIA
—→—→—	NAVRHOVANÝ ROZVOD PITNEJ VODY, HDPE, DĹ, 56 m
RŠt	NAVRHOVANÁ TUKOVÁ REVÍZNA ŠACHTA ø600
LT	NAVRHOVANÝ LAPAČ TUKU KL LT 4
RŠ1	NAVRHOVANÁ REVÍZNA ŠACHTA ø1000
RŠ2, RŠ3	NAVRHOVANÁ REVÍZNA ŠACHTA ø600
PN	NAVRHOVANÁ POŽIARNA NÁDRŽ KL PN 8 Objem 8 m3
VŠ	NAVRHOVANÁ VODOMERNÁ ŠACHTA
MaR	NAVRHOVANÁ SKRINKA PRE MERANIE A REGULÁCIU PLYNU
— — —	EXISTUJÚCA STL PRÍPOJKA PLYNU
—»»—	NAVRHOVANÁ DAŽĎOVÁ KANALIZÁCIA
FŠ1, FŠ2,FŠ3	NAVRHOVANÁ FILTRAČNÁ DAŽĎOVÁ ŠACHTA ø600
VS	NAVRHOVANÝ VSAKOVACÍ SYSTÉM, VSAKOVACÍ OBJEM
Šd1, Šd2, Šd3	NAVRHOVANÁ REVÍZNA KANALIZAČNÁ ŠACHTA ø600
—›—	NAVRHOVANÁ ZAOLEJOVANÁ DAŽĎOVÁ KANALIZÁCIA
UV-1	NAVRHOVANÝ ULIČNÝ VTOK, S KLAPKOU PROTI ZÁPACHU
DŠ01	NAVRHOVANÁ ZAOLEJOVANÁ REVÍZNA ŠACHTA ø600
ORL	NAVRHOVANÝ ODLUČOVAČ ROPNÝCH LÁTOK typ Klartec KL 15/1 sll

POZNÁMKY

- priebeh inžinierskych podzemných sietí bol zakreslený informatívne, pred začatím výkopových prác je nutné ich vytýčenie
- pred začatím každého výkopu, vrtu, alebo sondy je potrebné zrealizovať fyzické vytýčenie každého podzemného objektu jeho majiteľom, správcom alebo prevádzkovateľom
- pred realizáciou každého napojenia na inžinierske siete je potrebné pred začatím prác najskôr odhaliť a premerať bod napojenia
- pri realizácii a križovaní vedení musia byť dodržané dotknuté ustanovenia STN, ON a technologických predpisov
- pri realizácii jednotlivých vedení treba dodržať STN 73 6005 - Priestorová úprava vedení technického vybavenia
- projektant nenesie žiadnu zodpovednosť za zmeny uskutočnené bez jeho písomného súhlasu
- zhotoviteľ je povinný o zistených nezrovnalostiach v projektovej dokumentácii neodkladne informovať projektanta
- rozdiely zistené na stavbe oproti PD je nutné v technickom riešení odsúhlasiť s projektantom ešte pred samotnou realizáciou
- obsah výkresu je duševným vlastníctvom autorov a jeho použitie na iný účel podlieha autorskému zákonu

OBJEDNÁV

STUPEŇ PD:
DSP

DATUM SPR
03/2025