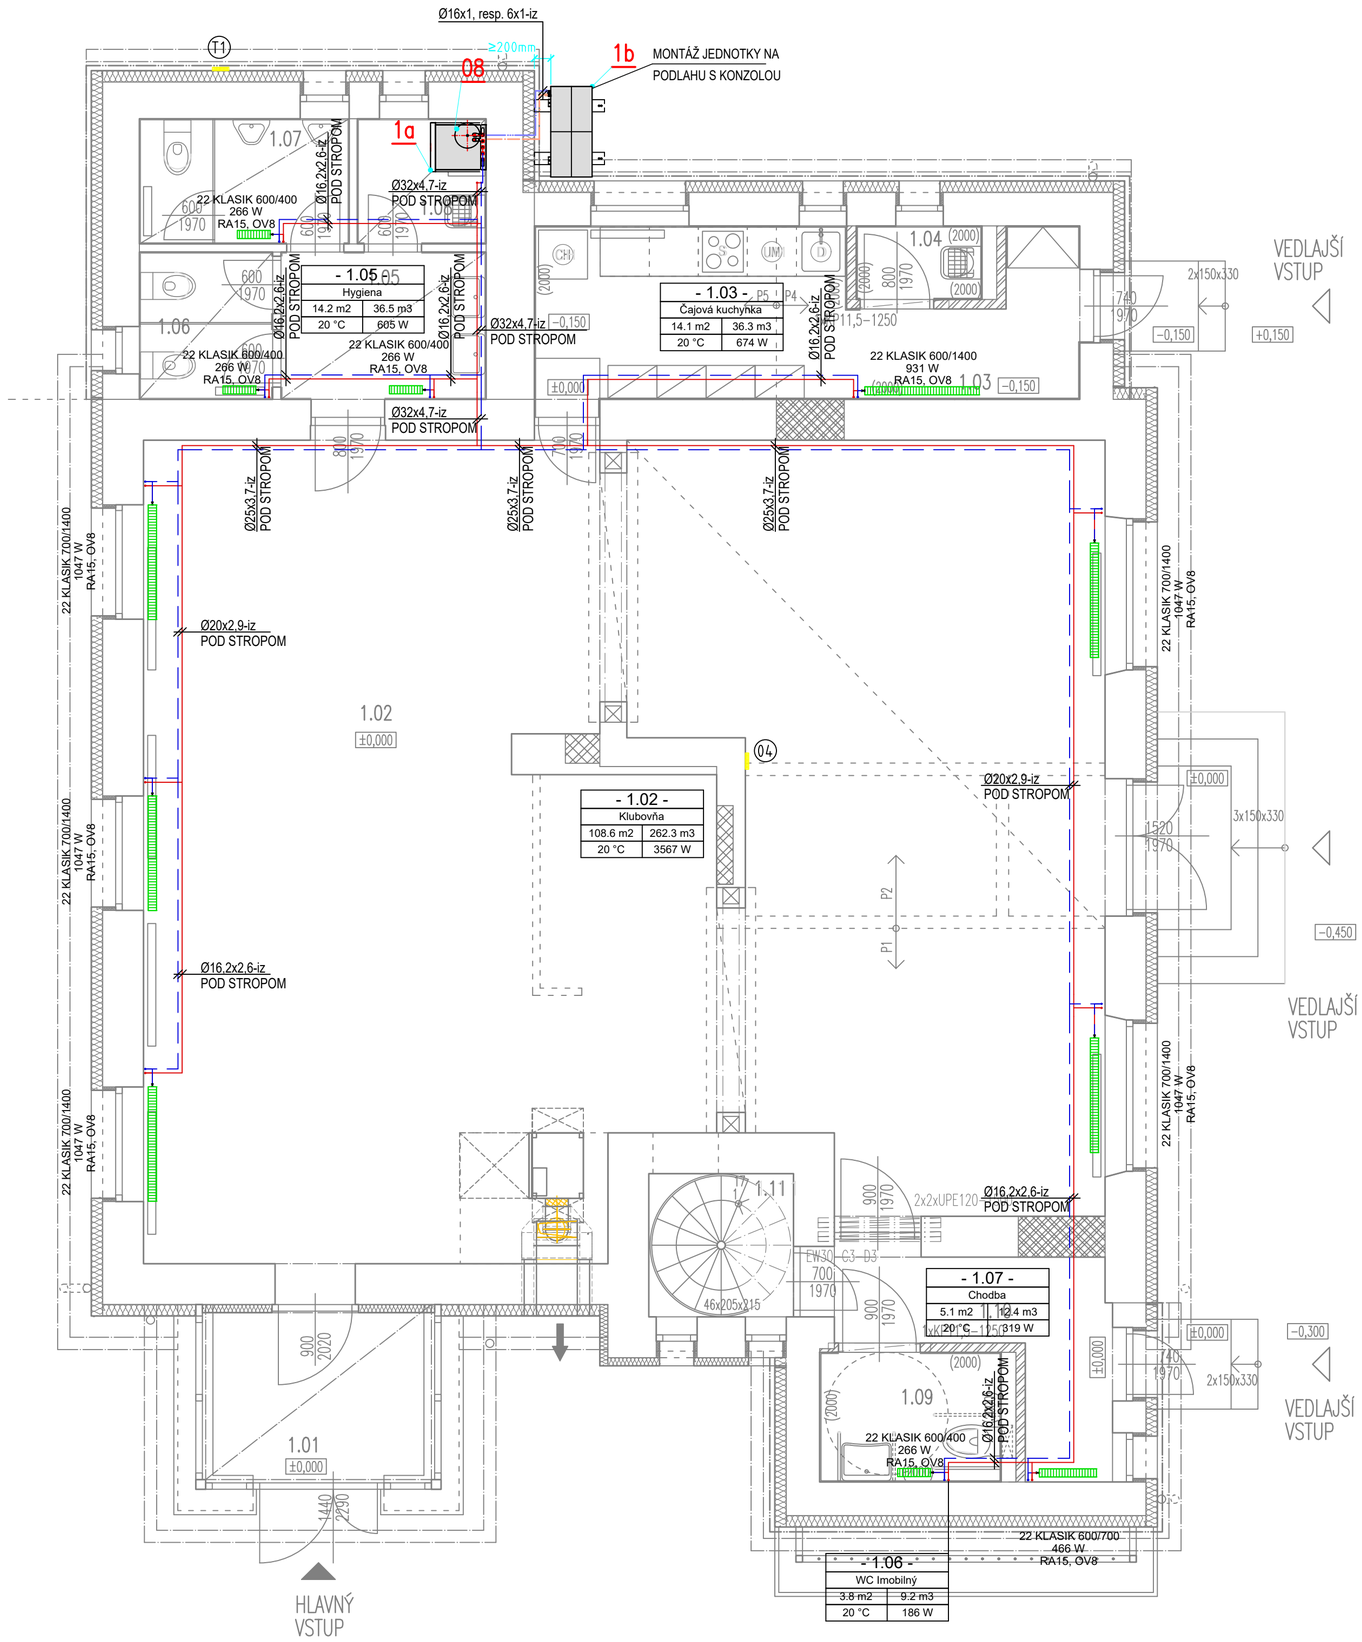


LEGENDA MIESTNOSTÍ:

ČÍSLO MIEST.	MIESTNOSŤ	PLOCHA M2	POD-LAHA	PODLAHA / SOKEL	STROP / STENY
1.01	ZÁDVERIE	5,18	P1	KERAMICKÁ DLAŽBA KERAMICKÝ SOKEL, V=100MM	SADROKARTÓNOVÝ PODHLAD KAZETOVÝ VNÚTORNÁ OMIETKA + VNÚTORNÁ FARBA BIELA KONTAKTNÝ ZATEPLOVACÍ SYSTÉM
1.02	KLUBOVŇA	109,80	P1,P2	KERAMICKÁ DLAŽBA PROTIŠMYKOVÁ KERAMICKÝ SOKEL, V=100MM	SADROKARTÓNOVÝ PODHLAD + MALBA (BIELA) VNÚTORNÁ OMIETKA + VNÚTORNÁ FARBA BIELA VNÚTORNÁ OMIETKA + VNÚTORNÁ FARBA BIELA
1.03	ČAJOVÁ KUCHYNKA	12,16	P4,P5	KERAMICKÁ DLAŽBA PROTIŠMYKOVÁ –	SADROKARTÓNOVÝ PODHLAD + MALBA (BIELA) VNÚTORNÁ OMIETKA + VNÚTORNÁ FARBA BIELA KERAMICKÝ OBKLAD, V=2,0m VNÚTORNÁ OMIETKA + VNÚTORNÁ FARBA BIELA
1.04	UPRATOVACIA MIESTNOSŤ	1,39	P4	KERAMICKÁ DLAŽBA PROTIŠMYKOVÁ –	SADROKARTÓNOVÝ PODHLAD + MALBA (BIELA) VNÚTORNÁ OMIETKA + VNÚTORNÁ FARBA BIELA KERAMICKÝ OBKLAD, V=2,0m VNÚTORNÁ OMIETKA + VNÚTORNÁ FARBA BIELA
1.05	PREDSIEŇ WC	4,52	P1	KERAMICKÁ DLAŽBA –	SADROKARTÓNOVÝ PODHLAD KAZETOVÝ KERAMICKÝ OBKLAD, V=PO STROP
1.06	WC ŽENY	2,93	P1	KERAMICKÁ DLAŽBA –	SADROKARTÓNOVÝ PODHLAD KAZETOVÝ KERAMICKÝ OBKLAD, V=PO STROP
1.07	WC MUŽI	3,92	P1	KERAMICKÁ DLAŽBA –	SADROKARTÓNOVÝ PODHLAD KAZETOVÝ KERAMICKÝ OBKLAD, V=PO STROP
1.08	TECHNICKÁ MIESTNOSŤ +UPRATOVACIA MIESTNOSŤ	2,41	P1	KERAMICKÁ DLAŽBA –	SADROKARTÓNOVÝ PODHLAD KAZETOVÝ KERAMICKÝ OBKLAD, V=PO STROP
1.09	WC IMOBILNÍ	3,52	P1	KERAMICKÁ DLAŽBA PROTIŠMYKOVÁ –	SADROKARTÓNOVÝ PODHLAD + MALBA (BIELA) VNÚTORNÁ OMIETKA + VNÚTORNÁ FARBA BIELA KERAMICKÝ OBKLAD, V=2,0m VNÚTORNÁ OMIETKA + VNÚTORNÁ FARBA BIELA
1.10	CHODBA	5,33	P1	KERAMICKÁ DLAŽBA PROTIŠMYKOVÁ KERAMICKÝ SOKEL, V=100MM	SADROKARTÓNOVÝ PODHLAD + MALBA (BIELA) VNÚTORNÁ OMIETKA + VNÚTORNÁ FARBA BIELA KERAMICKÝ OBKLAD, V=2,0m VNÚTORNÁ OMIETKA + VNÚTORNÁ FARBA BIELA
1.11	SCHODISKO	3,10	P1,P3	KERAMICKÁ DLAŽBA PROTIŠMYKOVÁ KERAMICKÝ SOKEL, V=100MM	– VNÚTORNÁ OMIETKA + VNÚTORNÁ FARBA BIELA
	1.NP SPOLU	154,26			

LEGENDA VYKUROVACÍCH TELIES:

SPÔSOB ZNAČENIA — OCEĽOVÉ DOSKOVÉ VYKUROVACIE TELESO KLASIK, TYP KLASIK, S BOČNÝM PRIPOJENÍM

22 KLASIK 600/1200
- 22 — TYP DVOJRADOVÝ
- KLASIK — PREVEDENIE KLASIK - S BOČNÝM PRIPOJENÍM
- 600 — STAVEBNÁ VÝŠKA V MILIMETROCH
- 1200 — STAVEBNÁ DĹŽKA V MILIMETROCH

LEGENDA POTRUBIA:

- POTRUBIE - PLASTHLINNÍKOVÁ RÚRKA RAUTITAN STABIL, fy. REHAU
  PRE OKRUHY KONVEKČNÉHO VYKUROVANIA, TEPLOTNÝ SPÁD 50/40°C, PRÍVOD A SPATOČKA
- ROZVOD ÚK PRE PRIMÁRNY OKRUH TEPELNÉHO ČERPADLA
  MATERIÁL MEĎ


LEGENDA ZARIADENÍ A ARMATÚR :

1a	KOMPAKTNÁ VNÚTORNÁ JEDNOTKA TEPELNÉHO ČERPADLA VITOCAL 222-S AWBT-M-E 221.E06
1b	VONKAJ.JEDNOTKA VITOCAL 222-S AWBT-M-E 221.E06 (230V) MAX.VÝSTUPNÁ TEPLOTA 60°C,TEPELNY VYKON 2,6-7,5kW A7/W35 EKOLOGICKE CHLADIVO R32, REGULÁCIA ONE-BASE,WIFI (Z022722)
04	BEZDRÔTOVÉ DIAĽKOVÉ OVLÁDANIE VITOTROL 300-E
08	UZAVRETÁ TLAKOVÁ EXPANZNÁ NÁDOBA VIESSMANN N25 OBJEM 25L, 3bar ROZMERY : Ø=308 mm, VÝŠKA 477 mm , HMOTNOSŤ 4,3 kg + NASTENNY DRZIAK PRE N25 (9572216)
T1	SNÍMAČ VONKAJŠEJ TEPLOTY
RA	RADIATOROVÝ VENTIL NAPR. VERAFIX-VKE, UZATVÁRACIE ŠRÓBENIE H-BLOK S VONKAJŠÍM ZÁVITOM EUROKONUS PRE VYKUROVACIE TELESÁ TYPU VENTIL-KOMPAKT, ROHOVÝ, DN15 PRIPOJENIE RADIÁTORA VONKAJŠÍ ZÁVIT 1/2", PRIPOJENIE RÚRKY VONKAJŠÍ ZÁVIT 3/4" TERMOSTATICKÁ HLAVICA SO VSTAVANÝM KVAPALINOVÝM SNÍMAČOM, ROZSAH 6-28°C
OV	ODVZDUŠŇOVACÍ VENTIL , PN 16/120°C

POZNÁMKA :

- V PRÍPADE NEJASNOSTÍ VO VÝKRESOVEJ DOKUMENTÁCII KONTAKTOVAŤ ZODPOVEDNÉHO PROJEKTANTA
- VŠETKY ROZMERY STAVEBNÝCH PRÁC KONTROLOVAŤ NA MIESTE STAVBY
- PRED UVEDENÍM SYSTÉMU DO PREVÁDZKY JE POTREBNÉ VYKONAŤ DÔKLADNÝ PREPLACH SYSTÉMU S VYČISTENÍM VŠETKÝCH FILTROV NA ROZVODE
- PO NAPUSTENÍ SYSTÉMU JE POTREBNÉ VYKONAŤ JEHO ODVZDUŠNENIE
- DODÁVATEL STAVBY JE POVINNÝ REALIZOVAŤ VŠETKY PRÁCE V ZMYSLE PLATNÝCH STN EN S DODRŽANÍM TECHNOLOGICKÝCH A BEZPEČNOSTNÝCH POSTUPOV. ĎALEJ JE POVINNÝ REŠPEKTOVAŤ USTANOVENIÁ STN 730421 O PRÍSLUŠNÝCH ROZMEROVÝCH ODCHÝLKACH REALIZOVANÝCH KONŠTRUKCIÍ PROTI PROJEKTOVANÉMU STAVU. KAŽDÚ ODCHÝLKU OD PROJEKTU JE POTREBNÉ PREROKOVAŤ S GP.

DETAIL OSADENIA VONKAJŠEJ JEDNOTKY NA STENE NA KONZOLE

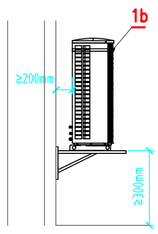

Autorom projektu a výhradným vlastníkom autorských a majetkových práv je spoločnosť M PRO s.r.o, Ing. Andrej Marcík. Projektová dokumentácia, ako aj samotné architektonické dielo podlieha autorskej ochrane podľa zákona 185/2015 Z. z. - Autorský zákon v znení neskorších predpisov. Vyhotovenie napodobenín, rozmnožovanie a akékoľvek úpravy bez písomného súhlasu autora je trestné.

Výškové osadenie: ±0,000= 130,875 m.n.m. (BPV)
Súradnicový systém: JTSK

Orientácia na svetové strany:

Generálny projektant: **M PRO s.r.o.**
Kadnárova 23, 831 52 Bratislava
mprosro@gmail.com +421 905 489 533
Ing. Andej Marcík

Projektant časti: **JOPRO group s.r.o.**
Trnavská cesta 67, 821 04 Bratislava
jokay@jopro.sk +421 905 549 978
Ing. Norbert Jókay

Autor/Spoluautor:
Ing. Andrej Marcík
Ing. Daniela Marcíková
Ing. Miroslav Greguš
Ing.Ing.arch.Mgr.art.J.Kuráň,PhD.

Zodpovedný projektant:
Ing. Norbert Jókay

Vypracoval:
Bc. Viktor Labovský

Názov projektu / stavby:

OBECNÝ DOM LIMBACH