- 1.02 -	
TZB + Toaleta	
12.7 m2	36.8 m3
20 °C	292 W

- 1.01 -	
Chodba	
18.8 m2	54.5 m3
22 °C	401 W

- 1.06 -	
Hygiena 2	
5.4 m2	15.8 m3
24 °C	244 W

- 1.03 -	
Spalňa	
19.8 m2	57.5 m3
22 °C	885 W

- 1.08 -	
Obývačka + kuhcyna	
46.4 m2	105.9 m3
22 °C	2637 W

- 1.04 -	
Hygiena 1	
6.9 m2	20.0 m3
24 °C	413 W

- 1.05 -	
Izba	
10.6 m2	30.6 m3
22 °C	576 W

LEGENDA MIESTNOSTÍ 1.PP

ČÍSLO	MIESTNOSŤ	M²
01.01	CHODBA	16,6
01.02	TOALETA + TZB	8,95
01.03	SPAĽŇA	19,84
01.04	HYGIENA	6,88
01.05	IZBA	10,56
01.06	HYGIENA	5,44
01.07	ŠPAJZA	2,88
01.08	HLAVNÝ OBYTNÝ PRIESTOR	46,36

ÚŽITKOVÁ PLOCHA 1.PP
CELKOVÁ ÚŽITKOVÁ PLOCHA OBJEKTU

LEGENDA PODLAHOVÉHO VYKUROVANIA:

PODLAHOVÉ KÚRENIE REHAU

Lpz=100 [mm]
S=8,6 m2
PZ: Keramická dlažba
Rúrka RAUTHERM S 17x2,0
Nast.=0,63 (48 kg/h)
lo/lp=12.7 m/1.6 m
RZ 1.
VARIONOVA

ROZOSTUP VYK. RÚROK
VYKUROVACIA PLOCHA
TYP NÁŠLAPNEJ VRSTVY
TYP VYKUROVACEJ RÚRKY
NASTAVENIE REG. OKRUHU(PRIETOK)
Dĺžka okruhu / dĺžka prípojky
rozdelovač na 1.NP 1. napojenie a
9 vetiev (tp - teplota prívodu)
typ prichytenia potrubi pre podlahove kurenie
maximálna povrchová teplota podlahovej zóny

LEGENDA POTRUBIA:

POTRUBIE - PLASTHLINNÍKOVÁ RURKA PE-Xa/AL/PE napr. RAUTITAN Stabil REHAU
SPÁJANÉ LISOVANÍM, IZOLOVANÉ POTRUBIE, TEPLOTNÝ SPÁD 45/35°C. PRE PODLAHOVÉ VYKUROVANIE

POTRUBIE - PLASTHLINNÍKOVÁ RÚRKA NAPR. GEBERIT MEPLA
SPÁJANÉ LISOVANÍM, IZOLOVANÉ POTRUBIE, TEPLOTNÝ SPÁD 45/35°C

ROZVOD ÚK PRE PRIMÁRNY OKRUH TEPELNÉHO ČERPADLA
PRE OKRUHY KONVEKČNÉHO VYKUROVANIA, PRÍVOD A SPATOČKA
MATERIÁL MEĎ

LEGENDA VYKUROVACÍCH TELIES:

EL2 - ELEKTRICKÝ REBRÍKOVÝ RADIÁTOR (MIN. VÝKON 300W), PRESNÝ TYP URČÍ ARCHITEKT

LEGENDA VYKUROVACÍCH TELIES:

ST01 - ELEKTRICKÉ SÁLAVÉ PANELY (MIN. VÝKON 300W), PRESNÝ TYP URČÍ ARCHITEKT
ST02 - ELEKTRICKÉ SÁLAVÉ PANELY (MIN. VÝKON 300W), PRESNÝ TYP URČÍ ARCHITEKT
ST03 - ELEKTRICKÉ SÁLAVÉ PANELY (MIN. VÝKON 750W), PRESNÝ TYP URČÍ ARCHITEKT
ST04 - ELEKTRICKÉ SÁLAVÉ PANELY (MIN. VÝKON 750W), PRESNÝ TYP URČÍ ARCHITEKT


RZ 1 - 1.PP (11/1) (tp=45.0°C)	1.02 - TZB + Toaleta
PZ 1: Keramická dlažba	VYK: PZ:31.4°C
Systém VARIONOVA	Rúrka RAUTHERM S 17x2,0
lo/lp=39.8 m/2.6 m	S=4.0 m2
Lpz=100 [mm]	VYK: 0.9 l/min

RZ 1 - 1.PP (11/2) (tp=45.0°C)	1.01 - Chodba
PZ 1: Keramická dlažba	VYK: PZ:27.9°C
Systém VARIONOVA	Rúrka RAUTHERM S 17x2,0
lo/lp=56.4 m/8.6 m	S=8.5 m2
Lpz=150 [mm]	VYK: 1.2 l/min

RZ 1 - 1.PP (11/3) (tp=45.0°C)	1.06 - Hygiena 2
PZ 1: Keramická dlažba	VYK: PZ:32.8°C
Systém VARIONOVA	Rúrka RAUTHERM S 17x2,0
lo/lp=32.0 m/30.4 m	S=3.2 m2
Lpz=100 [mm]	VYK: 0.7 l/min

RZ 1 - 1.PP (11/4) (tp=45.0°C)	1.08 - Obývačka + kuhcyna
PZ 1: Drevené parkety	VYK: PZ:24.8°C
Systém VARIONOVA	Rúrka RAUTHERM S 17x2,0
lo/lp=62.1 m/23.0 m	S=9.3 m2
Lpz=150 [mm]	VYK: 0.6 l/min

RZ 1 - 1.PP (11/5) (tp=45.0°C)	1.08 - Obývačka + kuhcyna
PZ 1: Drevené parkety	VYK: PZ:24.2°C [OZ:24.2°C]
Systém VARIONOVA	Rúrka RAUTHERM S 17x2,0
lo/lp=63.6 m/32.6 m	S=9.5 m2
Lpz/Loz=150/150 [mm]	VYK: 0.4 l/min

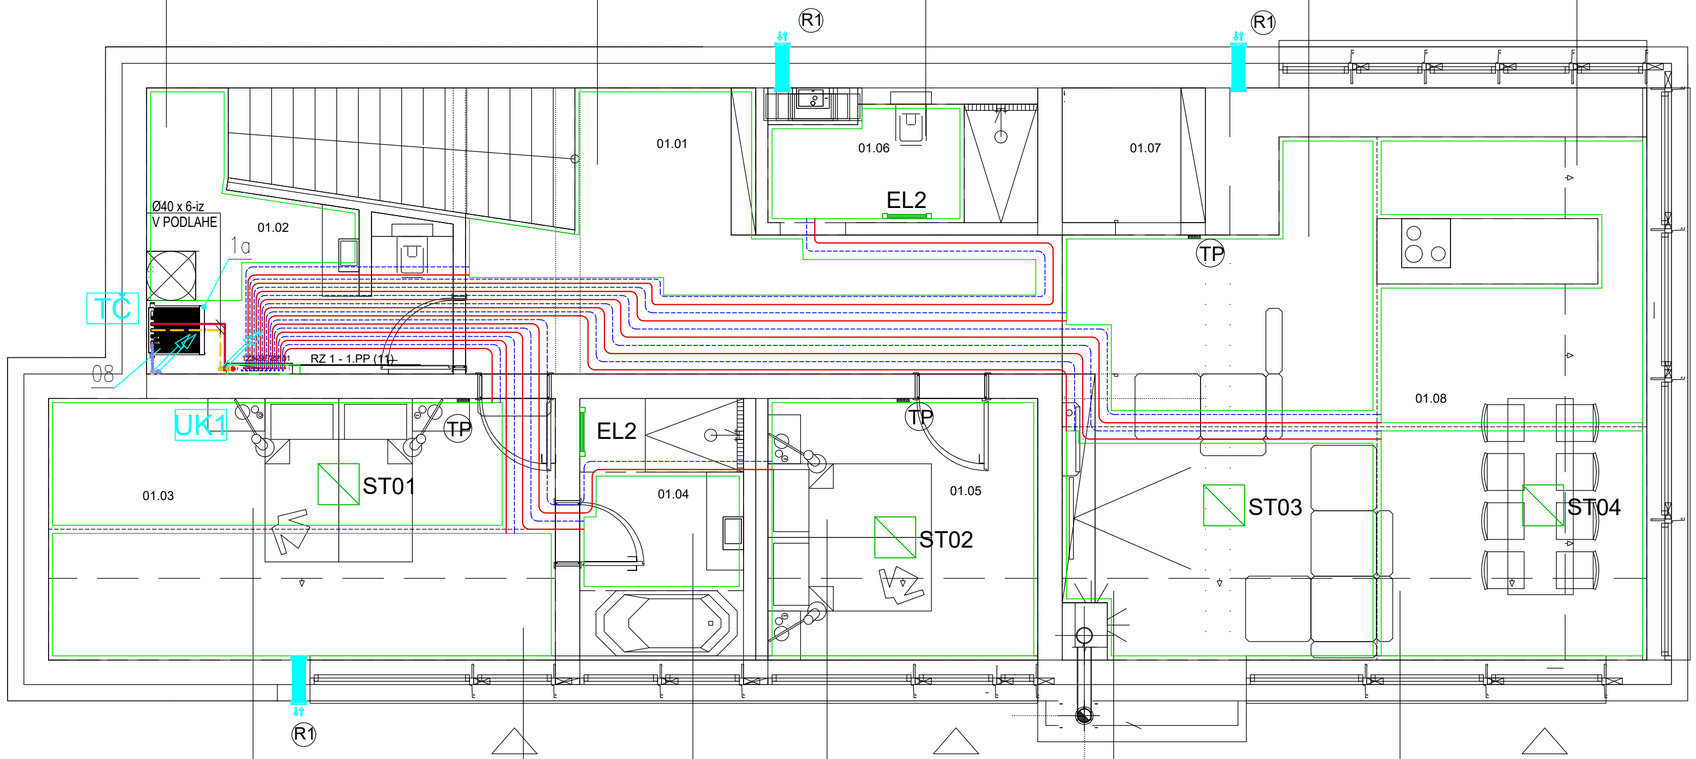

RZ 1 - 1.PP (11/11) (tp=45.0°C)	1.03 - Spalňa
PZ 1: Drevené parkety	VYK: PZ:25.4°C
Systém VARIONOVA	Rúrka RAUTHERM S 17x2,0
lo/lp=89.6 m/7.8 m	S=9.0 m2
Lpz=100 [mm]	VYK: 0.8 l/min

RZ 1 - 1.PP (11/10) (tp=45.0°C)	1.03 - Spalňa
PZ 1: Drevené parkety	VYK: PZ:24.8°C [OZ:24.8°C]
Systém VARIONOVA	Rúrka RAUTHERM S 17x2,0
lo/lp=99.2 m/11.8 m	S=9.9 m2
Lpz/Loz=100/100 [mm]	VYK: 0.4 l/min

RZ 1 - 1.PP (11/9) (tp=45.0°C)	1.04 - Hygiena 1
PZ 1: Keramická dlažba	VYK: PZ:34.0°C
Systém VARIONOVA	Rúrka RAUTHERM S 17x2,0
lo/lp=28.2 m/13.8 m	S=2.8 m2
Lpz=100 [mm]	VYK: 0.8 l/min

RZ 1 - 1.PP (11/8) (tp=45.0°C)	1.05 - Izba
PZ 1: Drevené parkety	VYK: PZ:24.8°C [OZ:25.3°C]
Systém VARIONOVA	Rúrka RAUTHERM S 17x2,0
lo/lp=81.4 m/19.5 m	S=10.6 m2
Lpz/Loz=150/100 [mm]	VYK: 0.8 l/min

RZ 1 - 1.PP (11/7) (tp=45.0°C)	1.08 - Obývačka + kuhcyna
PZ 1: Drevené parkety	VYK: PZ:24.2°C [OZ:24.6°C]
Systém VARIONOVA	Rúrka RAUTHERM S 17x2,0
lo/lp=78.6 m/24.4 m	S=10.1 m2
Lpz/Loz=150/100 [mm]	VYK: 0.4 l/min

RZ 1 - 1.PP (11/6) (tp=45.0°C)	1.08 - Obývačka + kuhcyna
PZ 1: Drevené parkety	VYK: PZ:24.3°C [OZ:24.6°C]
Systém VARIONOVA	Rúrka RAUTHERM S 17x2,0
lo/lp=83.3 m/32.5 m	S=9.4 m2
Lpz/Loz=150/100 [mm]	VYK: 0.4 l/min

LEGENDA ZARIADENÍ A ARMATÚR :

1a KOMPAKTNÁ VNÚTORNÁ JEDNOTKA TEPELNÉHO ČERPADLA VITOCAL 222-S AWBT-M-E 221.E06
1b VONKAJ.JEDNOTKA VITOCAL 222-S AWBT-M-E 221.E06 (230V)
MAX.VÝSTUPNÁ TEPLOTA 60°C,TEPELNY VYKON 2,6-7,5kW A7/W35
EKOLOGICKE CHLADIVO R32, REGULÁCIA ONE-BASE,WIFI (Z022722)
04 BEZDRÔDOTVÉ DIAĽKOVÉ OVLÁDANIE VITOTROL 300-E
08 UZAVRETÁ TLAKOVÁ EXPANZNÁ NÁDOBA VIESSMANN N25 OBJEM 25L, 3bar
ROZMERY : Ø=308 mm, VÝŠKA 477 mm , HMOTNOSŤ 4,3 kg + NASTENNY DRZIAK PRE N25 (9572216)
TP PRIESTOROVÝ REGULÁTOR NEA SMART 2.0 PRE MERANIE TEPLOTY V MIESTNOSTI, FY. REHAU
TE SNÍMAČ VONKAJŠEJ TEPLOTY
OV ODVZDUŠŇOVACÍ VENTIL , PN 16/120°C
TČ STUPACIE POTRUBIE PRIMÁRNEHO OKRUHU TEPELNÉHO ČERPADLA
UK1 STUPACIE POTRUBIE PODLAHOVÉHO VYKUROVANIA (Ø 32 x 4,7)

R1 DECENTRÁLNA REKUPERAČNÁ JEDNOTKA VIESSMANN VITOVENT 100-D, TYP H40E B55 (F)
VZDUCHOVÝ VÝKN S VENTILÁTOROM MAX. 55 m3/h, TRIEDA FILTRÁCIE G3, EL. PRIPOJENIE 230 V / 50 Hz
PRECHOD CEZ STENU Ø162 MM, HLUČNOSŤ NAJVIAC 46,2 dB, NAJMENENJ 24,8 dB
ROZMER 218x218x32,8 (výška * šírka * hĺbka), POLOHA OSADENIA = OS +2,00m OD H.P., 0,4m OD STENY
SPOTREBA PRÍKON MAX. 6,9 W, ÚČINNOSŤ REKUPERÁCIE 87%, BIELA FARBA

POZNÁMKA :

- V PRÍPADE NEJASNOSTÍ VO VÝKRESOVEJ DOKUMENTÁCII KONTAKTOVAŤ ZODPOVEDNÉHO PROJEKTANTA
- VŠETKY ROZMERY STAVEBNÝCH PRÁC KONTROLOVAŤ NA MIESTE STAVBY
- PRED UVEDENÍM DO PREVÁDZKY JE POTREBNÉ VYKONAŤ DÔKLADNÝ PREPLACH SYSTÉMU S VYČISTENÍM VŠETKÝCH FILTROV NA ROZVODE
- PO NAPUSTENÍ SYSTÉMU JE POTREBNÉ VYKONAŤ JEHO ODVZDUŠNENIE
- DODÁVATEL STAVBY JE POVINNÝ REALIZOVAŤ VŠETKY PRÁCE V ZMYSLE PLATNÝCH STN EN S DODRŽANÍM TECHNOLOGICKÝCH A BEZPEČNOSTNÝCH POSTUPOV. JE POVINNÝ REŠPEKTOVAŤ USTANOVENIÁ STN 730421 O PRÍSLUŠNÝCH ROZMEROVÝCH ODCHÝLKACH KONŠTRUKCIÍ PROTI PROJEKTOVANÉMU STAVU. KAŽDÚ ODCHÝLKU OD PROJEKTU JE POTREBNÉ PREROKOVAŤ S GP.