
| POZ. | NÁZOV, ROZMER | P. KS |
|---|---|---|
| 1a | VNUTORNA JEDNOTKA VITOCAL 222-S AWBT-M-E-AC 221.E10 2C | 1 |
| 1b | VONKAJ.JEDNOTKA VITOCAL 222-S AWBT-M-E-AC 221.E10 2C (230V) | 1 |
| | MAX.VÝSTUPNÁ TEPLOTA 60°C,TEPELNY VYKON 2,6-10,4kW A7/W35 | |
| | EKOLOGICKE CHLADIVO R32, REGULÁCIA ONE-BASE,WIFI (Z022740) | |
| 2 | ELEKTRIC.PRIETOKOVY OHRIEVAC 8kW -v rozsahu dodavky pol.1a | 1 |
| 3 | CANBUS KOMUNIKACNY KABEL MEDZI JEDNOTKY 15m (ZK06217) | 1 |
| 4 | BEZDRATOVÉ DIALKOVE OVLADANIE VITOTROL 300-E (7959522) | 1 |
| 5 | ELEKTRICKY ROZVADZAC OBJEKTU | 1 |
| 6 | INSTALAC.SADA 12/6 NA ZEM+KONZOLA - 12,5M RURY (ZK06313) | 1 |
| 7 | ELEKTRIC.VYHREVNY PAS PRE VANU KONDENZATU 2,5m (ZK04098) | 1 |
| 8 | EXPANZNA NADOBA N25 OBJEM 25L, 3bar BIELA (7938081) | 1 |
| | NASTENNY DRZIAK PRE N25 (9572216) | 1 |
| 9 | ODKALOVAC S MAGNETOM A IZOLACIOU VITOTRAP 28mm (ZK04654) | 1 |
| 10 | PRIPOJOVACIA SADA NA OMIETKU-ZHORA | 1 |
| | | |
| | | |
| TE | SNIMAC VONKAJSEJ TEPLOTY - v rozsahu dodavky tep.cerpadla | 1 |
| T2 | SNIMAC ROSNEHO BODU - VLHKOSTI (7181418) | 1 |
| | | |

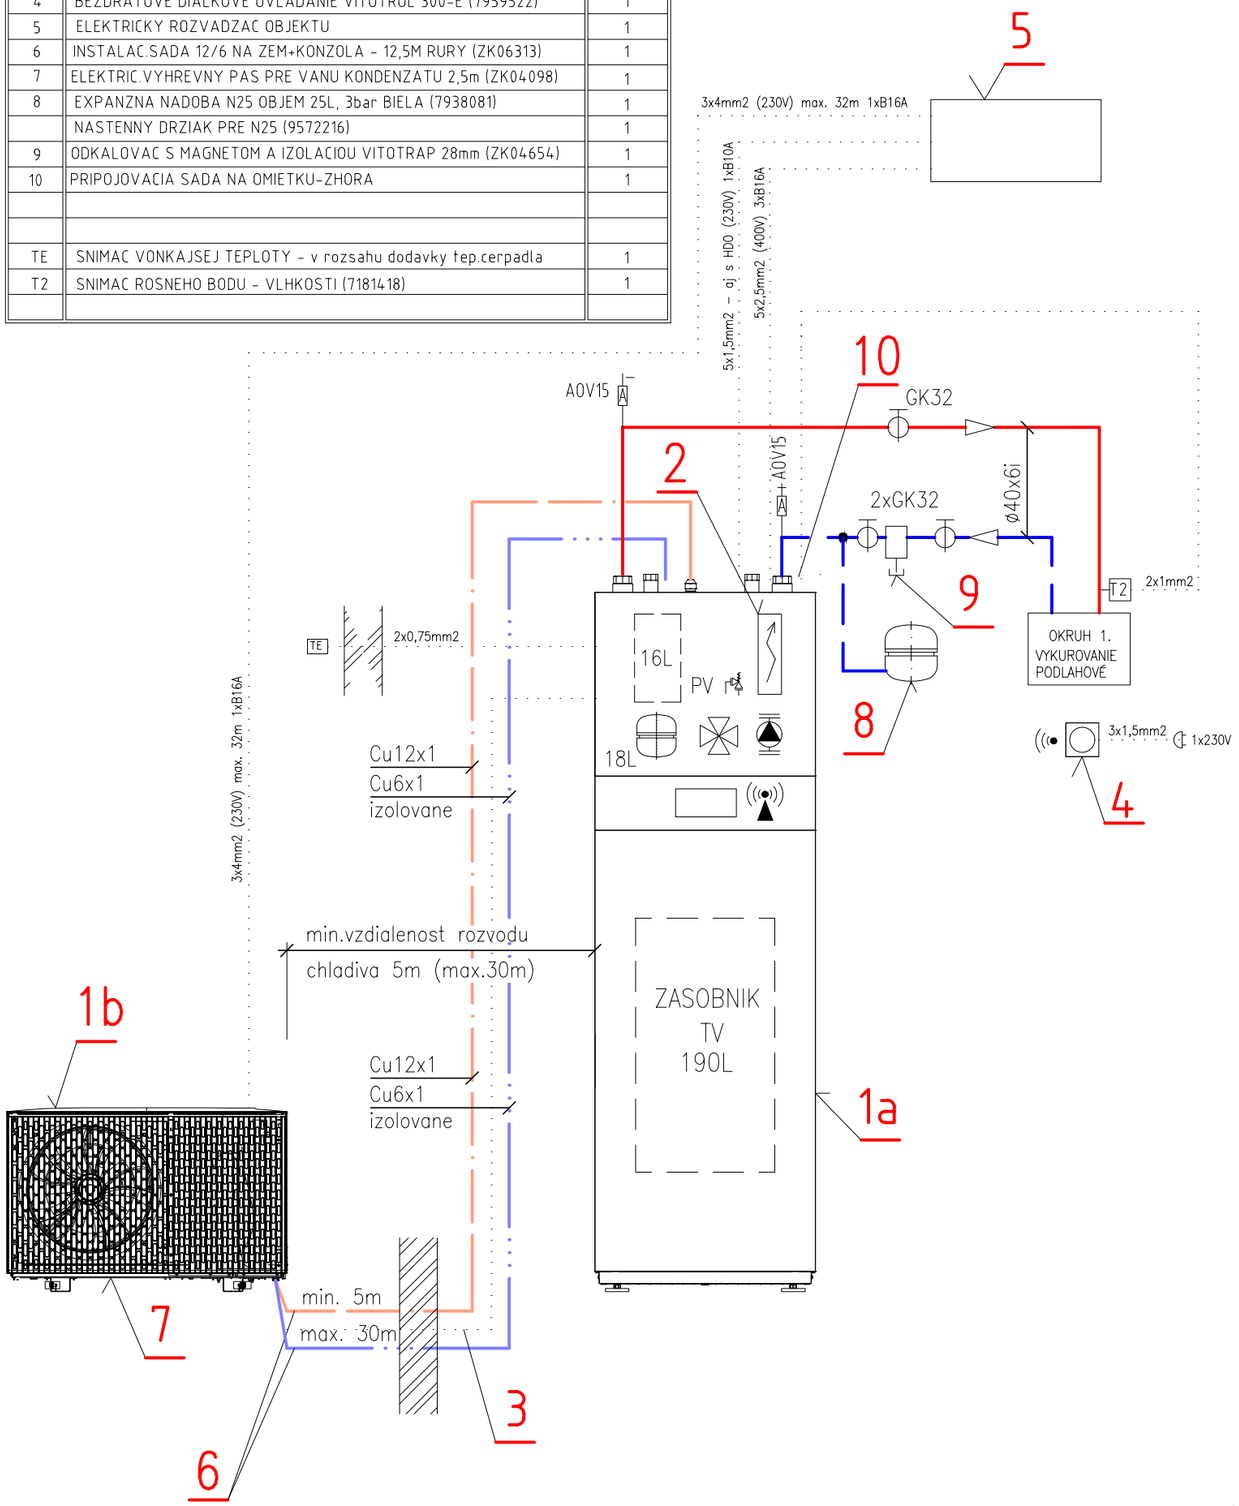


## LEGENDA POTRUBIA:

POTRUBIE - PLASTHLINNÍKOVÁ RURKA PE-Xa/AL/PE napr. RAUTITAN Stabil REHAU
SPÁJANÉ LISOVANÍM, IZOLOVANÉ POTRUBIE, TEPLOTNÝ SPÁD 45/35°C
POTRUBIE VEDENÉ PRI STENE, PRE PODLAHOVÉ VYKUROVANIE, PRÍVOD A SPIATOČKA

ROZVOD ÚK PRE PRIMÁRNY OKRUH TEPELNÉHO ČERPADLA
MATERIÁL MEĎ

## LEGENDA ARMATÚR :

| | |
|---|---|
| OV | ODVZDUŠŇOVACÍ VENTIL , PN 16/120°C |
| GK | GULOVÝ KOHÚT ZÁVITOVÝ , PN 16/120°C |
| AOV | AUTOMATICKÝ ODVZDUŠŇOVACÍ VENTIL S UZATVÁRACÍM VENTILOM , PN 16/120°C |
| VK | VYPÚŠŤACÍ KOHÚT , PN 16/120°C |
| F | FILTER ZÁVITOVÝ , SITO S OKOM 0,75mm , PN 16/120°C |
| PRV | REDUKČNÝ VENTIL S MANOMETROM fy. HONEYWELL typ D 06F, G 1/2" , PN 25/70°C |
| | ROZSAH NASTAVENIA 1,5 - 6,0 bar |

## POZNÁMKA :

- V PRÍPADE NEJASNOSTÍ VO VÝKRESOVEJ DOKUMENTÁCII KONTAKTOVAŤ ZODPOVEDNÉHO PROJEKTANTA
- VŠETKY ROZMERY STAVEBNÝCH PRÁC KONTROLOVAŤ NA MIESTE STAVBY
- PRED UVEDENÍM SYSTÉMU DO PREVÁDZKY JE POTREBNÉ VYKONAŤ DÔKLADNÝ PREPLACH SYSTÉMU S VYČISTENÍM VŠETKÝCH FILTROV NA ROZVODE
- PO NAPUSTENÍ SYSTÉMU JE POTREBNÉ VYKONAŤ JEHO ODVZDUŠNENIE
- DODÁVATEL STAVBY JE POVINNÝ REALIZOVAŤ VŠETKY PRÁCE V ZMYSLE PLATNÝCH STN EN S DODRŽANÍM TECHNOLOGICKÝCH A BEZPEČNOSTNÝCH POSTUPOV. ĎALEJ JE POVINNÝ REŠPEKTOVAŤ USTANOVENIÁ STN 730421 O PRÍSLUŠNÝCH ROZMEROVÝCH ODCHÝLKACH REALIZOVANÝCH KONŠTRUKCIÍ PROTI PROJEKTOVANÉMU STAVU. KAŽDÚ ODCHÝLKU OD PROJEKTU JE POTREBNÉ PREROKOVAŤ S GP.
- PRESTUPY INŽINIERSKYCH SIETÍ A ROZVODOV V OBJEKTE JE POTREBNÉ VYNECHAŤ PRI REALIZÁCII STAVBY.