
LEGENDA POTRUBIA:

POTRUBIE - PLASTHLINNÍKOVÁ RÚRKA NAPR. GEBERIT MEPLA
SPÁJANÉ LISOVANÍM, IZOLOVANÉ POTRUBIE, TEPLOTNÝ SPÁD 70/50°C
POTRUBIE VEDENÉ V PODLAHE, PRE RADIATORI

POTRUBIE - PLASTHLINNÍKOVÁ RÚRKA NAPR. GEBERIT MEPLA
SPÁJANÉ LISOVANÍM, IZOLOVANÉ POTRUBIE, TEPLOTNÝ SPÁD 45/35°C
POTRUBIE VEDENÉ V PODLAHE, PRE PODLAHOVÉ VYKUROVANIE

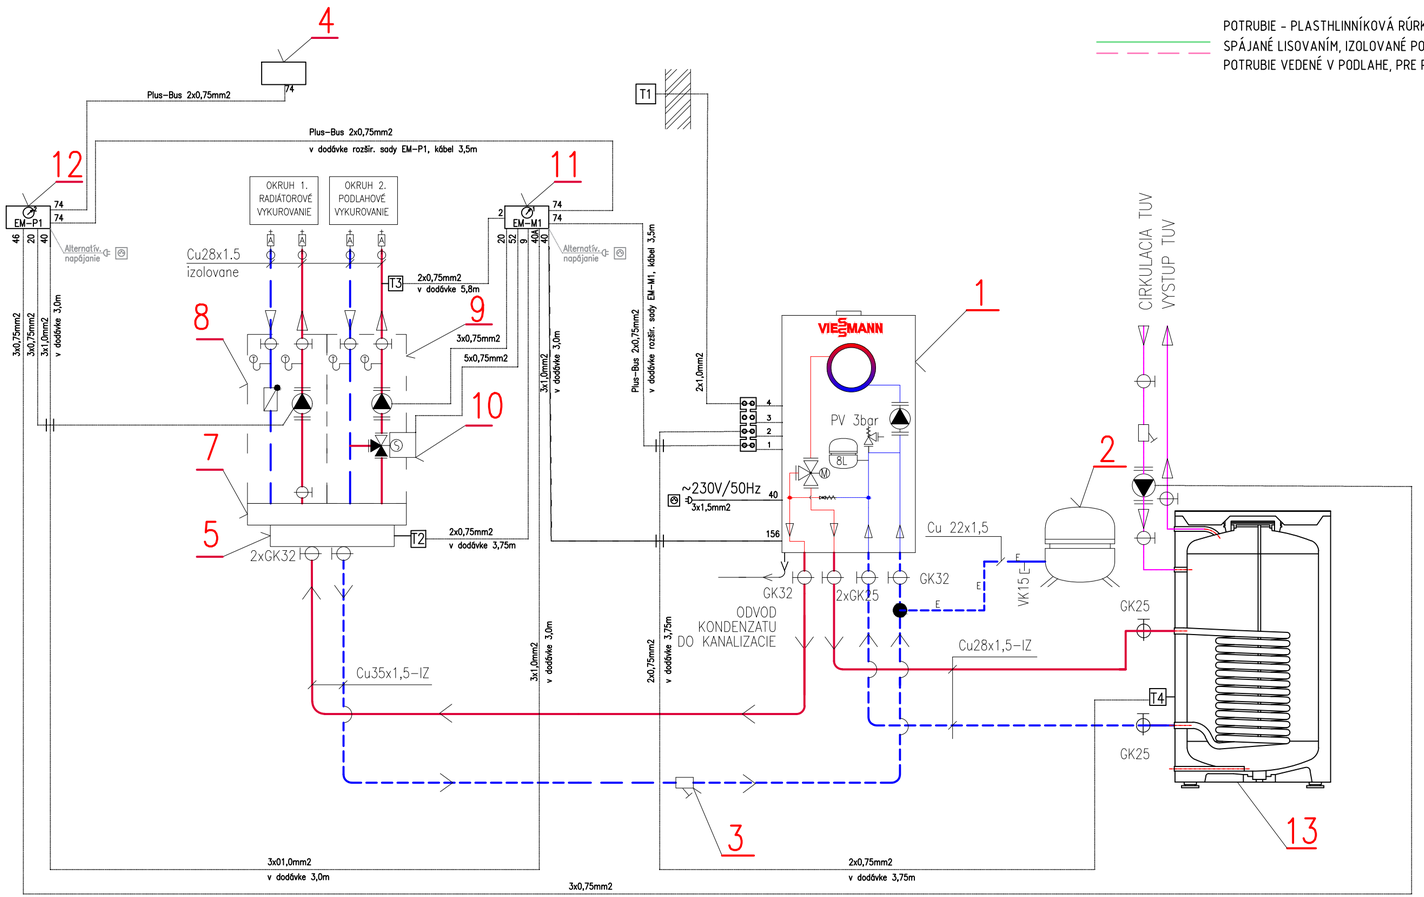

LEGENDA ZARIADENÍ:

POZ.	NÁZOV, ROZMER	P. KS
1	KONDENZAČNY KOTOL VIESSMANN VITODENS 100-W, TYP B1HF 3,2-32kW, 7-segment. displej	1
	MONTÁŽNE POMOCKA NA OMIETKU (ZK04307)	1
2	TLAKOVÁ EXPANZNÁ NÁDOBA S MEMBRÁNOU VIESSMANN N 35-BIELA+ BEZP. ARMATÚRA	1
3	ODKALOVAČ VITOTRAP S IZOLÁCIOU 1 1/4" (ZK04657)	1
4	DIALKOVÉ OVLÁDANIE VITOTROL 200-E (Z017415)	1
5	MODULÁRNY HYDRAULICKÝ VYROVNÁVAČ TLAKOV VIESSMANN DN25, DO 3,5 m3/h (7741533)	1
	PÚZDRO PRE PONORNÝ SNÍMAČ (9556119)	1
6	PONORNÝ SNÍMAČ TEPLOTY HVDT (ZK04032)	1
7	MODULÁRNY ROZDELOVAČ PRE 2 OKRUHY DN25 (7741065)	1
	UPEVNENIE NA STENU PRE ROZDELOVAČ DN25 (7011090)	1
8	RÝCHLOMONTÁŽNA SADA BEZ ZMIEŠAVAČA M31 DN20 ALPHA2-60 (7741073)	1
9	RÝCHLOMONTÁŽNA SADA SO ZMIEŠAVAČOM M32 DN25 ALPHA2-60 (7741079)	1
10	SERVOPOHON SR10 (7199567)	1
11	ROZŠIROVACIA SADA PRE JEDEN VYKUR.OKRUH SO ZMIEŠAVAČOM EM-M1 (Z017410)	1
12	ROZŠIROVACIA SADA PRE JEDEN VYKUR.OKRUH BEZ ZMIEŠAVAČA EM-P1 (Z017411)	1
13	ZÁSOBNÍKOVÝ OHRIEVAČ PITNEJ VODY VITOCELL 100-W, TYP CVAA 200L-vitopearlwhite(Z018468)	1
T1	SNÍMAČ VONKAJŠEJ TEPLOTY (ZK04306)	1
T2	SNÍMAČ HVDT (ZK04032)	1
T3	SNÍMAČ VÝSTUPNEJ TEPLOTY (v dodávke poz. 11)	1
T4	SNÍMAČ ZÁSOBNÍKA TÚV (ZK04671)	1

±0,000 = úroveň 1.N.P. = 126,40 m.n.m.