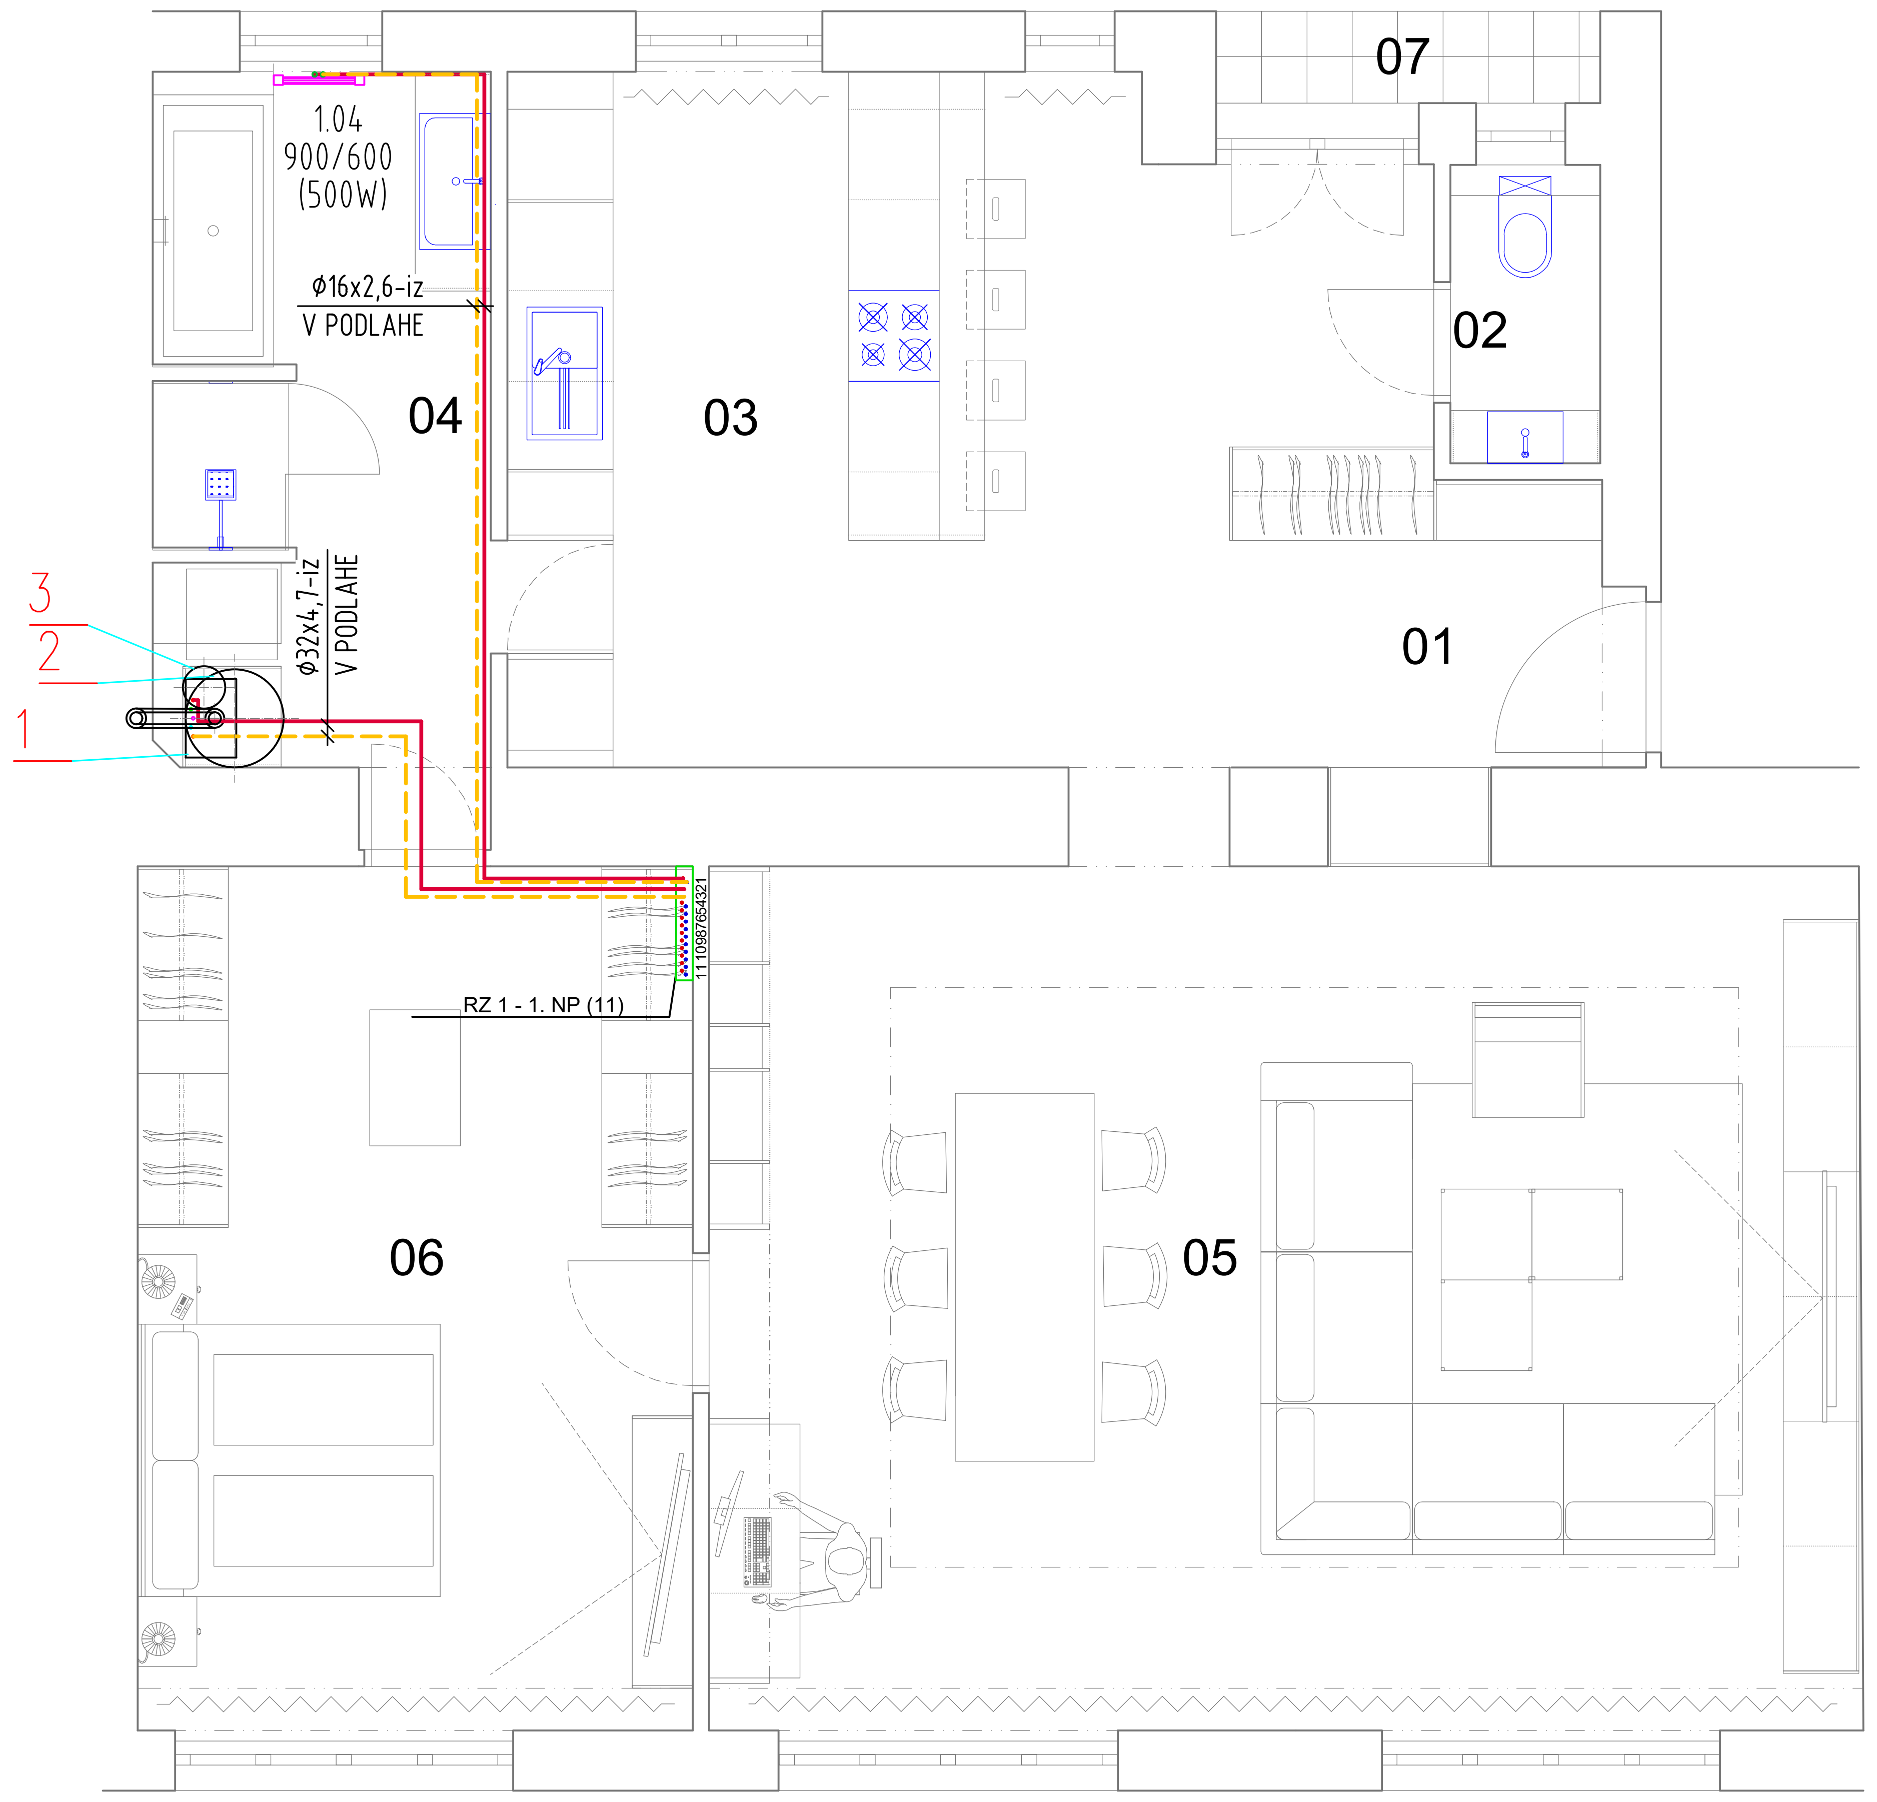

LEGENDA MIESTNOSTÍ

Č.M.	ÚČEL MIESTNOSTI	plocha v m2
01	vstupná hala	7,75
02	wc	1,76
03	kuchyňa	22,63
04	kúpelňa	10,61
05	obývacia izba	44,51
06	spálňa	21,12
celková plocha		108,38

07	loggia	1,55

LEGENDA POTRUBIA:

POTRUBIE - PLASTHLINNÍKOVÁ RURKA PE-Xa/AL/PE napr. RAUTI
SPÁJANÉ LISOVANÍM, IZOLOVANÉ POTRUBIE, TEPLOTNÝ SPÁD 45/

LEGENDA ZARIADENÍ

1 NASTENNY KONDENZAČNÝ KOTOL WTC-GW 15-B prev. W
MENOVITÝ TEPELNÝ PRÍKON 2 až 14 kW,

2 STACIONÁRNY ZÁSOBNÍK WAS 100 Eco/A S OBJEMOM 113l

3 UZAVRETÁ TLAKOVÁ EXPANZNÁ NÁDOBA REFLEX DD12 10/4,
O OBJEME 12l

RZ 1 - 1. NP (11)

ROZDEĽOVACIA STANICA PRE PODLAHOVÉ VYKUROVANIE 45/35°C

NAPR. FY. REHAU HKVD SX-AG 10, SKRINKA ROZDEĽOVAČA PRED OMIETKU AP 130/1005 10-13 okr.

REGULAČNÝ ROZVÁDZAČ REHAU NEA (230V) (1ks)

PRIESTOROVÝ TERMOSTAT REHAU NEA (230V) (1ks)

ELEKTRICKÝ SERVOPOHON REHAU UNI (24V) (5ks)

GUL KOHÚT DN 25 - 2 ks

AUTOMATICKÝ ODVZDUŠŇOVACÍ VENTIL S UZATVÁRACÍM VENTILOM , PN 16/120°C DN 15 - 2 ks

VYPÚŠŤACÍ KOHÚT , PN 16/120°C DN15 - 2 ks

LEGENDA VYKUROVACÍCH TELIES:

900/600 - REBRÍKOVÝ RADIATOR TYP URČÍ ARCHITEKT, MIN. VÝKON 500W

H.I.P
Ing. arch. Pet
Ing. arch. Mic
MIESTO STA
INVESTOR
NÁZOV
PROFESIA
OBSAH