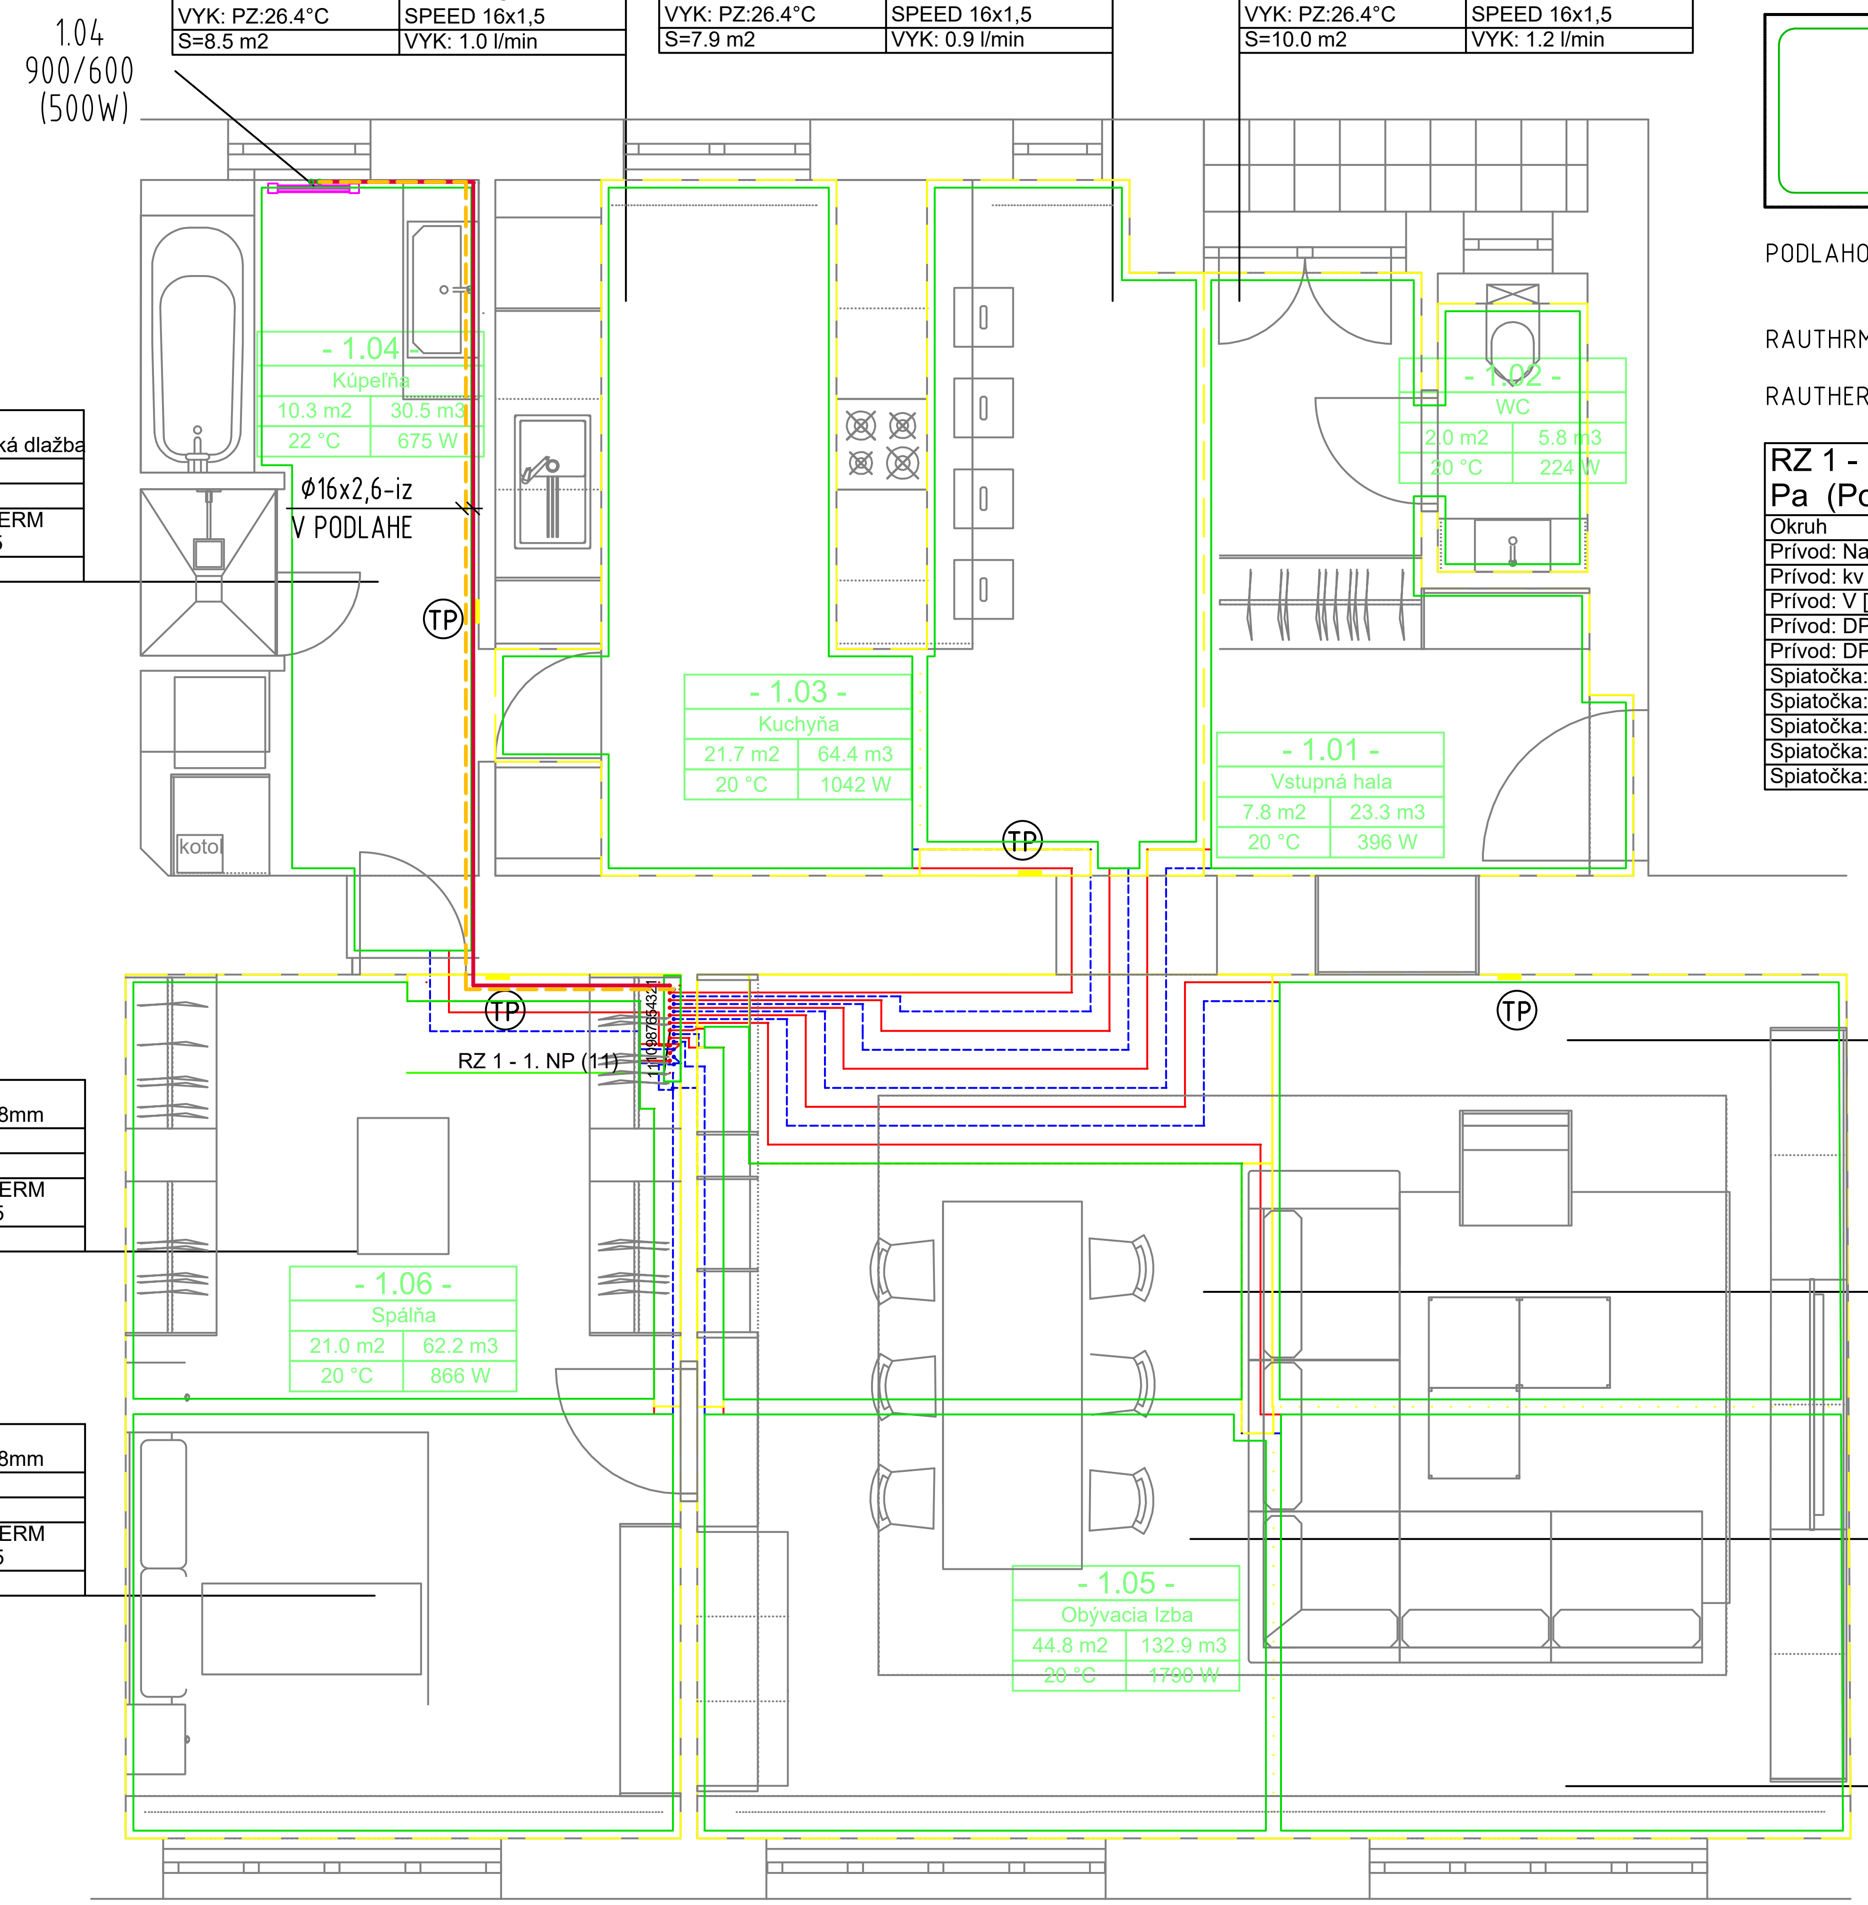

RZ 1 - 1. NP (10/1) (tp=45.0°C)	PZ 1: Parkety 8mm
Suchý systém REHAU	l-celk=78.3 m
Lpz=125 [mm]	1.03 - Kuchyňa
VYK: PZ:26.4°C	Rúrka RAUTHERM SPEED 16x1,5
S=8.5 m2	VYK: 1.0 l/min

RZ 1 - 1. NP (10/2) (tp=45.0°C)	PZ 1: Parkety 8mm
Suchý systém REHAU	l-celk=72.6 m
Lpz=125 [mm]	1.03 - Kuchyňa
VYK: PZ:26.4°C	Rúrka RAUTHERM SPEED 16x1,5
S=7.9 m2	VYK: 0.9 l/min

RZ 1 - 1. NP (10/3) (tp=45.0°C)	PZ 1: Parkety 8mm
Suchý systém REHAU	l-celk=91.7 m
Lpz=125 [mm]	1.01 - Vstupná hala
VYK: PZ:26.4°C	Rúrka RAUTHERM SPEED 16x1,5
S=10.0 m2	VYK: 1.2 l/min

RZ 1 - 1. NP (10/8) (tp=45.0°C)	PZ 1: Keramická dlažba
Suchý systém REHAU	l-celk=59.4 m
Lpz=125 [mm]	1.04 - Kúpeľňa
VYK: PZ:28.8°C	Rúrka RAUTHERM SPEED 16x1,5
S=6.8 m2	VYK: 0.8 l/min

RZ 1 - 1. NP (10/9) (tp=45.0°C)	PZ 1: Parkety 8mm
Suchý systém REHAU	l-celk=78.2 m
Lpz=125 [mm]	1.06 - Spálňa
VYK: PZ:26.4°C	Rúrka RAUTHERM SPEED 16x1,5
S=9.6 m2	VYK: 1.0 l/min

RZ 1 - 1. NP (10/10) (tp=45.0°C)	PZ 1: Parkety 8mm
Suchý systém REHAU	l-celk=89.5 m
Lpz=125 [mm]	1.06 - Spálňa
VYK: PZ:26.4°C	Rúrka RAUTHERM SPEED 16x1,5
S=10.5 m2	VYK: 1.2 l/min

RZ 1 - 1. NP (10/4) (tp=45.0°C)	PZ 1: Parkety 8mm
Suchý systém REHAU	l-celk=98.5 m
Lpz=125 [mm]	1.05 - Obývacia Izba
VYK: PZ:26.4°C	Rúrka RAUTHERM SPEED 16x1,5
S=10.9 m2	VYK: 1.3 l/min

RZ 1 - 1. NP (10/6) (tp=45.0°C)	PZ 1: Parkety 8mm
Suchý systém REHAU	l-celk=45.5 m
Lpz=125 [mm]	1.05 - Obývacia Izba
VYK: PZ:26.4°C	Rúrka RAUTHERM SPEED 16x1,5
S=5.7 m2	VYK: 0.6 l/min

RZ 1 - 1. NP (10/7) (tp=45.0°C)	PZ 1: Parkety 8mm
Suchý systém REHAU	l-celk=92.7 m
Lpz=125 [mm]	1.05 - Obývacia Izba
VYK: PZ:26.4°C	Rúrka RAUTHERM SPEED 16x1,5
S=10.8 m2	VYK: 1.2 l/min

RZ 1 - 1. NP (10/5) (tp=45.0°C)	PZ 1: Parkety 8mm
Suchý systém REHAU	l-celk=100.9 m
Lpz=125 [mm]	1.05 - Obývacia Izba
VYK: PZ:26.4°C	Rúrka RAUTHERM SPEED 16x1,5
S=10.9 m2	VYK: 1.3 l/min

LEGENDA PODLAHOVÉHO VYKUROVANIA:

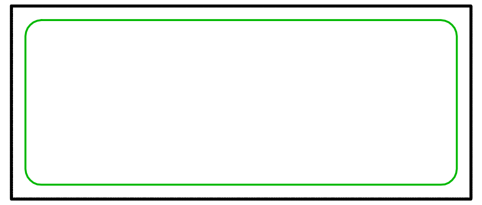

PODLAHOVÉ KÚRENIE REHAU

RAUTHRM SPEED 16x1,5	TYP VYKUROVACEJ RÚRKY
RAUTHERM SPEED	SYSTÉM PODLAHOVÉHO VYKUROVANIA

RZ 1 - 1. NP (11) H=3764 Pa Mh=10.0 l/min dPmax=3772 Pa (Podlahové Vykurovanie) (Voda)

Okruh	10	9	8	7	6	5	4	3	2	1
Prívod: Nast.	23 %	14 %	14 %	23 %	14 %	100.00 % Otv.	40 %	23 %	14 %	14 %
Prívod: kv	0.880	0.540	0.540	0.880	0.540	3.940	1.560	0.880	0.540	0.540
Prívod: V [l/min]	1.2	1.0	0.8	1.2	0.6	1.3	1.3	1.2	0.9	1.0
Prívod: DPv [Pa]	647	1327	817	687	463	40	244	674	1094	1265
Prívod: DPš [Pa]	615	1302	801	653	454	0	206	640	1073	1241
Spiatočka: Nast.	-- Otv.	-- Otv.	-- Otv.	-- Otv.	-- Otv.	-- Otv.	-- Otv.	-- Otv.	-- Otv.	-- Otv.
Spiatočka: kv	2.720	2.720	2.720	2.720	2.720	2.720	2.720	2.720	2.720	2.720
Spiatočka: V [l/min]	1.2	1.0	0.8	1.2	0.6	1.3	1.3	1.2	0.9	1.0
Spiatočka: DPv [Pa]	68	52	32	72	18	84	80	71	43	50
Spiatočka: DPš [Pa]	0	0	0	0	0	0	0	0	0	0

DETAIL PODLAHOVÉHO VYKUROVANIA:

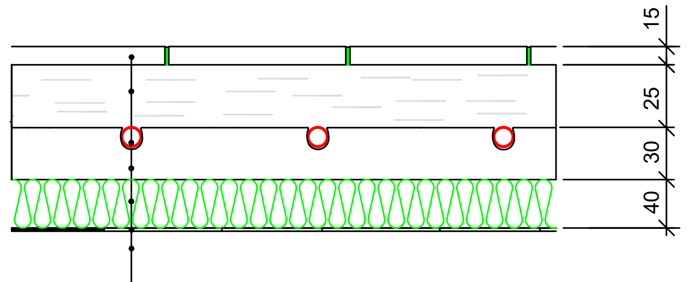

- PODLAHOVÁ VRSTVA
- PODLAHOVÉ SÁDROVLÁKNITÉ DOSKY
- REHAU KRYCIA FÓLIA PE
- POTRUBIE REHAU RAUTHERM Speed 16x1,5
- SYSTÉMOVÁ UKLADACIA DOSKA REHAU
- KROČAJOVÁ IZOLÁCIA
- VYROVNANÁ PEVNÁ PODLAHA

LEGENDA MIESTNOSTÍ:

Č.M.	ÚČEL MIESTNOSTI	plocha v m2
01	vstupná hala	7,75
02	wc	1,76
03	kuchyňa	22,63
04	kúpelňa	10,61
05	obývacia izba	44,51
06	spálňa	21,12
celková plocha		108,38

07	loggia	1,55

LEGENDA POTRUBIA:

- Plastový rozvod - plastová rúrka Pe-XA, RAUTHERM SPEED
- Potrubie pre napojenie rozdelovacej stanice vedené v podlahe uložiť do izolácie podlahy pod podlahové vykurovanie. Prívod aj spiatočka
- POTRUBIE - PLASTHLINNÍKOVÁ RURKA PE-Xa/AL/PE napr. RAUTITAN Stabil REHAU SPÁJANÉ LISOVANÍM, IZOLOVANÉ POTRUBIE, TEPLOTNÝ SPÁD 45/35°C.

LEGENDA VYKUROVACÍCH TELIES:

900/600 - REBRÍKOVÝ RADIATOR TYP URČÍ ARCHITEKT, MIN. VÝKON 500W

(TP) PRIESTOROVÝ TERMOSTAT

POZNÁMKA :

- V PRÍPADE NEJASNOSTÍ VO VÝKRESOVEJ DOKUMENTÁCIÍ KONTAKTOVAŤ ZODPOVEDNÉHO PROJEKTANTA
- VŠETKY ROZMERY STAVEBNÝCH PRÁC KONTROLOVAŤ NA MIESTE STAVBY
- PRED UVEDENÍM SYSTÉMU DO PREVÁDZKY JE POTREBNÉ VYKONAŤ DÔKLADNÝ PREPLACH SYSTÉMU S VYČISTENÍM VŠETKÝCH FILTROV NA ROZVODE
- PO NAPUSTENÍ SYSTÉMU JE POTREBNÉ VYKONAŤ JEHO ODVZDUŠNENIE
- DODÁVATEL STAVBY JE POVINNÝ REALIZOVAŤ VŠETKY PRÁCE V ZMYSLE PLATNÝCH STN EN S DODRŽANÍM TECHNOLOGICKÝCH A BEZPEČNOSTNÝCH POSTUPOV. ĎALEJ JE POVINNÝ REŠPEKTOVAŤ USTANOVENIÁ STN 730421 O PRÍSLUŠNÝCH ROZMEROVÝCH ODCHÝLKACH REALIZOVANÝCH KONŠTRUKCIÍ PROTI PROJEKTOVANÉMU STAVU. KAŽDÚ ODCHÝLKU OD PROJEKTU JE POTREBNÉ PREROKOVAŤ S GP.
- PRESTUPY INŽINIERSKYCH SIETÍ A ROZVODOV V OBJEKTE JE POTREBNÉ VYNECHAŤ PRI REALIZÁCII STAVBY.
- PROJEKTOVÁ D

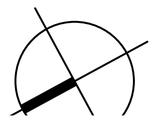

±0,000 = Vý

H.I.P
Ing. arch. Pete
Ing. arch. Mic
MIESTO STA
INVESTOR
NÁZOV
PROFESIA
OBSAH