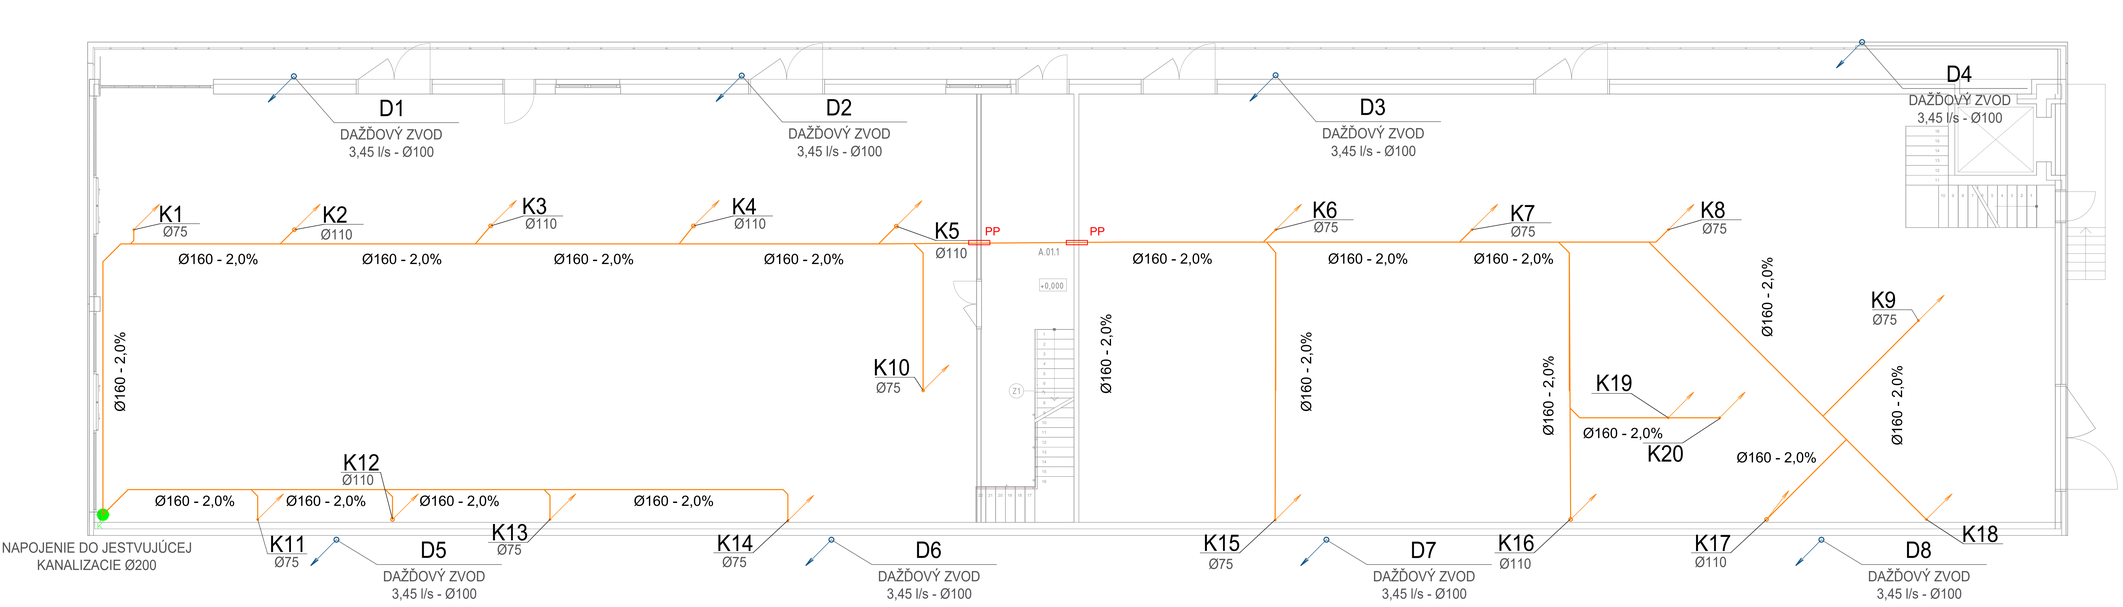



LEGENDA POTRUBIA

KANALIZAČNÉ HRDLOVÉ RÚRY - SPLAŠKOVÁ KANALIZÁCIA V STIENE - PP HT RÚRY

W EXISTUJÚCI VODOVOD, BOD NAPOJENIA Ø50

K EXISTUJÚCE ODPADOVÉ POTRUBIE SPLAŠKOVEJ KANALIZÁCIE, BOD NAPOJENIA Ø200

LEGENDA ZARIAĎOVACÍCH PREDMETOV A ARMATÚR

WC ZÁVESNÉ WC, INŠTALAČNÝ PRVOK PRE ZÁVESNÉ WC SO ZABUDOVANOU SPLACHOVACOU NÁDRŽKOU A ZÁPACHOVOU UZÁVIERKOU, S REDUKCIOU NA D 110

U UMÝVADLO, INŠTALAČNÝ PRVOK PRE UMÝVADLO, ZÁPACHOVÁ UZÁVIERKA D 40

D KUCHYNSKÝ DREZ, INŠTALAČNÝ PRVOK PRE DREZ A DREZOVÁ ZÁPACHOVÁ UZÁVIERKA D 50

S SPRCHOVÝ KÚT S NÁSTENNOU SPRCHOVOU JEDNOPÁKOVOU BATÉRIOU ZÁPACHOVÁ UZÁVIERKA D 50

B BIDETOVÁ SÚPRAVA, S BATÉRIOU A SPLACHOVACOU NÁDRŽKOU, ZÁPACHOVÁ UZÁVIERKA D 40

AP BIDETOVÁ SÚPRAVA, S BATÉRIOU A SPLACHOVACOU NÁDRŽKOU, ZÁPACHOVÁ UZÁVIERKA D 40

ZO ZÁSOBNÍKOVÝ OHRIEVAČ ELIZ EURO 80 HORIZONTÁLNY (2kW)

PO PRIETOKOVÝ OHRIEVAČ ESH 5 O.N Trend A+ (2kW)

PP POŽIARNY PRIESTUP

POZNÁMKY

Všetky kóty a rozmery PREMERAŤ NA STAVBE pred zahájením prác. Zvlášť prevenčí polohy pripojenia technologických zariadení.

Montážne firmy potrubí koordinovať s profesiami VZT a EL.

Práce realizovať striktne podľa platných STN/EN noriem. Kanalizačné potrubia osadiť v požadovanom spáde (min. 2%).

Zhotoviteľ je POVINNÝ pred zakrytím vykonať tlakovú skúšku vody a skúšku tesnosti kanalizácie. O skúškach vyhotoviť PROTOKOL.

Rozvody TÚV a SV izolovať izoláciou typu TUBOLIT (alebo ekvivalentom) v rozmnou požadovanej hrúbke.

Projektant nenesie zodpovednosť za funkčnosť systému v prípade, že montáž nebola vykonaná v súlade s touto PD, platnými normami a technologickými postupmi výrobcu.