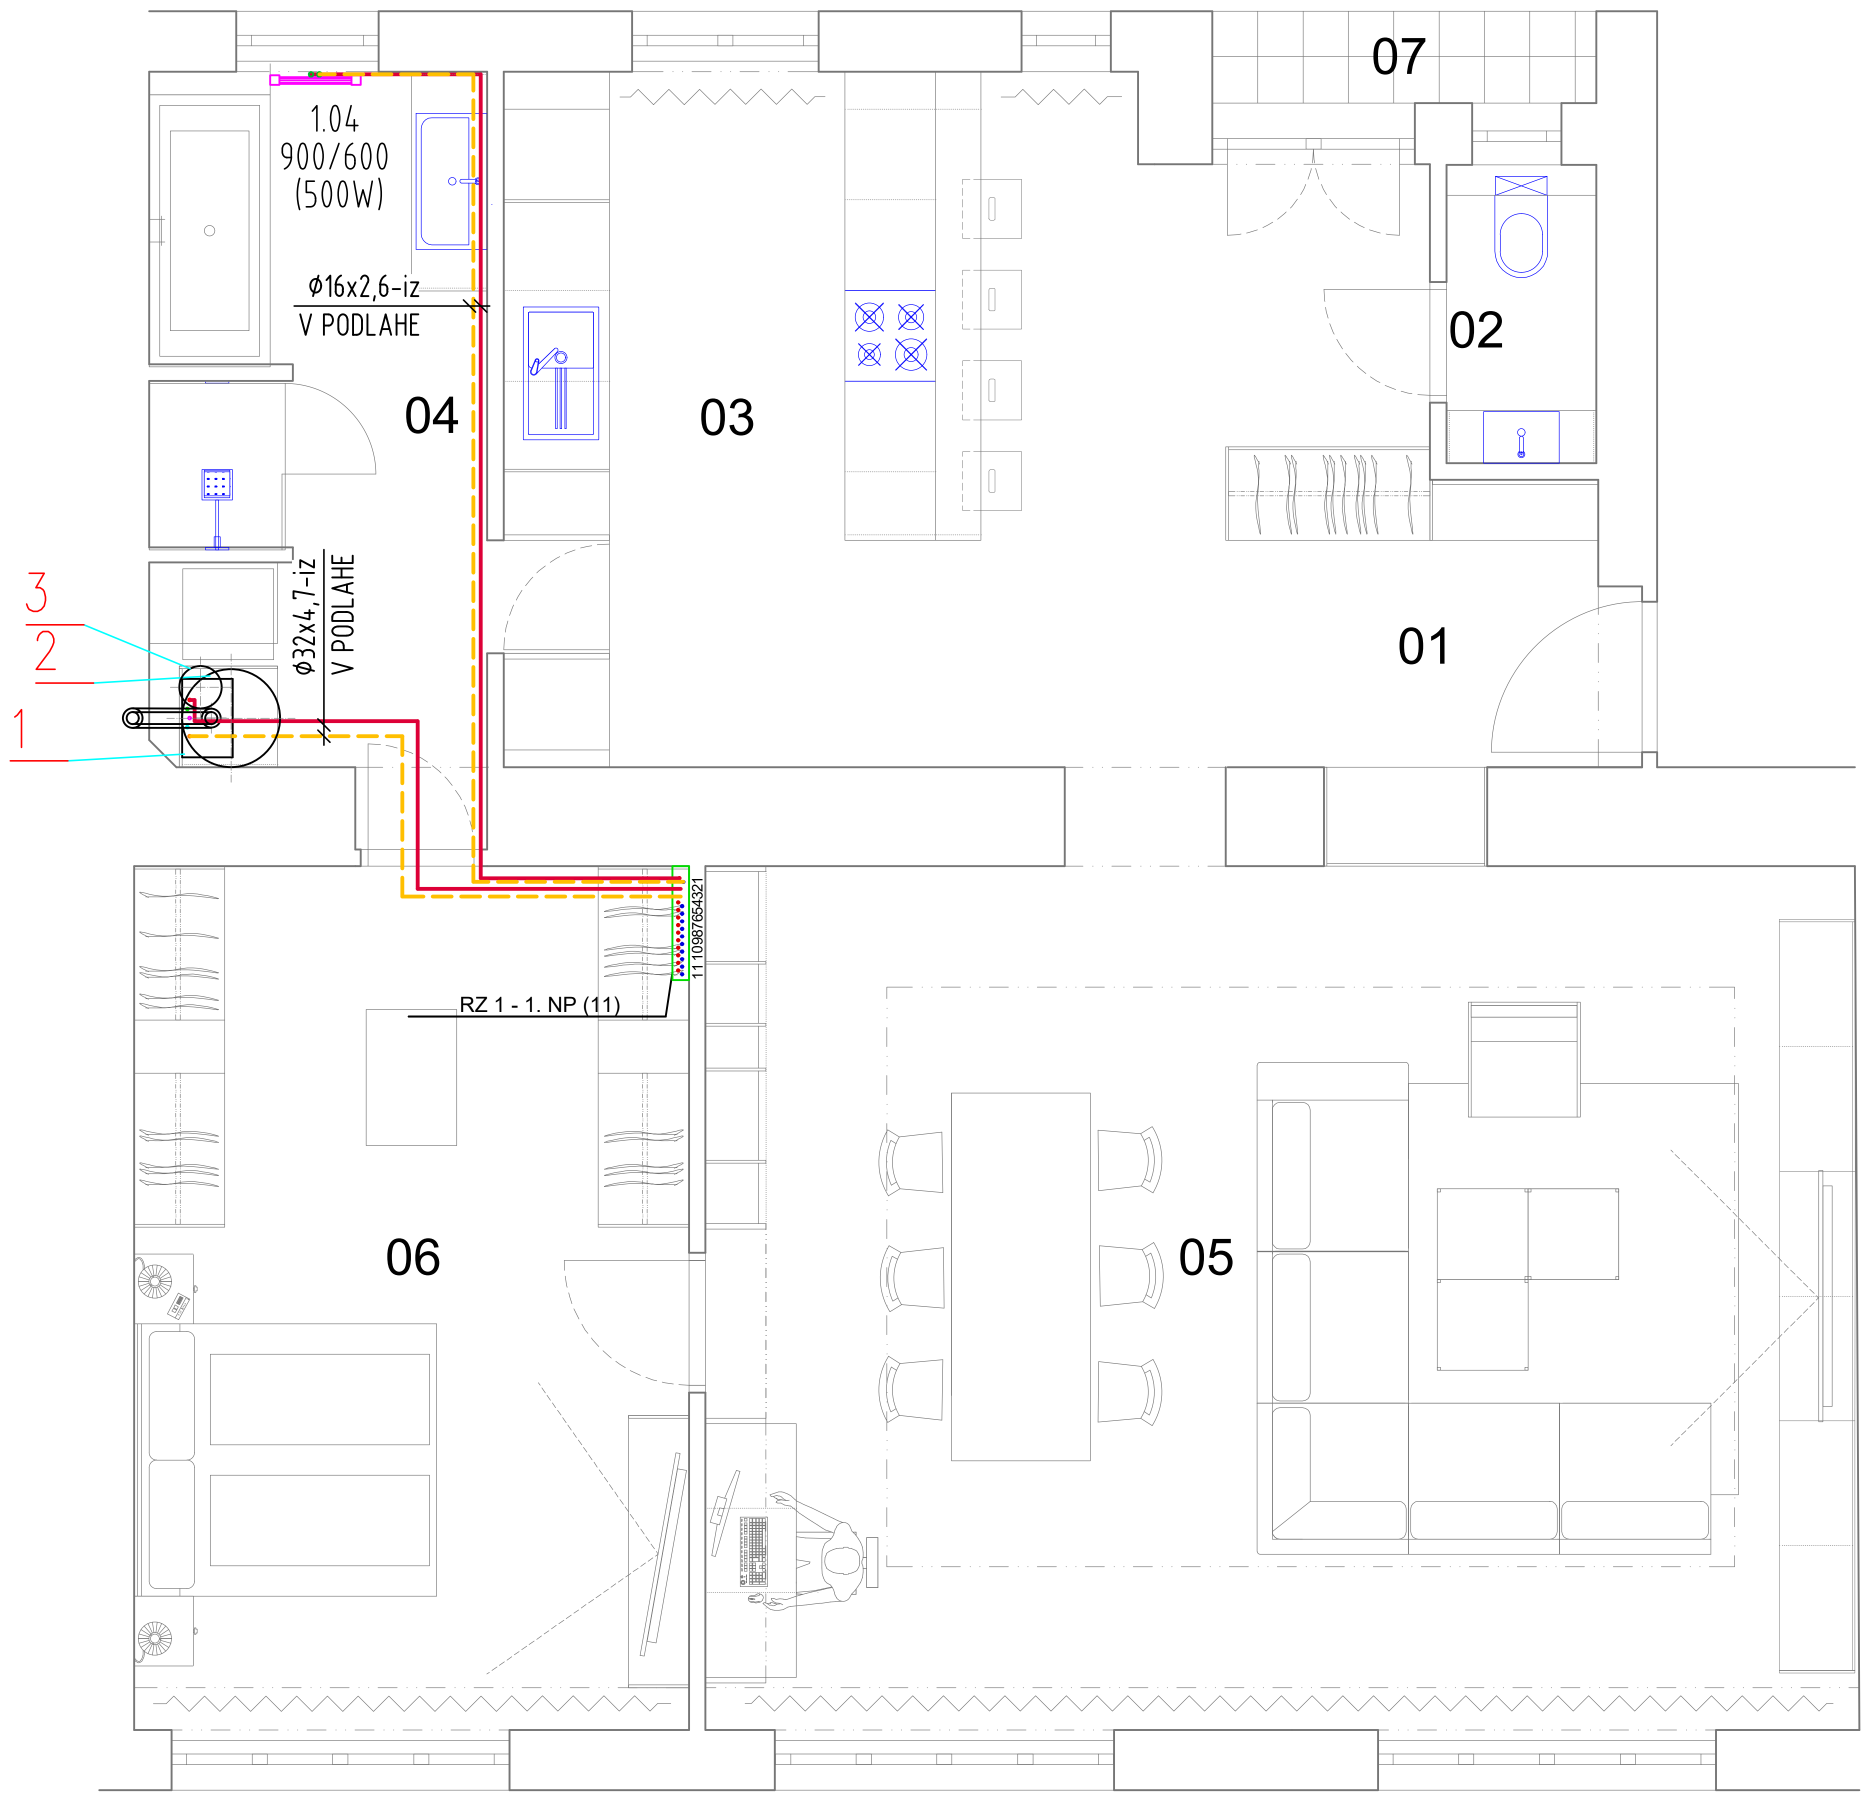

## LEGENDA MIESTNOSTÍ

| Č.M. | ÚČEL MIESTNOSTI | plocha v m2 |
|---|---|---|
| 01 | vstupná hala | 7,75 |
| 02 | wc | 1,76 |
| 03 | kuchyňa | 22,63 |
| 04 | kúpelňa | 10,61 |
| 05 | obývacia izba | 44,51 |
| 06 | spálňa | 21,12 |
| celková plocha | | 108,38 |

| | | |
|---|---|---|
| 07 | loggia | 1,55 |

## LEGENDA POTRUBIA:

━━ ╍╍ POTRUBIE - PLASTHLINNÍKOVÁ RURKA PE-Xa/AL/PE napr. RAUTI
SPÁJANÉ LISOVANÍM, IZOLOVANÉ POTRUBIE, TEPLOTNÝ SPÁD 45/

## LEGENDA ZARIADENÍ

1 NASTENNY KONDENZAČNÝ KOTOL WTC-GW 15-B prev. W
MENOVITÝ TEPELNÝ PRÍKON 2 až 14 kW,

2 STACIONÁRNY ZÁSOBNÍK WAS 100 Eco/A S OBJEMOM 113l

3 UZAVRETÁ TLAKOVÁ EXPANZNÁ NÁDOBA REFLEX DD12 10/4,
O OBJEME 12l

### RZ 1 - 1. NP (11)

ROZDEĽOVACIA STANICA PRE PODLAHOVÉ VYKUROVANIE 45/35°C
NAPR. FY. REHAU HKVD SX-AG 10, SKRINKA ROZDEĽOVAČA PRED OMIETKU AP 130/1005 10-13 okr.
REGULAČNÝ ROZVÁDZAČ REHAU NEA (230V) (1ks)
PRIESTOROVÝ TERMOSTAT REHAU NEA (230V) (1ks)
ELEKTRICKÝ SERVOPOHON REHAU UNI (24V) ( 5ks )
GUL KOHÚT DN 25 - 2 ks
AUTOMATICKÝ ODVZDUŠŇOVACÍ VENTIL S UZATVÁRACÍM VENTILOM , PN 16/120°C DN 15 - 2 ks
VYPÚŠŤACÍ KOHÚT , PN 16/120°C DN15 - 2 ks

## LEGENDA VYKUROVACÍCH TELIES:

900/600 - REBRÍKOVÝ RADIATOR TYP URČÍ ARCHITEKT, MIN. VÝKON 500W

| |
|---|
| H.I.P |
| Ing. arch. Pete |
| Ing. arch. Mic |
| MIESTO STA |
| INVESTOR |
| NÁZOV |
| PROFESIA |
| OBSAH |