| | |
|---|---|
| RZ 1 - 1. NP (10/1)<br>(tp=45.0°C) | PZ 1: Parkety 8mm |
| Suchý systém REHAU | l-celk=78.3 m |
| Lpz=125 [mm] | 1.03 - Kuchyňa |
| VYK: PZ:26.4°C | Rúrka RAUTHERM SPEED 16x1,5 |
| S=8.5 m2 | VYK: 1.0 l/min |

| | |
|---|---|
| RZ 1 - 1. NP (10/2)<br>(tp=45.0°C) | PZ 1: Parkety 8mm |
| Suchý systém REHAU | l-celk=72.6 m |
| Lpz=125 [mm] | 1.03 - Kuchyňa |
| VYK: PZ:26.4°C | Rúrka RAUTHERM SPEED 16x1,5 |
| S=7.9 m2 | VYK: 0.9 l/min |

| | |
|---|---|
| RZ 1 - 1. NP (10/3)<br>(tp=45.0°C) | PZ 1: Parkety 8mm |
| Suchý systém REHAU | l-celk=91.7 m |
| Lpz=125 [mm] | 1.01 - Vstupná hala |
| VYK: PZ:26.4°C | Rúrka RAUTHERM SPEED 16x1,5 |
| S=10.0 m2 | VYK: 1.2 l/min |

| | |
|---|---|
| RZ 1 - 1. NP (10/8)<br>(tp=45.0°C) | PZ 1: Keramická dlažba |
| Suchý systém REHAU | l-celk=59.4 m |
| Lpz=125 [mm] | 1.04 - Kúpeľňa |
| VYK: PZ:28.8°C | Rúrka RAUTHERM SPEED 16x1,5 |
| S=6.8 m2 | VYK: 0.8 l/min |

| | |
|---|---|
| RZ 1 - 1. NP (10/9)<br>(tp=45.0°C) | PZ 1: Parkety 8mm |
| Suchý systém REHAU | l-celk=78.2 m |
| Lpz=125 [mm] | 1.06 - Spálňa |
| VYK: PZ:26.4°C | Rúrka RAUTHERM SPEED 16x1,5 |
| S=9.6 m2 | VYK: 1.0 l/min |

| | |
|---|---|
| RZ 1 - 1. NP (10/10)<br>(tp=45.0°C) | PZ 1: Parkety 8mm |
| Suchý systém REHAU | l-celk=89.5 m |
| Lpz=125 [mm] | 1.06 - Spálňa |
| VYK: PZ:26.4°C | Rúrka RAUTHERM SPEED 16x1,5 |
| S=10.5 m2 | VYK: 1.2 l/min |

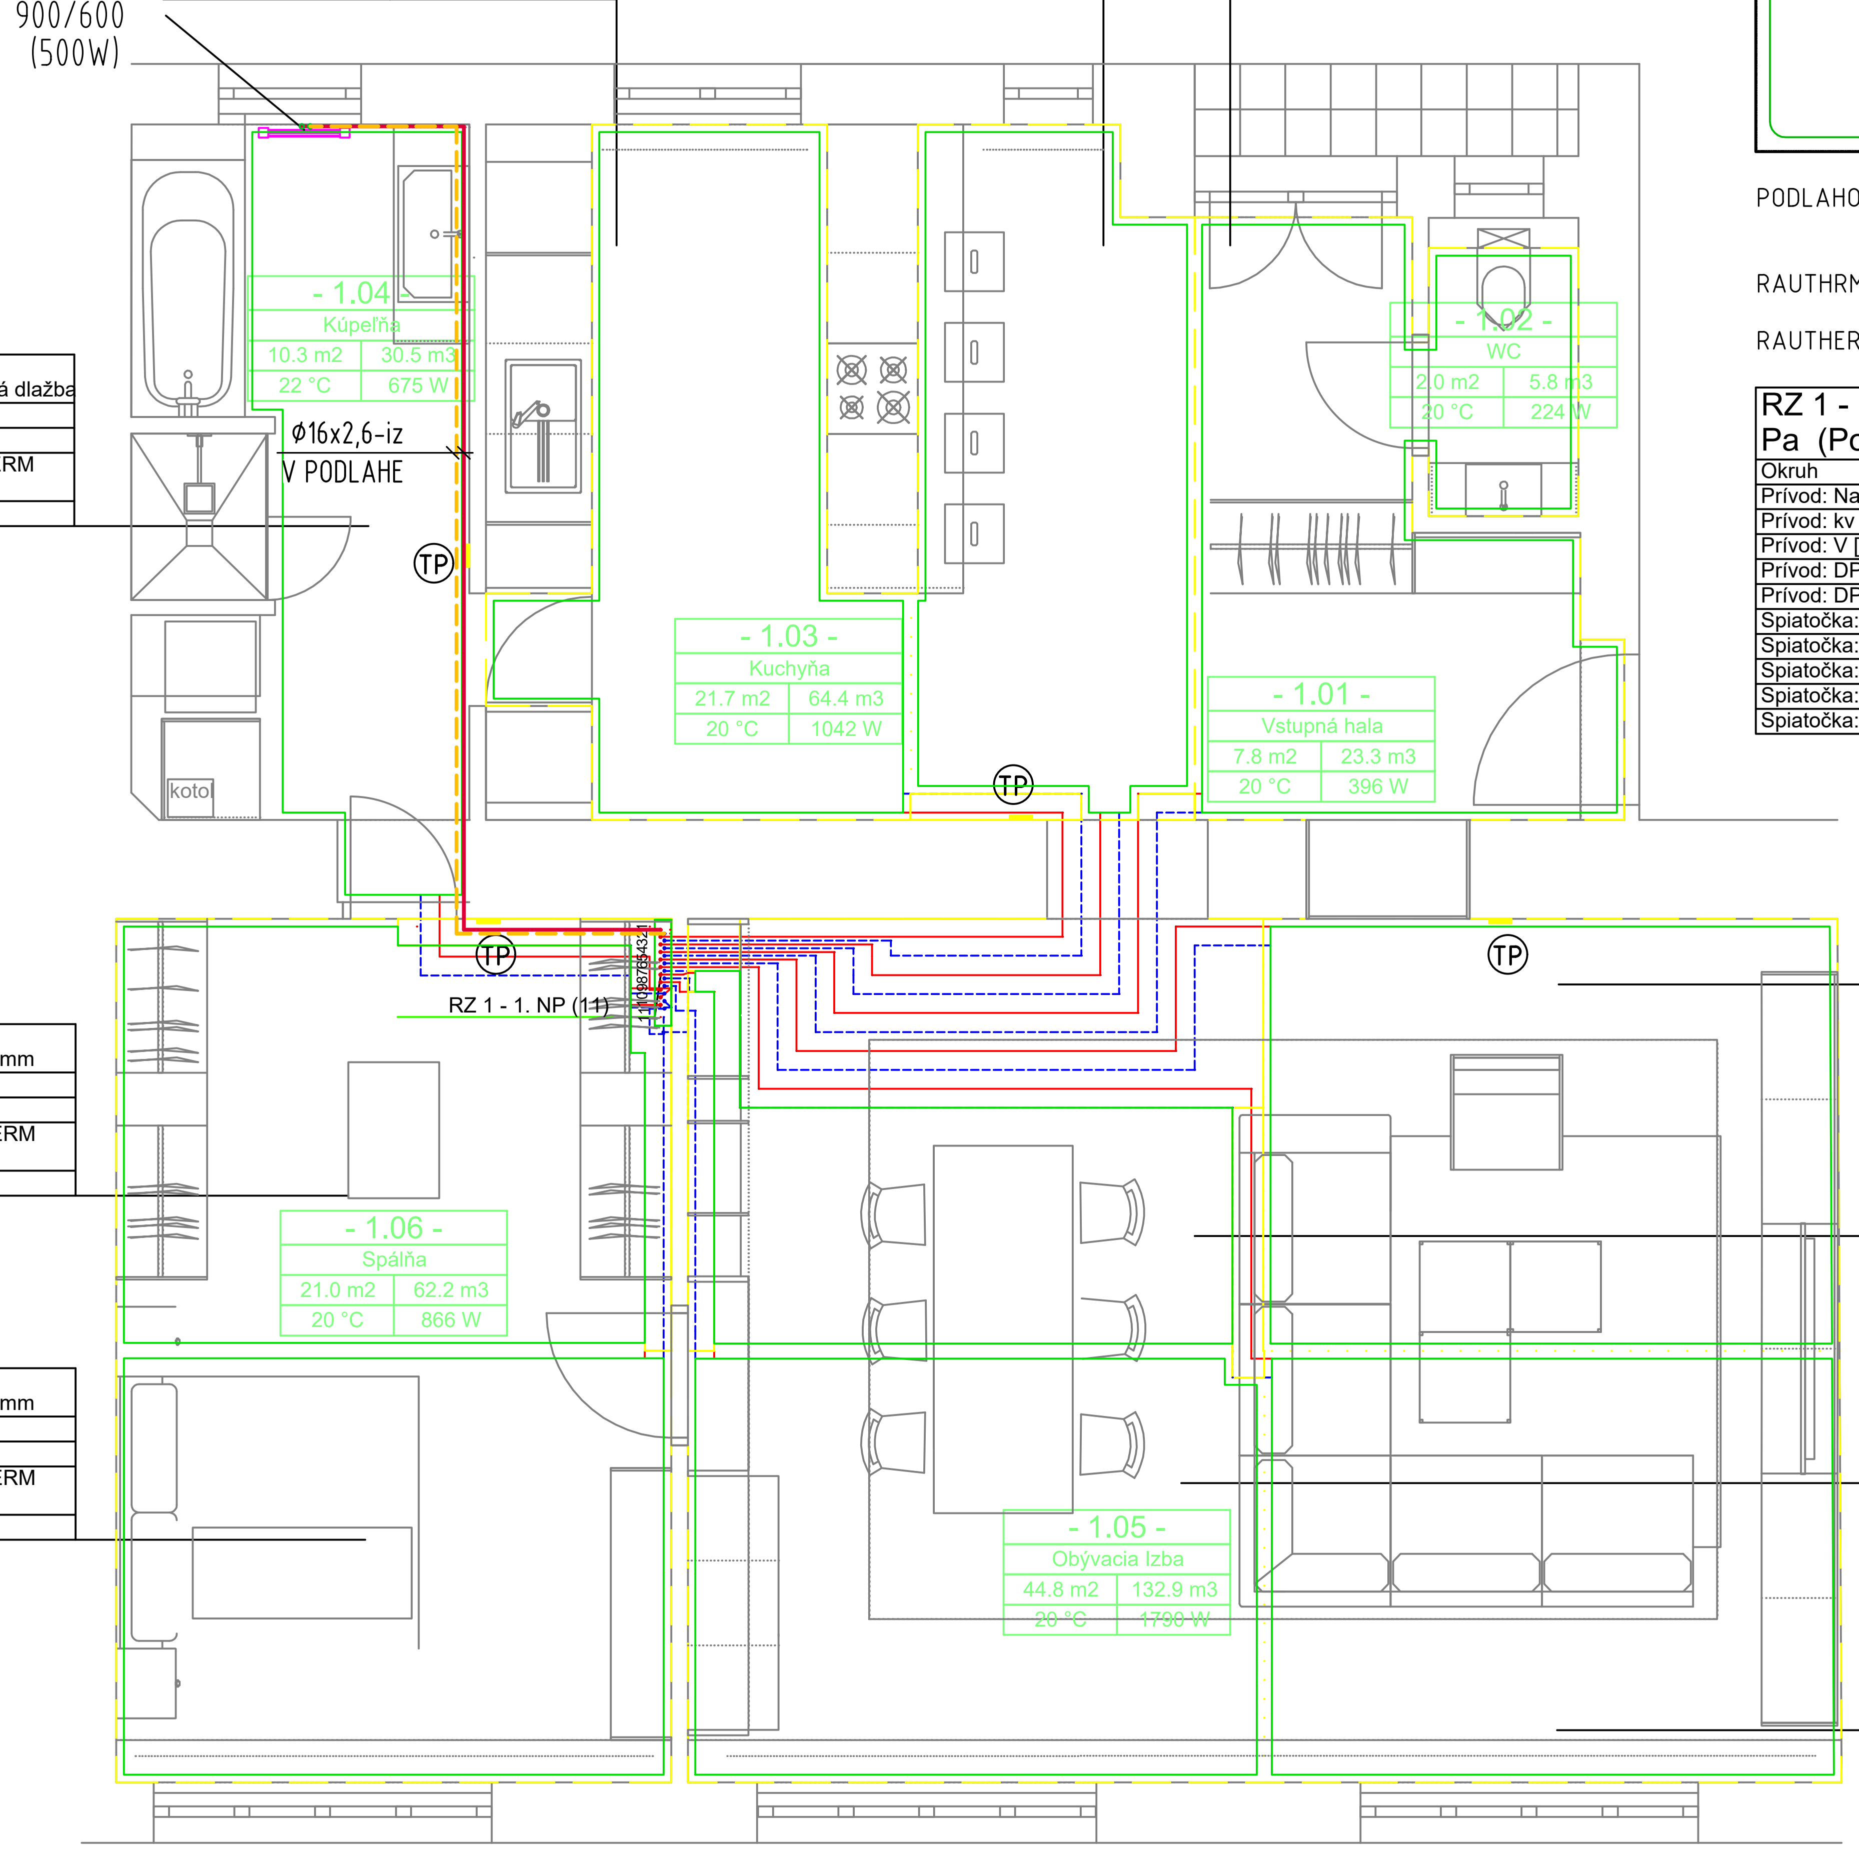

| | |
|---|---|
| RZ 1 - 1. NP (10/4)<br>(tp=45.0°C) | PZ 1: Parkety 8mm |
| Suchý systém REHAU | l-celk=98.5 m |
| Lpz=125 [mm] | 1.05 - Obývacia Izba |
| VYK: PZ:26.4°C | Rúrka RAUTHERM SPEED 16x1,5 |
| S=10.9 m2 | VYK: 1.3 l/min |

| | |
|---|---|
| RZ 1 - 1. NP (10/6)<br>(tp=45.0°C) | PZ 1: Parkety 8mm |
| Suchý systém REHAU | l-celk=45.5 m |
| Lpz=125 [mm] | 1.05 - Obývacia Izba |
| VYK: PZ:26.4°C | Rúrka RAUTHERM SPEED 16x1,5 |
| S=5.7 m2 | VYK: 0.6 l/min |

| | |
|---|---|
| RZ 1 - 1. NP (10/7)<br>(tp=45.0°C) | PZ 1: Parkety 8mm |
| Suchý systém REHAU | l-celk=92.7 m |
| Lpz=125 [mm] | 1.05 - Obývacia Izba |
| VYK: PZ:26.4°C | Rúrka RAUTHERM SPEED 16x1,5 |
| S=10.8 m2 | VYK: 1.2 l/min |

| | |
|---|---|
| RZ 1 - 1. NP (10/5)<br>(tp=45.0°C) | PZ 1: Parkety 8mm |
| Suchý systém REHAU | l-celk=100.9 m |
| Lpz=125 [mm] | 1.05 - Obývacia Izba |
| VYK: PZ:26.4°C | Rúrka RAUTHERM SPEED 16x1,5 |
| S=10.9 m2 | VYK: 1.3 l/min |

## LEGENDA PODLAHOVÉHO VYKUROVANIA:

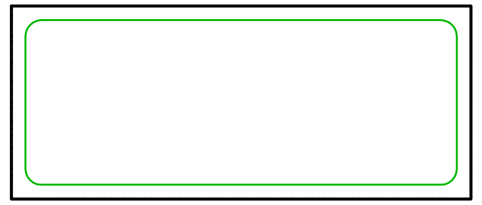

PODLAHOVÉ KÚRENIE REHAU

RAUTHRM SPEED 16x1,5 TYP VYKUROVACEJ RÚRKY

RAUTHERM SPEED SYSTÉM PODLAHOVÉHO VYKUROVANIA

**RZ 1 - 1. NP (11) H=3764 Pa Mh=10.0 l/min dPmax=3772 Pa (Podlahové Vykurovanie) (Voda)**

| Okruh | 10 | 9 | 8 | 7 | 6 | 5 | 4 | 3 | 2 | 1 |
|---|---|---|---|---|---|---|---|---|---|---|
| Prívod: Nast. | 23 % | 14 % | 14 % | 23 % | 14 % | 100.00 % Otv | 40 % | 23 % | 14 % | 14 % |
| Prívod: kv | 0.880 | 0.540 | 0.540 | 0.880 | 0.540 | 3.940 | 1.560 | 0.880 | 0.540 | 0.540 |
| Prívod: V [l/min] | 1.2 | 1.0 | 0.8 | 1.2 | 0.6 | 1.3 | 1.3 | 1.2 | 0.9 | 1.0 |
| Prívod: DPv [Pa] | 647 | 1327 | 817 | 687 | 463 | 40 | 244 | 674 | 1094 | 1265 |
| Prívod: DPš [Pa] | 615 | 1302 | 801 | 653 | 454 | 0 | 206 | 640 | 1073 | 1241 |
| Spiatočka: Nast. | -- Otv. | -- Otv. | -- Otv. | -- Otv. | -- Otv. | -- Otv. | -- Otv. | -- Otv. | -- Otv. | -- Otv. |
| Spiatočka: kv | 2.720 | 2.720 | 2.720 | 2.720 | 2.720 | 2.720 | 2.720 | 2.720 | 2.720 | 2.720 |
| Spiatočka: V [l/min] | 1.2 | 1.0 | 0.8 | 1.2 | 0.6 | 1.3 | 1.3 | 1.2 | 0.9 | 1.0 |
| Spiatočka: DPv [Pa] | 68 | 52 | 32 | 72 | 18 | 84 | 80 | 71 | 43 | 50 |
| Spiatočka: DPš [Pa] | 0 | 0 | 0 | 0 | 0 | 0 | 0 | 0 | 0 | 0 |

## DETAIL PODLAHOVÉHO VYKUROVANIA:

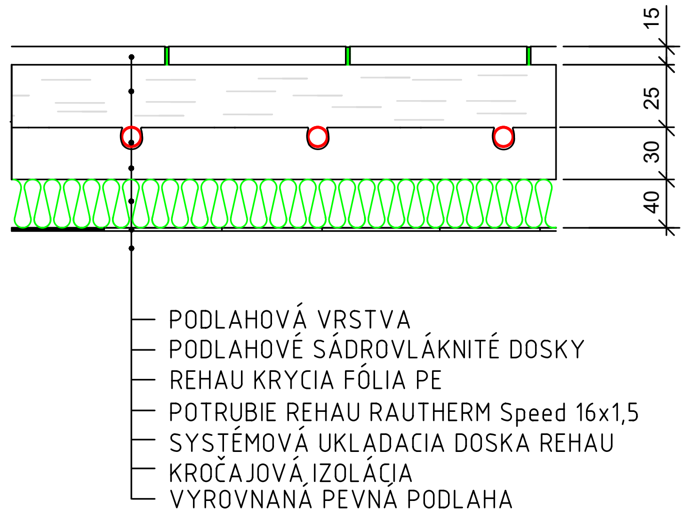
15
25
30
40
PODLAHOVÁ VRSTVA
PODLAHOVÉ SÁDROVLÁKNITÉ DOSKY
REHAU KRYCIA FÓLIA PE
POTRUBIE REHAU RAUTHERM Speed 16x1,5
SYSTÉMOVÁ UKLADACIA DOSKA REHAU
KROČAJOVÁ IZOLÁCIA
VYROVNANÁ PEVNÁ PODLAHA

## LEGENDA MIESTNOSTÍ:

| Č.M. | ÚČEL MIESTNOSTI | plocha v m2 |
|---|---|---|
| 01 | vstupná hala | 7,75 |
| 02 | wc | 1,76 |
| 03 | kuchyňa | 22,63 |
| 04 | kúpelňa | 10,61 |
| 05 | obývacia izba | 44,51 |
| 06 | spálňa | 21,12 |
| celková plocha | | 108,38 |

| | | |
|---|---|---|
| 07 | loggia | 1,55 |

## LEGENDA POTRUBIA:

| | |
|---|---|
| —— | Plastový rozvod - plastová rúrka Pe-XA, RAUTHERM SPEED |
| – – – | Potrubie pre napojenie rozdelovacej stanice vedené v podlahe uložiť do izolácie podlahy pod podlahové vykurovanie. Prívod aj spiatočka |
| ——<br>– – – | POTRUBIE - PLASTHLINNÍKOVÁ RURKA PE-Xa/AL/PE napr. RAUTITAN Stabil REHAU SPÁJANÉ LISOVANÍM, IZOLOVANÉ POTRUBIE, TEPLOTNÝ SPÁD 45/35°C. |

## LEGENDA VYKUROVACÍCH TELIES:

900/600 - REBRÍKOVÝ RADIATOR TYP URČÍ ARCHITEKT, MIN. VÝKON 500W

| | |
|---|---|
| (TP) | PRIESTOROVÝ TERMOSTAT |

## POZNÁMKA :

- V PRÍPADE NEJASNOSTÍ VO VÝKRESOVEJ DOKUMENTÁCIÍ KONTAKTOVAŤ ZODPOVEDNÉHO PROJEKTANTA
- VŠETKY ROZMERY STAVEBNÝCH PRÁC KONTROLOVAŤ NA MIESTE STAVBY
- PRED UVEDENÍM SYSTÉMU DO PREVÁDZKY JE POTREBNÉ VYKONAŤ DÔKLADNÝ PREPLACH SYSTÉMU S VYČISTENÍM VŠETKÝCH FILTROV NA ROZVODE
- PO NAPUSTENÍ SYSTÉMU JE POTREBNÉ VYKONAŤ JEHO ODVZDUŠNENIE
- DODÁVATEL STAVBY JE POVINNÝ REALIZOVAŤ VŠETKY PRÁCE V ZMYSLE PLATNÝCH STN EN S DODRŽANÍM TECHNOLOGICKÝCH A BEZPEČNOSTNÝCH POSTUPOV. ĎALEJ JE POVINNÝ REŠPEKTOVAŤ USTANOVENIÁ STN 730421 O PRÍSLUŠNÝCH ROZMEROVÝCH ODCHÝLKACH REALIZOVANÝCH KONŠTRUKCIÍ PROTI PROJEKTOVANÉMU STAVU. KAŽDÚ ODCHÝLKU OD PROJEKTU JE POTREBNÉ PREROKOVAŤ S GP.
- PRESTUPY INŽINIERSKYCH SIETÍ A ROZVODOV V OBJEKTE JE POTREBNÉ VYNECHAŤ PRI REALIZÁCII STAVBY.
- PROJEKTOVÁ D

±0,000 = Vý

| |
|---|
| H.I.P |
| Ing. arch. Pet |
| Ing. arch. Mic |
| MIESTO STA |
| INVESTOR |
| NÁZOV |
| PROFESIA |
| OBSAH |