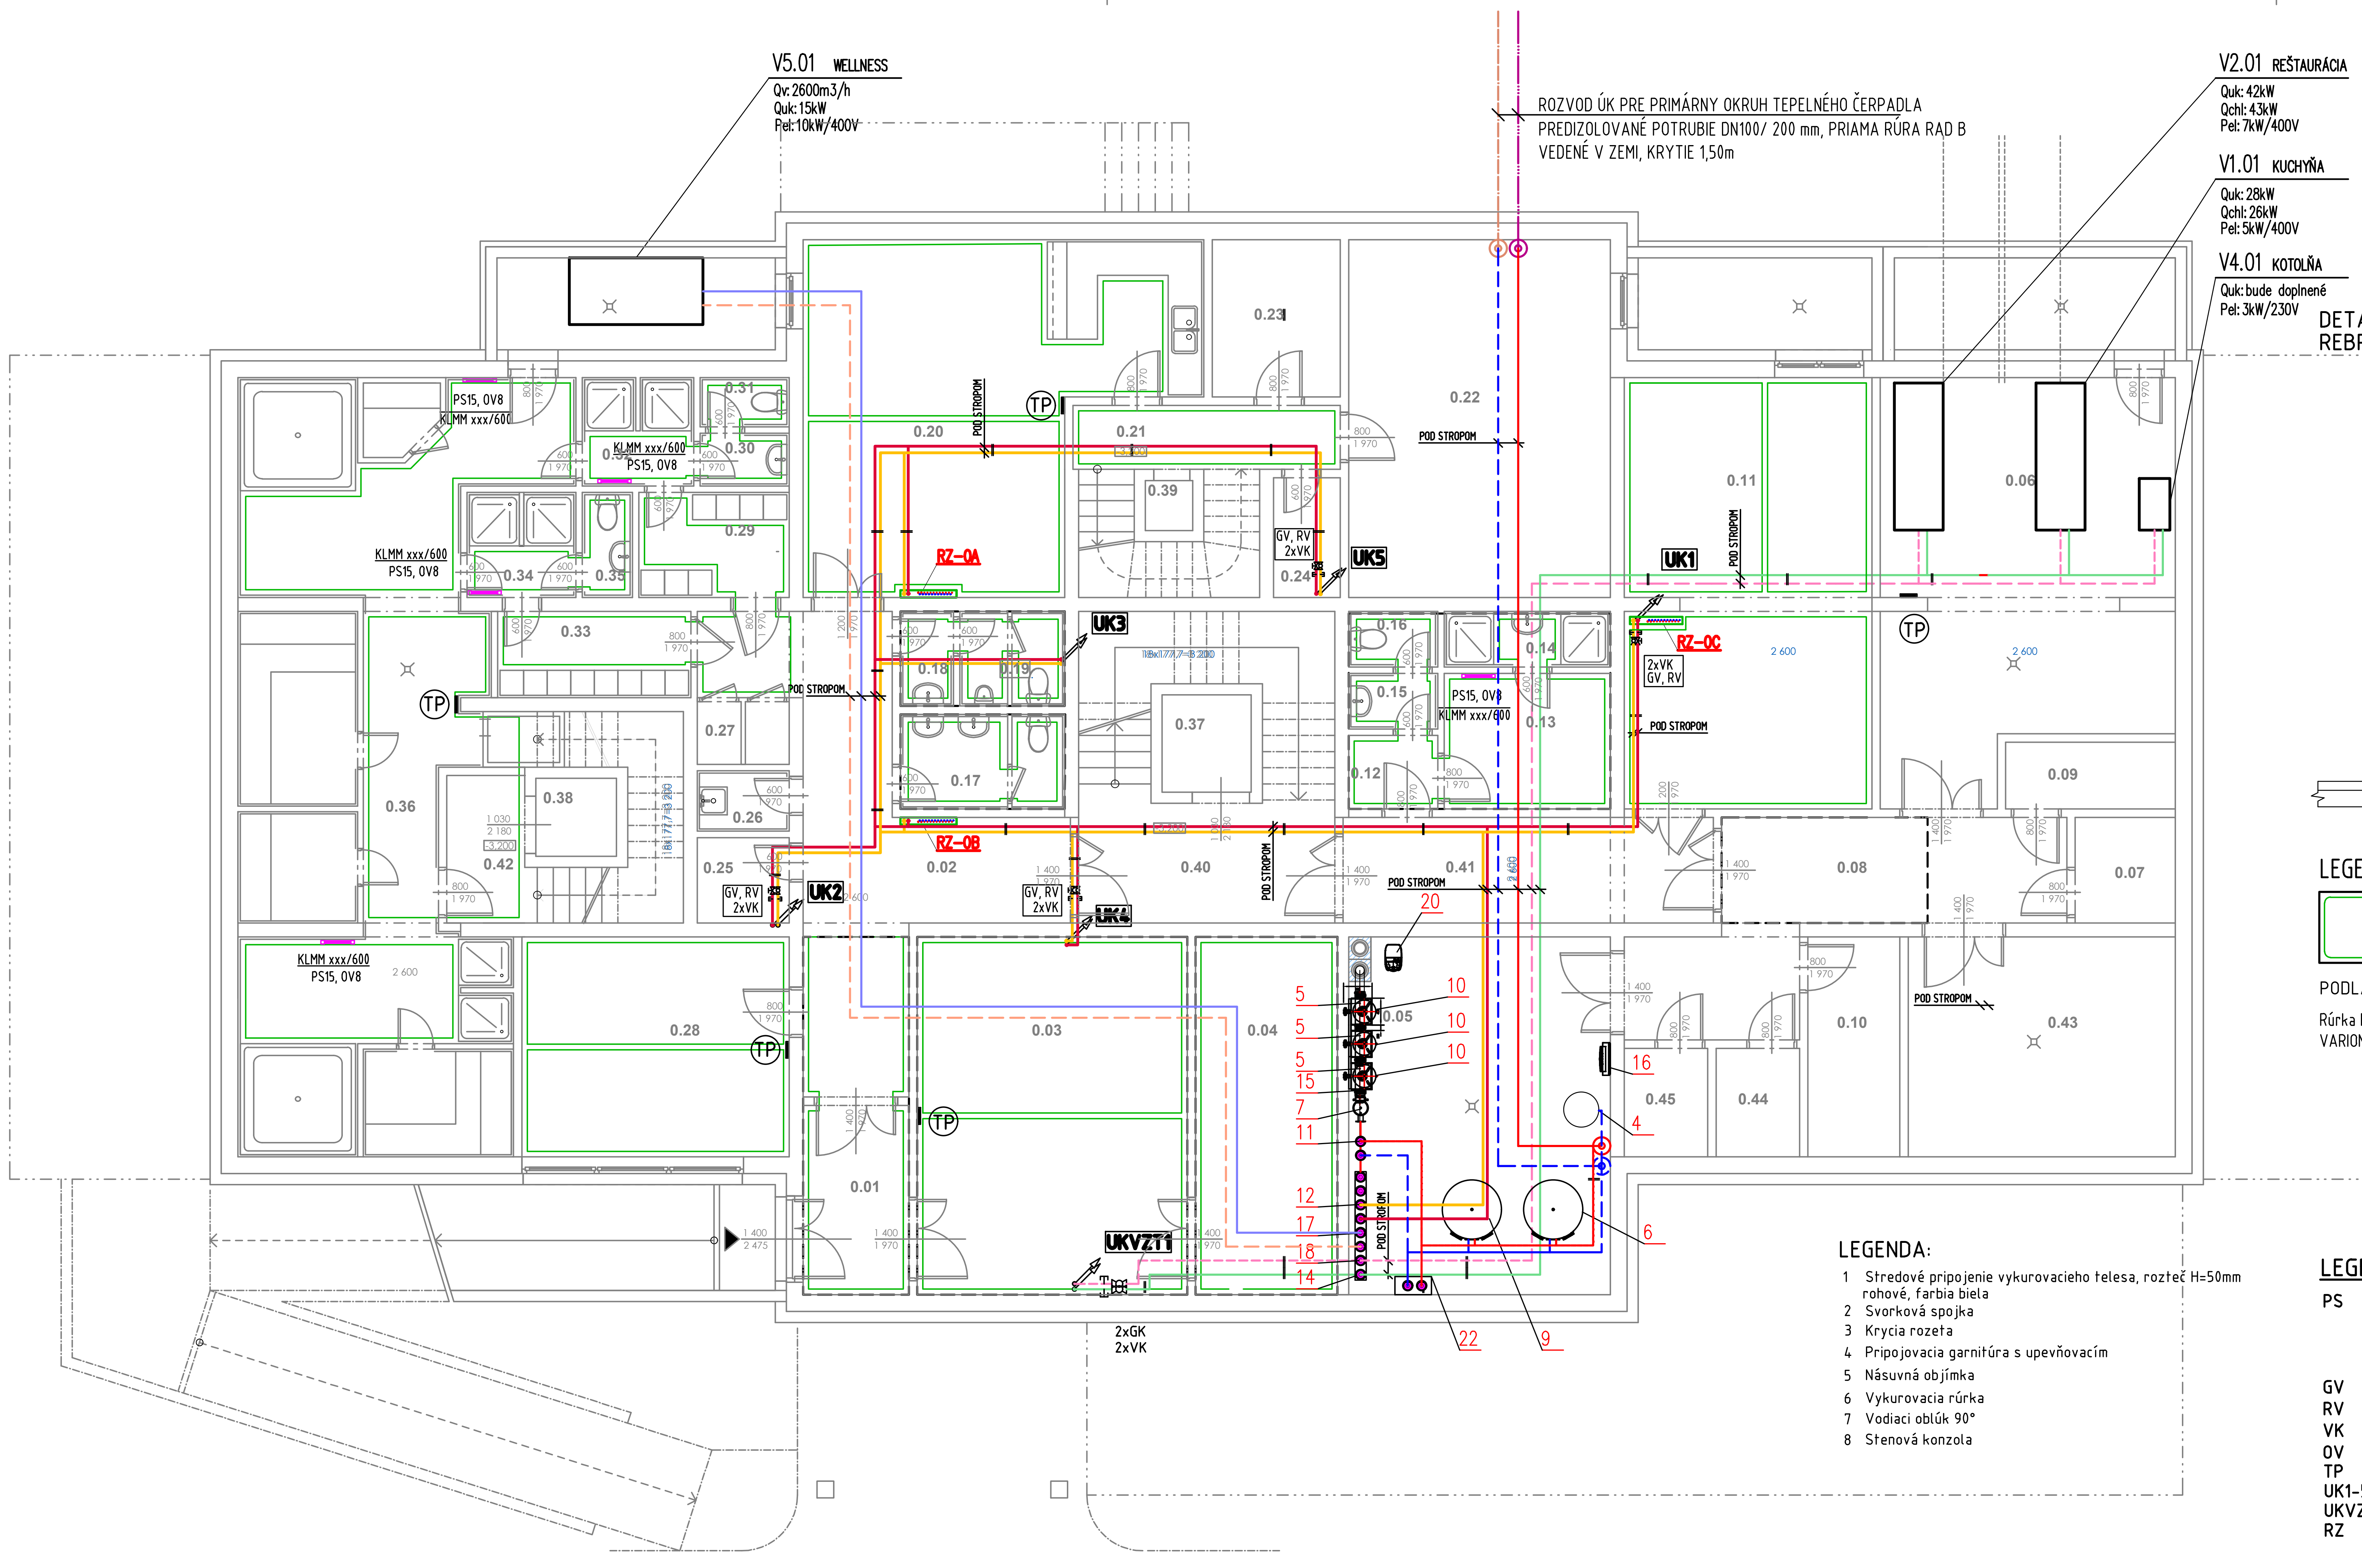

LEGENDA:

1 Stredové pripojenie vykurovacieho telesa, rozteč H=50mm rohové, farbia biela
2 Svorková spojka
3 Krycia rozeta
4 Pripojovacia garnitúra s upevňovacím
5 Násuvná objímka
6 Vykurovacia rúrka
7 Vodiaci oblúk 90°
8 Stenová konzola

DETAIL ZAPOJENIA VYKUROVACÍCH TELIES
REBRÍKOVÉ VYKUROVACIE TELESO

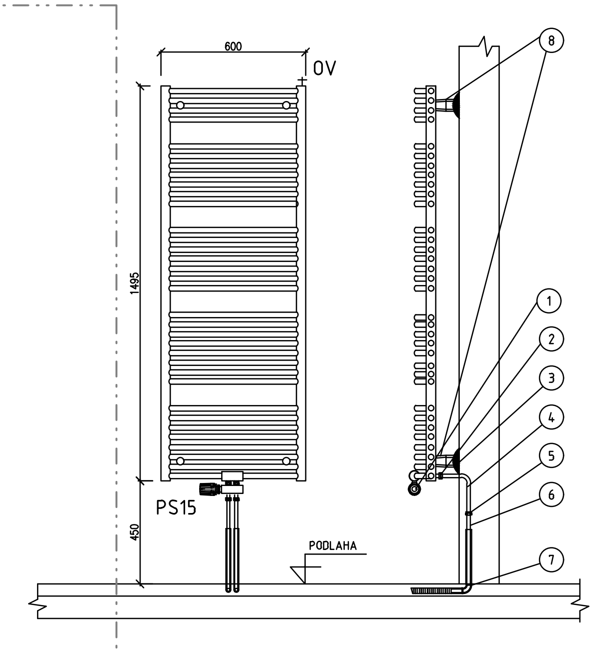

LEGENDA PODLAHOVÉHO VYKUROVANIA:

🟩

PODLAHOVÉ KÚRENIE REHAU

Rúrka RAUTHERM S 17x2,0	TYP VYKUROVACEJ RÚRKY
VARIONOVA	SYSTÉM PODLAHOVÉHO VYKUROVANIA

LEGENDA ZARIADENÍ A ARMATÚR :

PS	PRIPÁJACÍ BLOK S INTEGROVANÝM TERMOSTATICKÝM VENTILOM TYP BB PRE VYKUROVACIE TELESÁ SO STREDOVÝM PRIPOJENÍM, ROHOVÉ, DN15, PRIPOJENIE RADIÁTORA VONKAJŠÍ ZÁVIT 1/2", PRIPOJENIE DO STENY VONKAJŠÍ ZÁVIT 3/4" S TERMOSTATICKOU HLAVICOU NAPR. THERA-4 KLASIK S KVAPAL. SNÍMAČOM
GV	GUĽOVÝ VENTIL ZÁVITOVÝ
RV	PREDNASTAVITEĽNÝ REGULAČNÝ VENTIL PRIAMY - STAD
VK	VYPÚŠŤACÍ KOHÚT
OV	ODVZDUŠŇOVACÍ VENTIL
TP	PRIESTOROVÝ REGULÁTOR NEA SMART 2.0 PRE MERANIE TEPLOTY V MIESTNOSTI, FY. REHAU
UK1-5	STÚPAČKA VYKUROVANIA
UKVZT	STÚPAČKA VYKUROVANIA PRE OKRUH VZT ZARIADENÍ
RZ	ROZDELOVACIA STANICA PRE VYKUROVACIE TELESÁ A PODLAHOVĚ VYKUROVANIE

TABUĽKA MIESTNOSTÍ 1.PP

Č.M.	NÁZOV MIESTNOSTI	PLOCHA (m2)	PODLAHA
0.01	ZÁDVERIE	6,46	ker. dlažba
0.02	CHODBA	23,92	ker. dlažba
0.03	LYŽIAREŇ	31,16	ker. dlažba
0.04	SUŠIAREŇ	16,38	ker. dlažba
0.05	KOTOLŇA	29,88	ker. dlažba
0.06	TECH. MIESTNOSŤ (VZT)	36,29	ker. dlažba
0.07	SKLAD PRÁDLA - POUŽITÉ	3,42	ker. dlažba
0.08	CHODBA	17,96	ker. dlažba
0.09	SKLAD PRÁDLA - ČISTÉ	3,66	ker. dlažba
0.10	ELEKTROROZVODŇA	6,52	ker. dlažba
0.11	POSILŇOVŇA	34,24	ker. dlažba
0.12	ŠATŇA ZAM. PREDSIEŇ	2,11	ker. dlažba
0.13	ŠATŇA ZAM.	7,27	ker. dlažba
0.14	SPRCHA ZAM.	2,99	ker. dlažba
0.15	WC PREDSIEŇ ZAM.	1,60	ker. dlažba
0.16	WC ZAMESTN.	1,60	ker. dlažba
0.17	WC ŽENY	5,02	ker. dlažba
0.18	WC MUŽI PREDSIEŇ	1,62	ker. dlažba
0.19	WC MUŽI	3,20	ker. dlažba
0.20	VINÁREŇ	37,26	ker. dlažba
0.21	CHODBA	11,37	ker. dlažba
0.22	SKLAD POTRAVÍN	30,20	ker. dlažba
0.23	SKLAD NÁPOJOV	6,50	ker. dlažba
0.24	DENNÝ SKLAD	2,58	ker. dlažba
0.25	SKLAD	2,53	ker. dlažba
0.26	EKONOMAT	1,79	ker. dlažba
0.27	SKLAD UTERÁKOV	1,86	ker. dlažba
0.28	KANCELÁRIA	18,96	ker. dlažba
0.29	ŠATŇA MUŽI	5,09	ker. dlažba
0.30	WC PREDSIEŇ MUŽI	1,52	ker. dlažba
0.31	WC MUŽI	1,42	ker. dlažba
0.32	SPRCHY MUŽI	3,90	ker. dlažba
0.33	ŠATŇA ŽENY	5,38	ker. dlažba
0.34	SPRCHY ŽENY	3,69	ker. dlažba
0.35	WC ŽENY	1,70	ker. dlažba
0.36	WELLNESS	69,59	ker. dlažba
0.37	VÝŤAHOVÁ ŠACHTA	2,80	bet. poter
0.38	VÝŤAHOVÁ ŠACHTA	2,10	bet. poter
0.39	VÝŤAHOVÁ ŠACHTA	0,77	bet. poter
0.40	CHODBA	21,45	ker. dlažba
0.41	CHODBA	12,64	ker. dlažba
0.42	CHODBA	4,97	ker. dlažba
0.43	PRÁČOVŇA	18,96	ker. dlažba
0.44	HSP + EPS	2,93	ker. dlažba
0.45	CTSS (ZÁLOŽNÝ ZDROJ)	2,93	ker. dlažba

LEGENDA POTRUBIA:

SYSTÉMOVÁ RÚRA NAPR. GEBERIT MAPRESS - UHLÍKOVÁ OCEĽ S VONKAJŠÍM POZINKOVANÍM
OCEĽOVÉ ČIERNE BEZOŠVÉ HLADKÉ RÚRY, MATERIÁL 11 353.0 - POTRUBIE VEDENÉ POD STROPOM DO TECH.M.
POTRUBIE VEDENÉ POD STROPOM, PRI STENE, PRÍVOD A SPIATOČKA

ROZVOD ÚK PRE PRIMÁRNY OKRUH TEPELNÉHO ČERPADLA
PREDIZOLOVANÉ POTRUBIE , PRIAMA RÚRA RAD B
VEDENÉ V ZEMI, KRYTIE 1,50m

POTRUBIE - PLASTHLINNÍKOVÁ RÚRKA NAPR. GEBERIT MEPLA
SPÁJANÉ LISOVANÍM, IZOLOVANÉ POTRUBIE, TEPLOTNÝ SPÁD 45/35°C
POTRUBIE VEDENÉ V PODLAHE, V ŠACHTE, PRE PODLAHOVÉ VYKUROVANIE, PRÍVOD A SPIATOČKA

PROJEKTOVANÉ POTRUBIE Z UŠĽACHTILEJ OCELE NAPR. GEBERIT MAPRESS
SPÁJANÉ LISOVANÍM, IZOLOVANÉ POTRUBIE, TEPLOTNÝ SPÁD 70/50°C
POTRUBIE VEDENÉ POD STROPOM, PRE OHREV VZT JEDNOTKY, PRÍVOD A SPIATOČKA

LEGENDA ZARIADENÍ:

POZ.	NÁZOV, ROZMER	P. KS
1	TEPELNÉ ČERPADLO CARRIER 61AQ 120P TEP.VÝKON 35,4–115kW (A7/W35) CHLAD.VYKON 26,9–105kW (A35/W7) MAX. VÝSTUPNÁ TEPLOTA 75°C, CHLADIVO R290 GWP3 DVA SAMOSTATNE CHLADIVOVE OKRUHY S DVOMI MODULOVANÝMI KOMPRESORMI	1
1a	ANTIVIBRACNE BLOKY – SILENT BLOKY – SADA opcia 308	1
1b	REGULÁCIA TEP.ČERPADLA SmartVu – v rozsahu dodavky pol.1	1
1c	EC–ELEKTRONICKY RIADENY VENTILATOR – v rozsahu dodavky pol.1	2
1d	SNIMAC VONKAJSEJ TEPLOTY – opcia 312	1
1e	ODLUCOVAC CHLADIVA PROPÁN S ODVZDUSNOVACIM VENTILOM – v rozsahu dodavky pol.1	2
1f	TERMOSTATICKY VENTIL PROTI ZAMRZNUTIU – v rozsahu dodavky pol.1	2
1g	OBEHOVE CERPADLO S REGULÁCIOU OTÁČOK – opcia 116V	2
1h	EXPANZNÁ NÁDOBA OBJEM 8L – opcia 116V	1
1i	SADA FILTRA NA SYSTEM (treba namontovat) – v rozsahu dodavky pol.1	1
1j	POISTNY VENTIL PRE SYSTEM 4bar – v rozsahu dodavky pol.1	1
2	ODLUCOVAC SPIROTRAP S MAGNETOM DN80 PRIRUBOVY (7784180)	1
3	PODSTAVNA SADA S CERPADLOM PRE KOTOL VITODENS 200W – v dodavke pol.5	3
4	EXPANZNÁ NÁDOBA N200, OBJEM 200L, 6bar STRIEBORNA	1
5	3xNASTENNY KONDENZAČNÝ KOTOL VITODENS 200–W 12–49kW+KASKADOVA REGULACIA (B2HAI59) MENOVITÝ TEPELNÝ PRÍKON 11,2 až 45,7 kW, SÁLAVÝ HORÁK MATRIX, spotreba 4,84m3/hod	1
6	AKUM.ZÁSOBNÍK PRE UK VITOCELL 050–HC EC PRO SH1000HA OBJEM 1000L (Z028041)	1
7	HYDRAULIC.VYROVNAVAC TLAKOV S IZOLACIOU DN80 (ZK02627)	1
8	TROJCESTNY PREPINACI VENTIL TUV/UK DN50+SERVOPOHON 24V – opcia 347A	1
9	AKUM.ZÁSOBNÍK PRE OHREV TUV VITOCELL 050–HC EC PRO SH1000HA OBJEM 1000L (Z028041)	1
10	EXPANZNÁ NÁDOBA OBJEM 50L N50 6bar BIELA (7938085)	3
11	RYCHLOMONTAZNA SADA M31 BEZ ZMIESAVACA DN50 MAGNA3 50–80F (ZK01663)	1
12	RYCHLOMONTAZNA SADA M32 SO ZMIESAVACOM DN50 MAGNA3 50–80F (ZK01668)	1
13	SERVOPOHON SR10 230V/50Hz (7199567)	2
14	MODULARNY ROZDELOVAC PRE TRI OKRUHY –TYP 200/120, DN100, DL.1950mm, REFLEX SINUS HYDROFIXX	1
15	SPALINOVA KASKADA PRE TRI KOTLY 49kW DN160 (ZK00678)	1
16	KASKADOVA REGULACIA VITOTRONIC 300–K TYP MW2B – v dodavke pol.5	1
17	RYCHLOMONTAZNA SADA M32 SO ZMIESAVACOM DN32 ALPHA2+ 32–60 (7741080)	1
18	RYCHLOMONTAZNA SADA M31 BEZ ZMIESAVACA DN50 MAGNA3 50–120F (ZK01665)	1
19	MECHANIC.FILTER SO SPATNYM PREPLACHOM TYP DM DN20(7315966)	1
20	ÚPRAVŇA VODY PRE VYKUROVANIE AQUASET 500–N (7938283)	1
21	PLNIACE ZARIADENIE FULLCOMBI PLUS DN15 (ZK05478)	1
22	MODUL PRE PRIPRAVU TEPLEJ UZITKOVEJ VODY VITOTRANS 353 TYP PBSA do 48L/min(Z021864)	1
23	CIRKULACNE CERPADLO – dodavka ZTI	1
T1	SNIMAC VYSTUPNEJ TEPLOTY (7426463)	2
T2	SNIMAC TEPLOTY ZASOBNIKA – opcia 312A	1
T3	SNIMAC TEPLOTY ZASOBNIKA – v dodavke opcia 347A	1
T4	SNIMAC VONKAJSEJ TEPLOTY – v rozsahu dodavky pol.16	1
T5	SNIMAC TEPLOTY HYDRAULICKEJ VÝHYBKY – v rozsahu dodavky pol.16	1
T6	PONORNY SNIMAC TEPLOTY – v rozsahu dodavky pol.16	1

POZNÁMKA :

- V PRÍPADE NEJASNOSTÍ VO VÝKRESOVEJ DOKUMENTÁCIÍ KONTAKTOVAŤ ZODPOVEDNÉHO PROJEKTANTA
- VŠETKY ROZMERY STAVEBNÝCH PRÁC KONTROLOVAŤ NA MIESTE STAVBY
- PRED UVEDENÍM SYSTÉMU DO PREVÁDZKY JE POTREBNÉ VYKONAŤ DÔKLADNÝ PREPLACH SYSTÉMU S VYČISTENÍM VŠETKÝCH FILTROV NA ROZVODE
- PO NAPUSTENÍ SYSTÉMU JE POTREBNÉ VYKONAŤ JEHO ODVZDUŠNENIE
- DODÁVATEL STAVBY JE POVINNÝ REALIZOVAŤ VŠETKY PRÁCE V ZMYSLE PLATNÝCH STN EN S DODRŽANÍM TECHNOLOGICKÝCH A BEZPEČNOSTNÝCH POSTUPOV. ĎALEJ JE POVINNÝ REŠPEKTOVAŤ USTANOVENIÁ STN 730421 O PRÍSLUŠNÝCH ROZMEROVÝCH ODCHÝLKACH REALIZOVANÝCH KONŠTRUKCIÍ PROTI PROJEKTOVANÉMU STAVU. KAŽDÚ ODCHÝLKU OD PROJEKTU JE POTREBNÉ PREROKOVAŤ S GP.
- PRESTUPY INŽINIER
- PROJEKTOVÁ DOKU

OBJEDNÁV
O&L, s.r.o., Št
058 01 Popra

STUPEŇ PD
DSP

DATUM SPR
03/2025