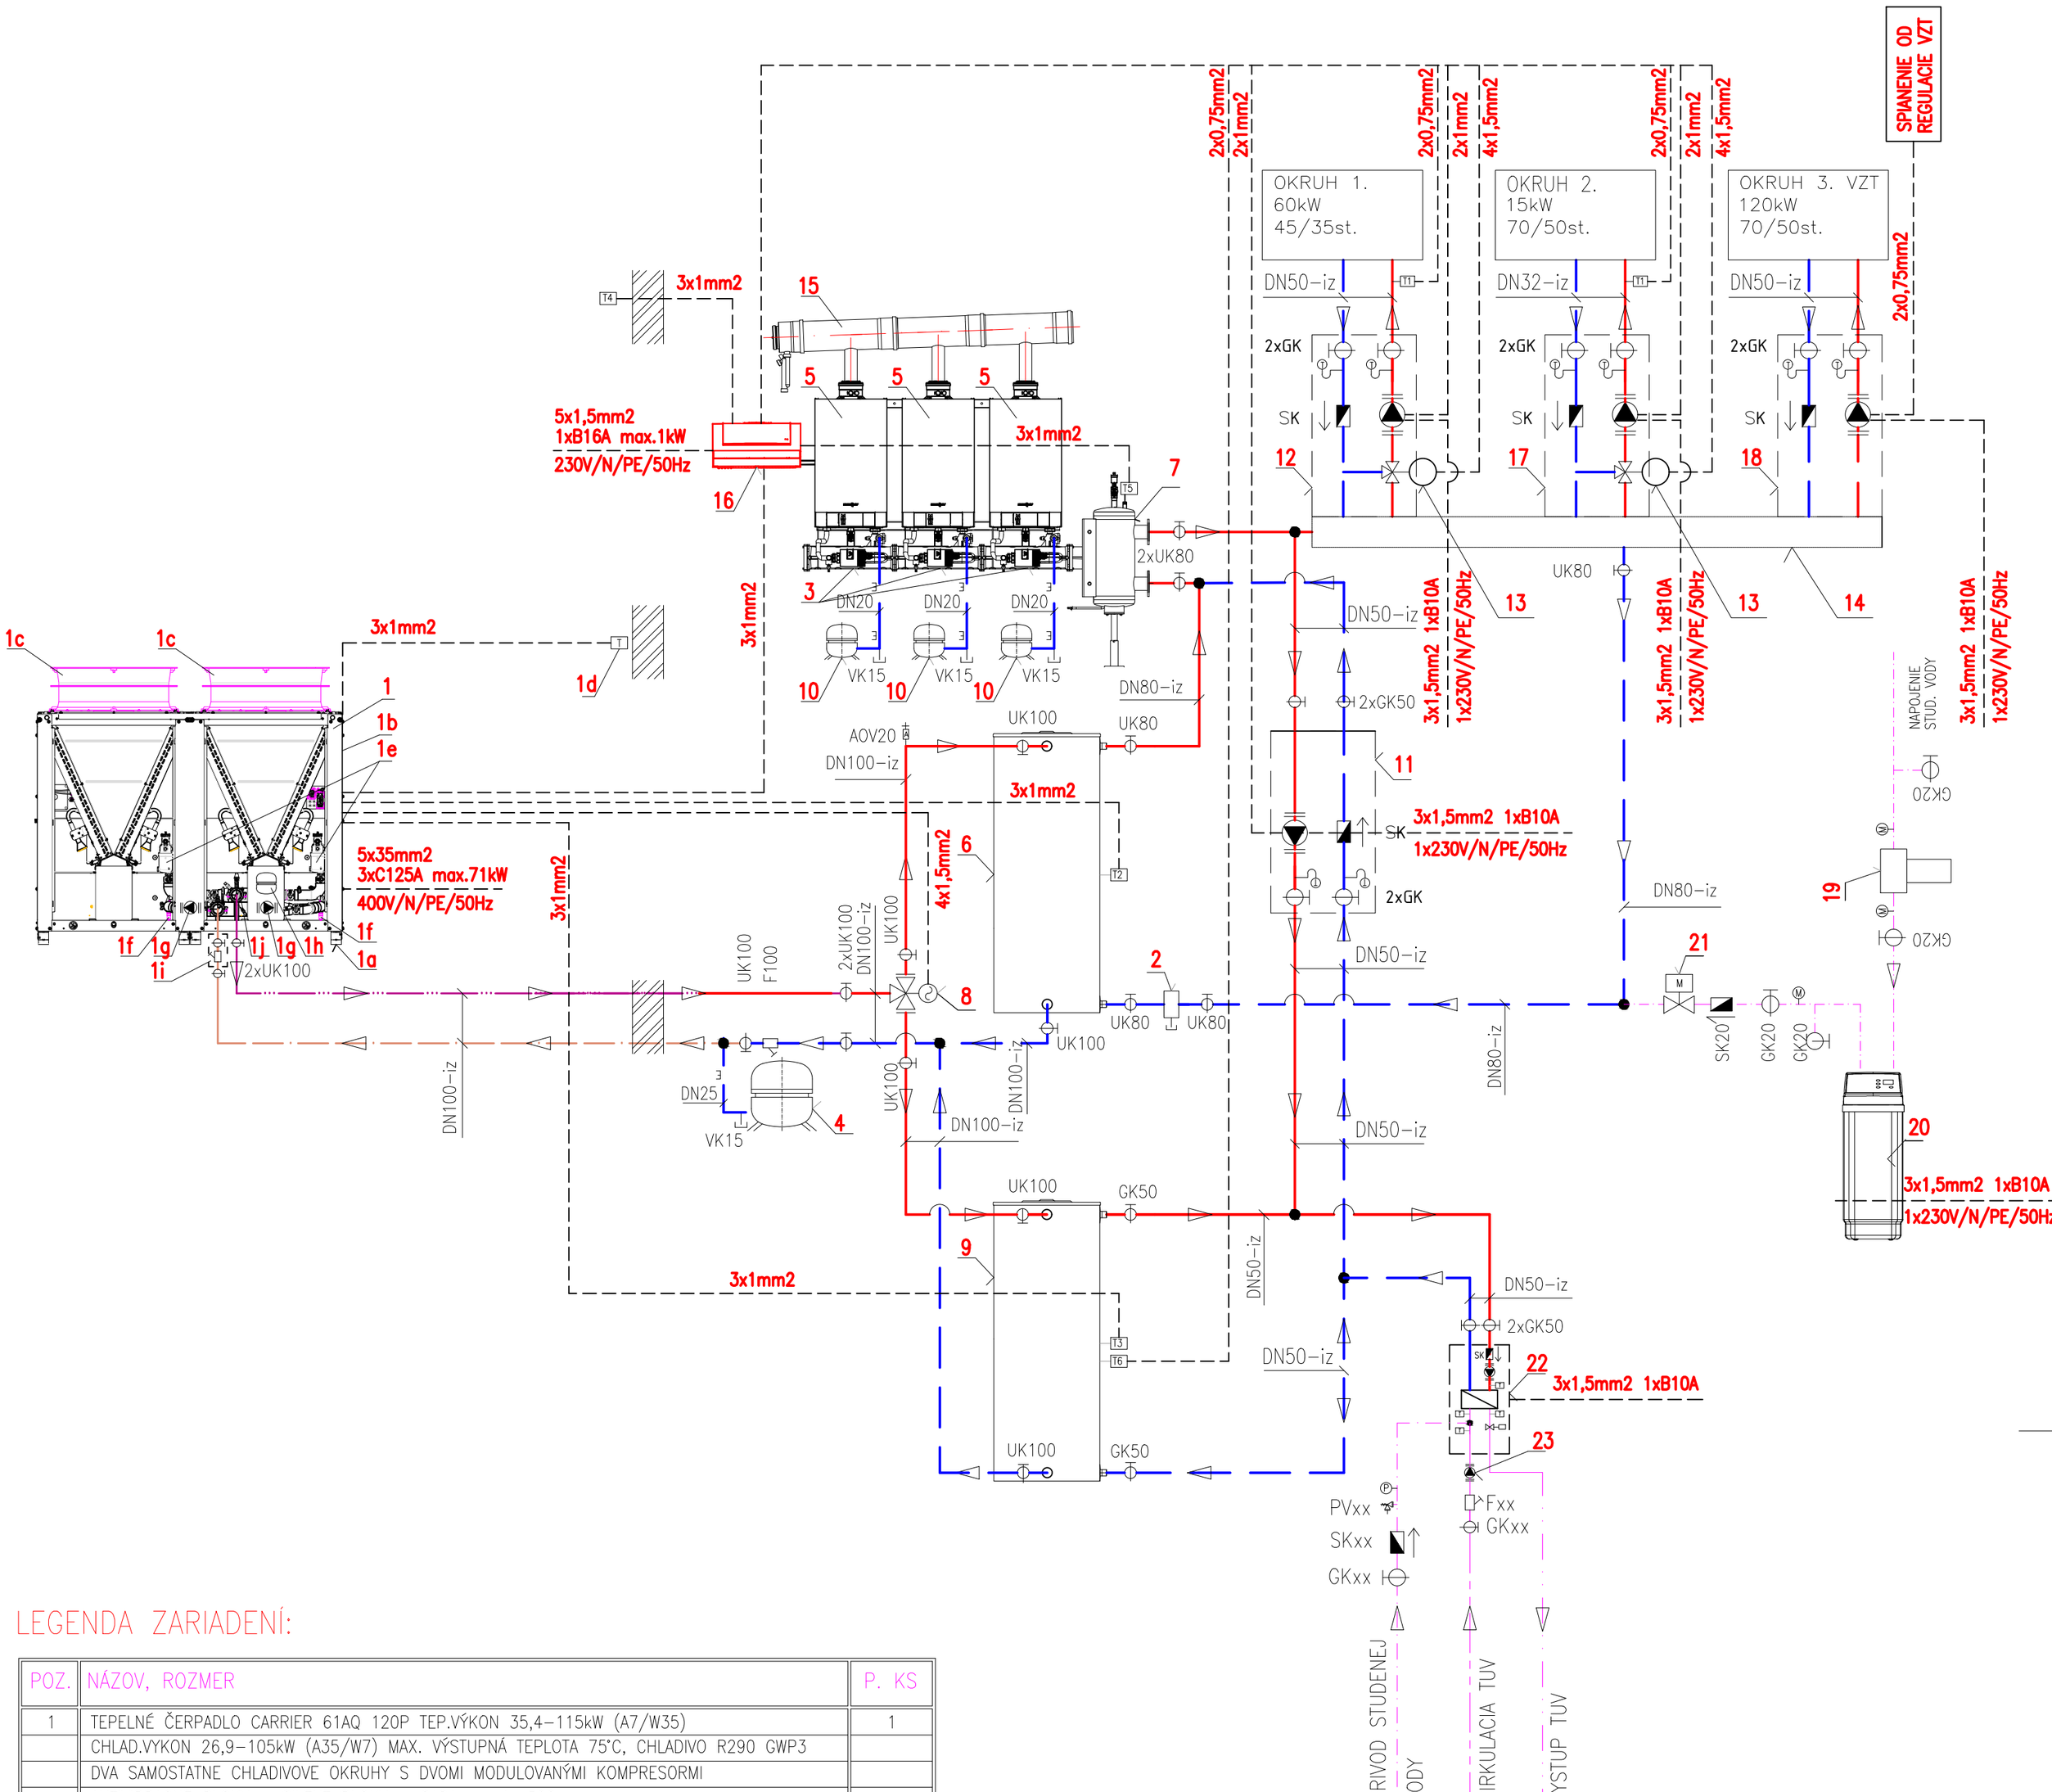


LEGENDA ZARIADENÍ:

POZ.	NÁZOV, ROZMER	P. KS
1	TEPELNÉ ČERPADLO CARRIER 61AQ 120P TEP.VÝKON 35,4–115kW (A7/W35)	1
	CHLAD.VYKON 26,9–105kW (A35/W7) MAX. VÝSTUPNÁ TEPLOTA 75°C, CHLADIVO R290 GWP3	
	DVA SAMOSTATNE CHLADIVOVE OKRUHY S DVOMI MODULOVANÝMI KOMPRESORMI	
1a	ANTIVIBRACNE BLOKY – SILENT BLOKY – SADA opcia 308	1
1b	REGULÁCIA TEP.ČERPADLA SmartVu – v rozsahu dodavky pol.1	1
1c	EC–ELEKTRONICKY RIADENY VENTILATOR – v rozsahu dodavky pol.1	2
1d	SNIMAC VONKAJSEJ TEPLOTY – opcia 312	1
1e	ODLUCOVAC CHLADIVA PROPÁN S ODVZDUSNOVACIM VENTILOM – v rozsahu dodavky pol.1	2
1f	TERMOSTATICKY VENTIL PROTI ZAMRZNUTIU – v rozsahu dodavky pol.1	2
1g	OBEHOVE CERPADLO S REGULÁCIOU OTÁČOK – opcia 116V	2
1h	EXPANZNÁ NÁDOBA OBJEM 8L – opcia 116V	1
1i	SADA FILTRA NA SYSTEM (treba namontovat) – v rozsahu dodavky pol.1	1
1j	POISTNY VENTIL PRE SYSTEM 4bar – v rozsahu dodavky pol.1	1
2	ODLUCOVAC SPIROTRAP S MAGNETOM DN80 PRIRUBOVY (7784180)	1
3	PODSTAVNA SADA S CERPADLOM PRE KOTOL VITODENS 200W – v dodavke pol.5	3
4	EXPANZNÁ NÁDOBA N200, OBJEM 200L, 6bar STRIEBORNA	1
5	3xNASTENNY KONDENZAČNÝ KOTOL VITODENS 200–W 12–49kW+KASKADOVA REGULACIA (B2HAI59) MENOVITÝ TEPELNÝ PRÍKON 11,2 až 45,7 kW, SÁLAVÝ HORÁK MATRIX, spotreba 4,84m3/hod	1
6	AKUM.ZÁSOBNÍK PRE UK VITOCELL 050–HC EC PRO SH1000HA OBJEM 1000L (Z028041)	1
7	HYDRAULIC.VYROVNAVAC TLAKOV S IZOLACIOU DN80 (ZK02627)	1
8	TROJCESTNY PREPINACI VENTIL TUV/UK DN50+SERVOPOHON 24V – opcia 347A	1
9	AKUM.ZÁSOBNÍK PRE OHREV TUV VITOCELL 050–HC EC PRO SH1000HA OBJEM 1000L (Z028041)	1
10	EXPANZNÁ NÁDOBA OBJEM 50L N50 6bar BIELA (7938085)	3
11	RYCHLOMONTAZNA SADA M31 BEZ ZMIESAVACA DN50 MAGNA3 50–80F (ZK01663)	1
12	RYCHLOMONTAZNA SADA M32 SO ZMIESAVACOM DN50 MAGNA3 50–80F (ZK01668)	1
13	SERVOPOHON SR10 230V/50Hz (7199567)	2
14	MODULARNY ROZDELOVAC PRE TRI OKRUHY –TYP 200/120, DN100, DL.1950mm, REFLEX SINUS HYDROFIXX	1
15	SPALINOVA KASKADA PRE TRI KOTLY 49kW DN160 (ZK00678)	1
16	KASKADOVA REGULACIA VITOTRONIC 300–K TYP MW2B – v dodavke pol.5	1
17	RYCHLOMONTAZNA SADA M32 SO ZMIESAVACOM DN32 ALPHA2+ 32–60 (7741080)	1
18	RYCHLOMONTAZNA SADA M31 BEZ ZMIESAVACA DN50 MAGNA3 50–120F (ZK01665)	1
19	MECHANIC.FILTER SO SPATNYM PREPLACHOM TYP DM DN20(7315966)	1
20	ÚPRAVŇA VODY PRE VYKUROVANIE AQUASET 500–N (7938283)	1
21	PLNIACE ZARIADENIE FULLCOMBI PLUS DN15 (ZK05478)	1
22	MODUL PRE PRIPRAVU TEPLEJ UZITKOVEJ VODY VITOTRANS 353 TYP PBSA do 48L/min(Z021864)	1
23	CIRKULACNE CERPADLO – dodavka ZTI	1
T1	SNIMAC VYSTUPNEJ TEPLOTY (7426463)	2
T2	SNIMAC TEPLOTY ZASOBNIKA – opcia 312A	1
T3	SNIMAC TEPLOTY ZASOBNIKA – v dodavke opcia 347A	1
T4	SNIMAC VONKAJSEJ TEPLOTY – v rozsahu dodavky pol.16	1
T5	SNIMAC TEPLOTY HYDRAULICKEJ VÝHYBKY – v rozsahu dodavky pol.16	1
T6	PONORNY SNIMAC TEPLOTY – v rozsahu dodavky pol.16	1

LEGENDA POTRUBIA:

SYSTÉMOVÁ RÚRA NAPR. GEBERIT MAPRESS - UHLÍKOVÁ OCEĽ S VONKAJŠÍM POZINKOVANÍM
OCEĽOVÉ ČIERNE BEZOŠVÉ HLADKÉ RÚRY, MATERIÁL 11 353.0 - POTRUBIE VEDENÉ POD STROPOM DO TECH.M.
POTRUBIE VEDENÉ POD STROPOM, PRI STENE, PRÍVOD A SPIATOČKA

ROZVOD ÚK PRE PRIMÁRNY OKRUH TEPELNÉHO ČERPADLA
PREDIZOLOVANÉ POTRUBIE , PRIAMA RÚRA RAD B
VEDENÉ V ZEMI, KRYTIE 1,50m

POTRUBIE - PLASTHLINNÍKOVÁ RÚRKA NAPR. GEBERIT MEPLA
SPÁJANÉ LISOVANÍM, IZOLOVANÉ POTRUBIE, TEPLOTNÝ SPÁD 45/35°C
POTRUBIE VEDENÉ V PODLAHE, V ŠACHTE, PRE PODLAHOVÉ VYKUROVANIE, PRÍVOD A SPIATOČKA

PROJEKTOVANÉ POTRUBIE Z UŠĽACHTILEJ OCELE NAPR. GEBERIT MAPRESS
SPÁJANÉ LISOVANÍM, IZOLOVANÉ POTRUBIE, TEPLOTNÝ SPÁD 70/50°C
POTRUBIE VEDENÉ POD STROPOM, PRE OHREV VZT JEDNOTKY, PRÍVOD A SPIATOČKA

OBJEDNÁVATEĽ: O&L, s.r.o., Štefánska 3793/22, 058 01 Poprad	STAVBA: **CHATA NA JANKOVEJ LÚKE** prestavba pôvodnej Jankovej koliby Štrba, Štrbské Pleso, ul. K vodopádom, č. 4095/17		**ZODP. PROJEKTANT:** Ing.
STUPEŇ PD: DSP			**VYPRACOVAL:** Bc. Viktor Labovský
DATUM SPRACOVANIA: 03/2025	**OBSAH VÝKRESU:** **SCHEMA ZAPOJENIA**	**MIERKA:**	**Č. VÝKRESU:** 06