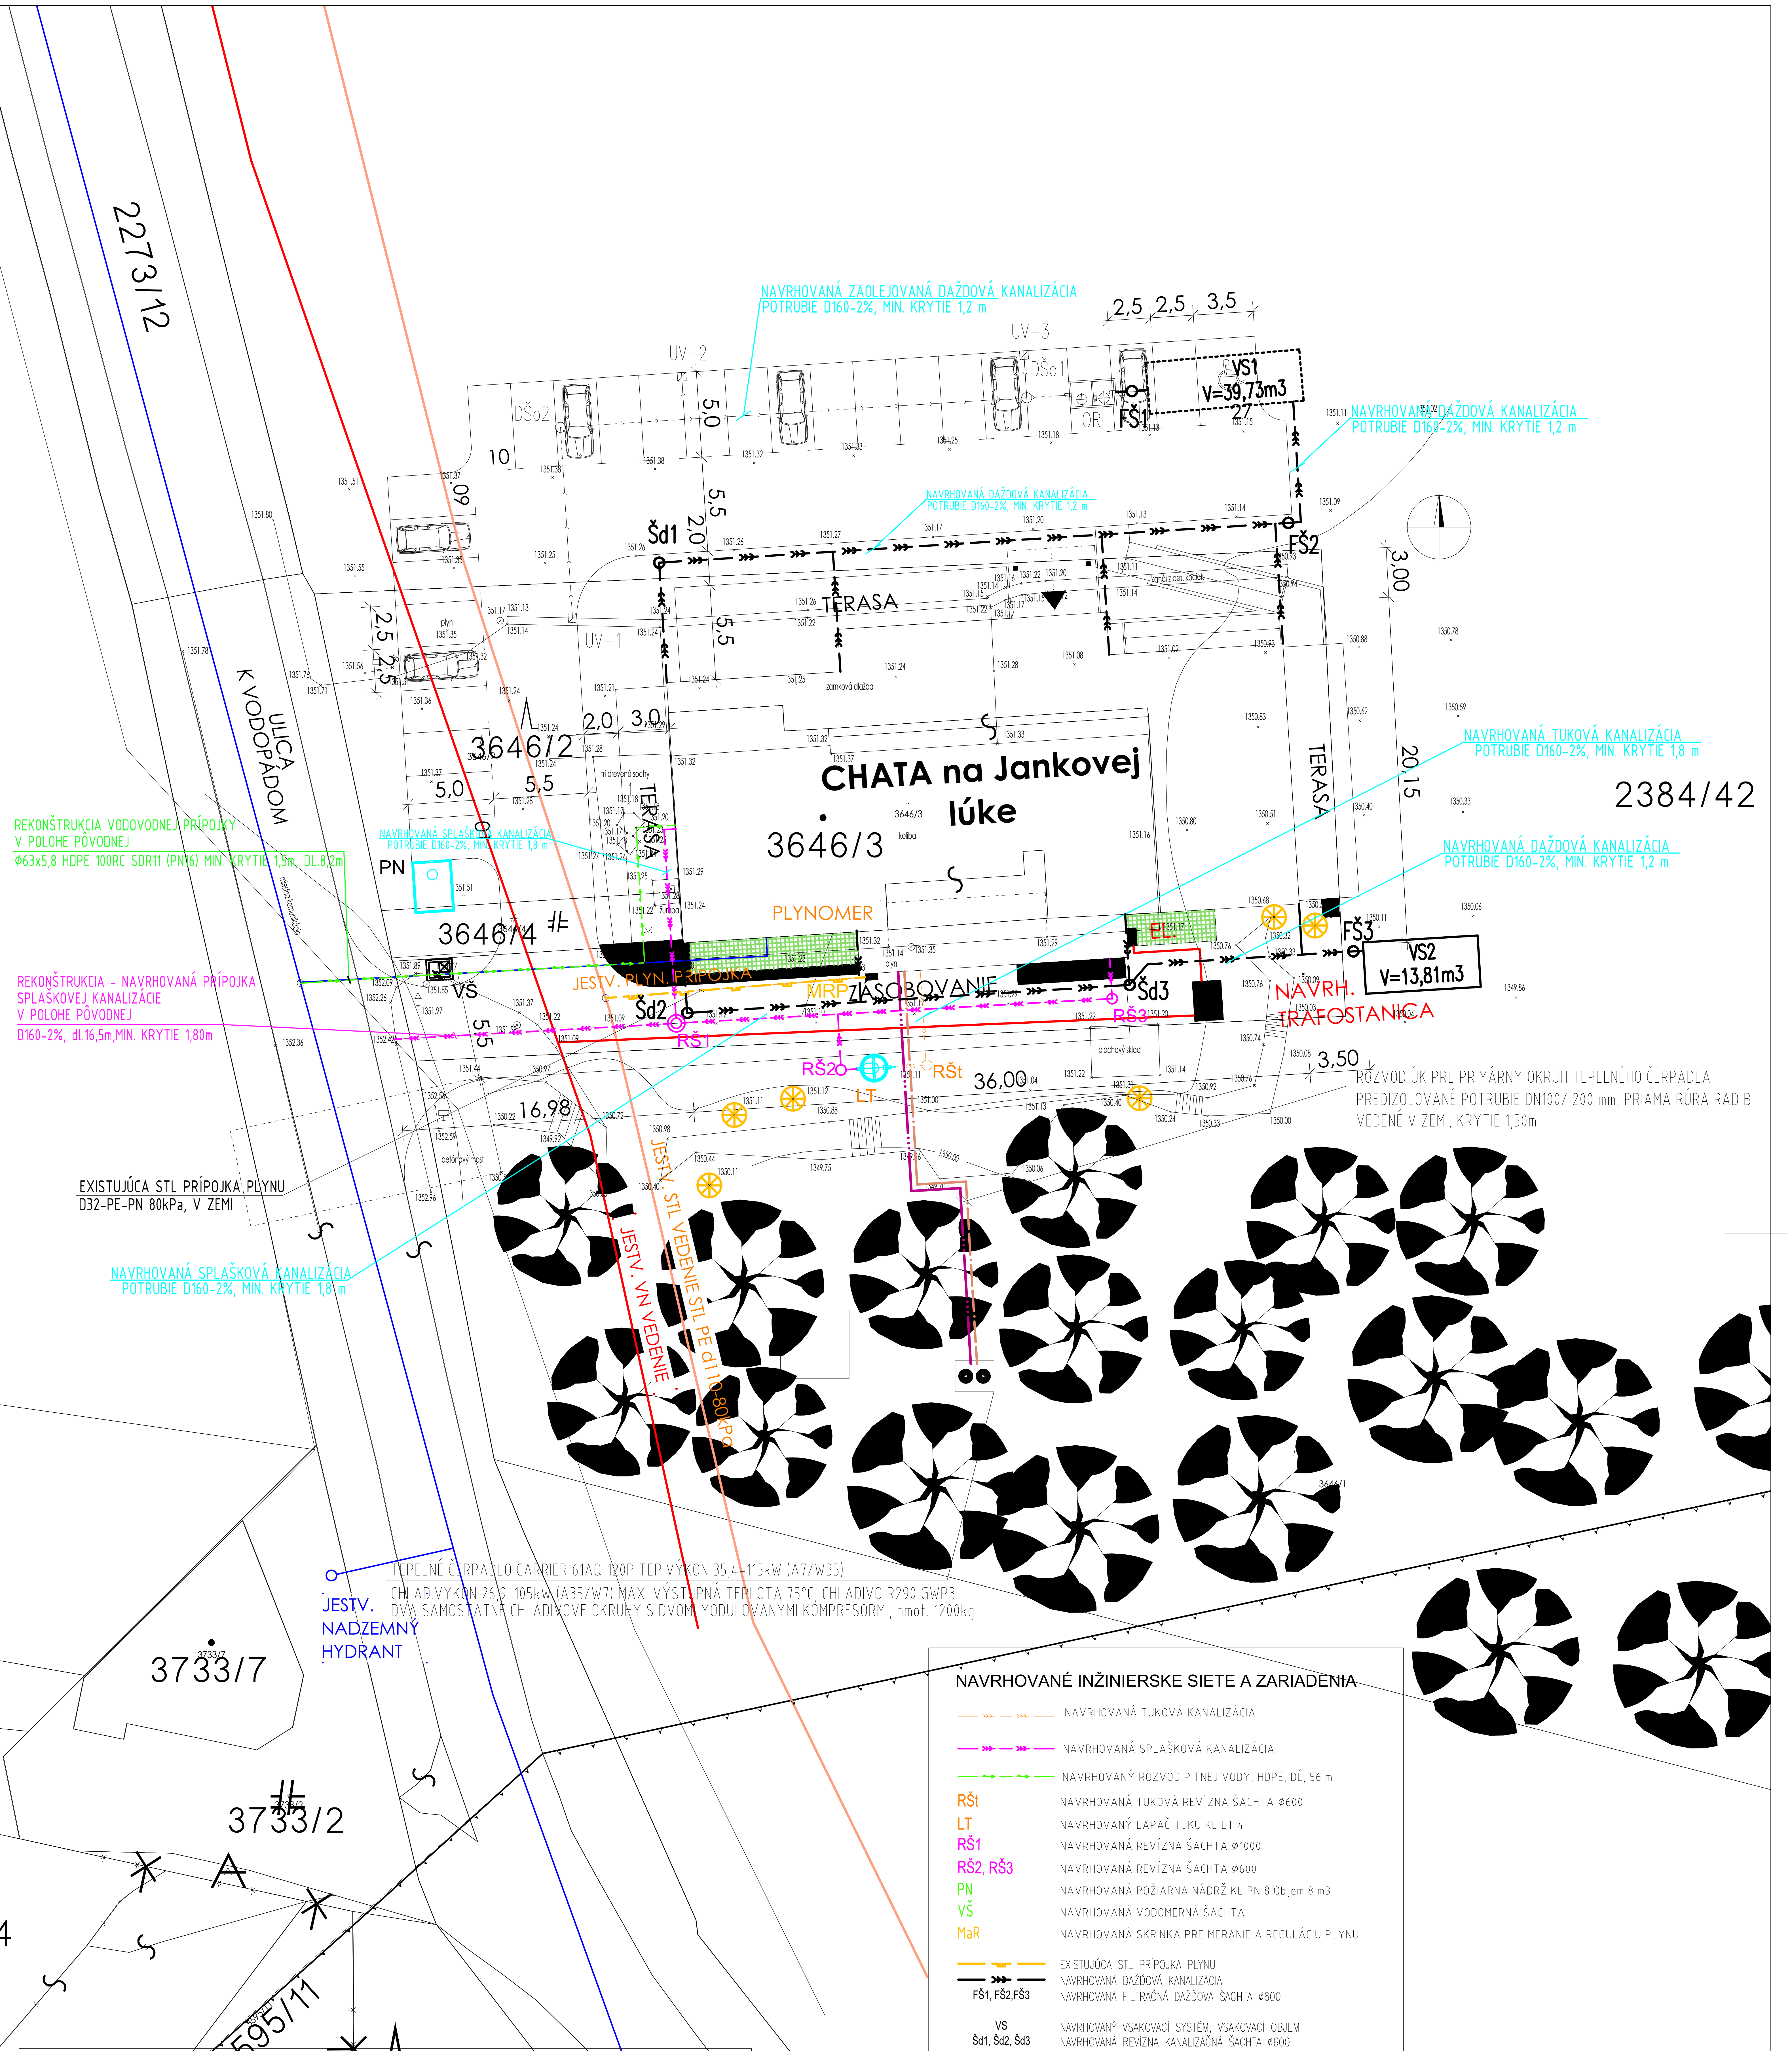
2273/12
ULICA K VODOPÁDOM
miestna komunikácia
NAVRHOVANÁ ZAOLEJOVANÁ DAŽDOVÁ KANALIZÁCIA
POTRUBIE D160-2%, MIN. KRYTIE 1,2 m
UV-2
UV-3
UV-1
DŠo1
DŠo2
ORL
FŠ1
FŠ2
FŠ3
VS1
V=39,73m3
VS2
V=13,81m3
NAVRHOVANÁ DAŽDOVÁ KANALIZÁCIA
POTRUBIE D160-2%, MIN. KRYTIE 1,2 m
Šd1
Šd2
Šd3
TERASA
zamková dlažba
kanál z bet. kociek
3646/2
3646/3
3646/4
2384/42
CHATA na Jankovej lúke
koliba
tri drevené sochy
žumpa
plyn
PLYNOMER
EL.
NAVRH. TRAFOSTANICA
NAVRHOVANÁ TUKOVÁ KANALIZÁCIA
POTRUBIE D160-2%, MIN. KRYTIE 1,8 m
REKONŠTRUKCIA VODOVODNEJ PRÍPOJKY
V POLOHE PÔVODNEJ
Ø63x5,8 HDPE 100RC SDR11 (PN16) MIN. KRYTIE 1,5m, DL.8,2m
NAVRHOVANÁ SPLAŠKOVÁ KANALIZÁCIA
POTRUBIE D160-2%, MIN. KRYTIE 1,8 m
PN
VŠ
REKONŠTRUKCIA - NAVRHOVANÁ PRÍPOJKA
SPLAŠKOVEJ KANALIZÁCIE
V POLOHE PÔVODNEJ
D160-2%, dl.16,5m,MIN. KRYTIE 1,80m
JESTV. PLYN. PRÍPOJKA
MRP
ZÁSOBOVANIE
RŠ1
RŠ2
RŠ3
RŠt
LT
plechový sklad
betónový most
EXISTUJÚCA STL PRÍPOJKA PLYNU
D32-PE-PN 80kPa, V ZEMI
ROZVOD ÚK PRE PRIMÁRNY OKRUH TEPELNÉHO ČERPADLA
PREDIZOLOVANÉ POTRUBIE DN100/ 200 mm, PRIAMA RÚRA RAD B
VEDENÉ V ZEMI, KRYTIE 1,50m
JESTV. STL VEDENIE STL PE d110 80kPa
JESTV. VN VEDENIE
TEPELNÉ ČERPADLO CARRIER 61AQ 120P TEP.VÝKON 35,4-115kW (A7/W35)
CHLAD.VYKON 26,9-105kW (A35/W7) MAX. VÝSTUPNÁ TEPLOTA 75°C, CHLADIVO R290 GWP3
DVA SAMOSTATNE CHLADIVOVE OKRUHY S DVOM MODULOVANÝMI KOMPRESORMI, hmot. 1200kg
JESTV. NADZEMNÝ HYDRANT
3733/7
3733/2
3595/11
3595/12
2,5
2,5
3,5
5,0
5,5
2,0
3,0
10
3,00
20,15
16,98
36,00
3,50
27

NAVRHOVANÉ INŽINIERSKE SIETE A ZARIADENIA

— ››› — ››› —	NAVRHOVANÁ TUKOVÁ KANALIZÁCIA
— ››› — ››› —	NAVRHOVANÁ SPLAŠKOVÁ KANALIZÁCIA
— → — → —	NAVRHOVANÝ ROZVOD PITNEJ VODY, HDPE, DĹ, 56 m
RŠt	NAVRHOVANÁ TUKOVÁ REVÍZNA ŠACHTA ⌀600
LT	NAVRHOVANÝ LAPAČ TUKU KL LT 4
RŠ1	NAVRHOVANÁ REVÍZNA ŠACHTA ⌀1000
RŠ2, RŠ3	NAVRHOVANÁ REVÍZNA ŠACHTA ⌀600
PN	NAVRHOVANÁ POŽIARNA NÁDRŽ KL PN 8 Objem 8 m3
VŠ	NAVRHOVANÁ VODOMERNÁ ŠACHTA
MaR	NAVRHOVANÁ SKRINKA PRE MERANIE A REGULÁCIU PLYNU
— — —	EXISTUJÚCA STL PRÍPOJKA PLYNU
— ››› —	NAVRHOVANÁ DAŽĎOVÁ KANALIZÁCIA
FŠ1, FŠ2,FŠ3	NAVRHOVANÁ FILTRAČNÁ DAŽĎOVÁ ŠACHTA ⌀600
VS	NAVRHOVANÝ VSAKOVACÍ SYSTÉM, VSAKOVACÍ OBJEM
Šd1, Šd2, Šd3	NAVRHOVANÁ REVÍZNA KANALIZAČNÁ ŠACHTA ⌀600
— › —	NAVRHOVANÁ ZAOLEJOVANÁ DAŽĎOVÁ KANALIZÁCIA
UV-1	NAVRHOVANÝ ULIČNÝ VTOK, S KLAPKOU PROTI ZÁPACHU
DŠ01	NAVRHOVANÁ ZAOLEJOVANÁ REVÍZNA ŠACHTA ⌀600
ORL	NAVRHOVANÝ ODLUČOVAČ ROPNÝCH LÁTOK typ Klartec KL 15/1 sll

POZNÁMKY

- priebeh inžinierskych podzemných sietí bol zakreslený informatívne, pred začatím výkopových prác je nutné ich vytýčenie
- pred začatím každého výkopu, vrtu, alebo sondy je potrebné zrealizovať fyzické vytýčenie každého podzemného objektu jeho majiteľom, správcom alebo prevádzkovateľom
- pred realizáciou každého napojenia na inžinierske siete je potrebné pred začatím prác najskôr odhaliť a premerať bod napojenia
- pri realizácii a križovaní vedení musia byť dodržané dotknuté ustanovenia STN, ON a technologických predpisov
- pri realizácii jednotlivých vedení treba dodržať STN 73 6005 - Priestorová úprava vedení technického vybavenia
- projektant nenesie žiadnu zodpovednosť za zmeny uskutočnené bez jeho písomného súhlasu
- zhotoviteľ je povinný o zistených nezrovnalostiach v projektovej dokumentácii neodkladne informovať projektanta
- rozdiely zistené na stavbe oproti PD je nutné v technickom riešení odsúhlasiť s projektantom ešte pred samotnou realizáciou
- obsah výkresu je duševným vlastníctvom autorov a jeho použitie na iný účel podlieha autorskému zákonu

OBJEDNÁV

STUPEŇ PD:
DSP

DATUM SPR
03/2025