ROZVODY VODA + ODPAD v predstene

Jestvujúce odpadové potrubie 110mm
v priestore zo stropu

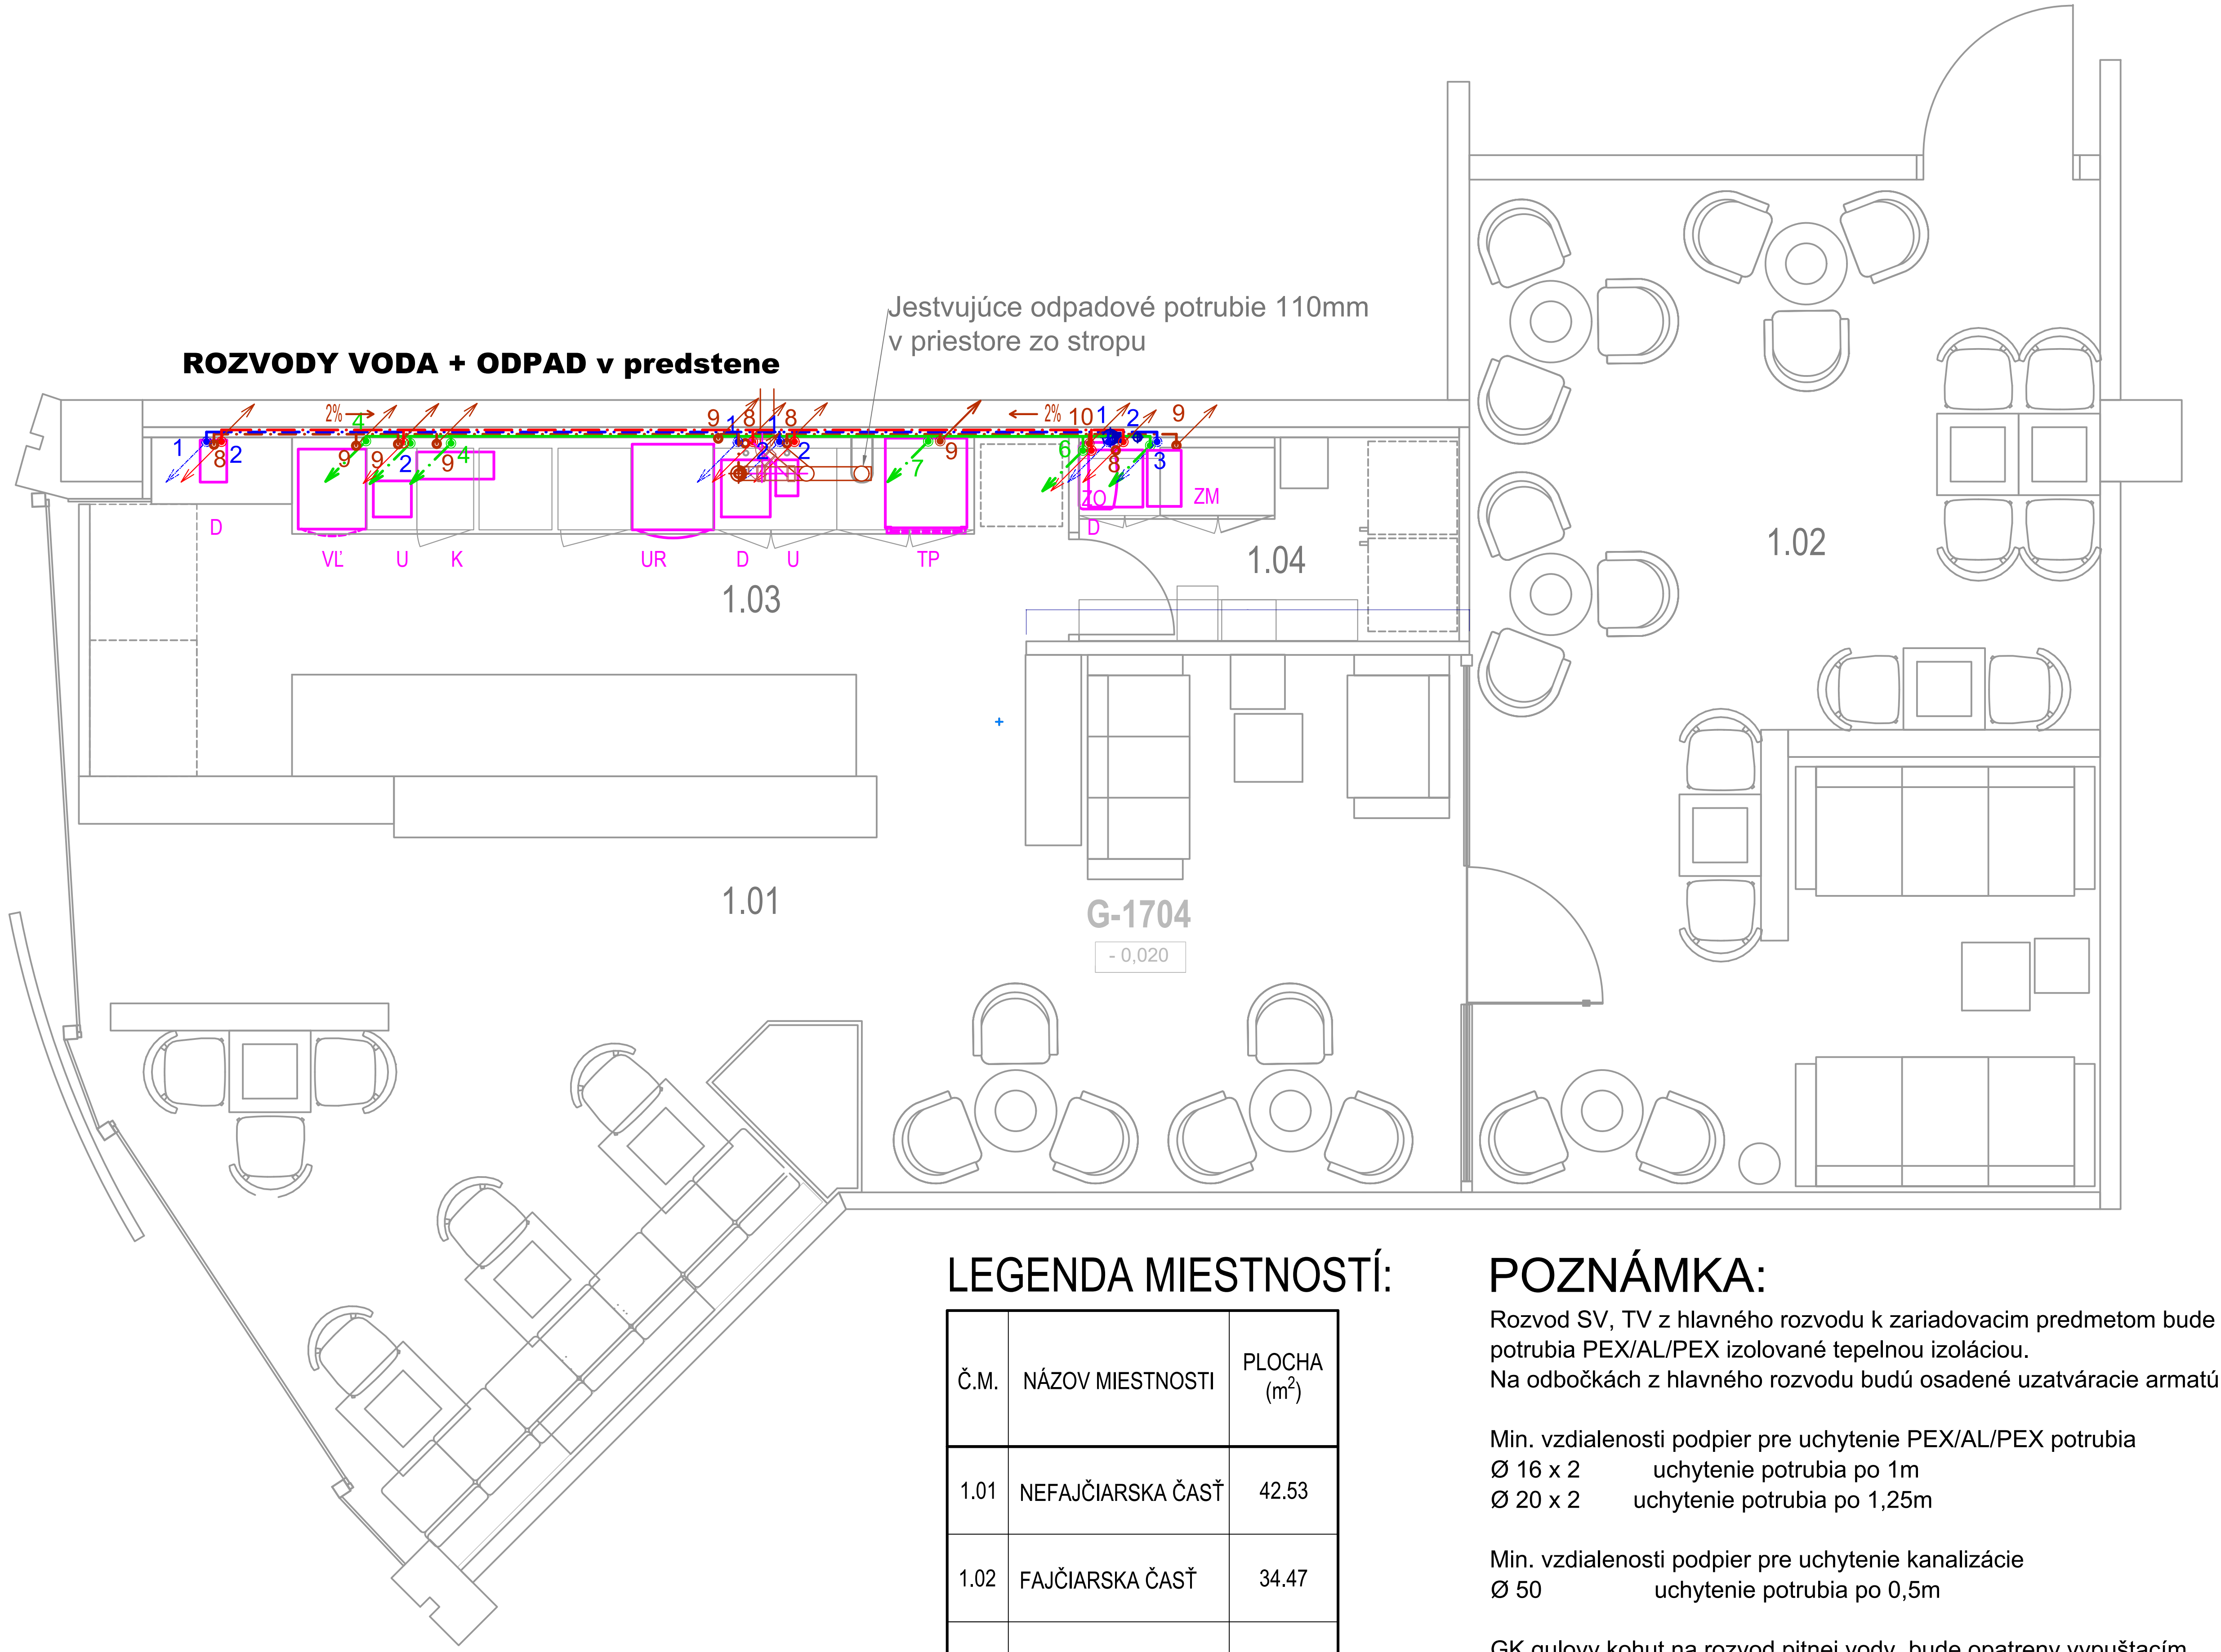

LEGENDA

— · — · —	STUDENÁ VODA (PEX/AL/PEX)
— · — · —	TEPLÁ ÚŽITKOVÁ VODA (PEX/AL/PEX)
— · — · —	STUDENÁ VODA ZMAKČENÁ (PEX/AL/PEX)
———	PRIPOJOVACIE A ODPADOVÉ KANALIZAČNÉ POTRUBIE Z PP RÚR - HT SYSTÉM

1- *Prívod studenej vody R1/2" pre stojankovú bateriu ukončenie ventilom R3/4" so sitkom v=650*
2- *Prívod teplej vody R1/2" pre stojankovú bateriu ukončenie ventilom R3/4" so sitkom v=650*
3- *Prívod studenej vody R1/2" pre zmäkčovač R3/4" ukončenie pračkovým ventilompre hadicu so sitkom v=650*
4- *Prívod zmäkčenej vody R1/2" pre trysku/kávovar ukončenie ventilom R3/4" pre hadicu v=750*
5- *Prívod zmäkčenej vody R1/2" pre umývačku/výrobník ľadu ukončenie pračkovým ventilom R3/4" pre hadicu a R3/8" ventil pre batériu v=650*
6- *Prívod zmäkčenej vody R1/2" pre ohrievač vody ukončenie ventilom R3/4" so sitkom v=2000*
7- *Prívod zmäkčenej vody R1/2" pre pec ukončenie ventilom R3/4" so sitkom v=850*
8- *Odpad pre drez/umývadlo pr50mm v=550*
9- *Odpad pre spotrebiče pr32/40/50mm v=viď kóta*
10 - *Odpad pre ohrievač vody pr32 ukončené prepadovým sifónom v=1950*

LEGENDA ZNAČIEK

K	KÁVOVAR + ZÁPACHOVÝ UZÁVER
D	KUCHYNSKÝ DREZ + ZÁPACHOVÝ UZÁVER ALEBO NAPOJIŤ NA SIFÓN DREZU
ZM	ZMAKČOVAČ VODY + ZÁPACHOVÝ UZÁVER
U	UMÝVADLO + ZÁPACHOVÝ UZÁVER
UR	UMÝVAČKA RIADU + ZÁPACHOVÝ UZÁVER ALEBO NAPOJIŤ NA SIFÓN DREZU
ZO	ELEKTRICKÝ ZÁSOBNÍKOVÝ OHRIEVAČ ELIZ EURO 120 , 2 kW (120L) + ZÁPACHOVÝ UZÁVER
OT	OPLACHOVACIA TRYSKA + ZÁPACHOVÝ UZÁVER
VĽ	VÝROBNÍK ĽADU + ZÁPACHOVÝ UZÁVER
TP	TEPLOVZDUŠNÁ PARNÁ PEC + ZÁPACHOVÝ UZÁVER
GK	GUĽOVÝ KOHÚT
F	FILTER MECH. NEČISTOT
SK	SPATNÁ KLAPKA

LEGENDA MIESTNOSTÍ:

Č.M.	NÁZOV MIESTNOSTI	PLOCHA (m^2)
1.01	NEFAJČIARSKA ČASŤ	42.53
1.02	FAJČIARSKA ČASŤ	34.47
1.03	PRIESTOR BARU	17.89
1.04	SKLAD	4.20
CELKOVÁ ÚŽIT. PLOCHA		99.09

POZNÁMKA:

Rozvod SV, TV z hlavného rozvodu k zariadovacim predmetom bude z potrubia PEX/AL/PEX izolované tepelnou izoláciou.
Na odbočkách z hlavného rozvodu budú osadené uzatváracie armatúry.

Min. vzdialenosti podpier pre uchytenie PEX/AL/PEX potrubia
Ø 16 x 2 uchytenie potrubia po 1m
Ø 20 x 2 uchytenie potrubia po 1,25m

Min. vzdialenosti podpier pre uchytenie kanalizácie
Ø 50 uchytenie potrubia po 0,5m

GK gulovy kohut na rozvod pitnej vody, bude opatreny vypuštacím

Všetky zariadenia pripojené na teplú a studenú vodu musia mať mechanický filter a uzatvárací rohový ventil.

G-1704	
Celková plocha:	104,91 m^2
Podlahová plocha:	99,09 m^2

0,000 = 137,50 m n.m., B.p.v.

ZODP. PROJEKTANT	**HIP**	**VYPRACOVAL**	
Ing. Lu			

STAVB
Č. OBC
INVEST
NÁZOV
PROFE
AUTOF
KONTA
NÁJOM
OBSAH

Obsah tohto