
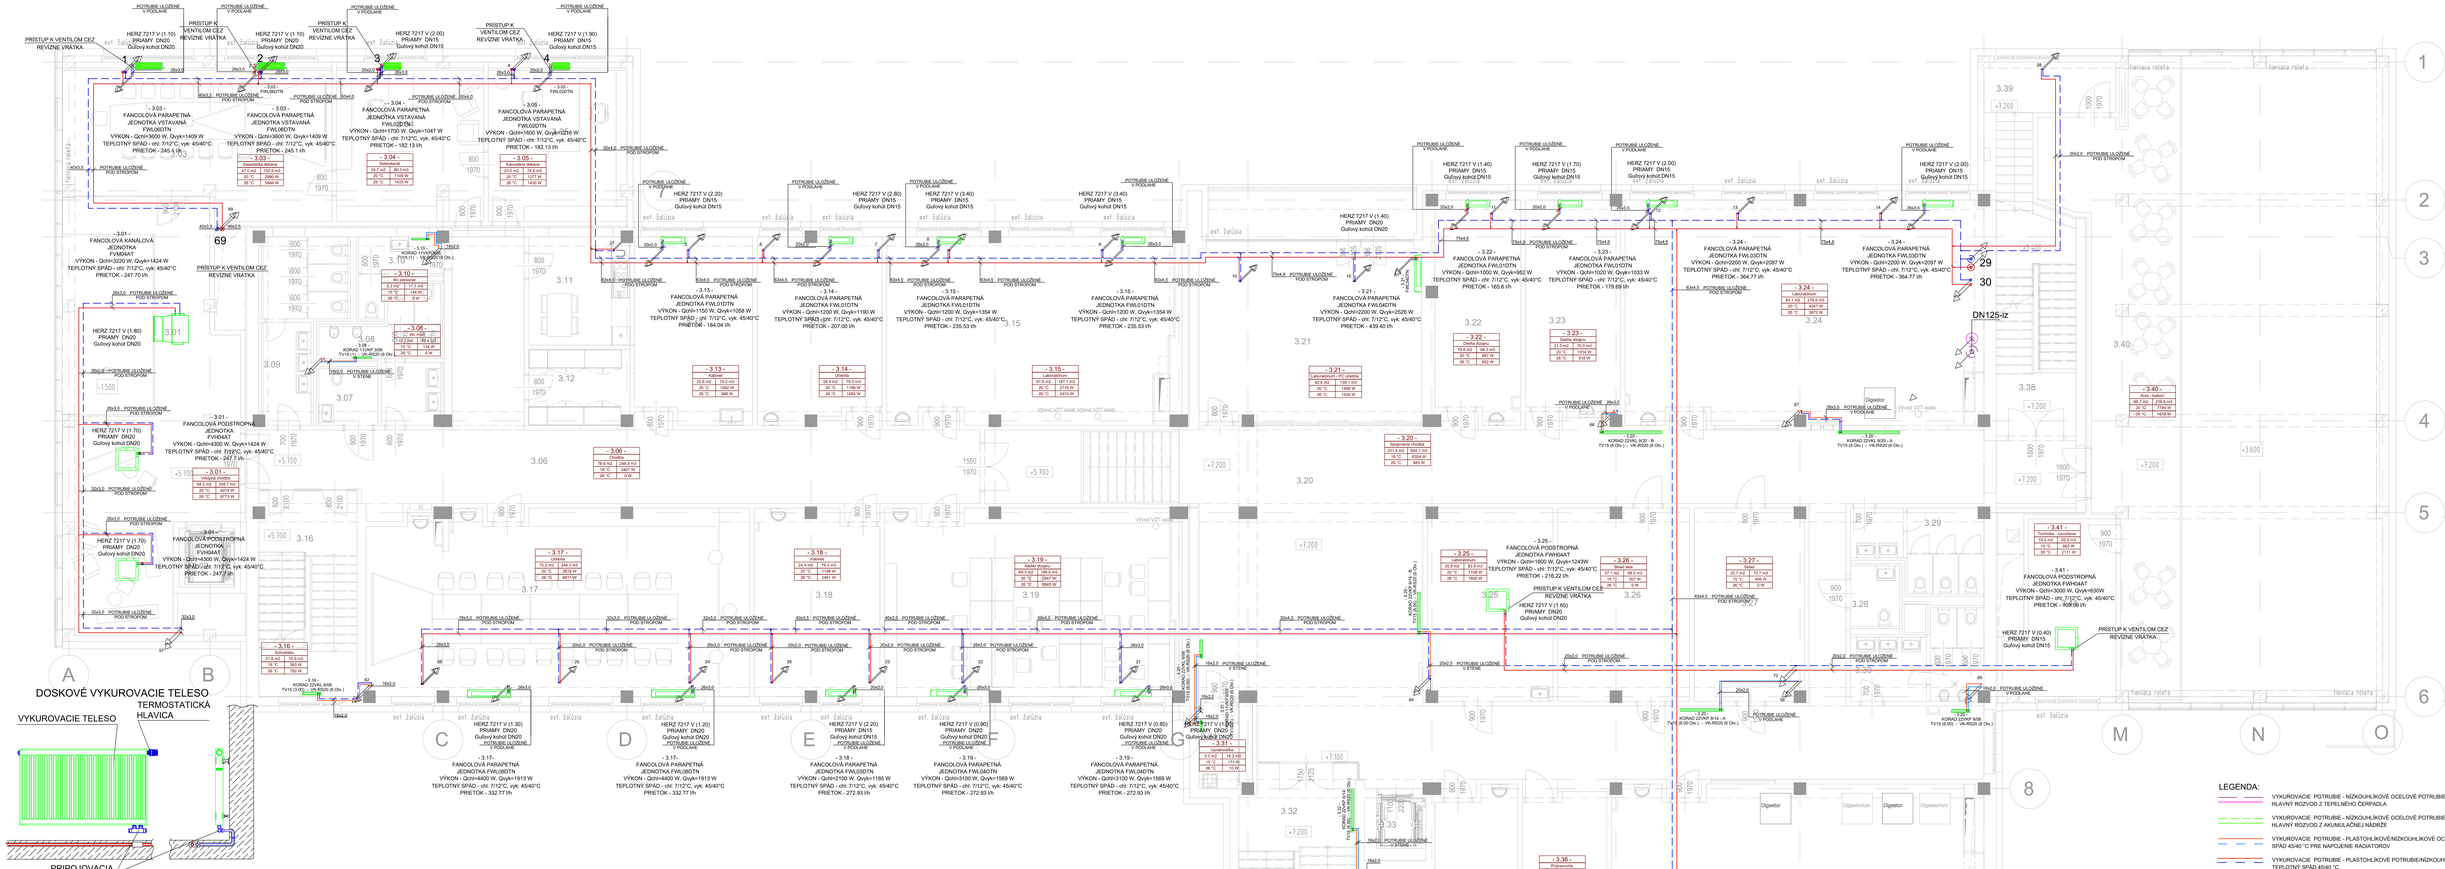


DOSKOVÉ VYKUROVACIE TELESO


L.M. 3.NP - PBS

Č.M.	Názov	Plocha
3.01	Vstupná hala	52.24
3.02	Výťah	3.47
3.03	Zasadačka dekana	41.13
3.04	Sekretáriat	24.72
3.05	kancelária dekana	23.39
3.06	Chodba	74.82
3.07	Bezbarier. záchodová kabína	3.90
3.08	WC muži	11.97
3.09	WC ženy	13.92
3.10	WC personál	4.27
3.11	Kuchynka	11.59
3.12	Archív + sklad	8.05
3.13	Kabinet	22.84
3.14	Učebňa	23.78
3.15	Laboratórium	55.03
3.16	Schodisko	21.49
3.17	Učebňa	73.82
3.18	Kabinet	24.16
3.19	Atelier dizajnu	56.41
3.20	Spojovacia chodba	200.53
3.21	Laboratórium - PC učebňa	40.89
3.22	Dielňa dizajnu	19.46
3.23	Dielňa dizajnu	21.43
3.24	Laboratórium	83.42
3.25	Laboratórium	25.59
3.26	Sklad skla	26.81
3.27	Sklad	22.44
3.28	Bezbarier. záchodová kabína	3.30
3.29	WC ženy	10.03
3.30	WC muži	10.36
3.31	Upratovačka	4.80
3.32	Schodisko	30.04
3.33	Výťah	4.10
3.34	Sklad	8.88
3.35	Laboratórium	18.93
3.36	Pripravovňa	19.07
3.37	Laboratórium	86.36
3.38	Schodisko	18.96
3.39	Schodisko	11.57
3.40	Aula - balkón	57.48
3.41	Technika - ozvučenie	18.64


DETAIL NAPOJENIA KAZETOVÉHO FANCOILU:

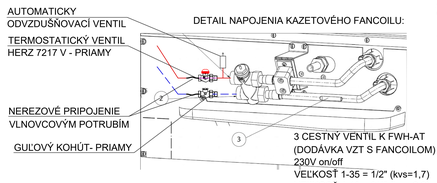

DETAIL NAPOJENIA KANÁLOVÉHO FANCOILU:

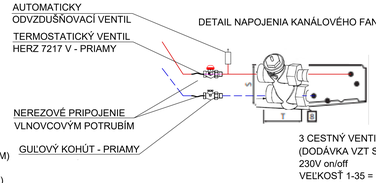

DETAIL NAPOJENIA PARAPETNÉHO FANCOILU:

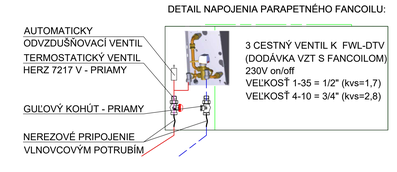


LEGENDA:

- VYKURVOVACIE POTRUBIE - NÍZKOUHLÍKOVÉ OCEĽOVÉ POTRUBIE TEPLOTNÝ SPÁD 60/50 °C HLAVNÝ ROZVOD Z TEPELNÉHO ČERPADLA
- VYKURVOVACIE POTRUBIE - NÍZKOUHLÍKOVÉ OCEĽOVÉ POTRUBIE TEPLOTNÝ SPÁD 60/50 °C HLAVNÝ ROZVOD Z AKUMULAČNEJ NÁDRŽE
- VYKURVOVACIE POTRUBIE - PLASTOHLIKOVÉ/NÍZKOUHLÍKOVÉ OCEĽOVÉ POTRUBIE TEPLOTNÝ SPÁD 45/40 °C PRE NAPOJENIE RADIATOROV
- VYKURVOVACIE POTRUBIE - PLASTOHLIKOVÉ POTRUBIE/NÍZKOUHLÍKOVÉ OCEĽOVÉ POTRUBIE TEPLOTNÝ SPÁD 45/40 °C
- EXPANZNÉ POTRUBIE
- DOSKOVÉ VYKUROVACIE TELESO
- STÚPANIE/KLESANIE POTRUBIA
- PARAPETNÁ FANCOIL JEDNOTKA
- KANÁLOVÁ VZDUCHOVÁ JEDNOTKA
- KAZETOVÁ STROPNÁ FANCOIL JEDNOTKA

LEGENDA VYKUROVACÍCH OKRUHOV:

UK1 - Prevádzka kancelária a 1NP Fancoil
UK2 - Prevádzka Aula Fancoil
UK3 - Prevádzka Aula Sálor Fancoil
UK4 - Prevádzka škola Juh Fancoil
UK5 - Prevádzka škola Radiátory

LEGENDA POPISOVÝCH TABULIEK:

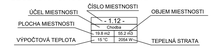

±0.000 = ÚROVEŇ PODLAHY 1.NP

SADA Číslo