L.M. 4.NP - PBS		
Č.M.	Názov	Plocha
4.01	Vstupná hala	52.75
4.02	Výťah	3.47
4.03	Študovňa	44.85
4.04	Sklad kníh	17.09
4.05	Bezbarier. záchodová kabína	3.71
4.06	WC ženy	5.62
4.07	WC personál	1.97
4.08	WC muži	13.03
4.09	Seminárna miestnosť	67.28
4.10	Kancelária	21.00
4.11	Kancelária	19.47
4.12	Kancelária	16.26
4.13	Jazyková učebňa	48.19
4.14	Schodisko	21.56
4.15	Kancelária	26.52
4.16	Kancelária	16.03
4.17	Kancelária	24.69
4.18	Kancelária	16.84
4.19	Kancelária	17.04
4.20	Kancelária	24.64
4.21	Kancelária	27.91
4.22	Spojovacia chodba	220.43
4.23	Kancelária	26.85
4.24	Kancelária	26.34
4.25	Kancelária	33.03
4.26	Kancelária	29.12
4.27	Kancelária	29.64
4.28	Kancelária	31.93
4.29	Multifunkčný priestor	75.60
4.30	Bezbarier. záchodová kabína	3.46
4.31	WC ženy	10.38
4.32	WC muži	11.27
4.33	Upratovačka	4.90
4.34	Schodisko	29.94
4.35	Výťah	4.10
4.36	Kancelária	31.11
4.37	Kancelária	19.20
4.38	Kancelária	19.61
4.39	Kancelária	19.60
4.41	Kancelária	19.61
4.42	Kancelária	19.33
4.43	Schodisko	18.02
4.44	Sklad dizajn	19.74
4.45	Seminárna miestnosť	111.65
4.46	Ateliér II	48.46
4.47	Kancelária	26.43
4.48	Chodba	53.88

DETAIL NAPOJENIA KAZETOVÉHO FANCOILU:

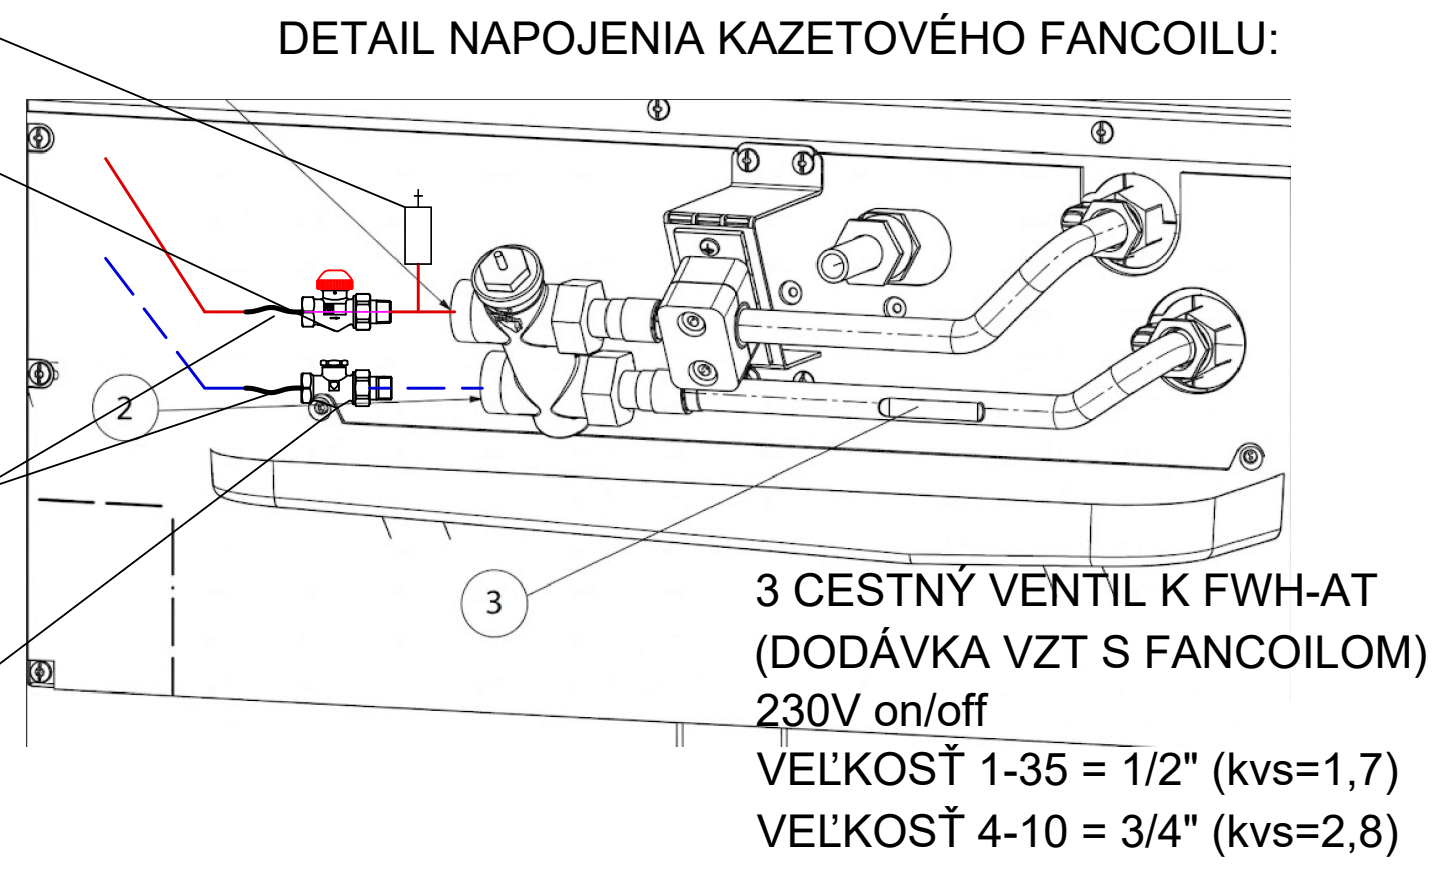

3 CESTNÝ VENTIL K FWH-AT
(DODÁVKA VZT S FANCOILOM)
230V on/off
VEĽKOSŤ 1-35 = 1/2" (kvs=1,7)
VEĽKOSŤ 4-10 = 3/4" (kvs=2,8)

DETAIL NAPOJENIA KANÁLOVÉHO FANCOILU:

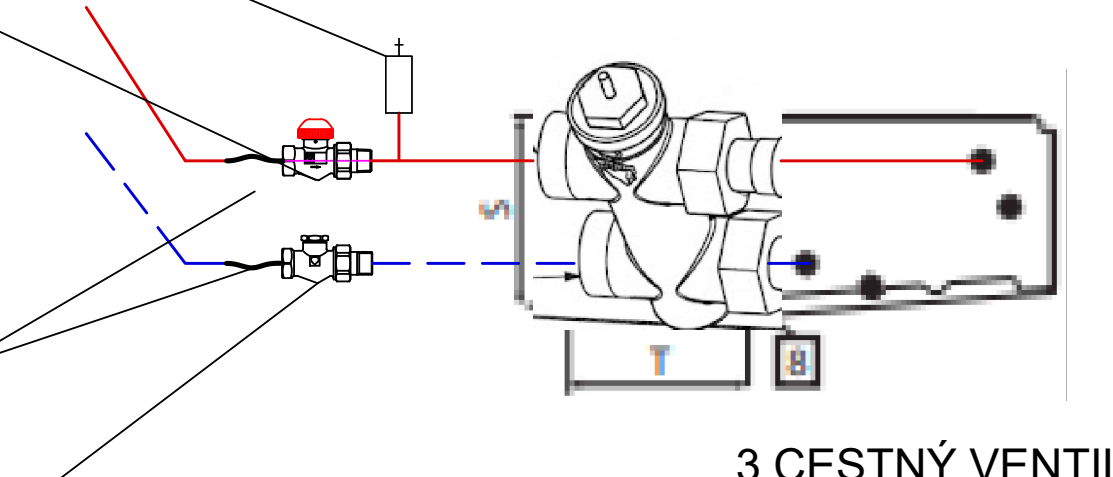

3 CESTNÝ VENTIL K FWM-AT
(DODÁVKA VZT S FANCOILOM)
230V on/off
VEĽKOSŤ 1-35 = 1/2" (kvs=1,7)
VEĽKOSŤ 4-10 = 3/4" (kvs=2,8)

DETAIL NAPOJENIA PARAPETNÉHO FANCOILU:

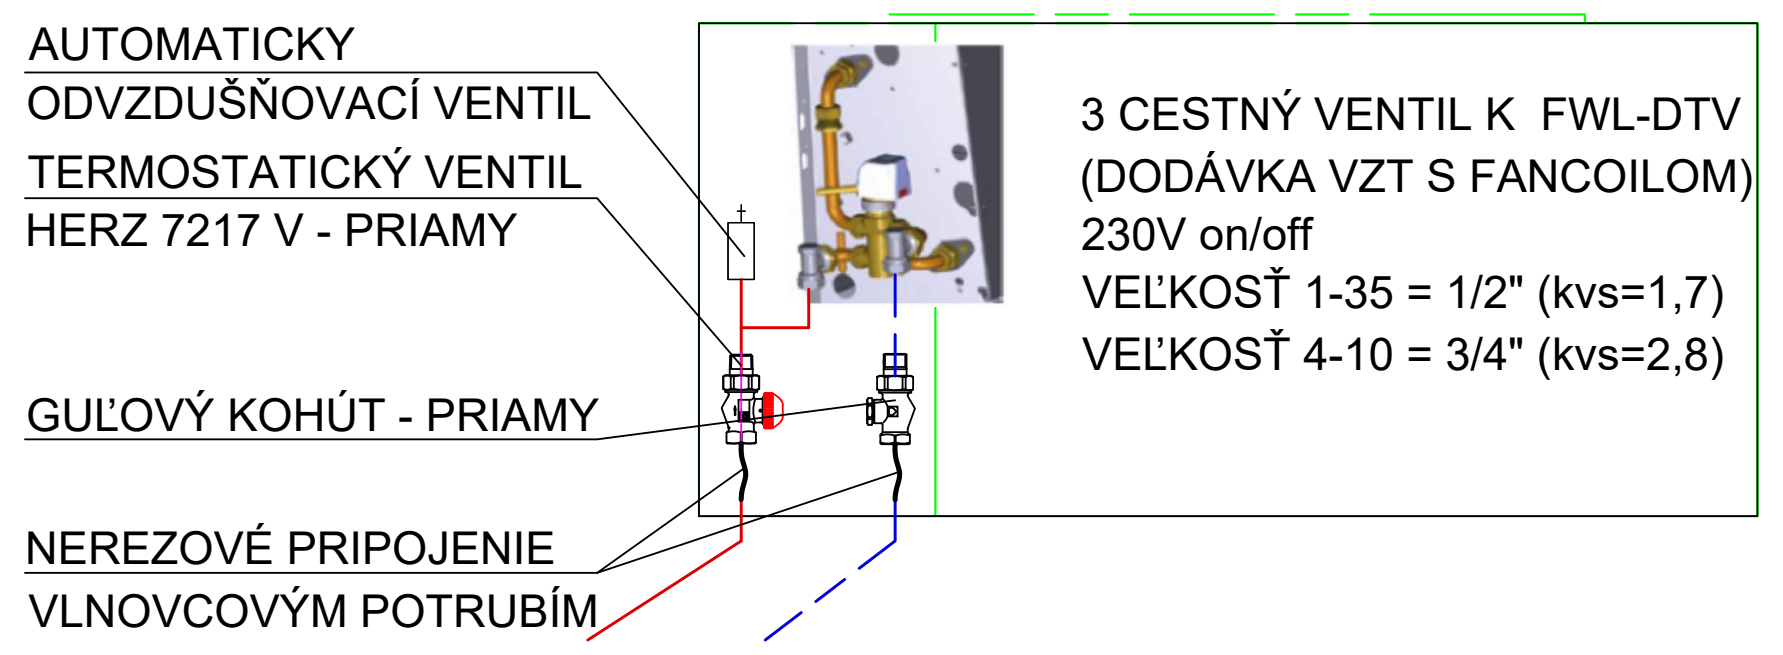

3 CESTNÝ VENTIL K FWL-DTV
(DODÁVKA VZT S FANCOILOM)
230V on/off
VEĽKOSŤ 1-35 = 1/2" (kvs=1,7)
VEĽKOSŤ 4-10 = 3/4" (kvs=2,8)

LEGENDA:

VYKUROVACIE POTRUBIE - NÍZKOUHLÍKOVÉ OCELOVÉ POTRUBIE TEPLOTNÝ SPÁD 60/50 °C HLAVNÝ ROZVOD Z TEPELNÉHO ČERPADLA

VYKUROVACIE POTRUBIE - NÍZKOUHLÍKOVÉ OCELOVÉ POTRUBIE TEPLOTNÝ SPÁD 60/50 °C HLAVNÝ ROZVOD Z AKUMULAČNEJ NÁDRŽE

VYKUROVACIE POTRUBIE - PLASTOHLÍKOVÉ/NÍZKOUHLÍKOVÉ OCELOVÉ POTRUBIE TEPLOTNÝ SPÁD 45/40 °C PRE NAPOJENIE RADIATOROV

VYKUROVACIE POTRUBIE - PLASTOHLÍKOVÉ POTRUBIE/NÍZKOUHLÍKOVÉ OCELOVÉ POTRUBIE TEPLOTNÝ SPÁD 45/40 °C

EXPANZNÉ POTRUBIE

DOSKOVÉ VYKUROVACIE TELESO

STÚPANIE/KLESANIE POTRUBIA

PARAPETNÁ FANCOIL JEDNOTKA

KANÁLOVÁ VZDUCHOVÁ JEDNOTKA

KAZETOVÁ STROPNÁ FANCOIL JEDNOTKA

LEGENDA VYKUROVACÍCH OKRUHOV:

UK1 - Prevádzka kancelárie 4.NP Fancoil
UK2 - Prevádzka Aula Fancoil
UK3 - Prevádzka škola Sever Fancoil
UK4 - Prevádzka škola Juh Fancoil
UK5 - Prevádzka škola Radiatory

LEGENDA POPISOVÝCH TABULIEK:

ČÍSLO MIESTNOSTI
ÚČEL MIESTNOSTI
PLOCHA MIESTNOSTI
VÝPOČTOVÁ TEPLOTA
OBJEM MIESTNOSTI
TEPELNÁ STRATA

- 1.12 -	
Chodba	
19.8 m2	55.2 m3
15 °C	2054 W

SADA ČÍSLO

±0,000 = ÚROVEŇ PODLAHY 1.NP

Objednávateľ: Trenčiansky samosprávny kraj, K dolnej stanici 7282/20A, 911 01 Trenčín,
Tre
Generálny projekt
Kontroloval: Ing.
Kraj: Trenčiansky
Investor: Trenčian
Trenčian
Miesto stavby: k.ú
15
Stupeň PD:
Akcia:
Objekt: SO 20
Obsah: Pôdor