LEGENDA:

🟥🟦	VYK. POTRUBIE NÍZKOUHLÍKOVÉ OCELOVÉ/PLASTOHLINÍKOVÉ POTRUBIE
🟥🟦	VYK. POTRUBIE NÍZKOUHLÍKOVÉ OCELOVÉ/PLASTOHLINÍKOVÉ POTRUBIE, RADIATOROVÉ
▤ PP	POŽIARNY PRESTUP

VETVA JUH

VETVA AULA

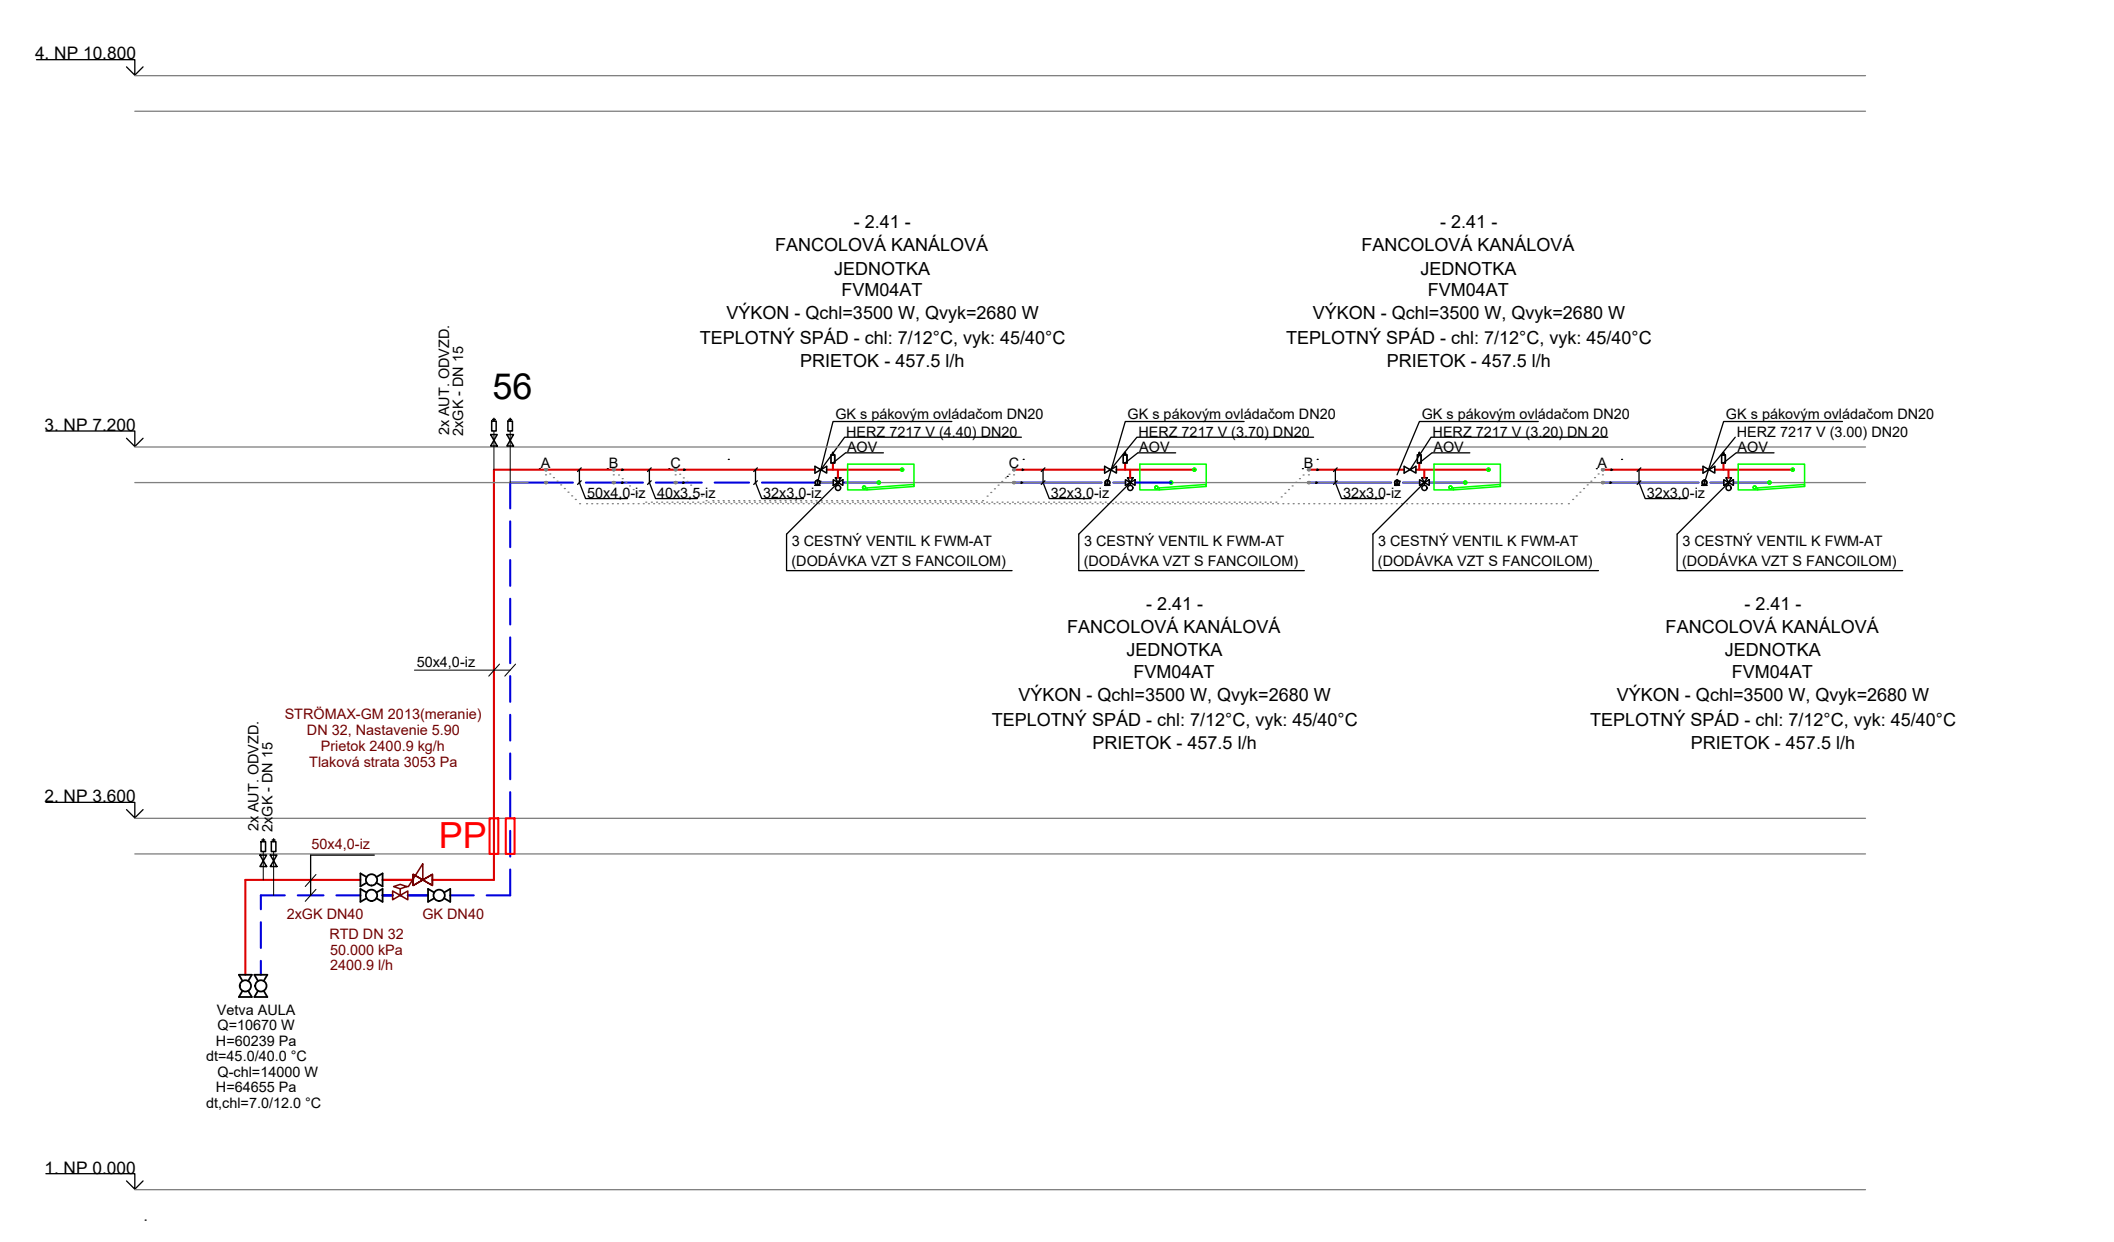

VETVA SEVER

DETAIL NAPOJENIA KANÁLOVÉHO FANCOILU:

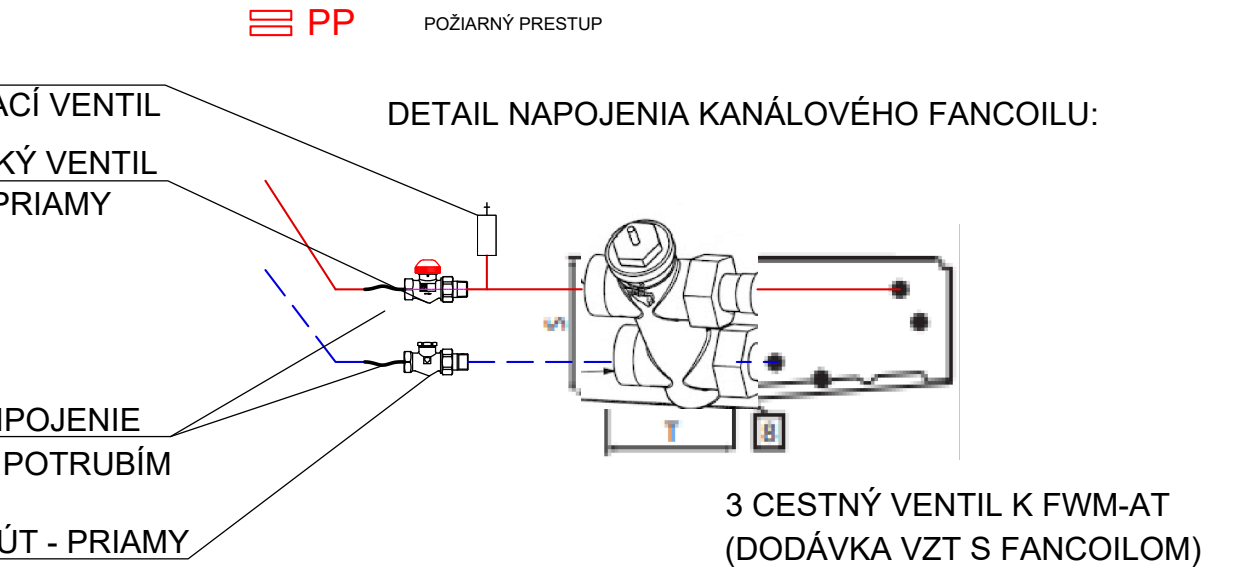

3 CESTNÝ VENTIL K FWM-AT
(DODÁVKA VZT S FANCOILOM)
230V on/off
VEĽKOSŤ 1-35 = 1/2" (kvs=1,7)
VEĽKOSŤ 4-10 = 3/4" (kvs=2,8)

DETAIL NAPOJENIA KAZETOVÉHO FANCOILU:

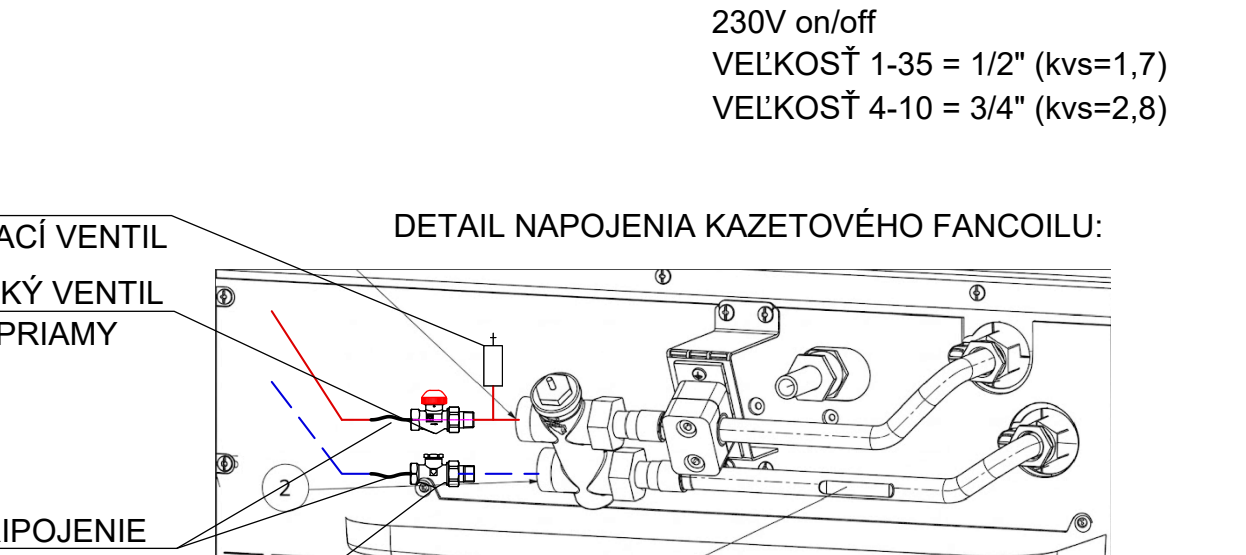

3 CESTNÝ VENTIL K FWH-AT
(DODÁVKA VZT S FANCOILOM)
230V on/off
VEĽKOSŤ 1-35 = 1/2" (kvs=1,7)
VEĽKOSŤ 4-10 = 3/4" (kvs=2,8)

DETAIL NAPOJENIA PARAPETNÉHO FANCOILU:

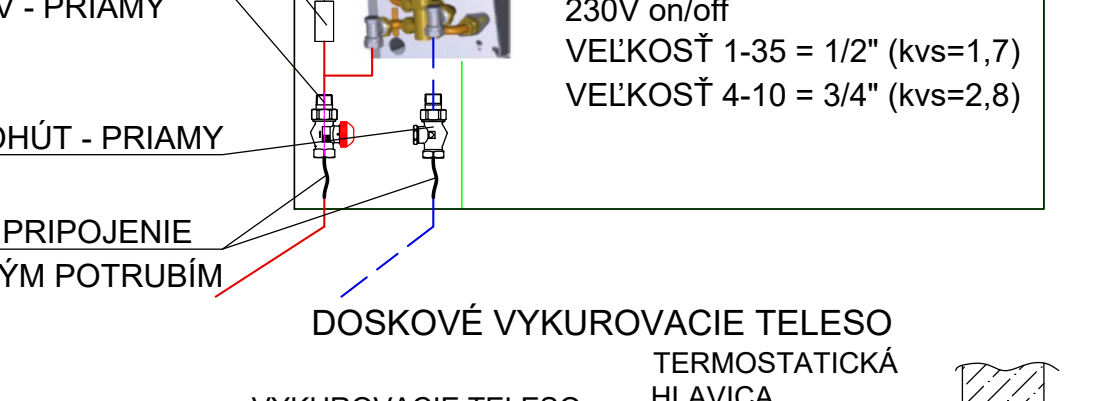

3 CESTNÝ VENTIL K FWL-DTV
(DODÁVKA VZT S FANCOILOM)
230V on/off
VEĽKOSŤ 1-35 = 1/2" (kvs=1,7)
VEĽKOSŤ 4-10 = 3/4" (kvs=2,8)

DOSKOVÉ VYKUROVACIE TELESO

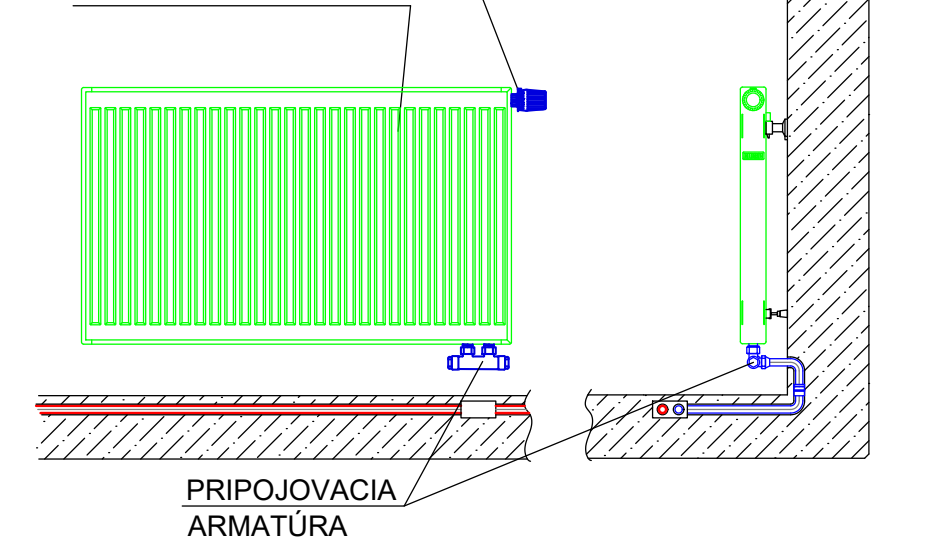

LEGENDA OSADENIA REGULÁCIE NA PÄTE STÚPAČKY:

GK - Guľový kohút
VK - Vypúšťací kohút DN15
RTD - Regulátor tlakovej diferencie
PTV - Partnerský vyvažovací ventil Herz Stromax GM 2013 - závit Rp

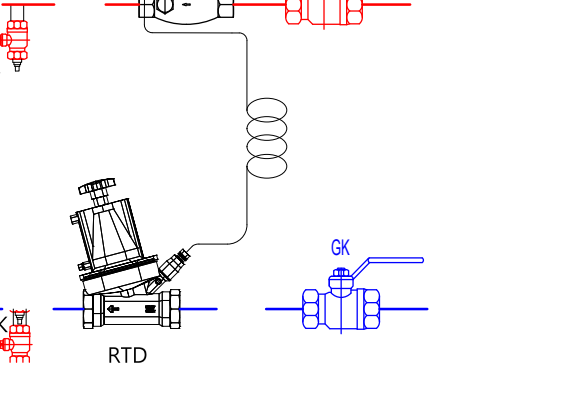

POZNÁMKY:

POTRUBIA A SPÁDOVANIE - Všetky potrubia ÚK a chladenia spádovať v smere prúdenia k najnižším bodom systému pod spádom min. 0,2 %. V najvyšších bodoch rozvodov osadiť automatické odvzdušňovacie ventily, v najnižších bodoch vypúšťacie kohúty s hadicovým nástavcom.

TEPELNÁ IZOLÁCIA POTRUBIA- Všetky potrubné rozvody tepla/chladu celoplošne a súvisle zaizolovať parotesnou elastomérnou izoláciou na báze syntetického kaučuku. Hrúbka izolácie musí byť dimenzovaná podľa priemeru potrubia v zmysle vyhlášky č. 14/2016 Z. z. (minimálne hrúbky pre vykurovanie) a zároveň musí bezpečne zabrániť vzniku kondenzátu v režime chladenia (min. hrúbka 13 mm pre DN 15–25, min. 19 mm pre DN 32 a väčšie, resp. podľa výpočtu pre dané prostredie).

FANCOILOVÉ JEDNOTKY A ZAPOJENIE - Pred montážou fancoilových jednotiek skontrolovať presný typ, výkon a orientáciu pripojenia podľa PD a dodávky stavby. Pripojenie fancoilu na pevné potrubné rozvody vyhotoviť pomocou nerezových vlnovcových potrubí z dôvodu eliminácie prenosu vibrácií a hluku do potrubnej siete. Pred každou fancoilovou jednotkou osadiť armatúry podľa PD.

SADA ČÍSLO

±0,000 = ÚROVEŇ PODLAHY 1.NP

Objednávateľ: Trenčiansky samosprávny kraj, K dolnej stanici 7282/20A, 911 01 Trenčín,
Tre
Generálny projek
Kontroloval: Ing.
Kraj: Trenčiansky
Investor: Trenčian
Trenčian
Miesto stavby: k.ú
15
Stupeň PD:
Akcia:
Objekt: SO 20
Obsah: Schém