1
2
3
4
5
6
A
B
C
D
E
F
M
N
O
1.11
1.12
1.13
1.14
1.15
1.16
1.17
1.07
1.08
1.09
1.18
1.19
1.20
1.21
1.24
1.25
1.26
1.27a
1.27b
1.28
1.29
1.30
1.43
1.44
1.45
1.46
1.47
1.48
DN125-iz
TČ1
ext. žalúzia
POTRUBIE ULOŽENÉ POD STROPOM
HERZ 7217 V (1.20) PRIAMY DN15 Guľový kohút DN15
- 1.02 - FANCOLOVÁ PARAPETNÁ VSTAVANÁ JEDNOTKA FWL02DTN VÝKON - Qchl=1600 W, Qvyk=1000 W TEPLOTNÝ SPÁD - chl: 7/12°C, vyk: 45/40°C PRIETOK - 173.9 l/h
- 1.14 - FANCOLOVÁ PARAPETNÁ VSTAVANÁ JEDNOTKA FWL04DTN VÝKON - Qchl=2700 W, Qvyk=1778 W TEPLOTNÝ SPÁD - chl: 7/12°C, vyk: 45/40°C PRIETOK - 309.3 l/h
- 1.01 - FANCOLOVÁ KANÁLOVÁ JEDNOTKA FWM04AT VÝKON - Qchl=2640 W, Qvyk=1714 W TEPLOTNÝ SPÁD - chl: 7/12°C, vyk: 45/40°C PRIETOK - 298.10 l/h
- 1.05 - FANCOLOVÁ KAZETOVÁ JEDNOTKA FWC04AT VÝKON - Qchl=1680 W, Qvyk=697 W TEPLOTNÝ SPÁD - chl: 7/12°C, vyk: 45/40°C PRIETOK - 121.20 l/h
- 1.18 - FANCOLOVÁ PARAPETNÁ JEDNOTKA FWL04DTN VÝKON - Qchl=3050 W, Qvyk=3050 W TEPLOTNÝ SPÁD - chl: 7/12°C, vyk: 45/40°C PRIETOK - 293.3 l/h
- 1.19 - FANCOLOVÁ PARAPETNÁ JEDNOTKA FWL03DTN VÝKON - Qchl=2200 W, Qvyk=1295 W TEPLOTNÝ SPÁD - chl: 7/12°C, vyk: 45/40°C PRIETOK - 225.3 l/h
- 1.20 - FANCOLOVÁ PARAPETNÁ JEDNOTKA FWL04DTN VÝKON - Qchl=3050 W, Qvyk=1120 W TEPLOTNÝ SPÁD - chl: 7/12°C, vyk: 45/40°C PRIETOK - 194.8 l/h

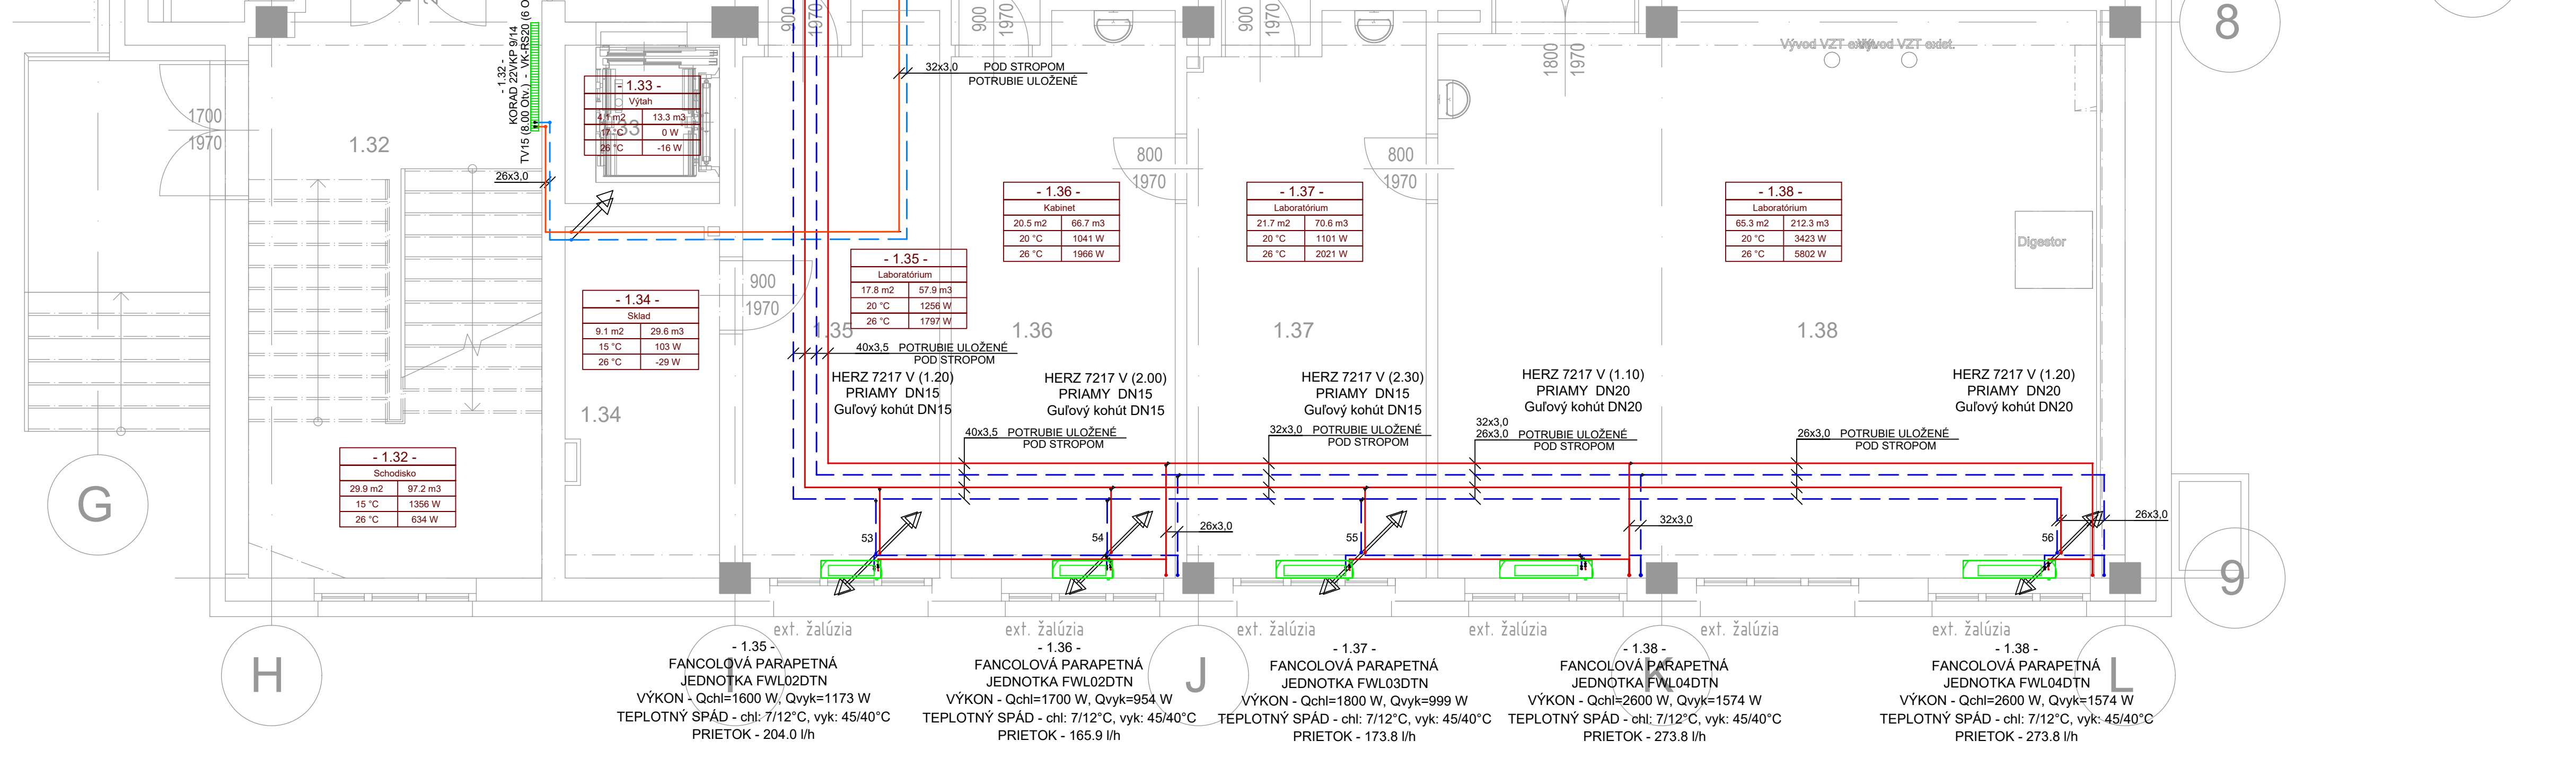

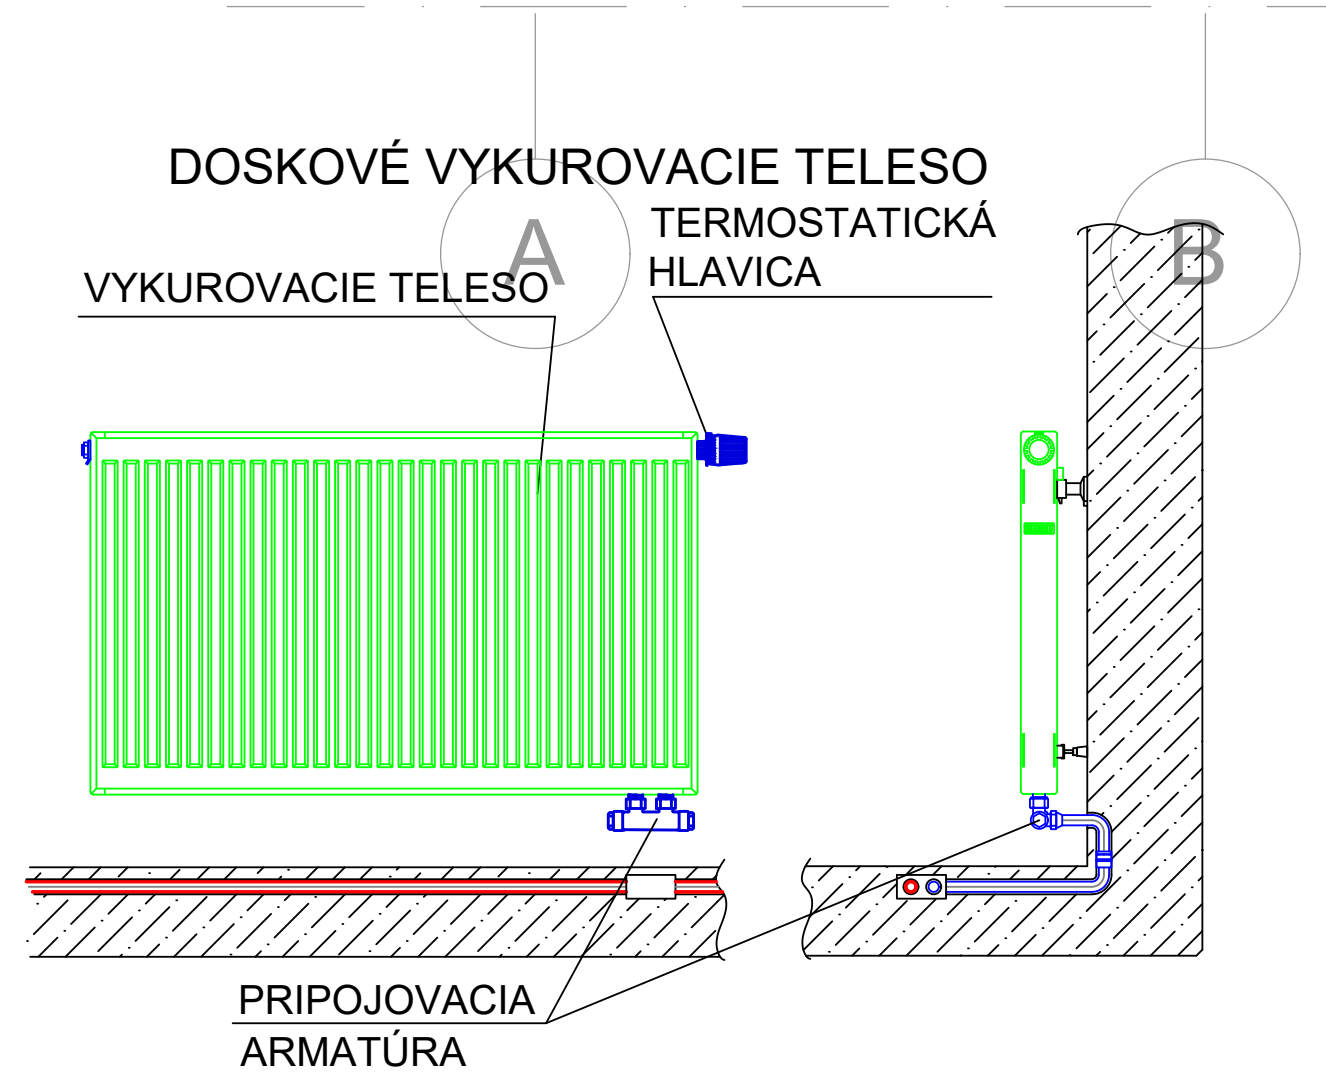

L.M. 1.NP - fakulta

Č.M.	Názov	Plocha
1.01	Vstupná hala	55.20 m^2
1.02	Bufet + kaviareň	64.16 m^2
1.04	Výťah	3.47 m^2
1.05	Recepcia	9.71 m^2
1.06	Zázemie - recepcia	4.72 m^2
1.07	Chodba	60.04 m^2
1.08	Schodisko	21.20 m^2
1.09	Chodba	15.79 m^2
1.10	Bezbarier. záchodová kabína	3.56 m^2
1.11	WC ženy	13.56 m^2
1.12	WC muži	11.20 m^2
1.13	Sklad pre učebňu 3D	4.50 m^2
1.14	Učebňa 3D modelovania	67.70 m^2
1.15	Kabinet	22.56 m^2
1.16	Kabinet	23.80 m^2
1.17	Učebňa	54.25 m^2
1.18	Učebňa	59.15 m^2
1.19	Kabinet	24.07 m^2
1.20	Učebňa	54.86 m^2
1.21	Spojovacia chodba	203.54 m^2
1.22	Zádverie	17.48 m^2
1.23	Vrátnica	9.77 m^2
1.24	Sklad	9.72 m^2
1.25	Laboratórium	42.20 m^2
1.26	Laboratórium	65.08 m^2
1.27a	Strojovňa tepelného čerp.	35.33 m^2
1.27b	Sklad	38.53 m^2
1.28	Bezbarier. záchodová kabína	3.16 m^2
1.29	WC ženy	9.86 m^2
1.30	WC muži	10.63 m^2
1.31	Rozvodňa NN	5.39 m^2
1.32	Schodisko	29.95 m^2
1.33	Výťah	4.10 m^2
1.34	Sklad	8.95 m^2
1.35	Laboratórium	17.79 m^2
1.36	Kabinet	20.54 m^2
1.37	Laboratórium	21.62 m^2
1.38	Laboratórium	61.60 m^2
1.39	Chodba	20.33 m^2
1.40	Schodisko	18.80 m^2
1.41	Chodba	13.62 m^2
1.42	Dielňa	62.02 m^2
1.43	Garáž	32.06 m^2
1.44	Spojovacia chodba	25.04 m^2
1.45	Sklad	14.71 m^2
1.46	Sklad	20.24 m^2
1.47	Sklad	12.92 m^2
1.48	Sklad	23.84 m^2
1.49	Upratovačka	5.65 m^2
1.50	Miestnosť CBS	4.89 m^2
		1442.82 m^2

LEGENDA OSADENIA REGULÁCIE NA PÄTE STÚPAČKY:

GK - Guľový kohút
VK - Vypúšťací kohút DN15
RTD - Regulátor tlakovej diferencie
PTV - Partnerský vyvažovací ventil Herz Stromax GM 2013 - závit Rp

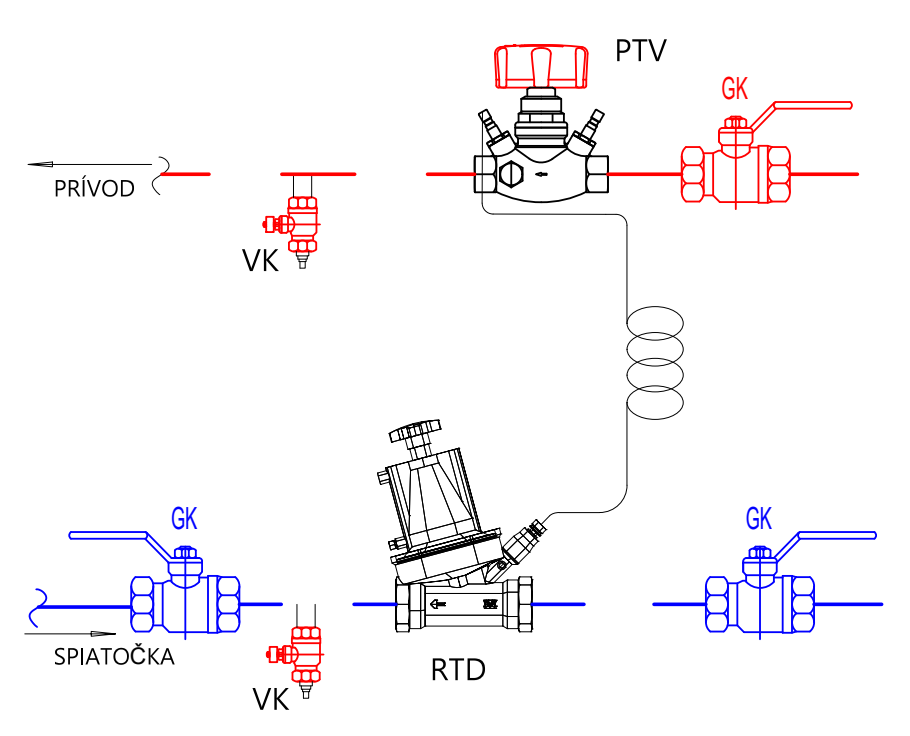

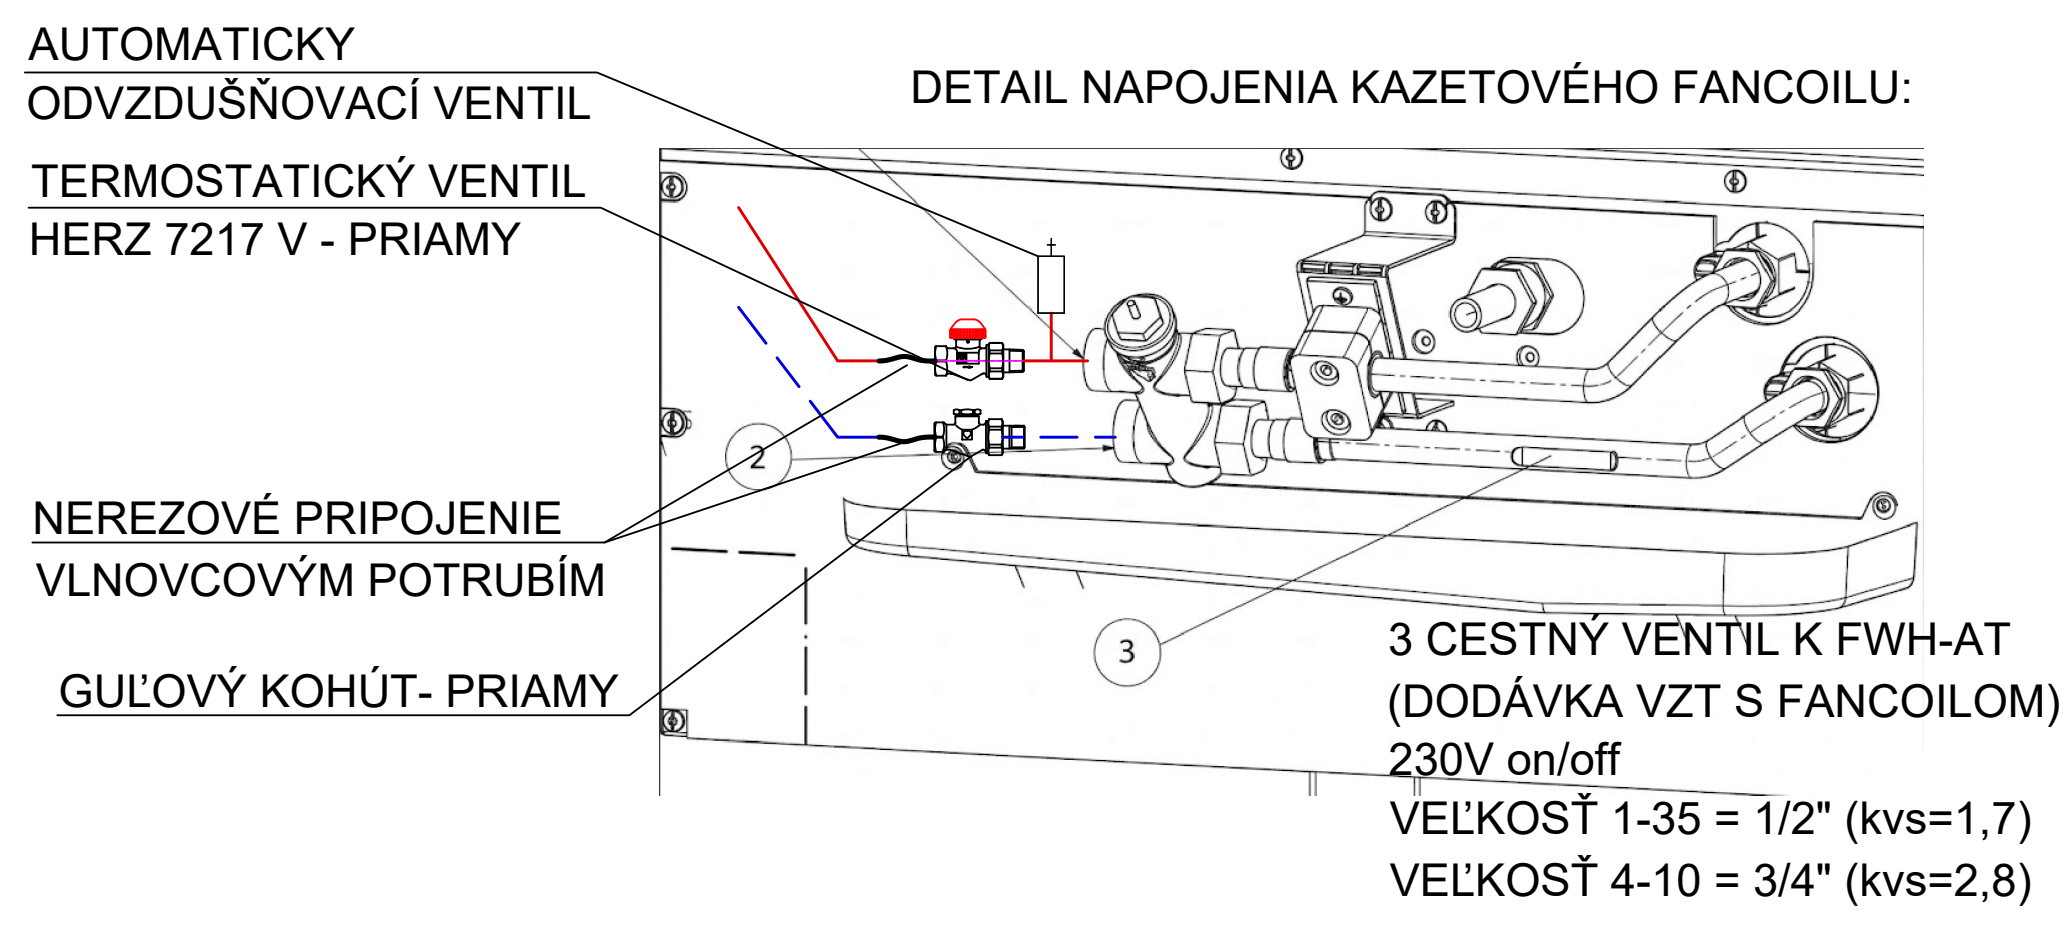
AUTOMATICKY ODVZDUŠŇOVACÍ VENTIL
DETAIL NAPOJENIA KAZETOVÉHO FANCOILU:
TERMOSTATICKÝ VENTIL HERZ 7217 V - PRIAMY
2
NEREZOVÉ PRIPOJENIE VLNOVCOVÝM POTRUBÍM
3
GUĽOVÝ KOHÚT- PRIAMY
3 CESTNÝ VENTIL K FWH-AT
(DODÁVKA VZT S FANCOILOM)
230V on/off
VEĽKOSŤ 1-35 = 1/2" (kvs=1,7)
VEĽKOSŤ 4-10 = 3/4" (kvs=2,8)

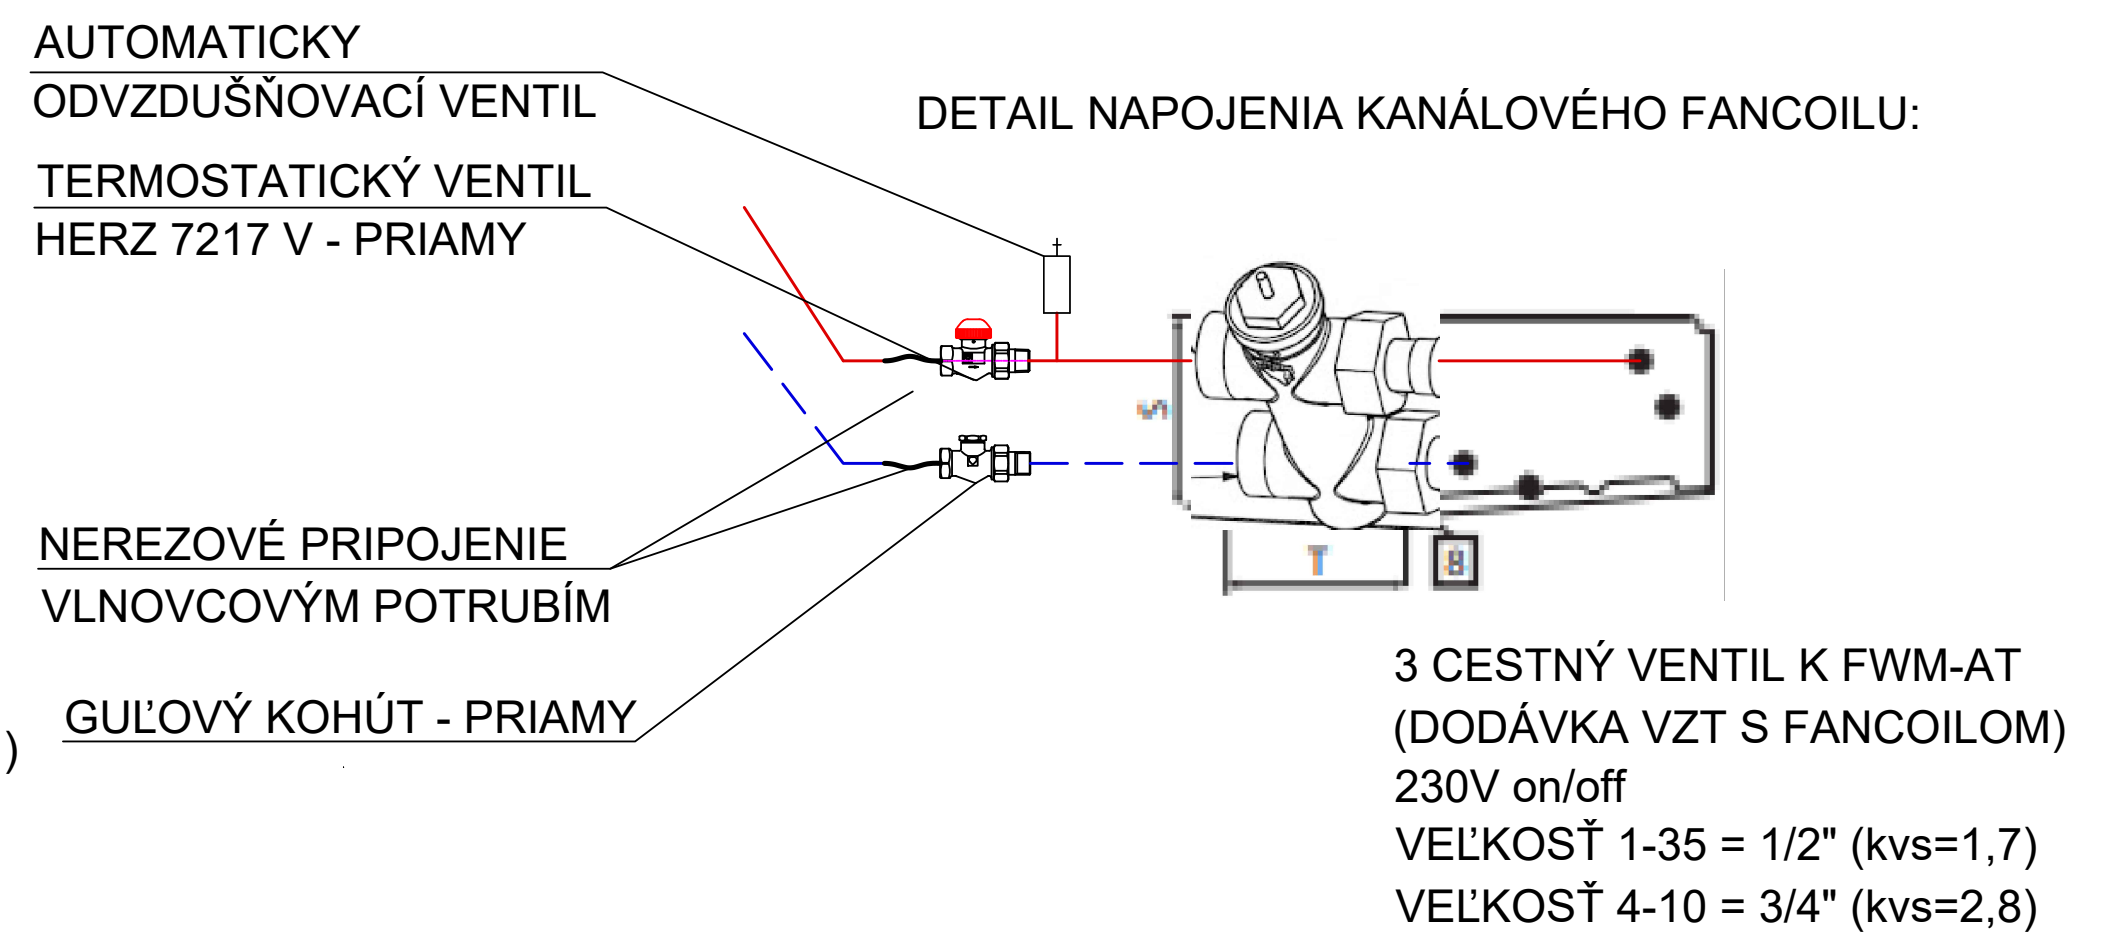
AUTOMATICKY ODVZDUŠŇOVACÍ VENTIL
DETAIL NAPOJENIA KANÁLOVÉHO FANCOILU:
TERMOSTATICKÝ VENTIL HERZ 7217 V - PRIAMY
NEREZOVÉ PRIPOJENIE VLNOVCOVÝM POTRUBÍM
GUĽOVÝ KOHÚT - PRIAMY
3 CESTNÝ VENTIL K FWM-AT
(DODÁVKA VZT S FANCOILOM)
230V on/off
VEĽKOSŤ 1-35 = 1/2" (kvs=1,7)
VEĽKOSŤ 4-10 = 3/4" (kvs=2,8)

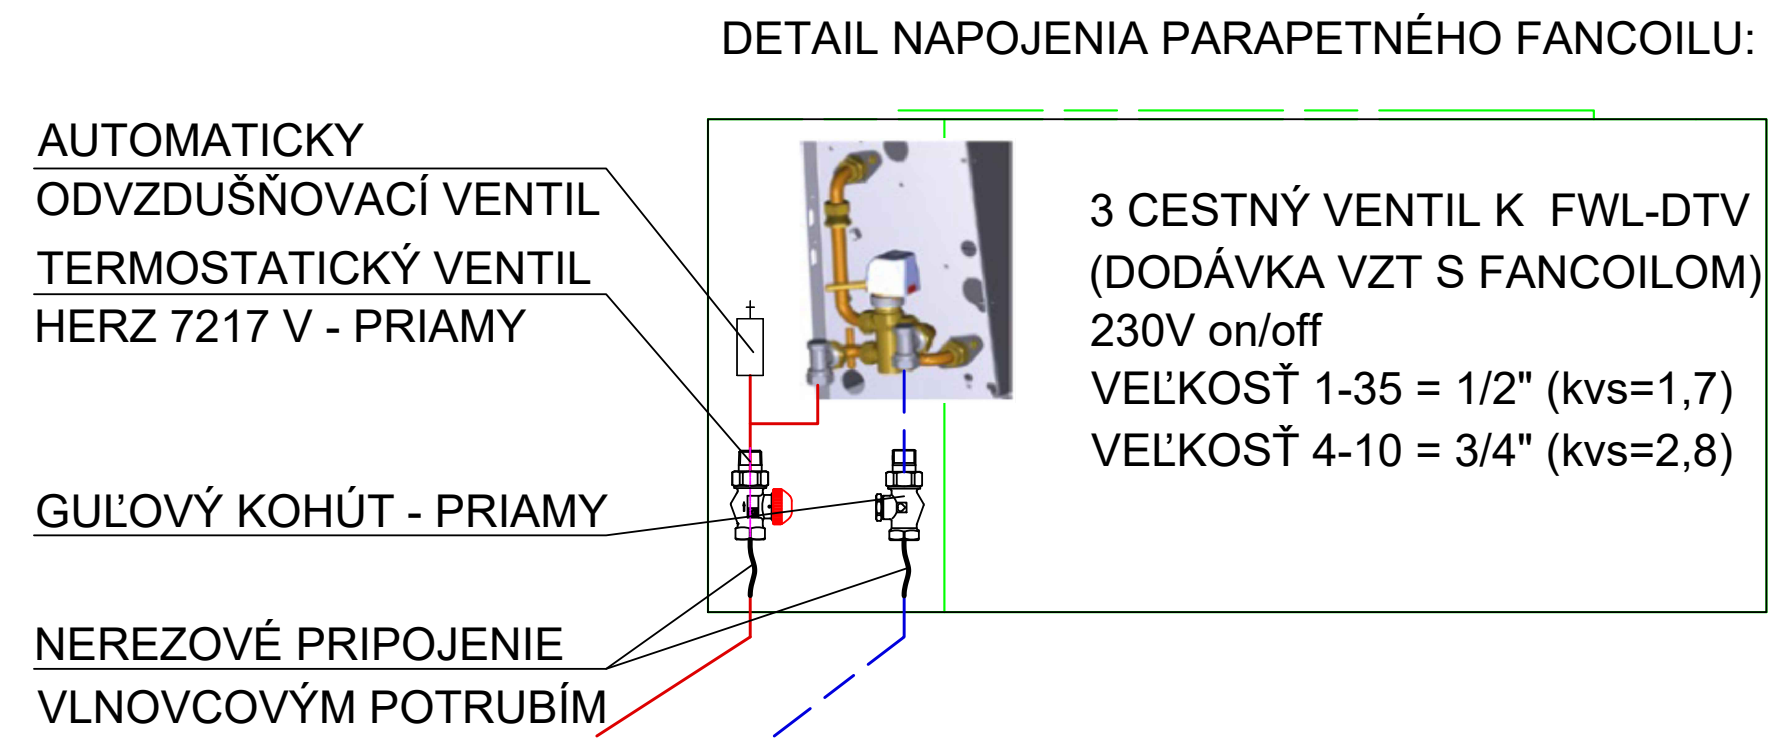
DETAIL NAPOJENIA PARAPETNÉHO FANCOILU:
AUTOMATICKY ODVZDUŠŇOVACÍ VENTIL
TERMOSTATICKÝ VENTIL HERZ 7217 V - PRIAMY
GUĽOVÝ KOHÚT - PRIAMY
NEREZOVÉ PRIPOJENIE VLNOVCOVÝM POTRUBÍM
3 CESTNÝ VENTIL K FWL-DTV
(DODÁVKA VZT S FANCOILOM)
230V on/off
VEĽKOSŤ 1-35 = 1/2" (kvs=1,7)
VEĽKOSŤ 4-10 = 3/4" (kvs=2,8)

LEGENDA:

- VYKUROVACIE POTRUBIE - NÍZKOUHLÍKOVÉ OCELOVÉ POTRUBIE TEPLOTNÝ SPÁD 60/50 °C HLAVNÝ ROZVOD Z TEPELNÉHO ČERPADLA
- VYKUROVACIE POTRUBIE - NÍZKOUHLÍKOVÉ OCELOVÉ POTRUBIE TEPLOTNÝ SPÁD 60/50 °C HLAVNÝ ROZVOD Z AKUMULAČNEJ NÁDRŽE
- VYKUROVACIE POTRUBIE - PLASTOHLÍKOVÉ/NÍZKOUHLÍKOVÉ OCELOVÉ POTRUBIE TEPLOTNÝ SPÁD 45/40 °C PRE NAPOJENIE RADIATOROV
- VYKUROVACIE POTRUBIE - PLASTOHLÍKOVÉ POTRUBIE/NÍZKOUHLÍKOVÉ OCELOVÉ POTRUBIE TEPLOTNÝ SPÁD 45/40 °C
- EXPANZNÉ POTRUBIE
- DOSKOVÉ VYKUROVACIE TELESO
- STÚPANIE/KLESANIE POTRUBIA
- PARAPETNÁ FANCOIL JEDNOTKA
- KANÁLOVÁ VZDUCHOVÁ JEDNOTKA
- KAZETOVÁ STROPNÁ FANCOIL JEDNOTKA

LEGENDA VYKUROVACÍCH OKRUHOV:

UK1 - Prevádzka kancelárie 4.NP Fancoil
UK2 - Prevádzka Aula Fancoil
UK3 - Prevádzka škola Sever Fancoil
UK4 - Prevádzka škola Juh Fancoil
UK5 - Prevádzka škola Radiatory

LEGENDA POPISOVÝCH TABULIEK:

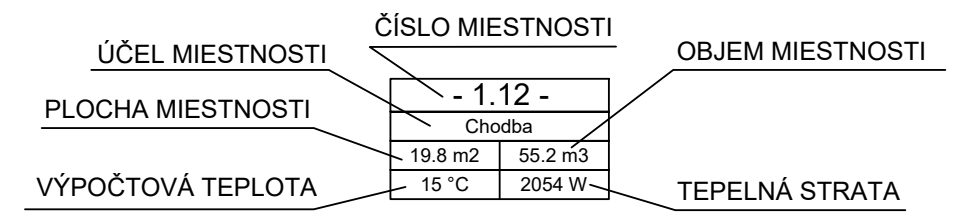

±0,000 = ÚROVEŇ PODLAHY 1.NP

SADA ČÍSLO

Objednávateľ: Trenčiansky samosprávny kraj, K dolnej stanici 7282/20A, 911 01 Trenčín,
Tre
Generálny projekt
Kontroloval: Ing.
Kraj: Trenčiansky
Investor: Trenčian
Trenčians
Miesto stavby: k.ú
15
Stupeň PD:
Akcia:
Objekt: SO 20
Obsah: Pôdory