
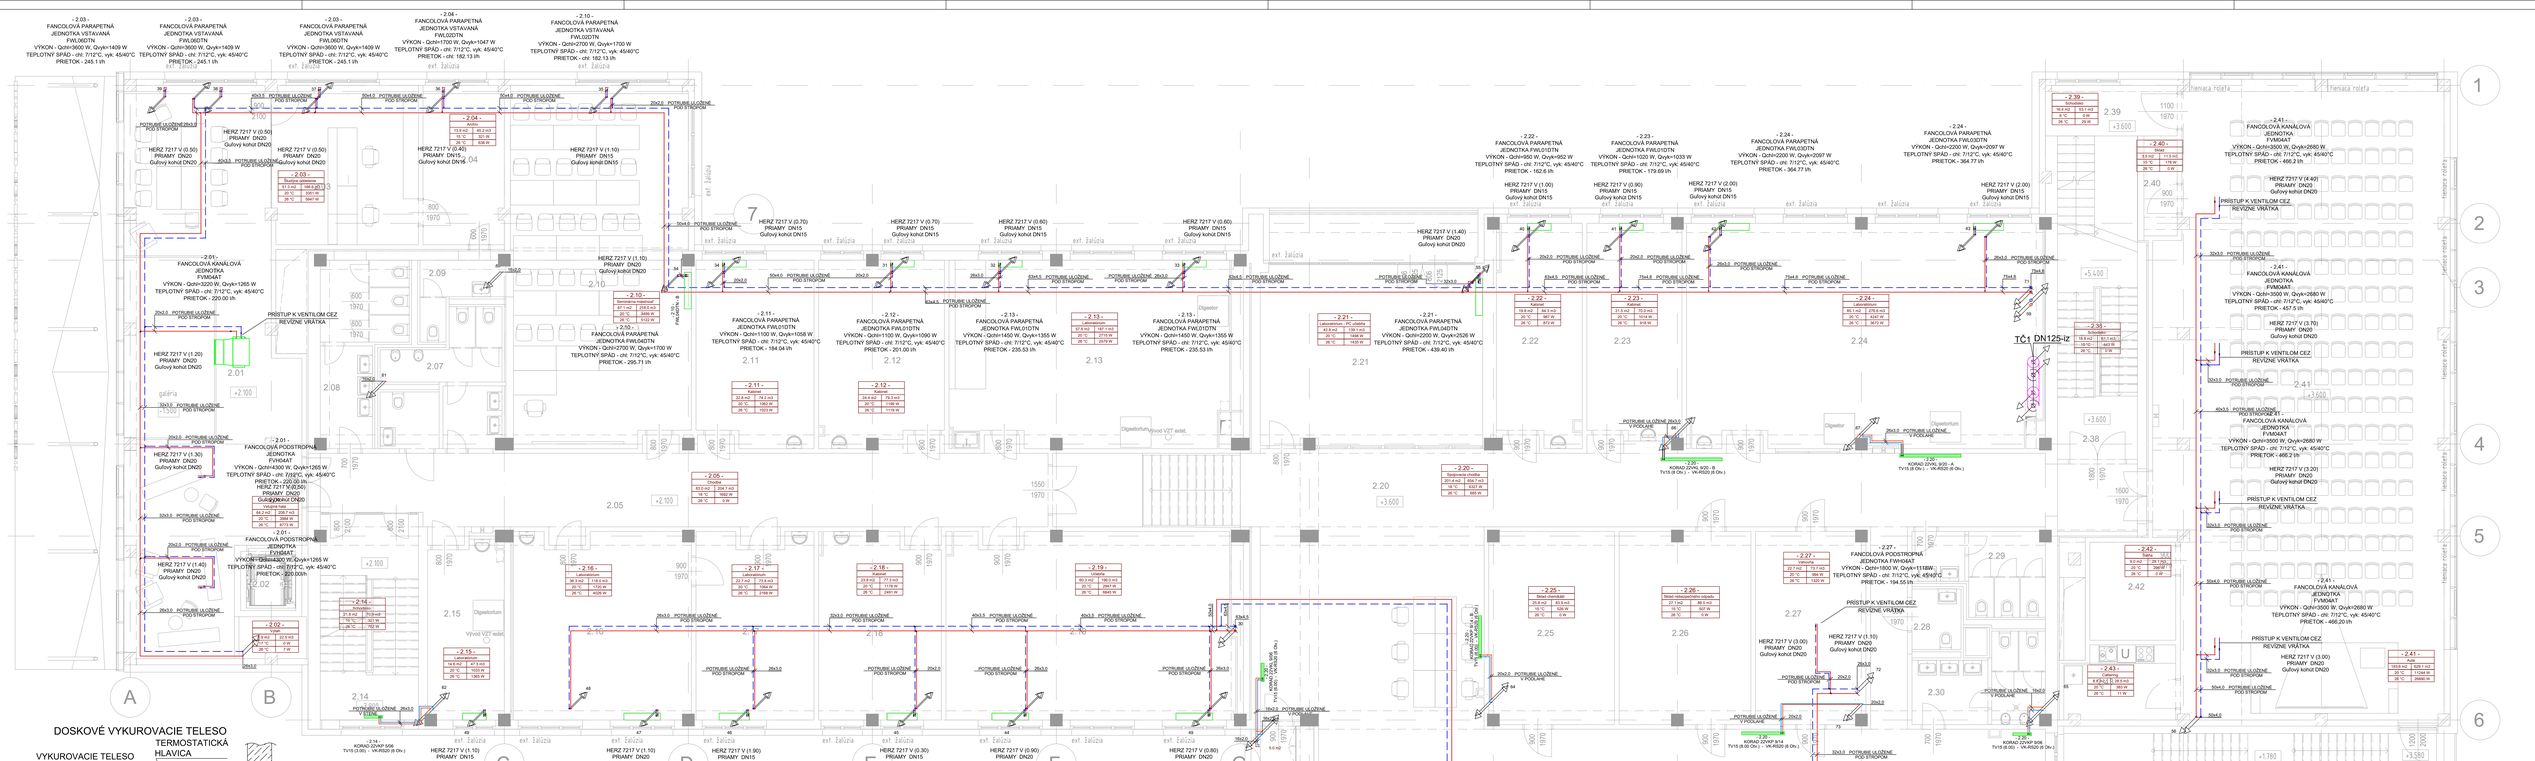



DOSKOVÉ VYKUROVACIE TELESO

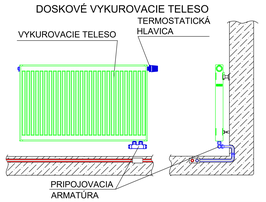


L.M. 2.NP - PBS

Č.M.	Názov	Plocha
2.01	Vstupná hala	73.09
2.02	Výťah	3.47
2.03	Študijné oddelenie	24.71
2.04	Archív	13.65
2.05	Chodba	61.99
2.06	Bezbarier. záchodová kabína	3.90
2.07	WC muži	12.01
2.08	WC ženy	14.67
2.09	WC personál	4.24
2.10	Seminárna miestnosť	67.43
2.11	Kabinet	24.00
2.12	Kabinet	25.03
2.13	Laboratórium	57.30
2.14	Schodisko	21.49
2.15	Laboratórium	14.07
2.16	Laboratórium	34.61
2.17	Laboratórium	22.72
2.18	Kabinet	23.45
2.19	Učebňa	56.09
2.20	Spojovacia chodba	199.76
2.21	Laboratórium - PC učebňa	40.89
2.22	Kabinet	19.28
2.23	Kabinet	21.43
2.24	Laboratórium	83.39
2.25	Sklad chemických látok	25.59
2.26	Sklad nebezpečného odpadu	26.81
2.27	Váhovňa	22.44
2.28	Bezbarier. záchodová kabína	3.30
2.29	WC ženy	10.04
2.30	WC muži	10.46
2.31	Upratovačka	4.80
2.32	Schodisko	30.04
2.33	Výťah	4.10
2.34	Sklad	8.86
2.35	Laboratórium	18.06
2.36	Laboratórium	19.43
2.37	Laboratórium	86.71
2.38	Schodisko	18.76
2.39	Schodisko	16.39
2.40	Sklad	3.38
2.41	Aula	186.87
2.42	Šatňa	8.96
2.43	Cattering	8.31


DETAIL NAPOJENIA KAZETOVÉHO FANCOILU:

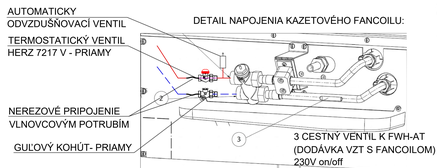

DETAIL NAPOJENIA KANÁLOVÉHO FANCOILU:

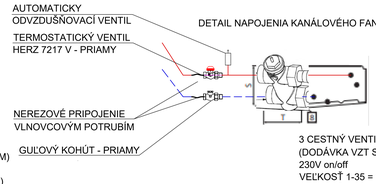

DETAIL NAPOJENIA PARAPETNÉHO FANCOILU:

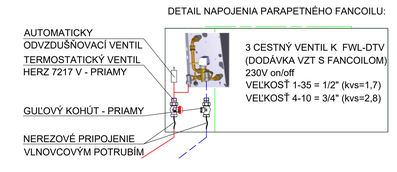

LEGENDA:

- VYKUROVACIE POTRUBIE - NÍZKOUHLÍKOVÉ OCEĽOVÉ POTRUBIE TEPLOTNÝ SPÁD 60/50 °C HLAVNÝ ROZVOD Z TEPELNÉHO ČERPADLA
- VYKUROVACIE POTRUBIE - NÍZKOUHLÍKOVÉ OCEĽOVÉ POTRUBIE TEPLOTNÝ SPÁD 60/50 °C HLAVNÝ ROZVOD Z AKUMULAČNEJ NÁDRŽE
- VYKUROVACIE POTRUBIE - PLASTOHLIKOVÉ/NÍZKOUHLÍKOVÉ OCEĽOVÉ POTRUBIE TEPLOTNÝ SPÁD 45/40 °C PRE NAPOJENIE RADIATOROV
- VYKUROVACIE POTRUBIE - PLASTOHLIKOVÉ POTRUBIE/NÍZKOUHLÍKOVÉ OCEĽOVÉ POTRUBIE TEPLOTNÝ SPÁD 45/40 °C
- EXPANZNÉ POTRUBIE
- DOSKOVÉ VYKUROVACIE TELESO
- STÚPANIE/KLESANIE POTRUBIA
- PARAPETNÁ FANCOIL JEDNOTKA
- KANÁLOVÁ VZDUCHOVÁ JEDNOTKA
- KAZETOVÁ STROPNÁ FANCOIL JEDNOTKA

LEGENDA VYKUROVACÍCH OKRUHOV:

- UK1 - Prevádzka kancelária a 6.NP Fancoil
- UK2 - Prevádzka Aula Fancoil
- UK3 - Prevádzka Bočná Južné Fancoil
- UK4 - Prevádzka Bočná Juh Fancoil
- UK5 - Prevádzka Bočná Radiátory

LEGENDA POPISOVÝCH TABULIEK:

ÚČEL MIESTNOSTI | ČÍSLO MIESTNOSTI | OBJEM MIESTNOSTI
PLOCHA MIESTNOSTI
VÝPOČTOVÁ TEPLOTA | TEPELNÁ STRATA

±0.000 = ÚROVEŇ PODLAHY 1.NP

SADA Číslo