1
2
3
4
5
6
A
B
C
D
E
F
G
M
N
O
4.01
4.02
4.03
4.04
4.05
4.06
4.07
4.08
4.09
4.10
4.11
4.12
4.13
4.14
4.15
4.16
4.17
4.18
4.19
4.20
4.21
4.22
4.23
4.24
4.25
4.26
4.27
4.28
4.29
4.30
4.31
4.32
4.33
4.43
4.44
4.45
4.46
4.47
4.48
POTRUBIE ULOŽENÉ V PODLAHE
POTRUBIE ULOŽENÉ POD STROPOM
PRÍSTUP K VENTILOM CEZ REVÍZNE VRÁTKA
HERZ 7217 V PRIAMY DN20 Guľový kohút DN20
HERZ 7217 V PRIAMY DN15 Guľový kohút DN15
FANCOLOVÁ PARAPETNÁ JEDNOTKA
FANCOLOVÁ PODSTROPNÁ JEDNOTKA
ext. žalúzia
DN125 iz
TČ1
UP
+9.000
+9.300
+10.800
+7.500

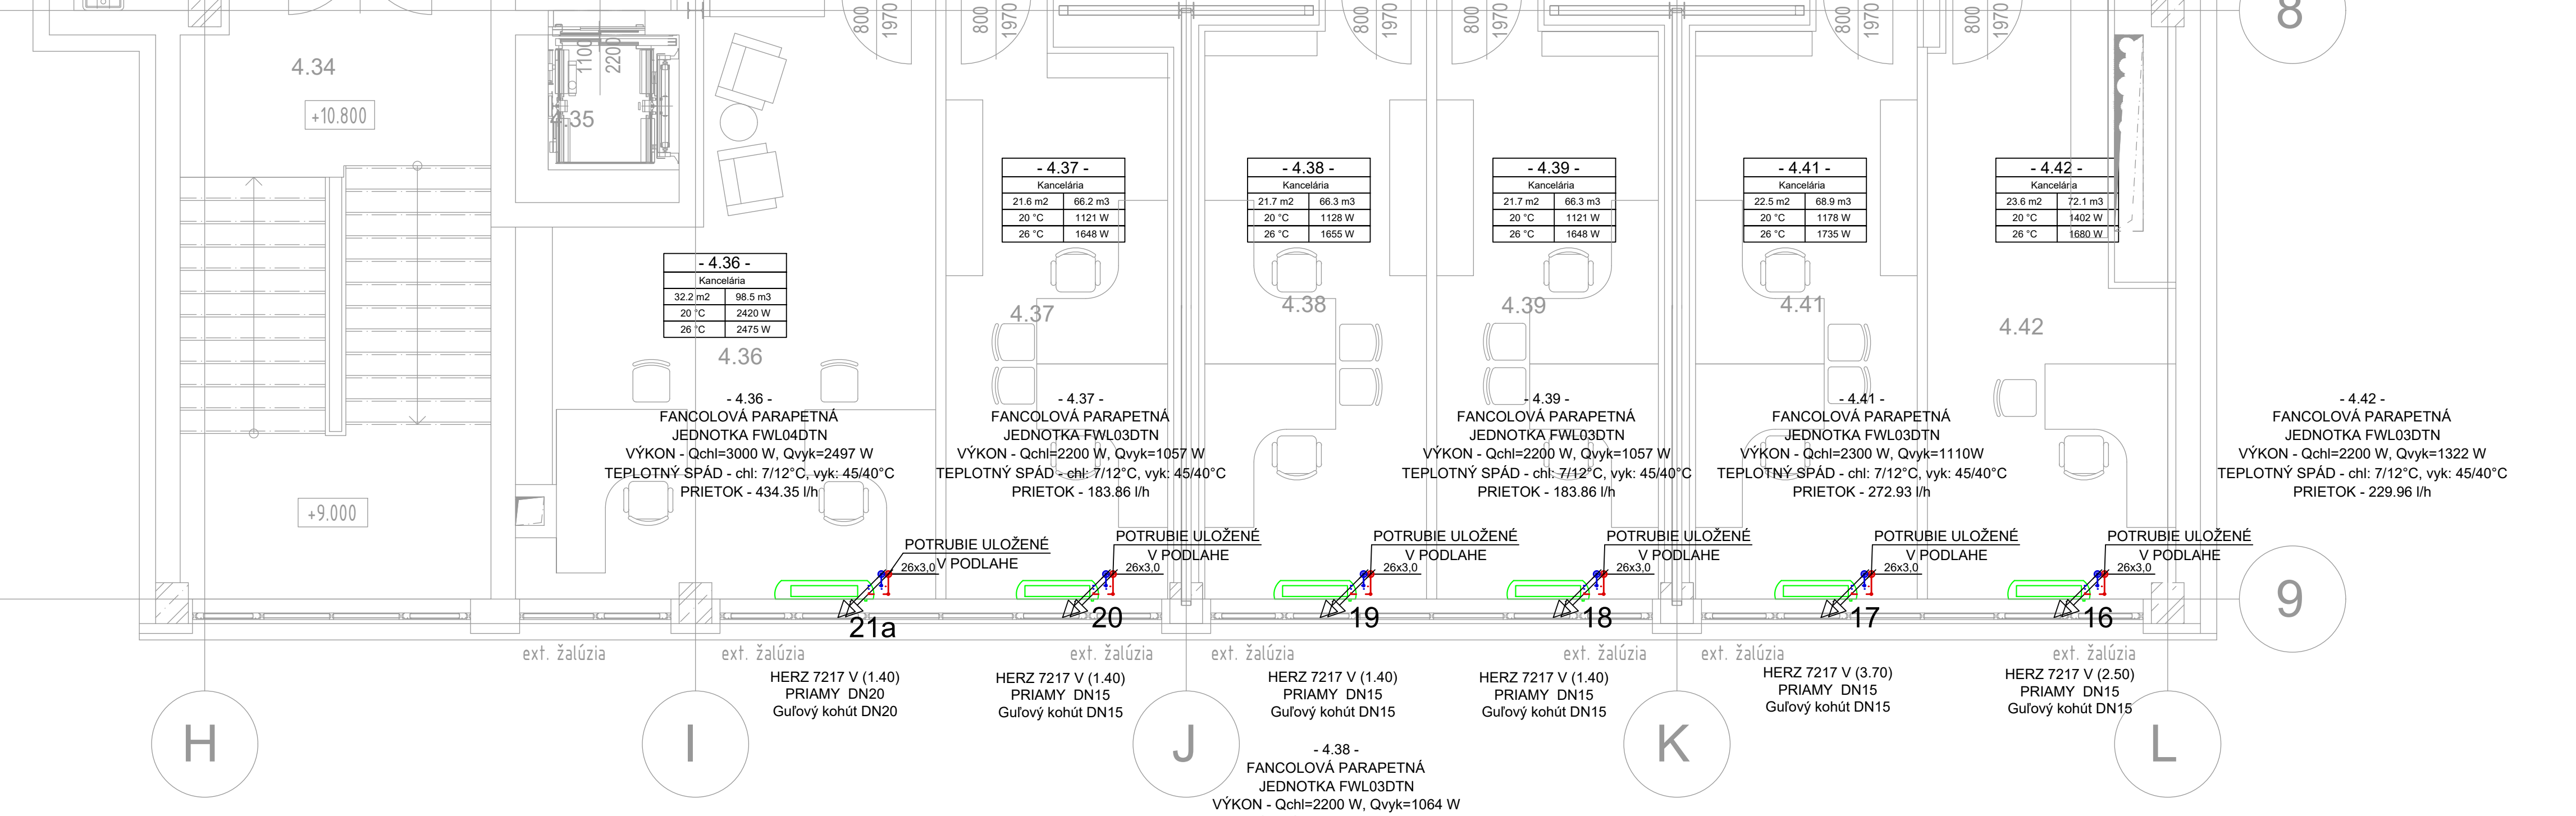

| L.M. 4.NP - PBS | | |
|---|---|---|
| Č.M. | Názov | Plocha |
| 4.01 | Vstupná hala | 52.75 |
| 4.02 | Výťah | 3.47 |
| 4.03 | Študovňa | 44.85 |
| 4.04 | Sklad kníh | 17.09 |
| 4.05 | Bezbarier. záchodová kabína | 3.71 |
| 4.06 | WC ženy | 5.62 |
| 4.07 | WC personál | 1.97 |
| 4.08 | WC muži | 13.03 |
| 4.09 | Seminárna miestnosť | 67.28 |
| 4.10 | Kancelária | 21.00 |
| 4.11 | Kancelária | 19.47 |
| 4.12 | Kancelária | 16.26 |
| 4.13 | Jazyková učebňa | 48.19 |
| 4.14 | Schodisko | 21.56 |
| 4.15 | Kancelária | 26.52 |
| 4.16 | Kancelária | 16.03 |
| 4.17 | Kancelária | 24.69 |
| 4.18 | Kancelária | 16.84 |
| 4.19 | Kancelária | 17.04 |
| 4.20 | Kancelária | 24.64 |
| 4.21 | Kancelária | 27.91 |
| 4.22 | Spojovacia chodba | 220.43 |
| 4.23 | Kancelária | 26.85 |
| 4.24 | Kancelária | 26.34 |
| 4.25 | Kancelária | 33.03 |
| 4.26 | Kancelária | 29.12 |
| 4.27 | Kancelária | 29.64 |
| 4.28 | Kancelária | 31.93 |
| 4.29 | Multifunkčný priestor | 75.60 |
| 4.30 | Bezbarier. záchodová kabína | 3.46 |
| 4.31 | WC ženy | 10.38 |
| 4.32 | WC muži | 11.27 |
| 4.33 | Upratovačka | 4.90 |
| 4.34 | Schodisko | 29.94 |
| 4.35 | Výťah | 4.10 |
| 4.36 | Kancelária | 31.11 |
| 4.37 | Kancelária | 19.20 |
| 4.38 | Kancelária | 19.61 |
| 4.39 | Kancelária | 19.60 |
| 4.41 | Kancelária | 19.61 |
| 4.42 | Kancelária | 19.33 |
| 4.43 | Schodisko | 18.02 |
| 4.44 | Sklad dizajn | 19.74 |
| 4.45 | Seminárna miestnosť | 111.65 |
| 4.46 | Ateliér II | 48.46 |
| 4.47 | Kancelária | 26.43 |
| 4.48 | Chodba | 53.88 |

DETAIL NAPOJENIA KAZETOVÉHO FANCOILU:

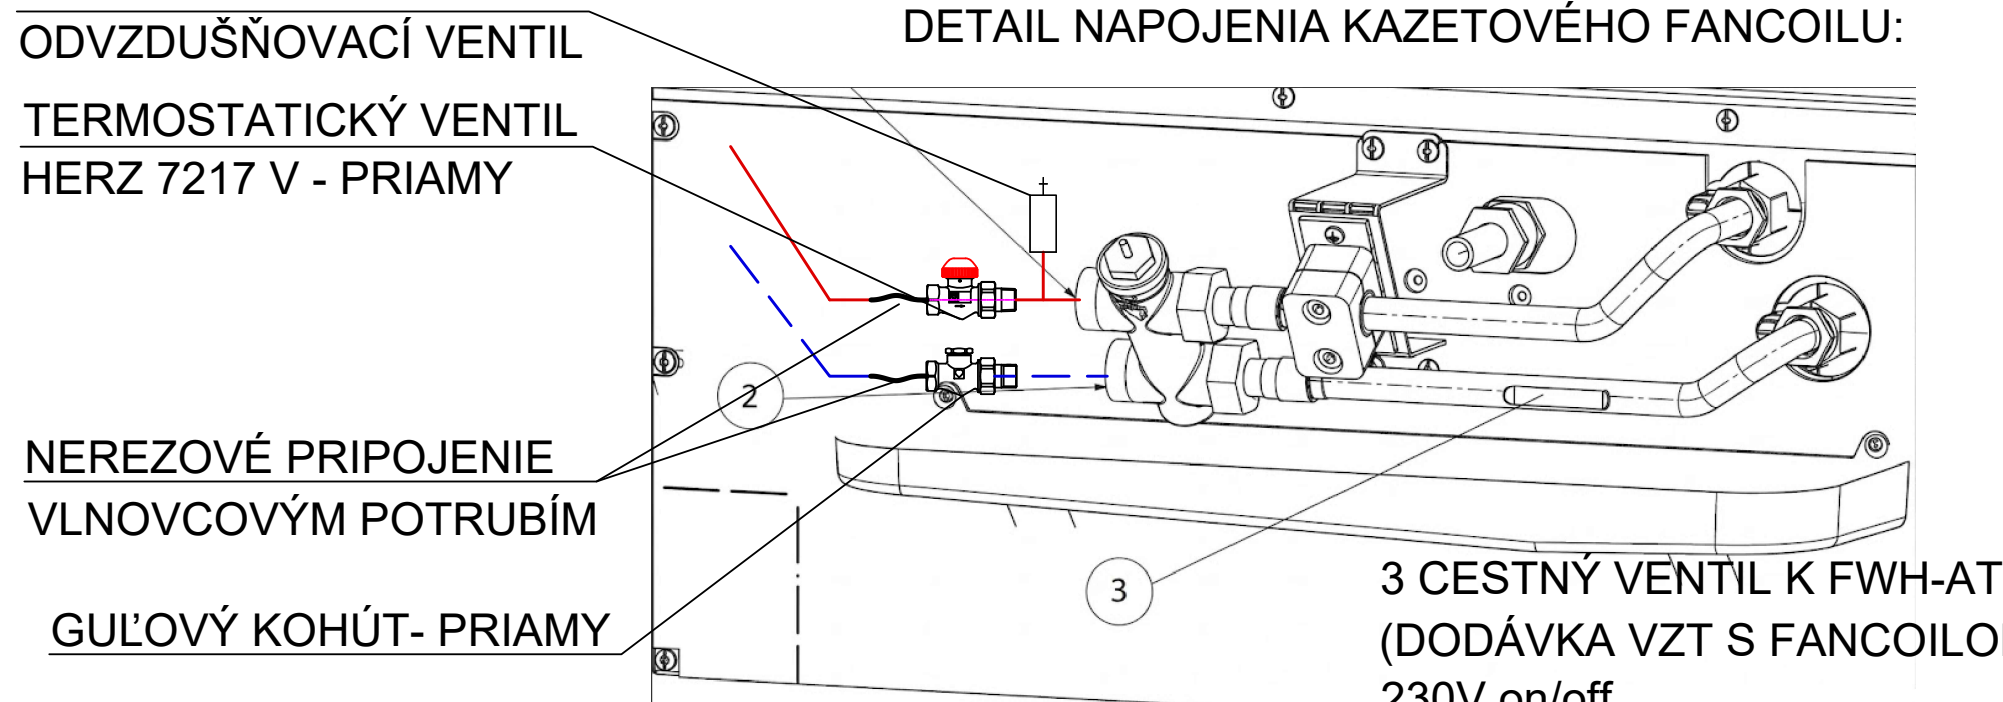
AUTOMATICKY ODVZDUŠŇOVACÍ VENTIL
TERMOSTATICKÝ VENTIL HERZ 7217 V - PRIAMY
NEREZOVÉ PRIPOJENIE VLNOVCOVÝM POTRUBÍM
GUĽOVÝ KOHÚT- PRIAMY
2
3

3 CESTNÝ VENTIL K FWH-AT
(DODÁVKA VZT S FANCOILOM)
230V on/off
VEĽKOSŤ 1-35 = 1/2" (kvs=1,7)
VEĽKOSŤ 4-10 = 3/4" (kvs=2,8)

DETAIL NAPOJENIA KANÁLOVÉHO FANCOILU:

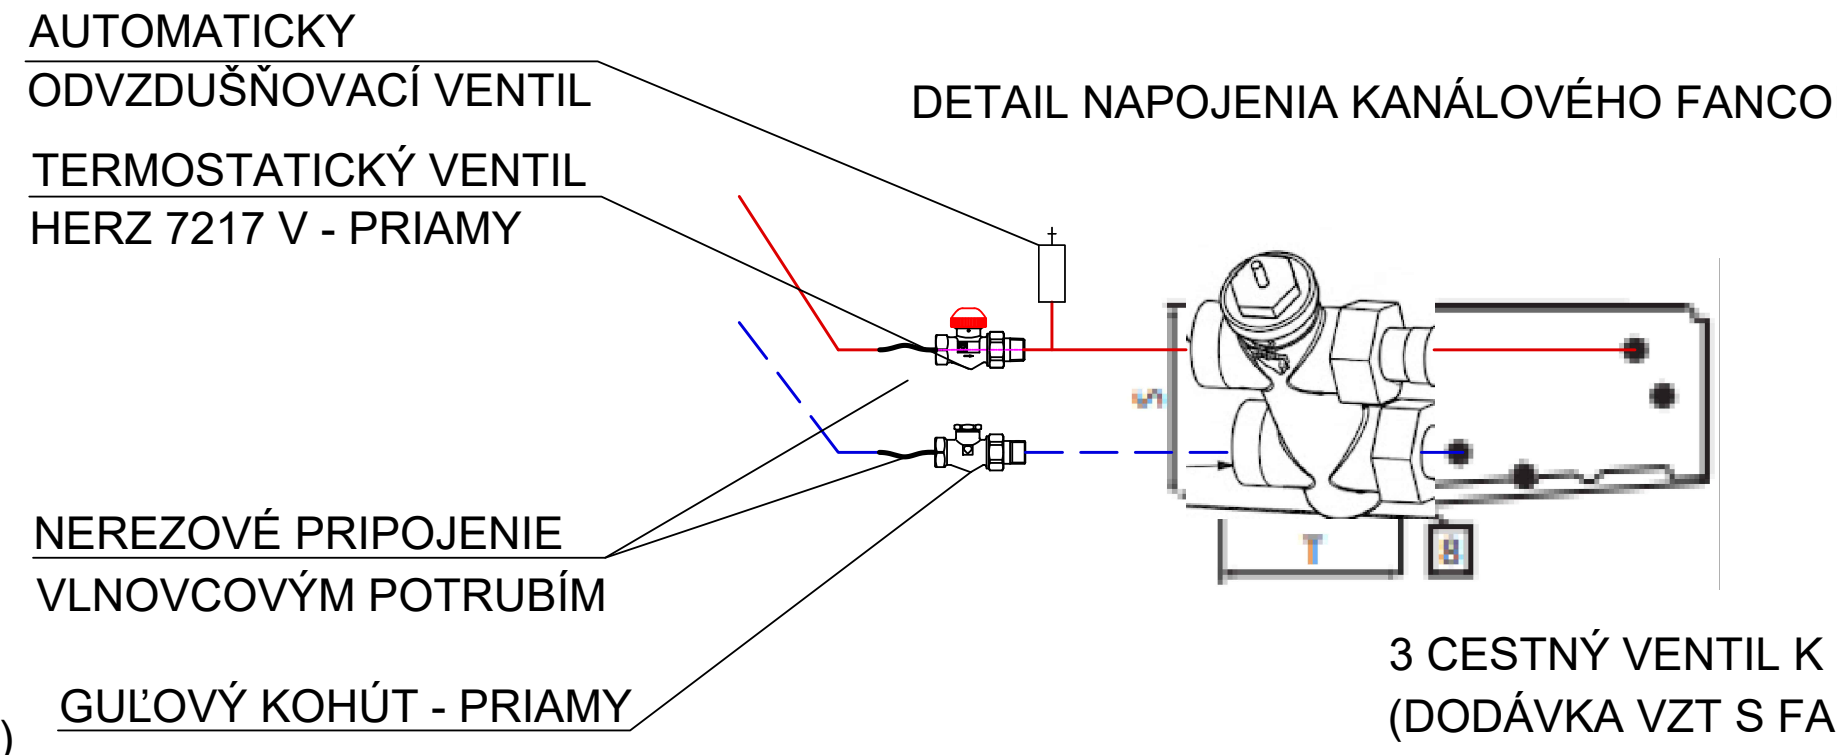
AUTOMATICKY ODVZDUŠŇOVACÍ VENTIL
TERMOSTATICKÝ VENTIL HERZ 7217 V - PRIAMY
NEREZOVÉ PRIPOJENIE VLNOVCOVÝM POTRUBÍM
GUĽOVÝ KOHÚT - PRIAMY
S
T
B

3 CESTNÝ VENTIL K FWM-AT
(DODÁVKA VZT S FANCOILOM)
230V on/off
VEĽKOSŤ 1-35 = 1/2" (kvs=1,7)
VEĽKOSŤ 4-10 = 3/4" (kvs=2,8)

DETAIL NAPOJENIA PARAPETNÉHO FANCOILU:

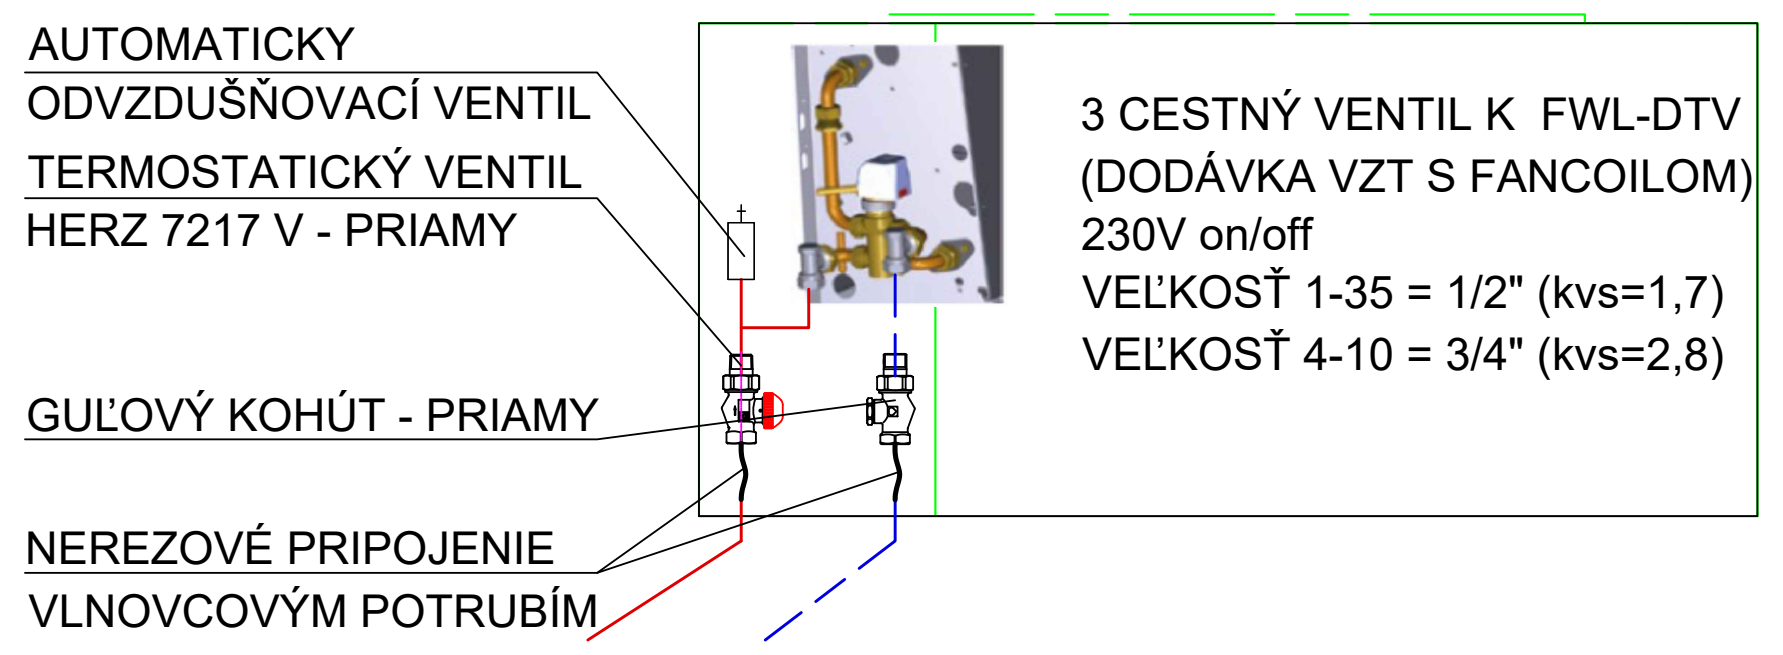
AUTOMATICKY ODVZDUŠŇOVACÍ VENTIL
TERMOSTATICKÝ VENTIL HERZ 7217 V - PRIAMY
GUĽOVÝ KOHÚT - PRIAMY
NEREZOVÉ PRIPOJENIE VLNOVCOVÝM POTRUBÍM

3 CESTNÝ VENTIL K FWL-DTV
(DODÁVKA VZT S FANCOILOM)
230V on/off
VEĽKOSŤ 1-35 = 1/2" (kvs=1,7)
VEĽKOSŤ 4-10 = 3/4" (kvs=2,8)

LEGENDA:

VYKUROVACIE POTRUBIE - NÍZKOUHLÍKOVÉ OCELOVÉ POTRUBIE TEPLOTNÝ SPÁD 60/50 °C HLAVNÝ ROZVOD Z TEPELNÉHO ČERPADLA

VYKUROVACIE POTRUBIE - NÍZKOUHLÍKOVÉ OCELOVÉ POTRUBIE TEPLOTNÝ SPÁD 60/50 °C HLAVNÝ ROZVOD Z AKUMULAČNEJ NÁDRŽE

VYKUROVACIE POTRUBIE - PLASTOHLÍKOVÉ/NÍZKOUHLÍKOVÉ OCELOVÉ POTRUBIE TEPLOTNÝ SPÁD 45/40 °C PRE NAPOJENIE RADIATOROV

VYKUROVACIE POTRUBIE - PLASTOHLÍKOVÉ POTRUBIE/NÍZKOUHLÍKOVÉ OCELOVÉ POTRUBIE TEPLOTNÝ SPÁD 45/40 °C

EXPANZNÉ POTRUBIE

DOSKOVÉ VYKUROVACIE TELESO

STÚPANIE/KLESANIE POTRUBIA

PARAPETNÁ FANCOIL JEDNOTKA

KANÁLOVÁ VZDUCHOVÁ JEDNOTKA

KAZETOVÁ STROPNÁ FANCOIL JEDNOTKA

LEGENDA VYKUROVACÍCH OKRUHOV:

UK1 - Prevádzka kancelárie 4.NP Fancoil
UK2 - Prevádzka Aula Fancoil
UK3 - Prevádzka škola Sever Fancoil
UK4 - Prevádzka škola Juh Fancoil
UK5 - Prevádzka škola Radiatory

LEGENDA POPISOVÝCH TABULIEK:

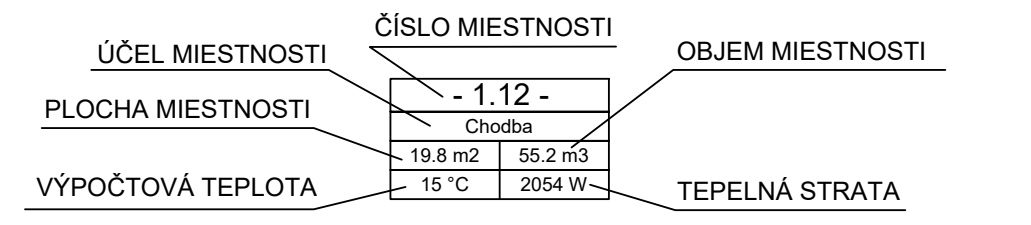

±0,000 = ÚROVEŇ PODLAHY 1.NP

SADA ČÍSLO

Objednávateľ: Trenčiansky samosprávny kraj, K dolnej stanici 7282/20A, 911 01 Trenčín,
Tre
Generálny projekt
Kontroloval: Ing.
Kraj: Trenčiansky
Investor: Trenčian
Trenčian
Miesto stavby: k.ú
15
Stupeň PD:
Akcia:
Objekt: SO 20
Obsah: Pôdor