VETVA RADIATORY

4. NP 10.800
3. NP 7.200
2. NP 3.600
1. NP 0.000
RADIATORY
- 3.31 -
KORAD 11VKP 6/04
TV15 (1) - VK-RS20 (6 Otv.)
176 W
- 3.20 -
KORAD 22VKL 9/06
TV15 (3.00) - VK-RS20 (6 Otv.)
543 W
- 3.32 -
KORAD 22VKP 6/14
TV15 (6.00) - VK-RS20 (6 Otv.)
1071 W
- 3.20 -
KORAD 22VKP 9/14 - B
TV15 (6.00) - VK-RS20 (6 Otv.)
1268 W
- 3.16 -
KORAD 22VKL 6/06
TV15 (2.00) - VK-RS20 (6 Otv.)
459 W
- 3.20 -
KORAD 22VKL 9/20 - B
TV15 (8 Otv.) - VK-RS20 (6 Otv.)
1812 W
- 3.20 -
KORAD 22VKL 9/20 - A
TV15 (8 Otv.) - VK-RS20 (6 Otv.)
1812 W
- 3.20 -
KORAD 22VKP 9/06
TV15 (3.00) - VK-RS20 (6 Otv.)
543 W
- 3.20 -
KORAD 22VKP 9/14 - A
TV15 (6.00) - VK-RS20 (6 Otv.)
1268 W
- 3.10 -
KORAD 11VKP 3/06
TV15 (1) - VK-RS20 (6 Otv.)
151 W
- 3.08 -
KORAD 11VKP 3/06
TV15 (1) - VK-RS20 (6 Otv.)
151 W
- 2.31 -
KORAD 11VKP 6/04
TV15 (1) - VK-RS20 (6 Otv.)
176 W
- 2.20 -
KORAD 22VKL 9/06
TV15 (3.00) - VK-RS20 (6 Otv.)
543 W
- 2.38 -
KORAD 22VKP 6/14
TV15 (6.00) - VK-RS20 (6 Otv.)
1071 W
- 2.20 -
KORAD 22VKP 9/14 - B
TV15 (6.00) - VK-RS20 (6 Otv.)
1268 W
- 2.14 -
KORAD 22VKP 5/06
TV15 (2.00) - VK-RS20 (6 Otv.)
399 W
- 2.20 -
KORAD 22VKL 9/20 - B
TV15 (8 Otv.) - VK-RS20 (6 Otv.)
1812 W
- 2.20 -
KORAD 22VKL 9/20 - A
TV15 (8 Otv.) - VK-RS20 (6 Otv.)
1812 W
- 2.20 -
KORAD 22VKP 9/06
TV15 (3.00) - VK-RS20 (6 Otv.)
543 W
- 2.20 -
KORAD 22VKP 9/14 - A
TV15 (6.00) - VK-RS20 (6 Otv.)
1268 W
- 1.21 -
KORAD 22VKL 9/14 - A
TV15 (6.00) - VK-RS20 (6 Otv.)
1268 W
- 1.32 -
KORAD 22VKP 9/14
TV15 (8.00 Otv.) - VK-RS20 (6 Otv.)
1480 W
- 1.21 -
KORAD 22VKL 9/14
TV15 (6.00) - VK-RS20 (6 Otv.)
1268 W
- 1.27 -
KORAD 22VKL 9/20
TV15 (8 Otv.) - VK-RS20 (6 Otv.)
2114 W
- 1.08 -
KORAD 22VKL 6/10
TV15 (4.00) - VK-RS20 (6 Otv.)
765 W
- 1.42 -
KORAD 22VKP 6/20 - A
TV15 (6.00) - VK-RS20 (6 Otv.)
1171 W
- 1.41 -
KORAD 22VKL 6/06
TV15 (2.00) - VK-RS20 (6 Otv.)
459 W
- 1.42 -
KORAD 22VKP 6/18
TV15 (6.00) - VK-RS20 (6 Otv.)
1054 W
- 1.43 -
KORAD 22VKP 6/20
TV15 (8.00 Otv.) - VK-RS20 (6 Otv.)
1531 W
- 1.21 -
KORAD 22VKL 9/20
TV15 (8 Otv.) - VK-RS20 (6 Otv.)
1812 W
- 1.21 -
KORAD 22VKL 9/20
TV15 (8 Otv.) - VK-RS20 (6 Otv.)
1812 W
- 1.42 -
KORAD 22VKP 6/20 - B
TV15 (6.00) - VK-RS20 (6 Otv.)
1171 W
- 1.44 -
KORAD 22VKP 9/14
TV15 (6.00) - VK-RS20 (6 Otv.)
1268 W
- 1.45 -
KORAD 22VKP 6/08
TV15 (3.00) - VK-RS20 (6 Otv.)
612 W
- 1.48 -
KORAD 22VKL 6/14
TV15 (6.00) - VK-RS20 (6 Otv.)
1071 W
- 1.47 -
KORAD 22VKP 6/08
TV15 (3.00) - VK-RS20 (6 Otv.)
612 W
- 1.39 -
KORAD 22VKP 6/16
TV15 (6.00) - VK-RS20 (6 Otv.)
1049 W
- 1.46 -
KORAD 22VKP 6/08
TV15 (3.00) - VK-RS20 (6 Otv.)
612 W
- 1.30 -
KORAD 11VKP 6/06
TV15 (1) - VK-RS20 (6 Otv.)
264 W
- 1.21 -
KORAD 22VKP 9/06
TV15 (3.00) - VK-RS20 (6 Otv.)
543 W
- 1.29 -
KORAD 11VKP 6/06
TV15 (1) - VK-RS20 (6 Otv.)
264 W
- 1.21 -
KORAD 22VKL 9/14 - B
TV15 (6.00) - VK-RS20 (6 Otv.)
1268 W
- 1.11 -
KORAD 22VKP 6/08
TV15 (2.00) - VK-RS20 (6 Otv.)
468 W
- 1.10 -
KORAD 11VKL 4/04
TV15 (1) - VK-RS20 (6 Otv.)
127 W
65
63
62
64
66
67
68
69
61
60
PP
2xGK - DN 15
2x AUT. ODVZD.
1F
2F
3F
4F
5F
6F
7F
11F
STRÖMAX-GM 2013(meranie)
DN 50, Nastavenie 7.00
Prietok 7343.5 l/h
Tlaková strata 4338 Pa
75x4,6
2xGK DN50
GK DN50
RTD DN 50
77.854 kPa
7343.5 l/h
Vetva RADIATORY
Q=42216 W
H=77821 Pa
dt=45.0/40.0 °C
16x2,0
20x2,0
26x3,0
32x3,0
40x3,5
50x4,0
63x4,5
75x4,6

VETVA 4.NP

4. NP 10.800
3. NP 7.200
- 4.43 -
FANCOLOVÁ PARAPETNÁ
JEDNOTKA FWL02DTN
VÝKON - Qchl=1350 W, Qvyk=976 W
TEPLOTNÝ SPÁD - chl: 7/12°C, vyk: 45/40°C
PRIETOK - 169.8 l/h
- 4.28 -
FANCOLOVÁ PARAPETNÁ
JEDNOTKA FWL04DTN
VÝKON - Qchl=2470 W, Qvyk=1998 W
TEPLOTNÝ SPÁD - chl: 7/12°C, vyk: 45/40°C
PRIETOK - 347.6 l/h
- 4.27 -
FANCOLOVÁ PARAPETNÁ
JEDNOTKA FWL03DTN
VÝKON - Qchl=2100 W, Qvyk=1584 W
TEPLOTNÝ SPÁD - chl: 7/12°C, vyk: 45/40°C
PRIETOK - 275.5 l/h
- 4.21 -
FANCOLOVÁ PARAPETNÁ
JEDNOTKA FWL04DTN
VÝKON - Qchl=3000 W, Qvyk=1771 W
TEPLOTNÝ SPÁD - chl: 7/12°C, vyk: 45/40°C
PRIETOK - 308.1 l/h
- 4.20 -
FANCOLOVÁ PARAPETNÁ
JEDNOTKA FWL04DTN
VÝKON - Qchl=2470 W, Qvyk=1387 W
TEPLOTNÝ SPÁD - chl: 7/12°C, vyk: 45/40°C
PRIETOK - 169.8 l/h
- 4.19 -
FANCOLOVÁ PARAPETNÁ
JEDNOTKA FWL02DTN
VÝKON - Qchl=1750 W, Qvyk=1024 W
TEPLOTNÝ SPÁD - chl: 7/12°C, vyk: 45/40°C
PRIETOK - 178.1 l/h
- 4.18 -
FANCOLOVÁ PARAPETNÁ
JEDNOTKA FWL02DTN
VÝKON - Qchl=1660 W, Qvyk=965 W
TEPLOTNÝ SPÁD - chl: 7/12°C, vyk: 45/40°C
PRIETOK - 167.9 l/h
- 4.17 -
FANCOLOVÁ PARAPETNÁ
JEDNOTKA FWL04DTN
VÝKON - Qchl=2470 W, Qvyk=1389 W
TEPLOTNÝ SPÁD - chl: 7/12°C, vyk: 45/40°C
PRIETOK - 169.8 l/h
- 4.16 -
FANCOLOVÁ PARAPETNÁ
JEDNOTKA FWL02DTN
VÝKON - Qchl=1600 W, Qvyk=937 W
TEPLOTNÝ SPÁD - chl: 7/12°C, vyk: 45/40°C
PRIETOK - 163.0 l/h
- 4.15 -
FANCOLOVÁ PARAPETNÁ
JEDNOTKA FWL04DTN
VÝKON - Qchl=2600 W, Qvyk=1791 W
TEPLOTNÝ SPÁD - chl: 7/12°C, vyk: 45/40°C
PRIETOK - 311.5 l/h
- 4.38 -
FANCOLOVÁ PARAPETNÁ
JEDNOTKA FWL03DTN
VÝKON - Qchl=2200 W, Qvyk=1064 W
TEPLOTNÝ SPÁD - chl: 7/12°C, vyk: 45/40°C
PRIETOK - 169.8 l/h
- 4.39 -
FANCOLOVÁ PARAPETNÁ
JEDNOTKA FWL03DTN
VÝKON - Qchl=2200 W, Qvyk=1057 W
TEPLOTNÝ SPÁD - chl: 7/12°C, vyk: 45/40°C
PRIETOK - 183.9 l/h
- 4.40 -
FANCOLOVÁ PARAPETNÁ
JEDNOTKA FWL03DTN
VÝKON - Qchl=2300 W, Qvyk=1569 W
TEPLOTNÝ SPÁD - chl: 7/12°C, vyk: 45/40°C
PRIETOK - 272.9 l/h
- 4.41 -
FANCOLOVÁ PARAPETNÁ
JEDNOTKA FWL03DTN
VÝKON - Qchl=2200 W, Qvyk=1322 W
TEPLOTNÝ SPÁD - chl: 7/12°C, vyk: 45/40°C
PRIETOK - 230.0 l/h
- 4.37 -
FANCOLOVÁ PARAPETNÁ
JEDNOTKA FWL03DTN
VÝKON - Qchl=2200 W, Qvyk=1057 W
TEPLOTNÝ SPÁD - chl: 7/12°C, vyk: 45/40°C
PRIETOK - 183.9 l/h
- 4.36 -
FANCOLOVÁ PARAPETNÁ
JEDNOTKA FWL04DTN
VÝKON - Qchl=3000 W, Qvyk=2497 W
TEPLOTNÝ SPÁD - chl: 7/12°C, vyk: 45/40°C
PRIETOK - 434.4 l/h
- 4.26 -
FANCOLOVÁ PARAPETNÁ
JEDNOTKA FWL03DTN
VÝKON - Qchl=2100 W, Qvyk=1569 W
TEPLOTNÝ SPÁD - chl: 7/12°C, vyk: 45/40°C
PRIETOK - 272.9 l/h
- 4.25 -
FANCOLOVÁ PARAPETNÁ
JEDNOTKA FWL04DTN
VÝKON - Qchl=2400 W, Qvyk=1775 W
TEPLOTNÝ SPÁD - chl: 7/12°C, vyk: 45/40°C
PRIETOK - 308.8 l/h
- 4.24 -
FANCOLOVÁ PARAPETNÁ
JEDNOTKA FWL03DTN
VÝKON - Qchl=2050 W, Qvyk=1510 W
TEPLOTNÝ SPÁD - chl: 7/12°C, vyk: 45/40°C
PRIETOK - 262.7 l/h
- 4.23 -
FANCOLOVÁ PARAPETNÁ
JEDNOTKA FWL03DTN
VÝKON - Qchl=2000 W, Qvyk=1499 W
TEPLOTNÝ SPÁD - chl: 7/12°C, vyk: 45/40°C
PRIETOK - 260.8 l/h
- 4.13 -
FANCOLOVÁ PARAPETNÁ
JEDNOTKA FWL02DTN
VÝKON - Qchl=1850 W, Qvyk=1418 W
TEPLOTNÝ SPÁD - chl: 7/12°C, vyk: 45/40°C
PRIETOK - 246.7 l/h
- 4.13 -
FANCOLOVÁ PARAPETNÁ
JEDNOTKA FWL02DTN
VÝKON - Qchl=1850 W, Qvyk=1418 W
TEPLOTNÝ SPÁD - chl: 7/12°C, vyk: 45/40°C
PRIETOK - 246.7 l/h
- 4.12 -
FANCOLOVÁ PARAPETNÁ
JEDNOTKA FWL01DTN
VÝKON - Qchl=1100 W, Qvyk=921 W
TEPLOTNÝ SPÁD - chl: 7/12°C, vyk: 45/40°C
PRIETOK - 160.2 l/h
- 4.11 -
FANCOLOVÁ PARAPETNÁ
JEDNOTKA FWL02DTN
VÝKON - Qchl=1500 W, Qvyk=1138 W
TEPLOTNÝ SPÁD - chl: 7/12°C, vyk: 45/40°C
PRIETOK - 198.0 l/h
- 4.10 -
FANCOLOVÁ PARAPETNÁ
JEDNOTKA FWL02DTN
VÝKON - Qchl=1660 W, Qvyk=1200 W
TEPLOTNÝ SPÁD - chl: 7/12°C, vyk: 45/40°C
PRIETOK - 208.7 l/h
- 4.09 -
FANCOLOVÁ PARAPETNÁ
JEDNOTKA FWL04DTN
VÝKON - Qchl=3000 W, Qvyk=1760 W
TEPLOTNÝ SPÁD - chl: 7/12°C, vyk: 45/40°C
PRIETOK - 306.2 l/h
- 4.09 -
FANCOLOVÁ PARAPETNÁ VSTAVANÁ
JEDNOTKA FWL04DTN
VÝKON - Qchl=3000 W, Qvyk=1760 W
TEPLOTNÝ SPÁD - chl: 7/12°C, vyk: 45/40°C
PRIETOK - 306.2 l/h
- 4.04 -
FANCOLOVÁ PARAPETNÁ VSTAVANÁ
JEDNOTKA FWL01DTN
VÝKON - Qchl=1100 W, Qvyk=458 W
TEPLOTNÝ SPÁD - chl: 7/12°C, vyk: 45/40°C
PRIETOK - 79.7 l/h
- 4.03 -
FANCOLOVÁ PARAPETNÁ VSTAVANÁ
JEDNOTKA FWL02DTN
VÝKON - Qchl=5300 W, Qvyk=1946 W
TEPLOTNÝ SPÁD - chl: 7/12°C, vyk: 45/40°C
PRIETOK - 338.5 l/h
- 4.03 -
FANCOLOVÁ PARAPETNÁ VSTAVANÁ
JEDNOTKA FWL02DTN
VÝKON - Qchl=5300 W, Qvyk=1946 W
TEPLOTNÝ SPÁD - chl: 7/12°C, vyk: 45/40°C
PRIETOK - 338.5 l/h
- 4.01 -
FANCOLOVÁ PODSTROPNÁ
JEDNOTKA
FVH04AT
VÝKON - Qchl=4300 W, Qvyk=744 W
TEPLOTNÝ SPÁD - chl: 7/12°C, vyk: 45/40°C
PRIETOK - 129.4 l/h
- 4.22 -
FANCOLOVÁ PODSTROPNÁ
JEDNOTKA
FVH04AT
VÝKON - Qchl=4000 W, Qvyk=3017 W
TEPLOTNÝ SPÁD - chl: 7/12°C, vyk: 45/40°C
PRIETOK - 524.8 l/h
- 4.29 -
FANCOLOVÁ PODSTROPNÁ
JEDNOTKA
FVH04AT
VÝKON - Qchl=4000 W, Qvyk=3017 W
TEPLOTNÝ SPÁD - chl: 7/12°C, vyk: 45/40°C
PRIETOK - 524.8 l/h
- 4.46 -
FANCOLOVÁ PODSTROPNÁ
JEDNOTKA
FVH04AT
VÝKON - Qchl=1899 W, Qvyk=3000 W
TEPLOTNÝ SPÁD - chl: 7/12°C, vyk: 45/40°C
PRIETOK - 521.8 l/h
- 4.44 -
FANCOLOVÁ PODSTROPNÁ
JEDNOTKA
FVH04AT
VÝKON - Qchl=4500 W, Qvyk=3136 W
TEPLOTNÝ SPÁD - chl: 7/12°C, vyk: 45/40°C
PRIETOK - 545.5 l/h
- 4.45 -
FANCOLOVÁ PODSTROPNÁ
JEDNOTKA
FVH04AT
VÝKON - Qchl=4100 W, Qvyk=3080 W
TEPLOTNÝ SPÁD - chl: 7/12°C, vyk: 45/40°C
PRIETOK - 535.8 l/h
AOV
HERZ 7217 V (1.10) DN 15
GK s pákovým ovládačom DN 15
GK s pákovým ovládačom DN 20
HERZ 7217 V (1.00) DN20
GK s pákovým ovládačom DN20
3 CESTNÝ VENTIL K FWL-DTN
3 CESTNÝ VENTIL K FWH-AT
(DODÁVKA VZT S FANCOILOM)
69
59
29
PP
2xGK - DN 15
2x AUT. ODVZD.
75x4,6-iz
108x2,0-iz
STRÖMAX-GM 2013(meranie)
DN 80, Nastavenie 6.75
Prietok 11669.4 l/h
Tlaková strata 3036 Pa
GK DN40
2xGK DN40
RTD DN 50
50.000 kPa
11669.4 l/h
1F
Vetva 4.NP
Q=67085 W
H=141665 Pa
dt=45.0/40.0 °C
Q-chl=104979 W
H=125614 Pa
dt,chl=7.0/12.0 °C

LEGENDA:

- VYK. POTRUBIE NÍZKOUHLÍKOVÉ OCELOVÉ/PLASTOHLINÍKOVÉ POTRUBIE
- VYK. POTRUBIE NÍZKOUHLÍKOVÉ OCELOVÉ/PLASTOHLINÍKOVÉ POTRUBIE, RADIATOROVÉ
- PP POŽIARNY PRESTUP

DETAIL NAPOJENIA KANÁLOVÉHO FANCOILU:

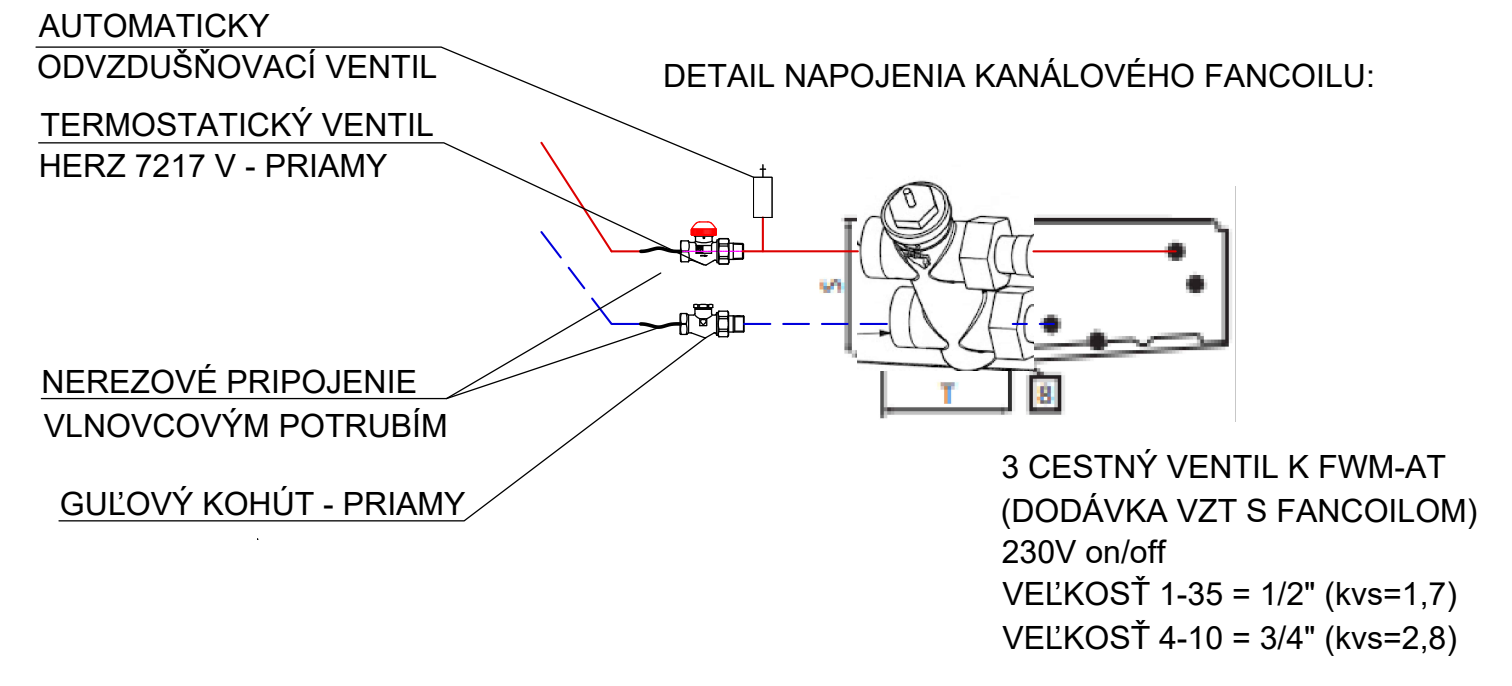
AUTOMATICKY ODVZDUŠŇOVACÍ VENTIL
TERMOSTATICKÝ VENTIL HERZ 7217 V - PRIAMY
NEREZOVÉ PRIPOJENIE VLNOVCOVÝM POTRUBÍM
GUĽOVÝ KOHÚT - PRIAMY

3 CESTNÝ VENTIL K FWM-AT
(DODÁVKA VZT S FANCOILOM)
230V on/off
VEĽKOSŤ 1-35 = 1/2" (kvs=1,7)
VEĽKOSŤ 4-10 = 3/4" (kvs=2,8)

DETAIL NAPOJENIA KAZETOVÉHO FANCOILU:

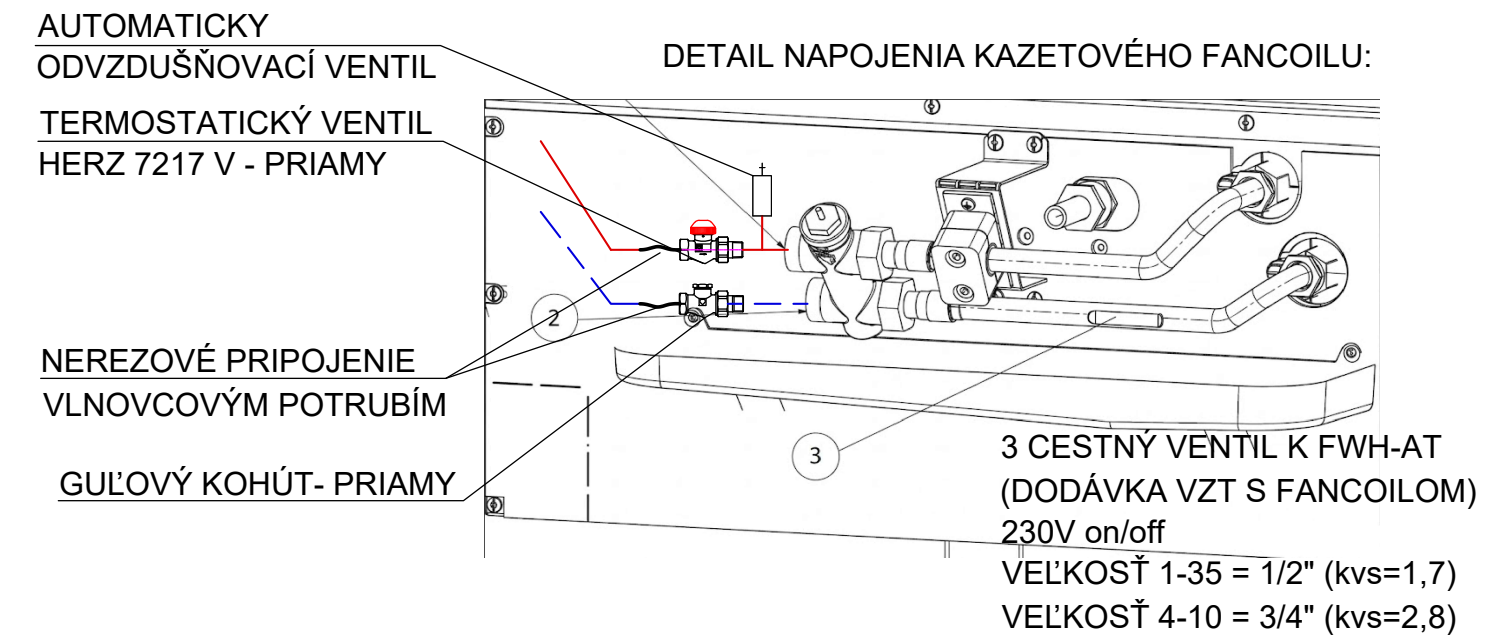
AUTOMATICKY ODVZDUŠŇOVACÍ VENTIL
TERMOSTATICKÝ VENTIL HERZ 7217 V - PRIAMY
NEREZOVÉ PRIPOJENIE VLNOVCOVÝM POTRUBÍM
GUĽOVÝ KOHÚT- PRIAMY
2
3

3 CESTNÝ VENTIL K FWH-AT
(DODÁVKA VZT S FANCOILOM)
230V on/off
VEĽKOSŤ 1-35 = 1/2" (kvs=1,7)
VEĽKOSŤ 4-10 = 3/4" (kvs=2,8)

DETAIL NAPOJENIA PARAPETNÉHO FANCOILU:

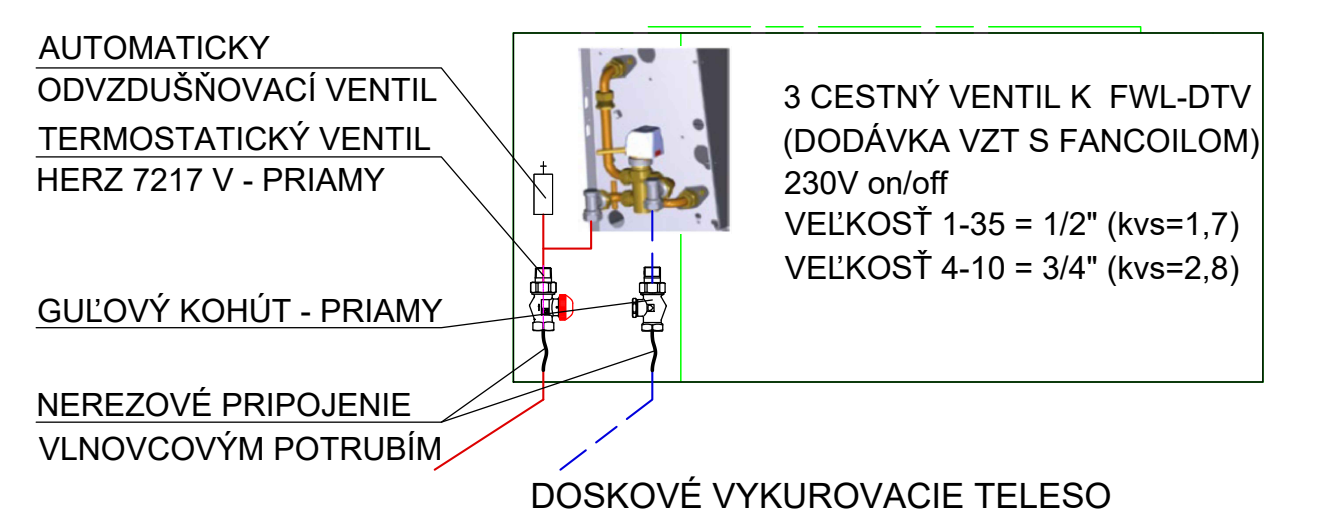
AUTOMATICKY ODVZDUŠŇOVACÍ VENTIL
TERMOSTATICKÝ VENTIL HERZ 7217 V - PRIAMY
GUĽOVÝ KOHÚT - PRIAMY
NEREZOVÉ PRIPOJENIE VLNOVCOVÝM POTRUBÍM

3 CESTNÝ VENTIL K FWL-DTV
(DODÁVKA VZT S FANCOILOM)
230V on/off
VEĽKOSŤ 1-35 = 1/2" (kvs=1,7)
VEĽKOSŤ 4-10 = 3/4" (kvs=2,8)

DOSKOVÉ VYKUROVACIE TELESO

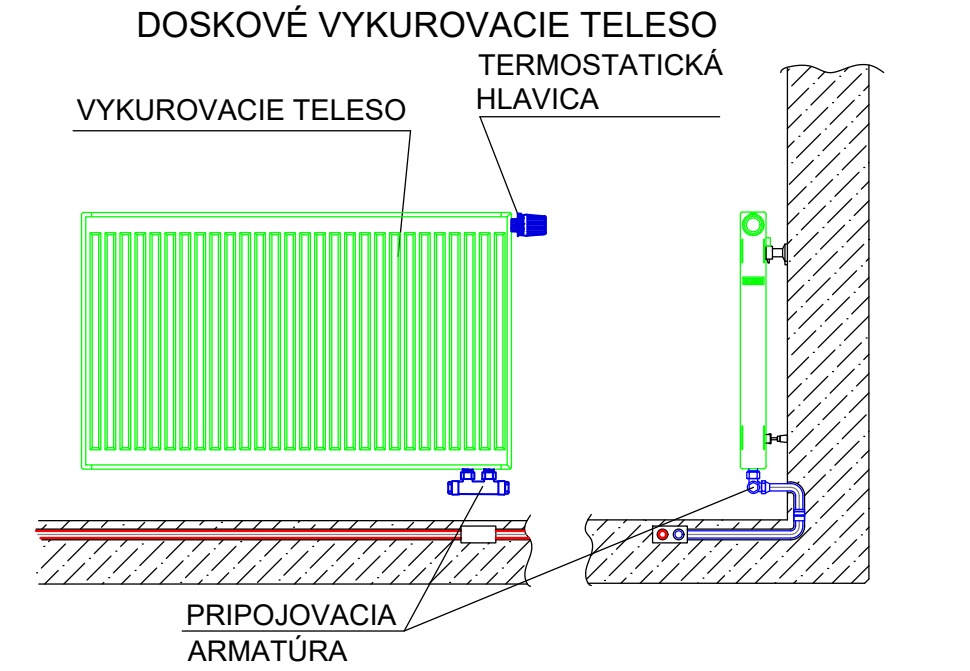
VYKUROVACIE TELESO
TERMOSTATICKÁ HLAVICA
PRIPOJOVACIA ARMATÚRA

LEGENDA OSADENIA REGULÁCIE NA PÄTE STÚPAČKY:

GK - Guľový kohút
VK - Vypúšťací kohút DN15
RTD - Regulátor tlakovej diferencie
PTV - Partnerský vyvažovací ventil Herz Stromax GM 2013 - závit Rp

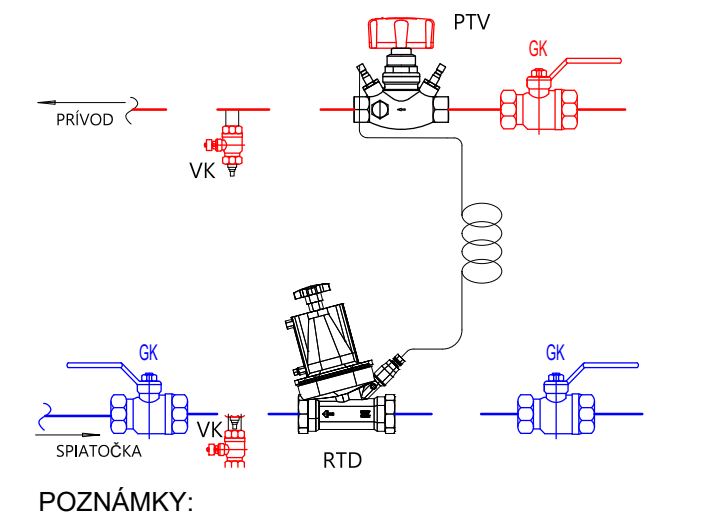
PTV
GK
PRÍVOD
VK
GK
GK
SPIATOČKA
VK
RTD

POZNÁMKY:

POTRUBIA A SPÁDOVANIE - Všetky potrubia ÚK a chladenia spádovať v smere prúdenia k najnižším bodom systému pod spádom min. 0,2 %. V najvyšších bodoch rozvodov osadiť automatické odvzdušňovacie ventily, v najnižších bodoch vypúšťacie kohúty s hadicovým nástavcom.

TEPELNÁ IZOLÁCIA POTRUBIA- Všetky potrubné rozvody tepla/chladu celoplošne a súvisle zaizolovať parotesnou elastomérnou izoláciou na báze syntetického kaučuku. Hrúbka izolácie musí byť dimenzovaná podľa priemeru potrubia v zmysle vyhlášky č. 14/2016 Z. z. (minimálne hrúbky pre vykurovanie) a zároveň musí bezpečne zabrániť vzniku kondenzátu v režime chladenia (min. hrúbka 13 mm pre DN 15–25, min. 19 mm pre DN 32 a väčšie, resp. podľa výpočtu pre dané prostredie).

FANCOILOVÉ JEDNOTKY A ZAPOJENIE - Pred montážou fancoilových jednotiek skontrolovať presný typ, výkon a orientáciu pripojenia podľa PD a dodávky stavby. Pripojenie fancoilu na pevné potrubné rozvody vyhotoviť pomocou nerezových vlnovcových potrubí z dôvodu eliminácie prenosu vibrácií a hluku do potrubnej siete. Pred každou fancoilovou jednotkou osadiť armatúry podľa PD.

SADA ČÍSLO

±0,000 = ÚROVEŇ PODLAHY 1.NP

Objednávateľ: Trenčiansky samosprávny kraj, K dolnej stanici 7282/20A, 911 01 Trenčín,
Tre
Generálny projekt
Kontroloval: Ing.
Kraj: Trenčiansky
Investor: Trenčian
Trenčian
Miesto stavby: k.ú
15
Stupeň PD:
Akcia:
Objekt: SO 20
Obsah: Schém