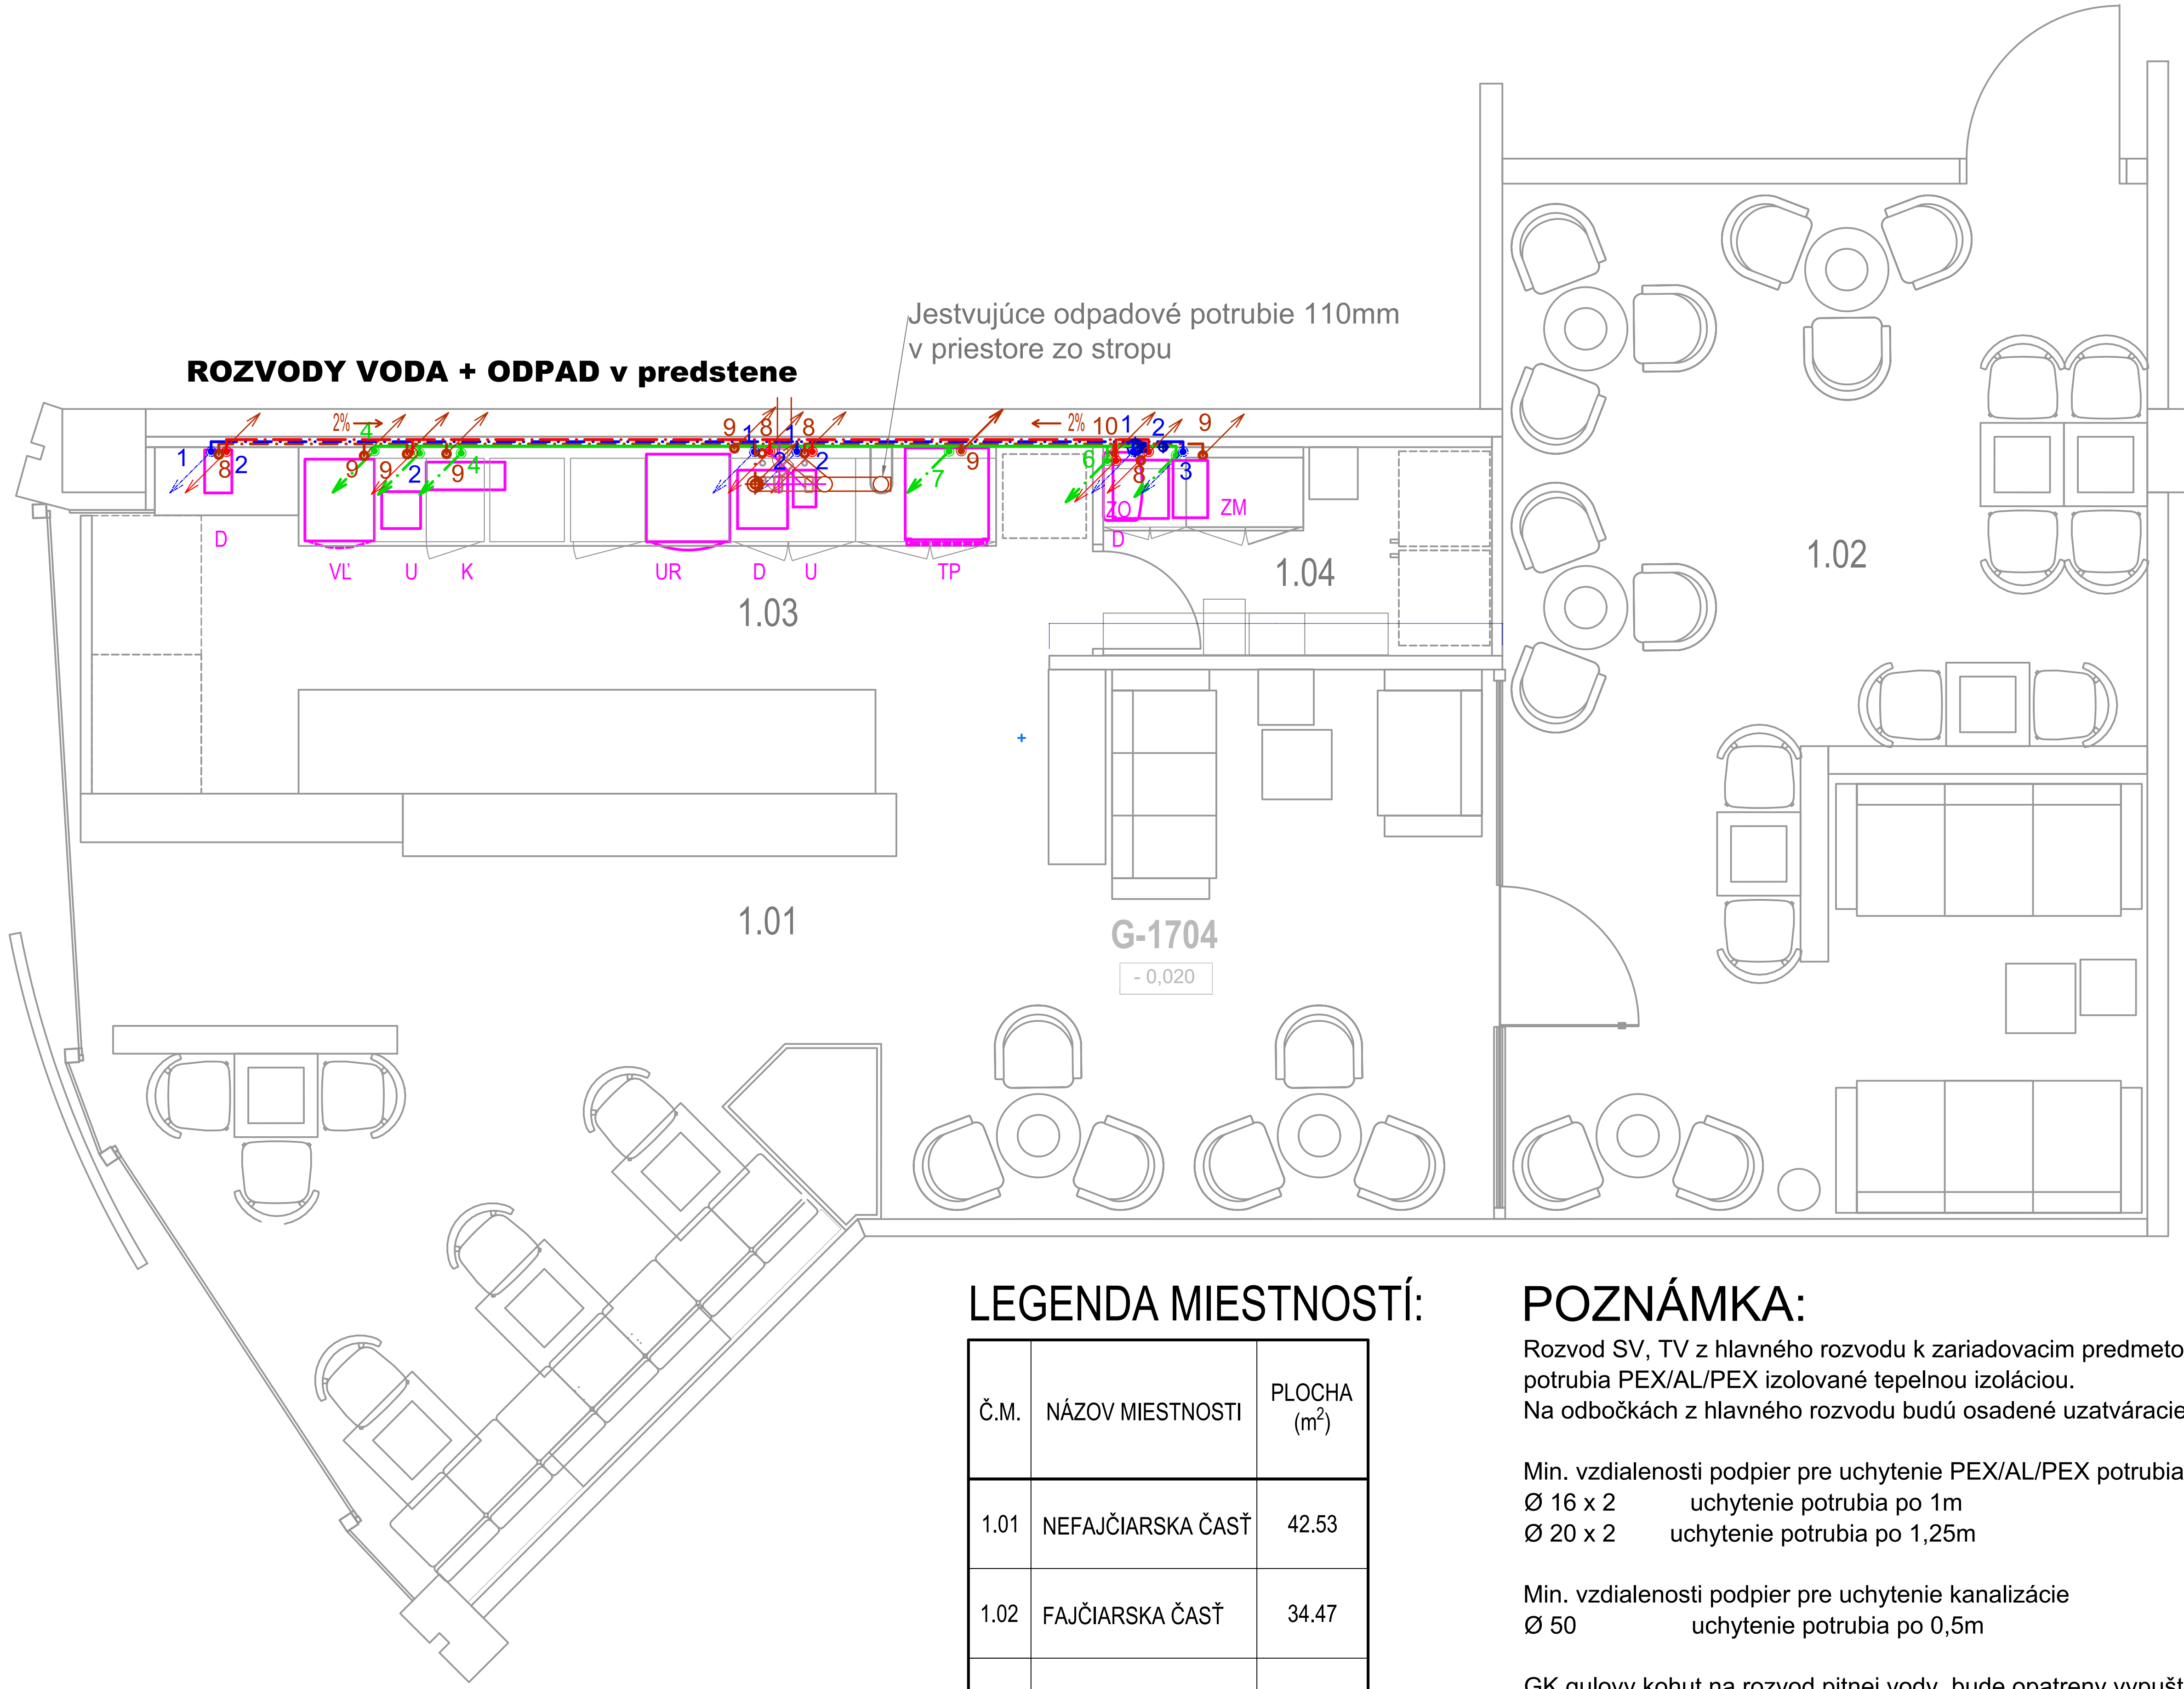

**ROZVODY VODA + ODPAD v predstene**

Jestvujúce odpadové potrubie 110mm v priestore zo stropu

# LEGENDA

| | |
|---|---|
| ─·─·─ | STUDENÁ VODA (PEX/AL/PEX) |
| ─·─·─ | TEPLÁ ÚŽITKOVÁ VODA (PEX/AL/PEX) |
| ─·─·─ | STUDENÁ VODA ZMAKČENÁ (PEX/AL/PEX) |
| ──── | PRIPOJOVACIE A ODPADOVÉ KANALIZAČNÉ POTRUBIE Z PP RÚR - HT SYSTÉM |

1- *Prívod studenej vody R1/2" pre stojankovú bateriu ukončenie ventilom R3/4" so sitkom v=650*
2- *Prívod teplej vody R1/2" pre stojankovú bateriu ukončenie ventilom R3/4" so sitkom v=650*
3- *Prívod studenej vody R1/2" pre zmäkčovač R3/4" ukončenie pračkovým ventilompre hadicu so sitkom v=650*
4- *Prívod zmäkčenej vody R1/2" pre trysku/kávovar ukončenie ventilom R3/4" pre hadicu v=750*
5- *Prívod zmäkčenej vody R1/2" pre umývačku/výrobník ľadu ukončenie pračkovým ventilom R3/4" pre hadicu a R3/8" ventil pre batériu v=650*
6- *Prívod zmäkčenej vody R1/2" pre ohrievač vody ukončenie ventilom R3/4" so sitkom v=2000*
7- *Prívod zmäkčenej vody R1/2" pre pec ukončenie ventilom R3/4" so sitkom v=850*
8- *Odpad pre drez/umývadlo pr50mm v=550*
9- *Odpad pre spotrebiče pr32/40/50mm v=viď kóta*
10 - *Odpad pre ohrievač vody pr32 ukončené prepadovým sifónom v=1950*

# LEGENDA ZNAČIEK

| | |
|---|---|
| K | KÁVOVAR + ZÁPACHOVÝ UZÁVER |
| D | KUCHYNSKÝ DREZ + ZÁPACHOVÝ UZÁVER ALEBO NAPOJIŤ NA SIFÓN DREZU |
| ZM | ZMAKČOVAČ VODY + ZÁPACHOVÝ UZÁVER |
| U | UMÝVADLO + ZÁPACHOVÝ UZÁVER |
| UR | UMÝVAČKA RIADU + ZÁPACHOVÝ UZÁVER ALEBO NAPOJIŤ NA SIFÓN DREZU |
| ZO | ELEKTRICKÝ ZÁSOBNÍKOVÝ OHRIEVAČ ELIZ EURO 120 , 2 kW (120L) + ZÁPACHOVÝ UZÁVER |
| OT | OPLACHOVACIA TRYSKA + ZÁPACHOVÝ UZÁVER |
| VĽ | VÝROBNÍK ĽADU + ZÁPACHOVÝ UZÁVER |
| TP | TEPLOVZDUŠNÁ PARNÁ PEC + ZÁPACHOVÝ UZÁVER |
| GK | GUĽOVÝ KOHÚT |
| F | FILTER MECH. NEČISTOT |
| SK | SPATNÁ KLAPKA |

# LEGENDA MIESTNOSTÍ:

| Č.M. | NÁZOV MIESTNOSTI | PLOCHA ($m^2$) |
|---|---|---|
| 1.01 | NEFAJČIARSKA ČASŤ | 42.53 |
| 1.02 | FAJČIARSKA ČASŤ | 34.47 |
| 1.03 | PRIESTOR BARU | 17.89 |
| 1.04 | SKLAD | 4.20 |
| CELKOVÁ ÚŽIT. PLOCHA | | 99.09 |

# POZNÁMKA:

Rozvod SV, TV z hlavného rozvodu k zariadovacim predmetom bude z potrubia PEX/AL/PEX izolované tepelnou izoláciou.
Na odbočkách z hlavného rozvodu budú osadené uzatváracie armatúry.

Min. vzdialenosti podpier pre uchytenie PEX/AL/PEX potrubia
Ø 16 x 2 uchytenie potrubia po 1m
Ø 20 x 2 uchytenie potrubia po 1,25m

Min. vzdialenosti podpier pre uchytenie kanalizácie
Ø 50 uchytenie potrubia po 0,5m

GK gulovy kohut na rozvod pitnej vody, bude opatreny vypuštacím

Všetky zariadenia pripojené na teplú a studenú vodu musia mať mechanický filter a uzatvárací rohový ventil.

| G-1704 | |
|---|---|
| Celková plocha: | 104,91 $m^2$ |
| Podlahová plocha: | 99,09 $m^2$ |

**0,000 = 137,50 m n.m., B.p.v.**

| | | |
|---|---|---|
| **ZODP. PROJEKTANT** | **HIP** | **VYPRACOVAL** |
| **Ing. Lu** | | |
| **STAV** | | |
| **Č. OB** | | |
| **INVES** | | |
| **NÁZO** | | |
| **PROF** | | |
| **AUTO** | | |
| **KONT**<br>**NÁJO** | | |
| **OBSA** | | |

Obsah toht