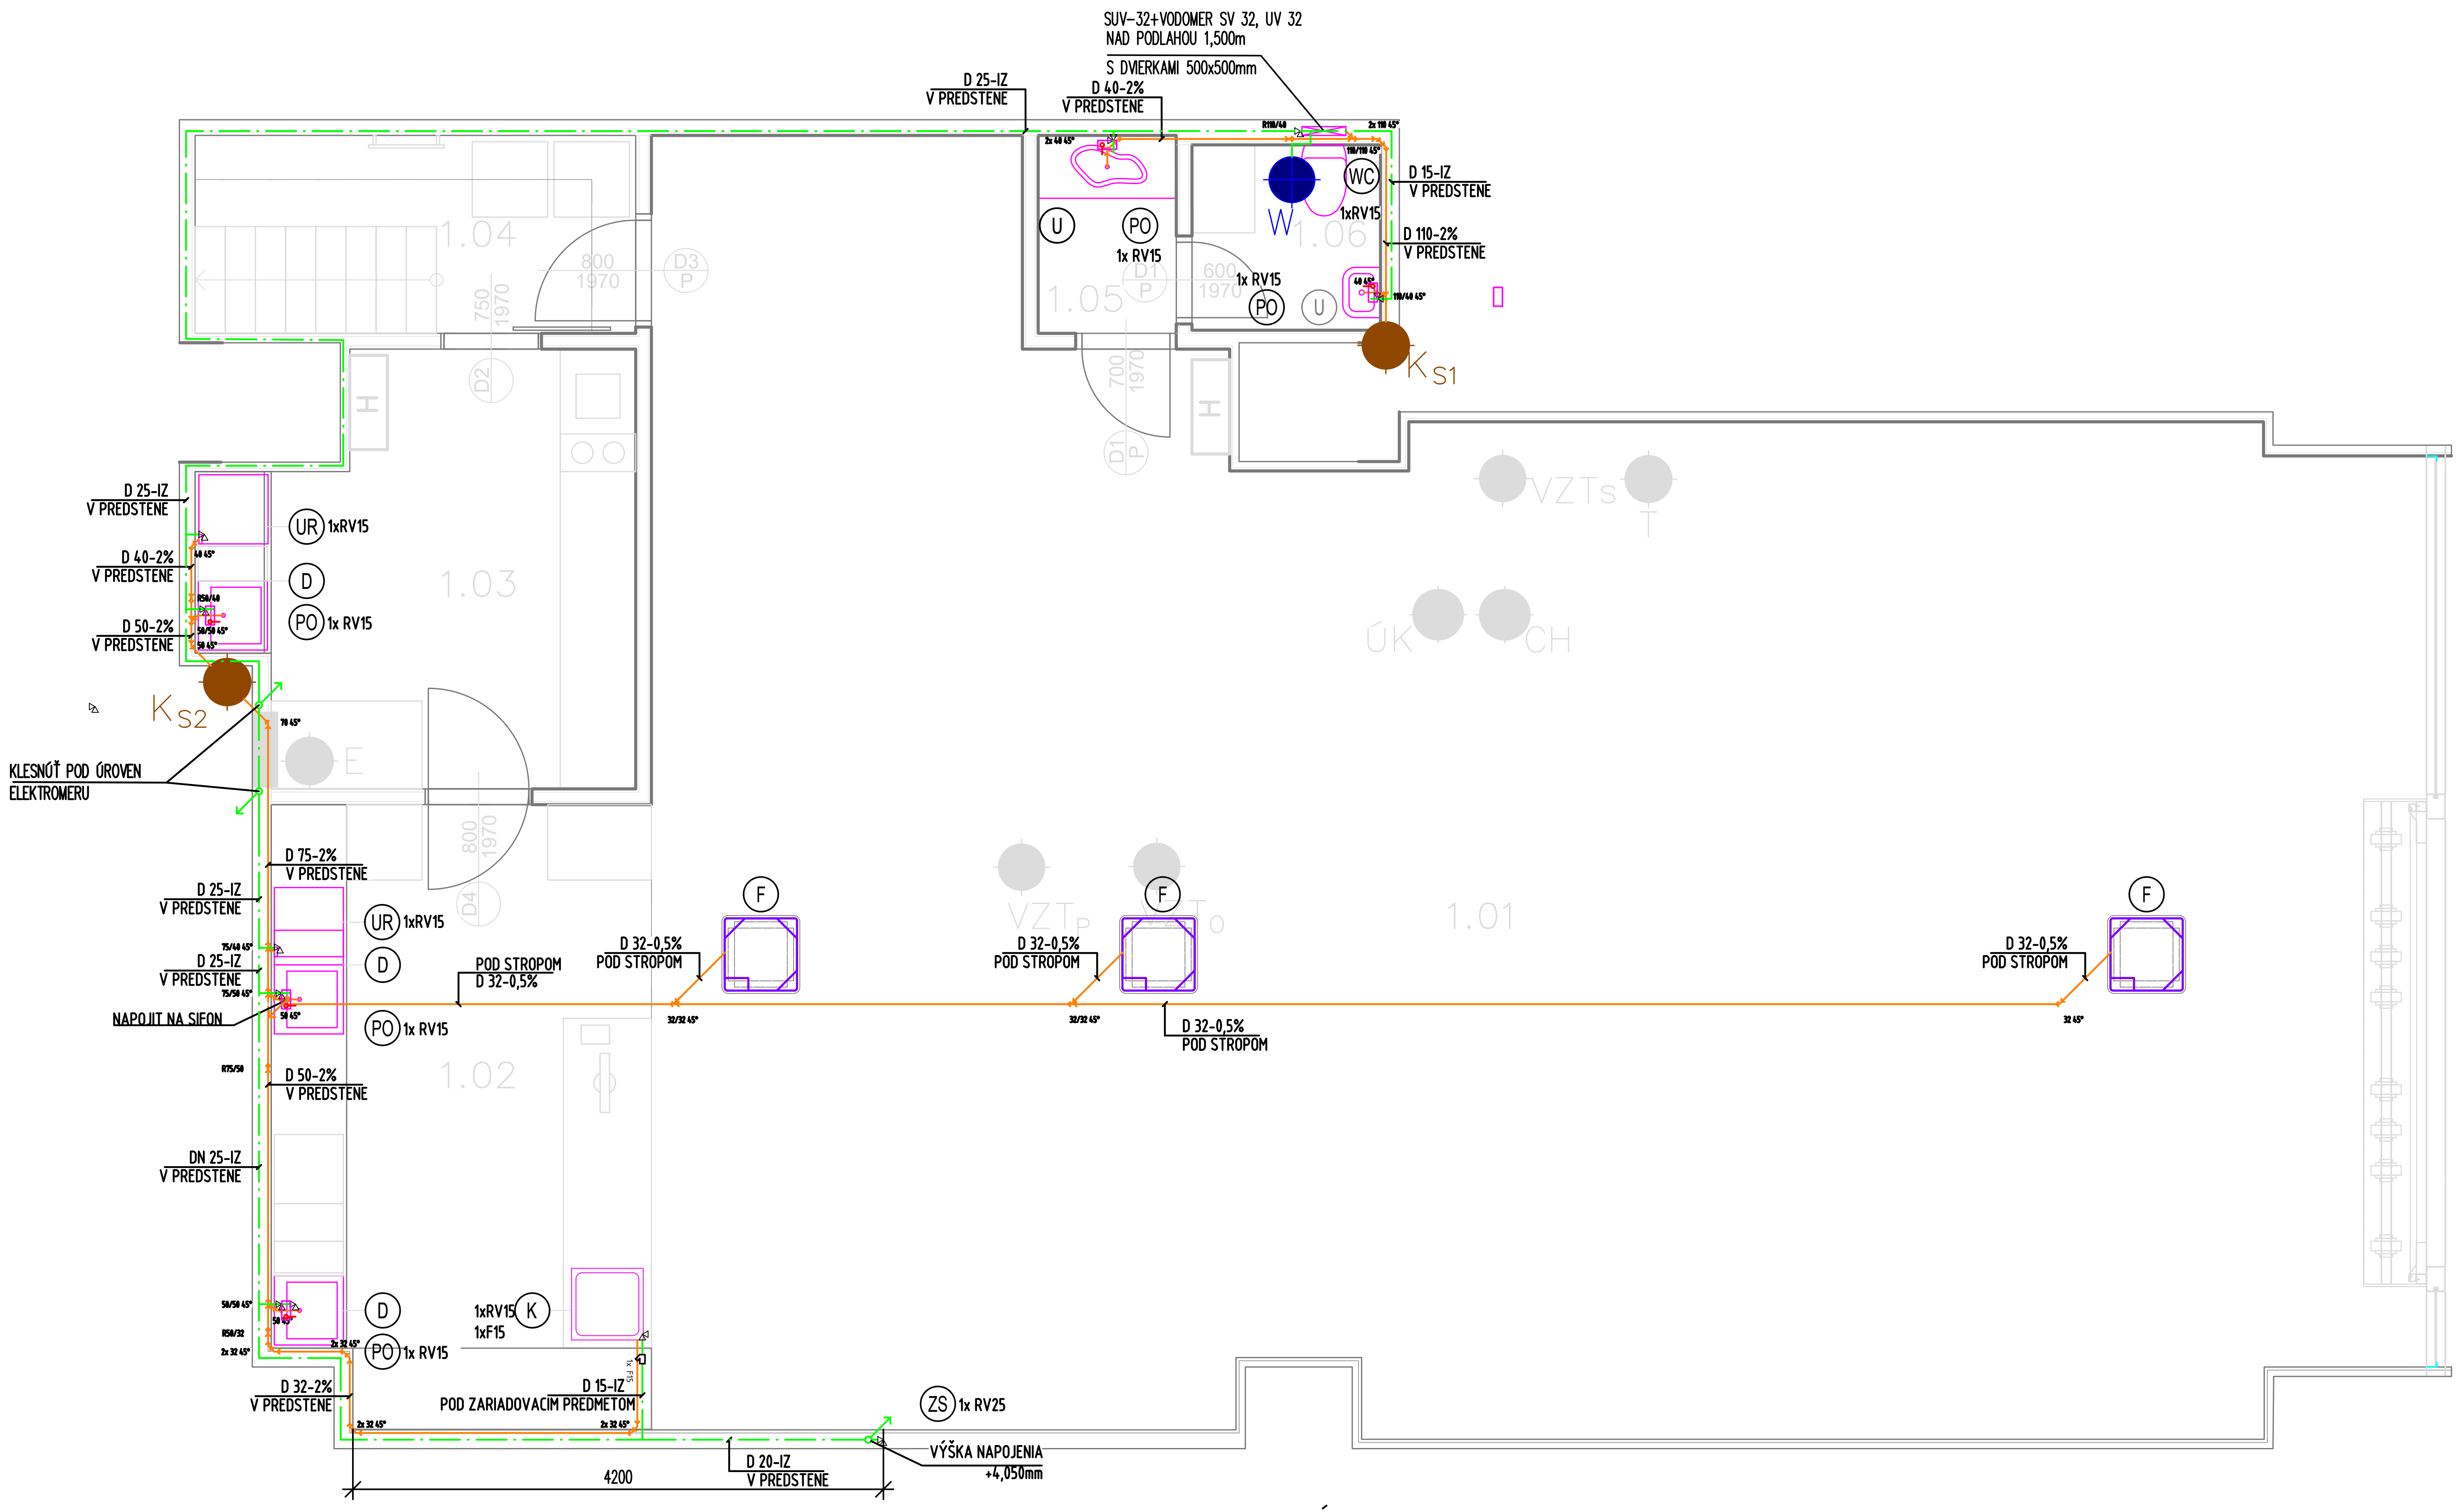

## LEGENDA MIESTNOSTÍ 02.OP.05 / SU – A 102:

| Č.M. | NÁZOV MIESTNOSTI | PLOCHA (m$^2$) | POPIS POVRCHOVÝCH ÚPRAV | | | | | |
|---|---|---|---|---|---|---|---|---|
| | | | STENY | | STROPY | | PODLAHA | |
| | | | DRUH | OBKLAD | DRUH | PODHĽAD | DRUH | SOKEL |
| 1.01 | PRIESTOR KAVIARNE | 119.60 | DVOJNÁSOBNÝ NÁTER | – | NÁSTREK EXISTUJÚCEHO PODHĽADU | – | KERAMICKÁ DLAŽBA | – |
| 1.02 | PRIESTOR BARU | 14.62 | DVOJNÁSOBNÝ NÁTER | NAD PRACOVNOU DOSKOU | | – | KERAMICKÁ DLAŽBA | KERAMICKÁ DLAŽBA V. 70 mm |
| 1.03 | KUCHYNKA | 10.41 | DVOJNÁSOBNÝ NÁTER | NAD PRACOVNOU DOSKOU | | SDK PODHĽAD S.V. 2800 mm | KERAMICKÁ DLAŽBA | KERAMICKÁ DLAŽBA V. 70 mm |
| 1.04 | SKLAD | 5.53 | DVOJNÁSOBNÝ NÁTER | – | | SDK PODHĽAD S.V. 3800 mm | KERAMICKÁ DLAŽBA | KERAMICKÁ DLAŽBA V. 70 mm |
| 1.05 | UMYVÁRKA | 1.68 | DVOJNÁSOBNÝ NÁTER | KERAMICKÝ OBKLAD V. 1,2 m | | SDK PODHĽAD S.V. 2800 mm | KERAMICKÁ DLAŽBA | KERAMICKÝ OBKLAD V. 1,2 m |
| 1.06 | TOALETA | 2.21 | DVOJNÁSOBNÝ NÁTER | KERAMICKÝ OBKLAD V. 1,2 m | | SDK PODHĽAD S.V. 2800 mm | KERAMICKÁ DLAŽBA | KERAMICKÝ OBKLAD V. 1,2 m |
| CELKOVÁ ÚŽITKOVÁ PLOCHA | | 154.05 | | | | | | |

## LEGENDA ZARIAĎOVACÍCH PREDMETOV A ARMATÚR

| | |
|---|---|
| WC | ZÁVESNÉ WC, INŠTALAČNÝ PRVOK PRE ZÁVESNÉ WC SO ZABUDOVANOU SPLACHOVACOU NÁDRŽKOU A ZÁPACHOVOU UZÁVIERKOU, S REDUKCIOU NA D 110 |
| U | UMÝVADLO, INŠTALAČNÝ PRVOK PRE UMÝVADLO, ZÁPACHOVÁ UZÁVIERKA D 40 |
| D | KUCHYNSKÝ DREZ, DREZOVÁ ZÁPACHOVÁ UZÁVIERKA D 50 |
| K | KÁVOVAR, ZÁPACHOVÁ UZÁVIERKA D 32 |
| UR | UMÝVAČKA RIADU S INTEGROVANOU PODOMIETKOVOU ZÁPACHOVOU UZÁVIERKOU D 40 |
| F | FANCOIL |
| PO | PRIETOKOVÝ OHRIEVAČ ESH 5 U-N Trend (2kW) |
| ZS | ZELENÁ STENA, VÝŠKA NAPOJENIA +4,050mm NAD PODLAHOU |

| SU – A 102 | |
|---|---|
| **Plocha nájmu (Leasing):** | **171,80 m$^2$** |
| **Podlahová plocha:** | **154,05 m$^2$** |

0,000 = 137,50 m n.m., B.p.v.

| ZODP. PROJEKTANT | HIP | VYPRACOVAL |
|---|---|---|
| Ing. Norber | | |

STAVBA
Č. OBCHOD
INVESTOR
NÁZOV OB
PROFESIA
AUTORI PR
KONTAKTN. NÁJOMCU
OBSAH VÝ

Obsah tohto výkr

## LEGENDA POTRUBIA

| | |
|---|---|
| —— | KANALIZAČNÉ ZVODOVÉ POTRUBIE HRDLOVÉ Z RÚR A TVAROVIEK S GUMOVÝM TESNENÍM<br>MATERIÁL: WAVIN AS PRE VNÚTORNÉ ROZVODY |
| —·—·— | POTRUBIE ROZVODU STUDENEJ PITNEJ VODY - IZOLOVANÝ TEPELNOU IZOLÁCIOU TUBOLIT DG HR. 9mm<br>MATERIAL: PEX/Al/PEX |
| —··— | POTRUBIE ROZVODU TEPLEJ VODY - PRIPOJOVACIA FLEXI HADICA |
| W | EXISTUJÚCI VODOVOD, BOD NAPOJENIA D32 |
| $K_{S1}$ , $K_{S2}$ | EXISTUJÚCE ODPADOVÉ POTRUBIE SPLAŠKOVEJ KANALIZÁCIE, BOD NAPOJENIA D110 |

## POZNÁMKY

Všetky kóty a rozmery PREMERAŤ NA STAVBE pred zahájením prác. Zvlášť preveriť polohy pripojenia technologických zariadení.
Montážne trasy potrubí koordinovať s profesiami VZT a EL.
Práce realizovať striktne podľa platných STN/EN noriem. Kanalizačné potrubia osadiť v požadovanom spáde (min. 2%).
Zhotoviteľ je POVINNÝ pred zakrytím vykonať tlakovú skúšku vody a skúšku tesnosti kanalizácie. O skúškach vyhotoviť PROTOKOL.
Rozvody TÚV a SV izolovať izoláciou typu TUBOLIT (alebo ekvivalentom) v normou požadovanej hrúbke.
Projektant nenesie zodpovednosť za funkčnosť systému v prípade, že montáž nebola vykonaná v súlade s touto PD, platnými normami a technologickými postupmi výrobcu.