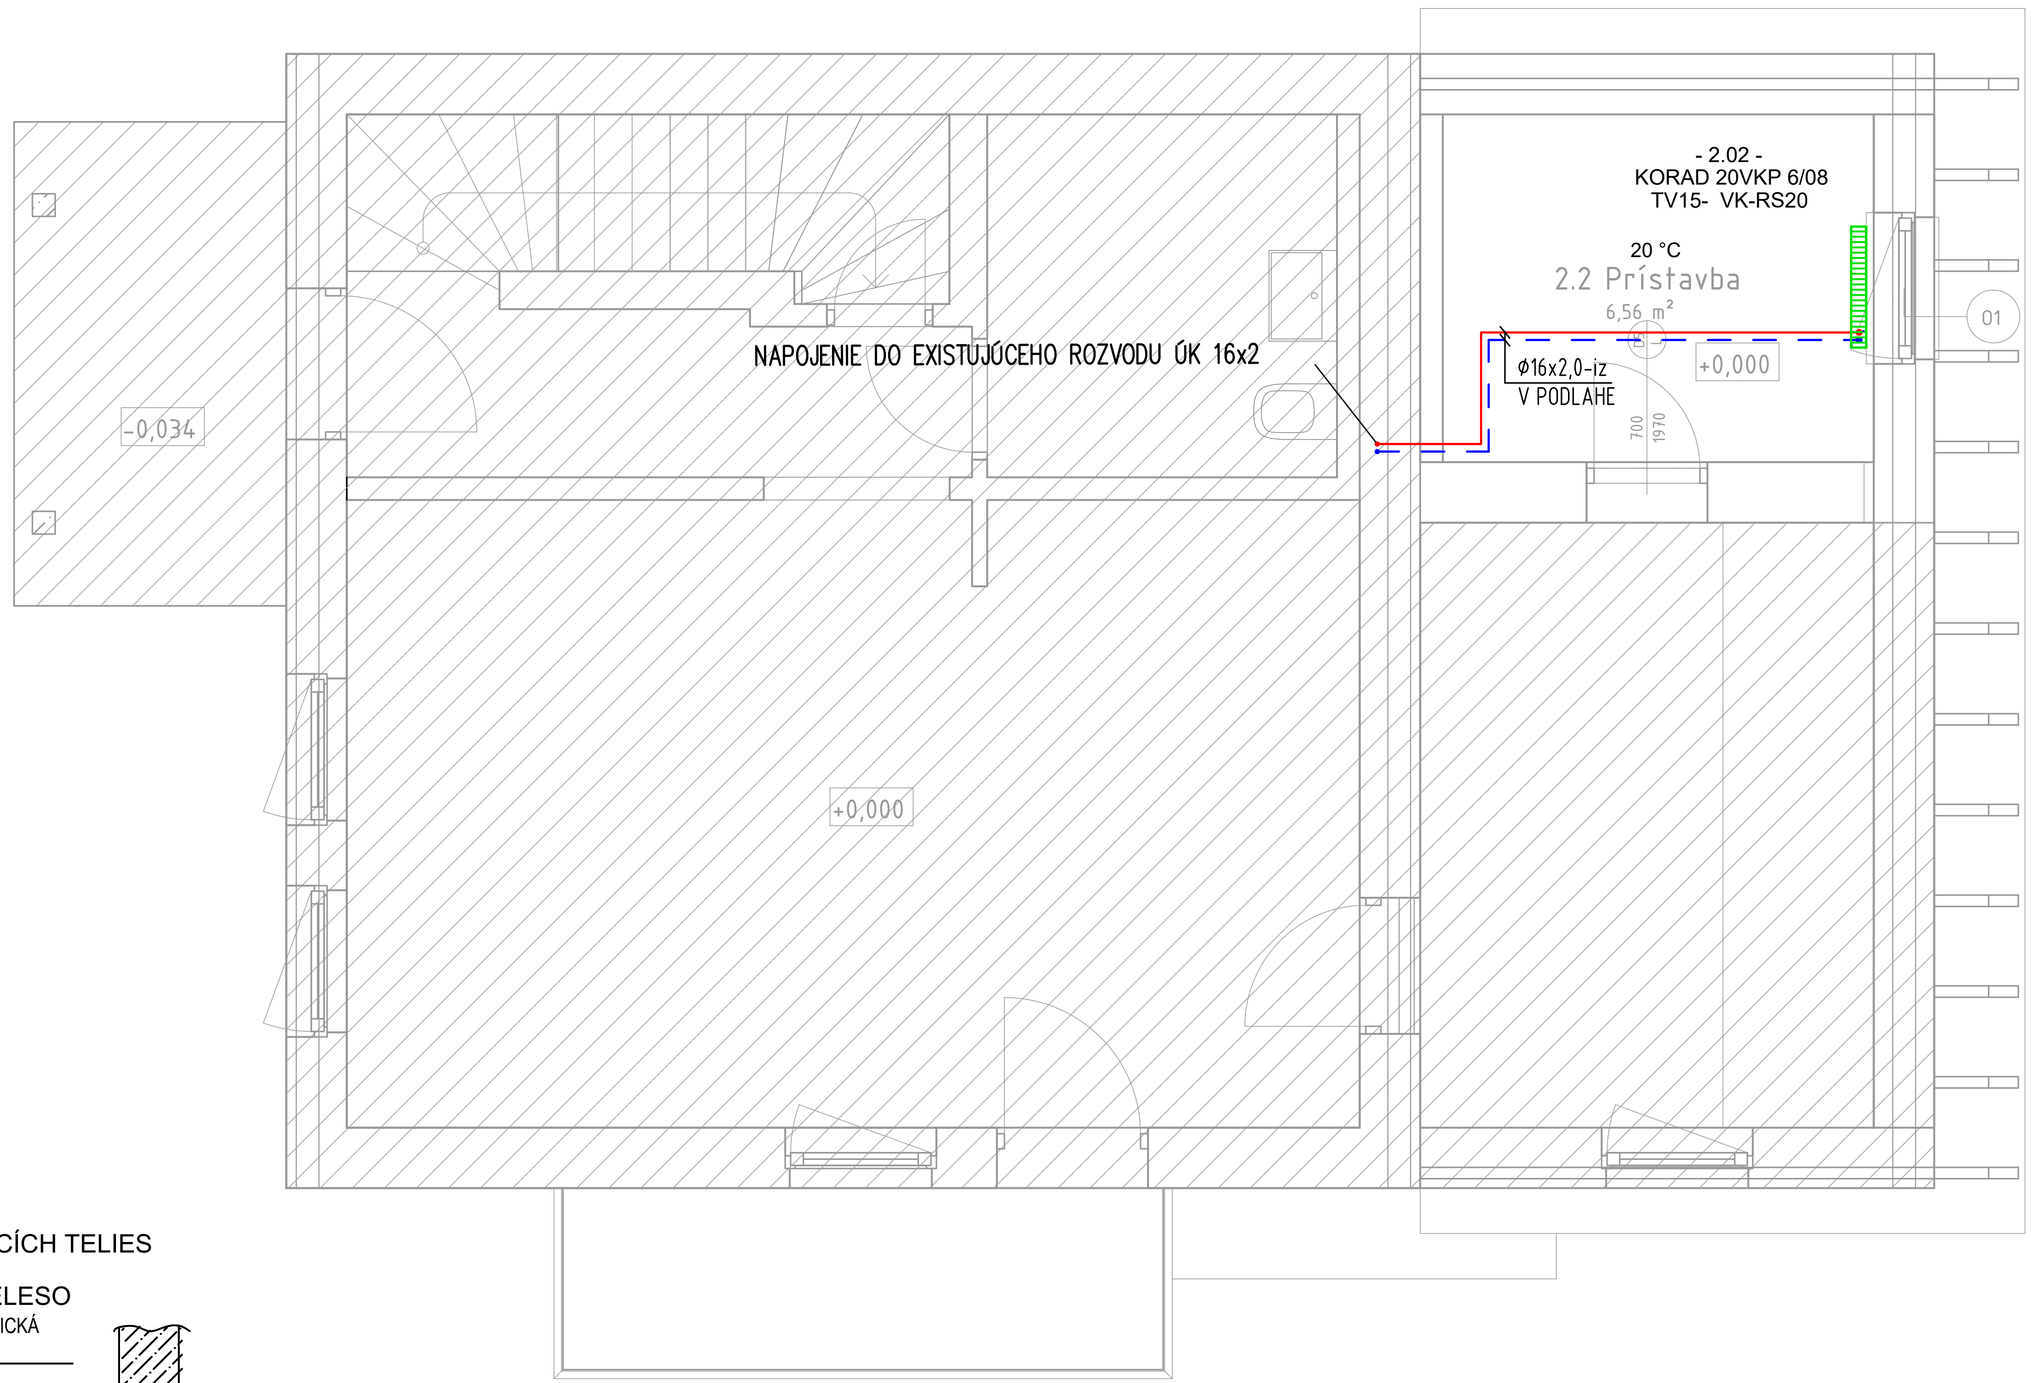

DETAIL NAPOJENIA VYKUROVACÍCH TELIES

DOSKOVÉ VYKUROVACIE TELESO

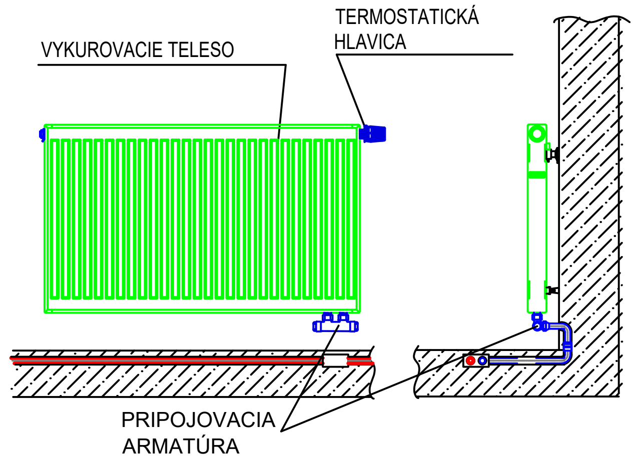

LEGENDA

🟥 / 🟦 POTRUBIE – PLASTHLINNÍKOVÁ RÚRKA PE–Xa/AL/PE napr. RAUTITAN STABIL SPÁJANÉ LISOVANÍM, IZOLOVANÉ POTRUBIE

🟩 OCE?OVÉ DOSKOVÉ VYKUROVACIE TELESO min. VÝKON 600W napr. KORAD

POZNÁMKA :

- V PRÍPADE NEJASNOSTÍ VO VÝKRESOVEJ DOKUMENTÁCIÍ KONTAKTOVAŤ ZODPOVEDNÉHO PROJEKTANTA
- VŠETKY ROZMERY STAVEBNÝCH PRÁC KONTROLOVAŤ NA MIESTE STAVBY
- PRED UVEDENÍM SYSTÉMU DO PREVÁDZKY JE POTREBNÉ VYKONAŤ DÔKLADNÝ PREPLACH SYSTÉMU S VYČISTENÍM VŠETKÝCH FILTROV NA ROZVODE
- PO NAPUSTENÍ SYSTÉMU JE POTREBNÉ VYKONAŤ JEHO ODVZDUŠNENIE
- DODÁVATEL STAVBY JE POVINNÝ REALIZOVAŤ VŠETKY PRÁCE V ZMYSLE PLATNÝCH STN EN S DODRŽANÍM TECHNOLOGICKÝCH A BEZPEČNOSTNÝCH POSTUPOV. ĎALEJ JE POVINNÝ REŠPEKTOVAŤ USTANOVENIÁ STN 730421 O PRÍSLUŠNÝCH ROZMEROVÝCH ODCHÝLKACH REALIZOVANÝCH KONŠTRUKCIÍ PROTI PROJEKTOVANÉMU STAVU. KAŽDÚ ODCHÝLKU OD PROJEKTU JE POTREBNÉ PREROKOVAŤ S GP.
- PRESTUPY INŽINIERSKYCH SIETÍ A ROZVODOV V OBJEKTE JE POTREBNÉ VYNECHAŤ PRI REALIZÁCII STAVBY.
- DOKUMENTÁCIA SLÚŽI VÝHRADNE AKO PROJEKT PRE STAVEBNÝ ZÁMER A OVERENIE PROJEKTU STAVBY

TABULKA REVIZIÍ

ČISLO REVÍZIE	DÁTUM	POPIS ZMENY	VYPRACOVAL

0,000=132,6 m n. m.

AUTOR PROJEKTU: Ing. arch. Ivor Mečiar ArtD.
H.I.P.: Ing. arch. Ivor Mečiar ArtD.
ZODP. PROJEKTANT
VYPRACOVAL:

GENERÁLNY PROJEKTANT:
Alla s.r.o.
Riazanská 70/683
831 02 Bratislava

INVESTOR:
NÁZOV PROJEKTU:
MIESTO STAVBY:
OBSAH VÝKRESU:
STAVEBNÝ OBJEKT:
ID STAVBY:
STUP
SZ
NÁZOV VÝKRESU V