LEGENDA PODLAHOVÉHO VYKUROVANIA:

Podlahové vykurovanie Rehau

Vykurovacia plocha: S=4.2 m²

Typ nášľapnej vrstvy (PX): Keramická dlažba

Typ vykurovacej rúrky: Rúrka Rautherm S 17×2,0

Rozdeľovač: Rozdeľovač Rehau HKV-D 9, skrinka rozdeľovača . 1. NP, napojenie 9 okruhov (tp=45 °C)

Systém uchytenia: Varionova – typ prichytenia potrubia pre podlahové kúrenie

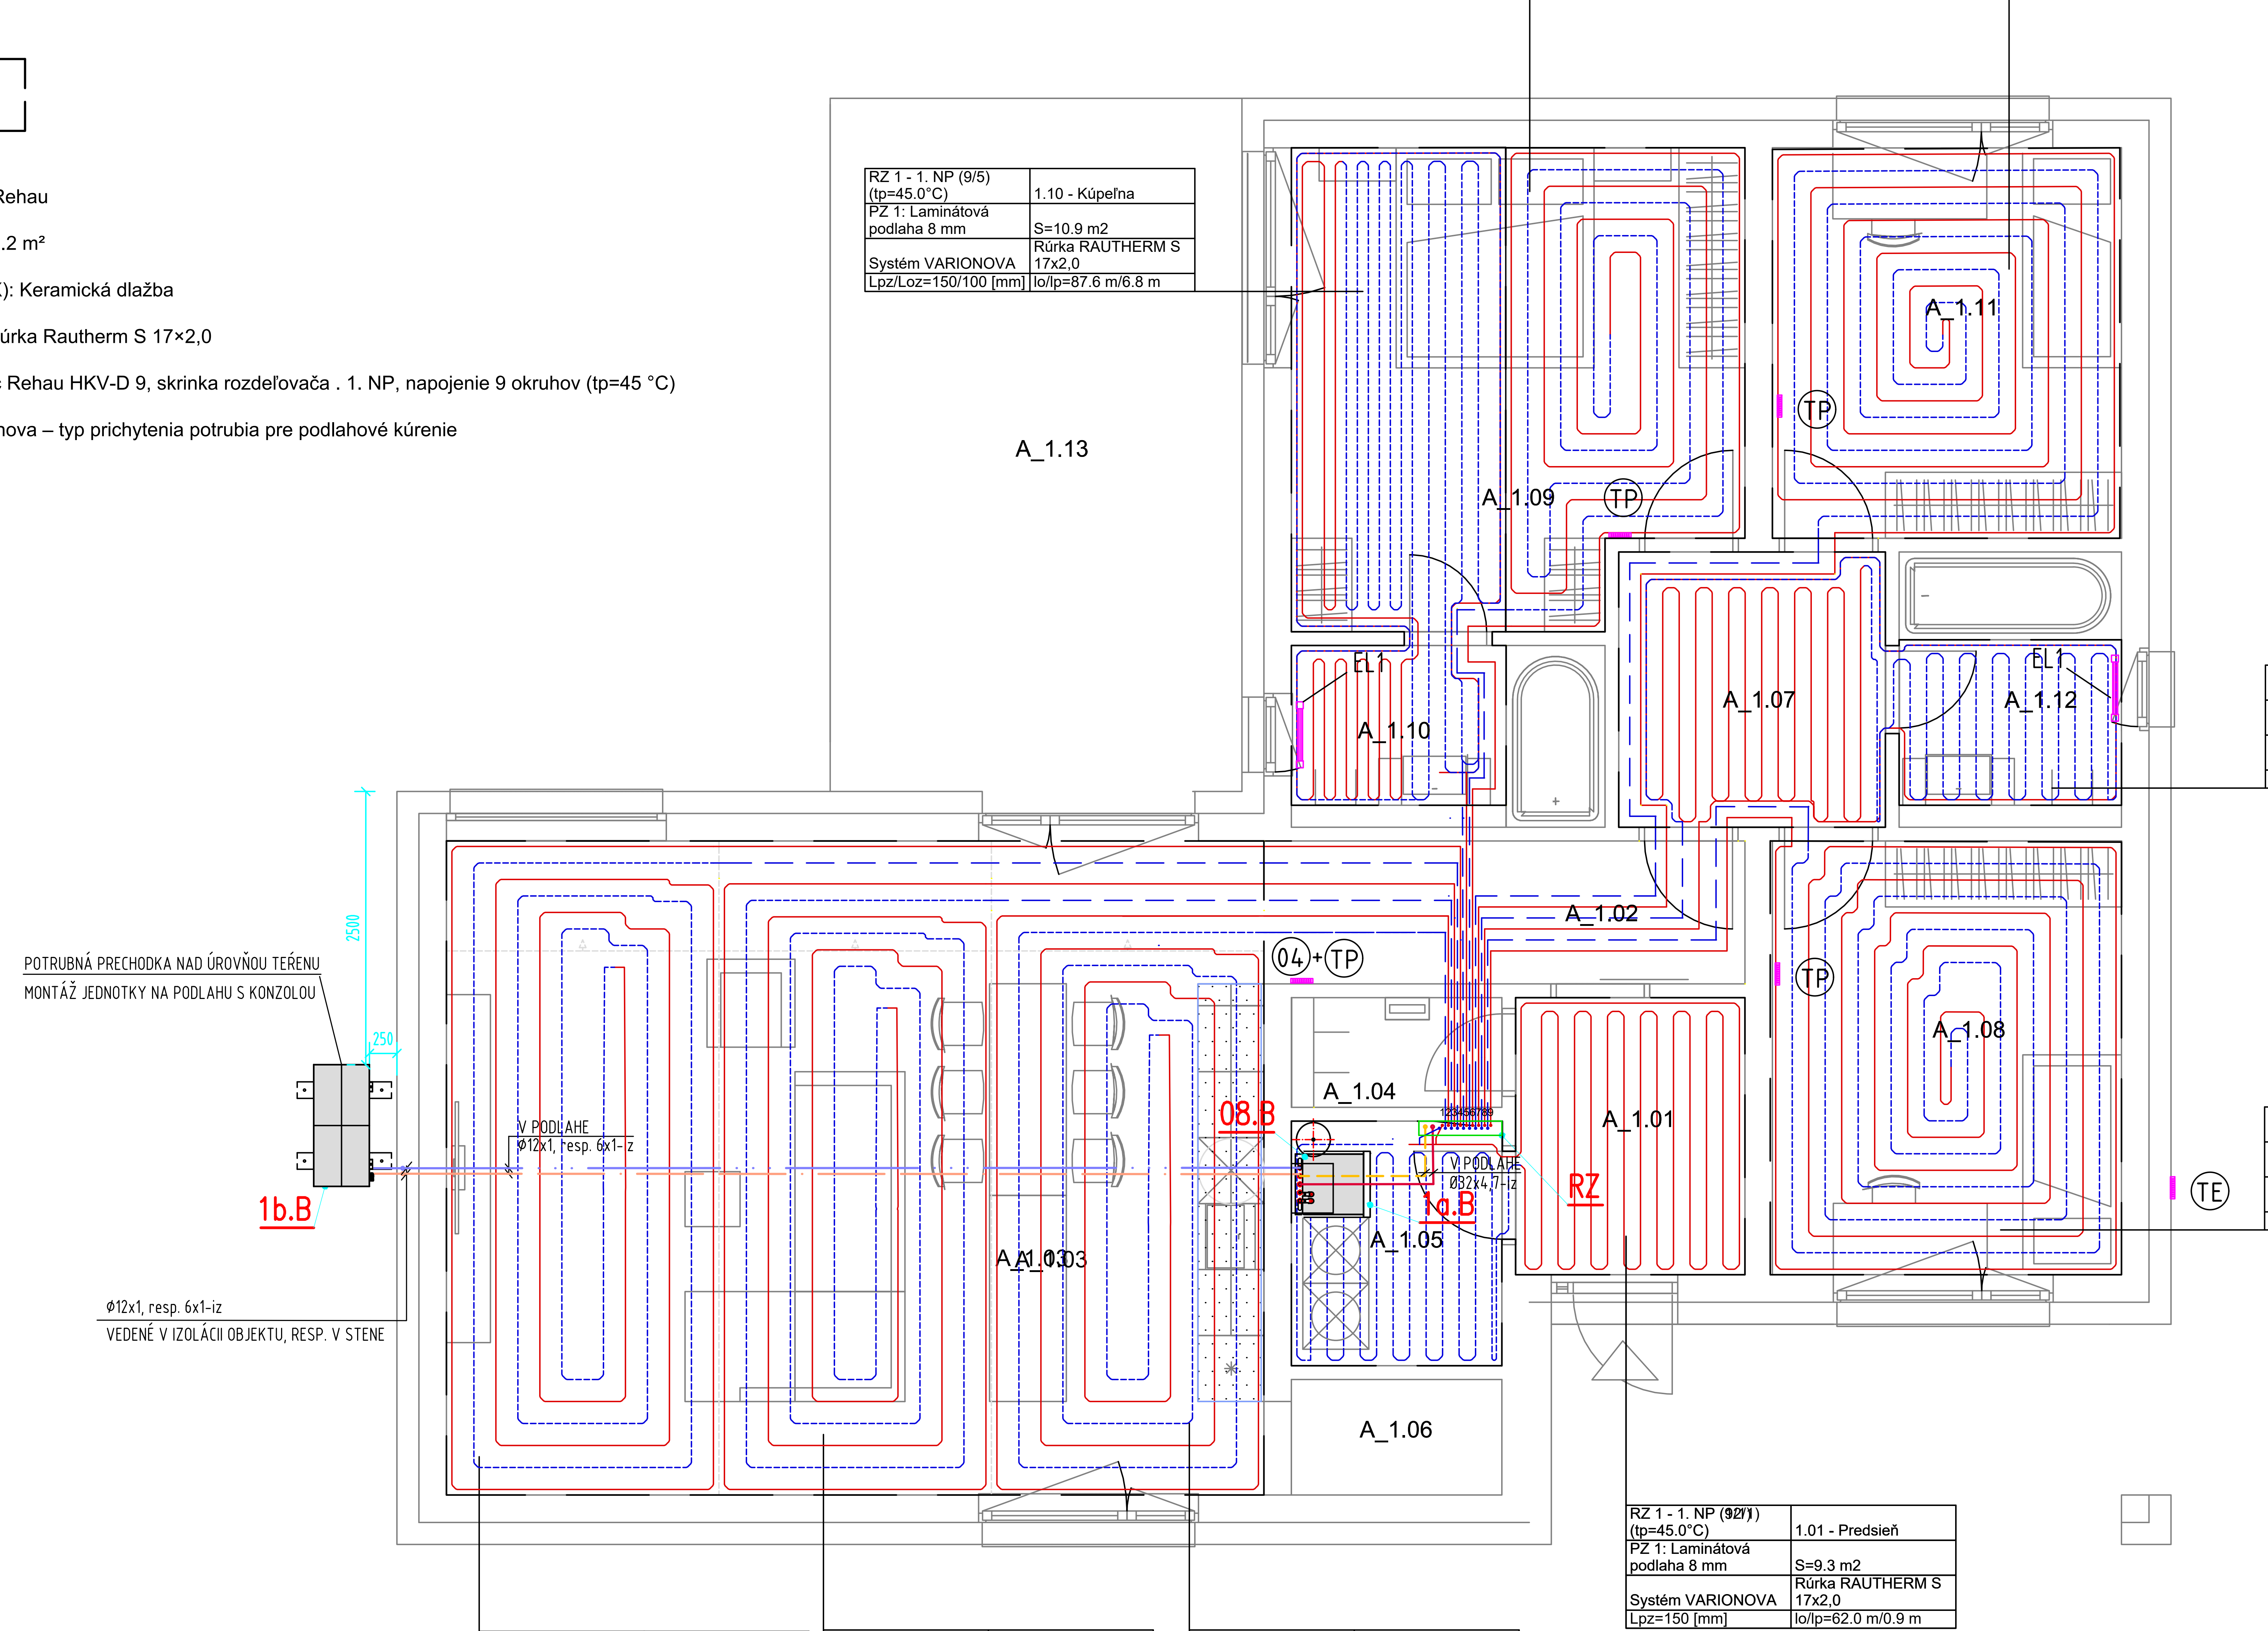

RZ 1 - 1. NP (12/6) (tp=45.0°C)	1.09 - Spálňa
PZ 1: Laminátová podlaha 8 mm	S=8.5 m2
Systém VARIONOVA	Rúrka RAUTHERM S 17x2,0
Lpz=150 [mm]	lo/lp=56.6 m/12.0 m

RZ 1 - 1. NP (12/7) (tp=45.0°C)	1.11 - Izba
PZ 1: Laminátová podlaha 8 mm	S=11.2 m2
Systém VARIONOVA	Rúrka RAUTHERM S 17x2,0
Lpz=150 [mm]	lo/lp=74.7 m/19.1 m

RZ 1 - 1. NP (9/5) (tp=45.0°C)	1.10 - Kúpeľna
PZ 1: Laminátová podlaha 8 mm	S=10.9 m2
Systém VARIONOVA	Rúrka RAUTHERM S 17x2,0
Lpz/Loz=150/100 [mm]	lo/lp=87.6 m/6.8 m

RZ 1 - 1. NP (9/8) (tp=45.0°C)	1.12 - Kúpeľňa
PZ 1: Laminátová podlaha 8 mm	S=8.1 m2
Systém VARIONOVA	Rúrka RAUTHERM S 17x2,0
Lpz=150 [mm]	lo/lp=54.3 m/10.3 m

RZ 1 - 1. NP (12/9) (tp=45.0°C)	1.08 - Izba
PZ 1: Laminátová podlaha 8 mm	S=12.6 m2
Systém VARIONOVA	Rúrka RAUTHERM S 17x2,0
Lpz=150 [mm]	lo/lp=83.9 m/13.0 m

RZ 1 - 1. NP (9/1) (12/1) (tp=45.0°C)	1.01 - Predsieň
PZ 1: Laminátová podlaha 8 mm	S=9.3 m2
Systém VARIONOVA	Rúrka RAUTHERM S 17x2,0
Lpz=150 [mm]	lo/lp=62.0 m/0.9 m

RZ 1 - 1. NP (11/4) (tp=45.0°C)	1.03 - Obývačka
PZ 3: Laminátová podlaha 8 mm	S=14.7 m2
Systém VARIONOVA	Rúrka RAUTHERM S 17x2,0
Lpz/Loz=200/150 [mm]	lo/lp=77.8 m/18.6 m

RZ 1 - 1. NP (11/3) (tp=45.0°C)	1.03 - Obývačka
PZ 2: Laminátová podlaha 8 mm	S=13.9 m2
Systém VARIONOVA	Rúrka RAUTHERM S 17x2,0
Lpz/Loz=200/150 [mm]	lo/lp=72.2 m/12.8 m

RZ 1 - 1. NP (11/2) (tp=45.0°C)	1.03 - Obývačka
PZ 1: Laminátová podlaha 8 mm	S=13.2 m2
Systém VARIONOVA	Rúrka RAUTHERM S 17x2,0
Lpz/Loz=200/150 [mm]	lo/lp=67.4 m/7.2 m

- 1.12 -	
Kúpeľňa	
5.0 m2	13.1 m3
24 °C	284 W

- 1.11 -	
Izba	
11.2 m2	29.1 m3
22 °C	538 W

- 1.10 -	
Kúpeľna	
4.7 m2	12.2 m3
24 °C	274 W

- 1.09 -	
Spálňa	
17.2 m2	44.7 m3
22 °C	782 W

- 1.08 -	
Izba	
12.6 m2	32.7 m3
22 °C	609 W

- 1.05 -	
Technická	
4.3 m2	11.1 m3
20 °C	149 W

- 1.03 -	
Obývačka	
44.3 m2	158.1 m3
22 °C	2307 W

- 1.01 -	
Predsieň	
5.3 m2	13.6 m3
20 °C	231 W

LEGENDA POTRUBÍ:

🟥 / 🟦	Plasthliníkové potrubie napr. Rautherm S 17×2,0 Rehau pre podlahové vykurovanie, teplotný spád 45/35 °C, vedené v podlahe.
🟥 / 🟨	Plasthliníkové potrubie materiál: PE-Xa/AL/PE napr. Rautitan Stabil, zaizolované potrubie, teplotný spád 45/35 °C.
🟦 / 🟧	Medené potrubie primárneho okruhu tepelného čerpadla: Cu ϕ12×1, 6×1-iz.

LEGENDA ZARIADENÍ:

1A	Tepelné čerpadlo (vnútorná jednotka) napr.: Viessmann Vitocal 222-S (AWBT-M-E-AC 221.E06). Integrovaný zásobník na TV (220 l), napájanie 230V/50Hz. Hmotnosť: 168 kg.
1B	Tepelné čerpadlo (vonkajšia jednotka) napr.: Vitocal 222-S (vzduch-voda). Výkon (A7/W35): 3,5 – 7,5 kW, COP 4,7. Chladivo R410A.
4	Ovládanie: Bezdrôtový diaľový ovládač napr. Vitotrol 300-E.
8	Expanzná nádoba napr: Viessmann N25 (objem 25 l, max. tlak 3 bar).
TP	Izbový regulátor napr.: REHAU Nea Smart 2.0 (meranie teploty).
TE	Snímač teploty exteriéru.
EL1	Elektrické vykurovacie teleso (rebrík) do kúpeľne, min. výkon 300 W (konkrétny model podľa výberu architekta).
R-Z	Zostava rozdeľovača podlahového vykurovania (teplotný spád 45/35 °C)

9-okruhový rozdeľovač napr. REHAU HKV-D 9, skrinka osadená na stenu.
Ďiaľkové ovládanie termostatov napr. REHAU NEA (230V)

4 ks priestrový termostat napr. REHAU NEA (230V)

12 ks elektrický servo-pohon (230V)

POZNÁMKY :

- V prípade akýchkoľvek nejasností v projektovej dokumentácii je nutné kontaktovať zodpovedného projektanta.

- Všetky stavebné rozmery a prestupy je potrebné overiť priamo na mieste realizácie.

- Pred samotným spustením systému do prevádzky sa musí vykonať dôkladný preplach rozvodov a vyčistenie všetkých inštalovaných filtrov.

- Po napustení vykurovacej sústavy médiom je nevyhnutné zabezpečiť jej postupné odvzdušnenie.

- Zhotoviteľ je povinný postupovať v súlade s platnými normami STN EN a dodržiavať technologické aj bezpečnostné predpisy. Zároveň musí rešpektovať ustanovenia STN 730421 o rozmerových odchýlkach. Každú zmenu oproti projektu je nutné vopred skonzultovať s HIP.

- Otvory pre prestupy inžinierskych sietí a potrubných rozvodov v objekte je potrebné pripraviť počas realizácie hrubej stavby.

- Táto dokumentácia nenahrádza realizačnú dokumentáciu stavby!

-Výšková úroveň ±0,000 v projekte zodpovedá úrovni finálnej nášľapnej vrstvy podlahy.

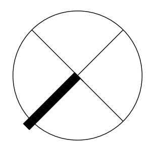

VONKAJŠIA VÝPOČTOVÁ TEPLOTA -11°C

TABUĽKA REVÍZIÍ

ČÍSLO REVÍZIE	DÁTUM	POPIS ZMENY	VYPRACOVAL

0,000=+0,300 nad korunou komunikácie m n. m.

AUTOR PROJEKTU:	Ing. arch Pavel Vojtek, Ing. arch Ivor Mečiar, ArtD.	GENERÁLNY PROJEKTANT: **Alla s.r.o.** Riazanská 70/683 831 02 Bratislava
H.I.P.:	Ing. arch Ivor Mečiar, ArtD.	
ZODP. PROJEKTANT:		
VYPRACOVAL:		

INVESTOR:	
NÁZOV PROJEKTU:	
MIESTO STAVBY:	
OBSAH VÝKRESU:	
STAVEBNÝ OBJEKT:	
ID STAVBY: --	STUPE P
NÁZOV VÝKRESU V ELEKTR	