RZ 1 - 1. NP (7)

ROZDEĽOVACIA STANICA PRE PODLAHOVÉ VYKUROVANIE 45/35°C
NAPR. FY. REHAU HKV-D 7, SKRINKA ROZDEĽOVAČA NA STENU 130/805 (805x730x130mm)
REGULAČNÝ ROZVÁDZAČ REHAU NEA (230V) (1ks)
PRIESTOROVÝ TERMOSTAT REHAU NEA (230V) (2ks)
ELEKTRICKÝ SERVOPOHON REHAU (230V) (7ks)

RZ 1 - 1. NP (7/7) (tp=45.0°C)	1.08 - Kupelna
PZ 1: Keramická dlažba 10 mm	VYK: PZ:33.4°C
Systém VARIONOVA	Rúrka RAUTHERM S 17x2,0
lo/lp=37.2 m/11.8 m	S=3.7 m2
Lpz=100 [mm]	VYK: 0.6 l/min

RZ 1 - 1. NP (7/1) (tp=45.0°C)	1.10 - Technicka miestnost
PZ 1: Keramická dlažba 10 mm	VYK: PZ:31.7°C
Systém VARIONOVA	Rúrka RAUTHERM S 17x2,0
lo/lp=19.4 m/13.9 m	S=1.9 m2
Lpz=100 [mm]	VYK: 0.4 l/min

RZ 1 - 1. NP (7/2) (tp=45.0°C)	1.12 - Obývačka + jedalen
PZ 1: PVC 5 mm	VYK: PZ:28.0°C [OZ:28.6°C]
Systém VARIONOVA	Rúrka RAUTHERM S 17x2,0
lo/lp=82.1 m/18.7 m	S=10.5 m2
Lpz/Loz=150/100 [mm]	VYK: 1.2 l/min

RZ 1 - 1. NP (7/6) (tp=45.0°C)	1.07 - Spálňa
PZ 1: PVC 5 mm	VYK: PZ:29.4°C
Systém VARIONOVA	Rúrka RAUTHERM S 17x2,0
lo/lp=74.3 m/7.7 m	S=11.2 m2
Lpz=150 [mm]	VYK: 1.0 l/min

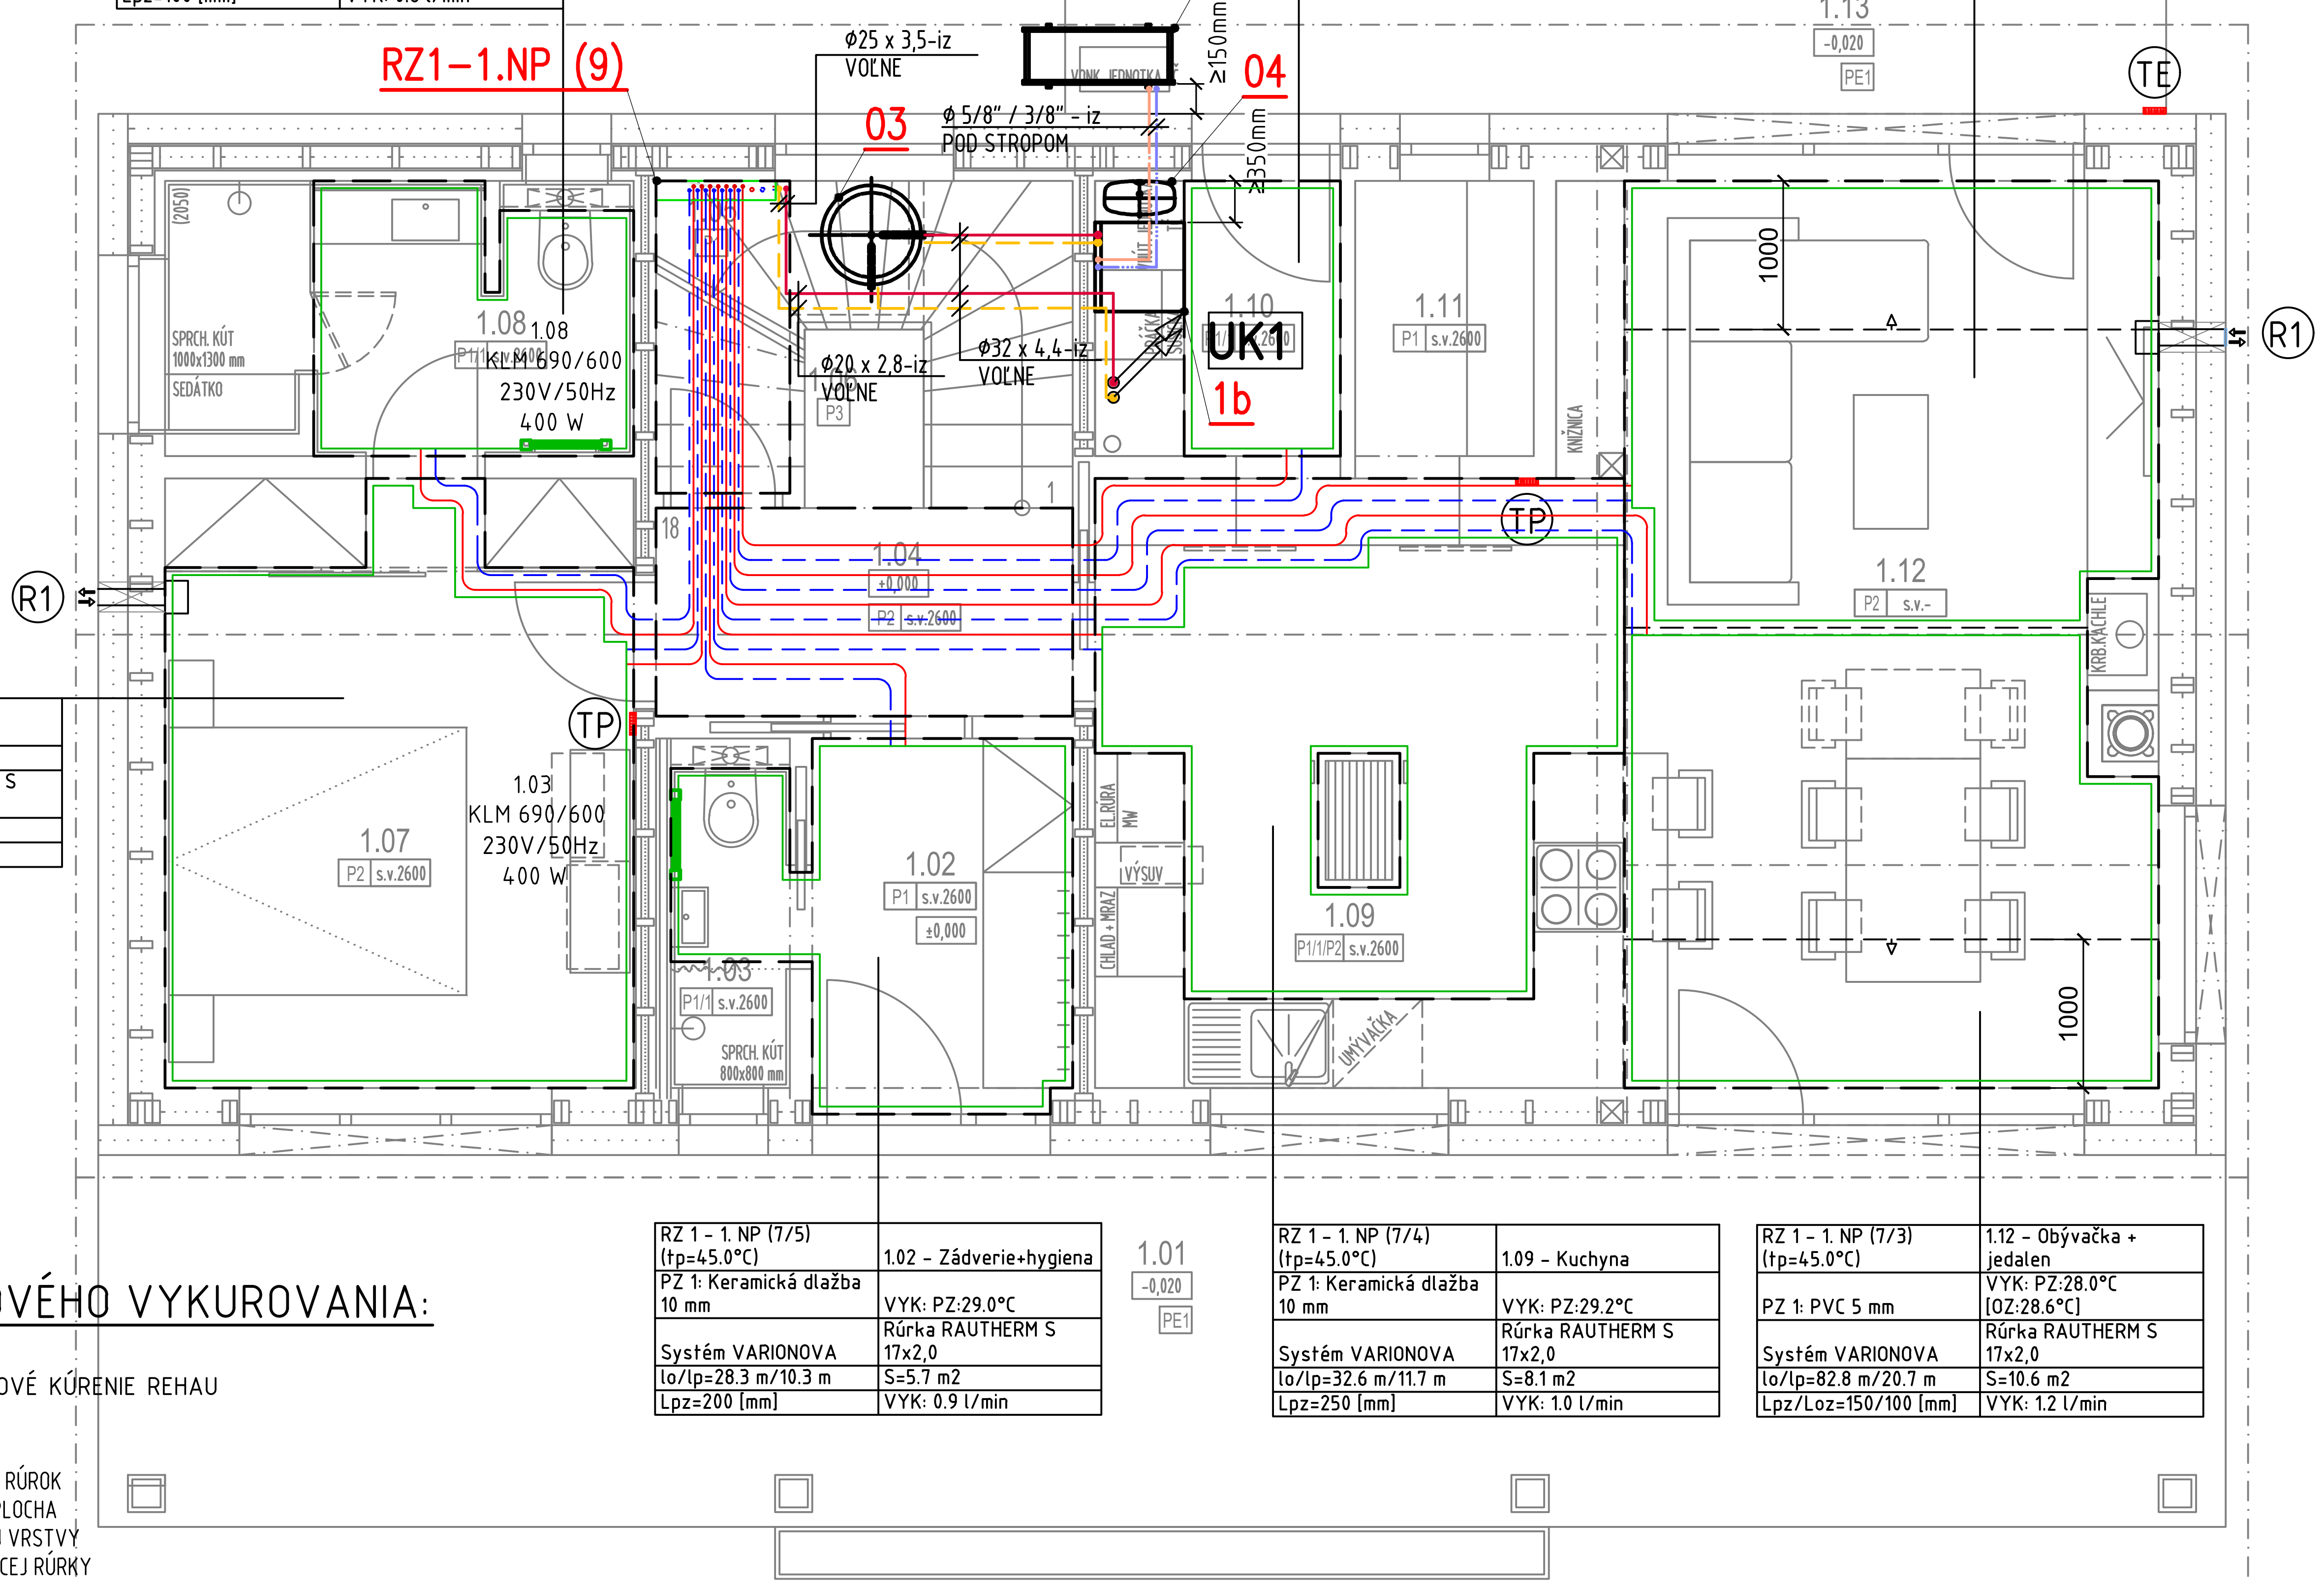
RZ1-1.NP (9)
Φ25 x 3,5-iz
VOĽNE
1a
≥150mm
04
03
Φ 5/8" / 3/8" - iz
POD STROPOM
≥350mm
VONK. JEDNOTKA
1.13
-0,020
PE1
TE
(2050)
SPRCH. KÚT
1000x1300 mm
SEDÁTKO
1.08
P1/1 s.v.2600
1.08
KLM 690/600
230V/50Hz
400 W
Φ20 x 2,8-iz
VOĽNE
P3
Φ32 x 4,4-iz
VOĽNE
1.10
UK1
1b
1.11
P1 s.v.2600
KNIŽNICA
1000
R1
1.12
P2 s.v.-
KRB.KACHLE
1000
18
1
1.04
±0,000
P2 s.v.2600
TP
R1
TP
1.07
P2 s.v.2600
1.03
KLM 690/600
230V/50Hz
400 W
1.03
P1/1 s.v.2600
SPRCH. KÚT
800x800 mm
1.02
P1 s.v.2600
±0,000
EL.RÚRA
MW
VÝSUV
CHLAD.+ MRAZ.
1.09
P1/1/P2 s.v.2600
UMÝVAČKA
1.01
-0,020
PE1

RZ 1 - 1. NP (7/5) (tp=45.0°C)	1.02 - Zádverie+hygiena
PZ 1: Keramická dlažba 10 mm	VYK: PZ:29.0°C
Systém VARIONOVA	Rúrka RAUTHERM S 17x2,0
lo/lp=28.3 m/10.3 m	S=5.7 m2
Lpz=200 [mm]	VYK: 0.9 l/min

RZ 1 - 1. NP (7/4) (tp=45.0°C)	1.09 - Kuchyna
PZ 1: Keramická dlažba 10 mm	VYK: PZ:29.2°C
Systém VARIONOVA	Rúrka RAUTHERM S 17x2,0
lo/lp=32.6 m/11.7 m	S=8.1 m2
Lpz=250 [mm]	VYK: 1.0 l/min

RZ 1 - 1. NP (7/3) (tp=45.0°C)	1.12 - Obývačka + jedalen
PZ 1: PVC 5 mm	VYK: PZ:28.0°C [OZ:28.6°C]
Systém VARIONOVA	Rúrka RAUTHERM S 17x2,0
lo/lp=82.8 m/20.7 m	S=10.6 m2
Lpz/Loz=150/100 [mm]	VYK: 1.2 l/min

- 1.02 -	- 1.03 -	- 1.04 -	- 1.07 -	- 1.08 -	- 1.09 -	- 1.10 -	- 1.12 -
Zádverie	WC + Sprcha	Chodba	Spálňa	Kupelna	Kuchyna	Technicka miestnost	Obývačka + jedalen
4.1 m2 10.7 m3	2.1 m2 5.5 m3	4.9 m2 12.7 m3	12.9 m2 33.6 m3	5.6 m2 15.7 m3	15.5 m2 40.2 m3	3.1 m2 7.9 m3	21.8 m2 56.6 m3
20 °C 234 W	24 °C 108 W	20 °C 82 W	24 °C 596 W	24 °C 334 W	22 °C 524 W	20 °C 206 W	22 °C 1585 W

LEGENDA PODLAHOVÉHO VYKUROVANIA:

PODLAHOVÉ KÚRENIE REHAU

Lpz=100 [mm]	ROZOSTUP VYK. RÚROK
S=8,6 m2	VYKUROVACIA PLOCHA
PZ: Keramická dlažba	TYP NÁŠLAPNEJ VRSTVY
Rúrka RAUTHERM S 17x2,0	TYP VYKUROVACEJ RÚRKY
Nast.=0,63 (48 kg/h)	NASTAVENIE REG. OKRUHU(PRIETOK)
lo/lp=12.7 m/1.6 m	Dlžka okruhu / dlžka prípojky
RZ 1. NP-1/9 (tp=45°C)	rozdelovač na 1 .NP 1. napojenie a
VARIONOVA	9 vetiev (tp - teplota prívodu)
PZ:21°C	typ prichytenia potrubi pre podlahove kurenie
	maximálna povrchová teplota podlahovej zóny

LEGENDA VYKUROVACÍCH TELIES:

OCEĽOVÉ DOSKOVÉ VYKUROVACIE TELESO RADIK
TYP RADIK, SO SPODNÝM PRIPOJENÍM

SPÔSOB ZNAČENIA

33 VK 900 /900

- 900 (druhé) - STAVEBNÁ DĹŽKA V MILIMETROCH
- 900 (prvé) - STAVEBNÁ VÝŠKA V MILIMETROCH
- VK - PREVEDENIE VENTIL KOMPAKT - SO SPODNÝM PRIPOJENÍM
- 33 - TYP DVOJRADOVÝ

ELEKTRICKÉ PRIAMOVÝHREVNÉ REBRÍKOVÉ VYKUROVACIE TELESO
TYP KORALUX LINEAR MAX-ERA, FY. KORADO

FÓLIOVÁ TECHNOLÓGIA SYSTÉMU VYHRIEVANIA NA ZÁKLADE DLHOVLNNÉHO
INFRAČERVENÉHO ŽIARENIA

LEGENDA POTRUBIA:

POTRUBIE - PLASTHLINNÍKOVÁ RURKA PE-Xa/AL/PE napr. RAUTITAN Stabil REHAU
SPÁJANÉ LISOVANÍM, IZOLOVANÉ POTRUBIE, TEPLOTNÝ SPÁD 45/35°C. PRE PODLAHOVÉ VYKUROVANIE
POTRUBIE - PLASTHLINNÍKOVÁ RURKA PE-Xa/AL/PE napr. RAUTITAN Stabil REHAU
SPÁJANÉ LISOVANÍM, IZOLOVANÉ POTRUBIE, TEPLOTNÝ SPÁD 45/35°C.

ROZVOD ÚK PRE PRIMÁRNY OKRUH TEPELNÉHO ČERPADLA
PRE OKRUHY KONVEKČNÉHO VYKUROVANIA, PRÍVOD A SPATOČKA
MATERIÁL MEĎ

LEGENDA ZARIADENÍ A ARMATÚR :

1a	VNÚTORNÁ JEDNOTKA TEPELNÉHO ČERPADLA BRILON ELCO AEROTOP SPLIT 08.2 M-CR 1Z
1b	VONKAJ.JEDNOTKA BRILON ELCO AEROTOP SPLIT 08.2 M-CR 1Z MAX.VÝSTUPNÁ TEPLOTA 60°C,TEPELNY VYKON 8kW A7/W35, 3f-400V
03	AKUMULAČNÍ ZÁSOBNÍK VYKUROVACEJ VODY WPPS 130, Objem 130l
04	UZAVRETÁ TLAKOVÁ EXPANZNÁ NÁDOBA VIESSMANN C35 OBJEM 35L, 3bar
TP	TERMOSTAT PRIESTOROVÝ REMOCON PLUS 2
TE	SNÍMAČ VONKAJŠEJ TEPLOTY
R1	LOKÁLNA REKUPERAČNÁ JEDNOTKA TYPU NAPR. VIESSMANN VITOVENT 100-D

- PRÍPADNÉ ZMENY PROJEKTU JE NUTNÉ PRED ICH REALIZÁCIOU PREKONZULTOVAŤ S AUTOROM PROJEKTU, ICH REALIZÁCIA JE MOŽNÁ NA ZÁKLADE JEHO PÍSOMNÉHO SÚHLASU !
- PRÍPADNÉ NEJASNOSTI V PROJEKTE JE NUTNÉ BEZODKLADNE OZNÁMIŤ ZODPOVEDNÉMU PROJEKTANTOVI !
- PROJEKTOVANÉ ROZMERY STAVEBNÝCH VÝROBKOV A KONŠTRUKCIÍ JE NUTNÉ PRED ICH ZADANÍM DO VÝROBY OVERIŤ PREMERANÍM PRIAMO NA STAVBE !

±0,000 = 300 mm nad U.T

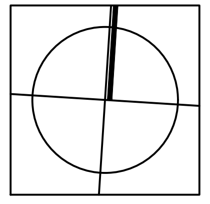

AUTOR PROJEKTU
ZODPOVEDNÝ PRO
INVESTOR
MIESTO STAVBY
PROFESIA
DRUH STAVBY
NÁZOV VÝKRESU
OZNAČENIE VÝKRE