DETAIL ZAPOJENIA VYKUROVACÍCH TELIES
REBRÍKOVÉ VYKUROVACIE TELESO

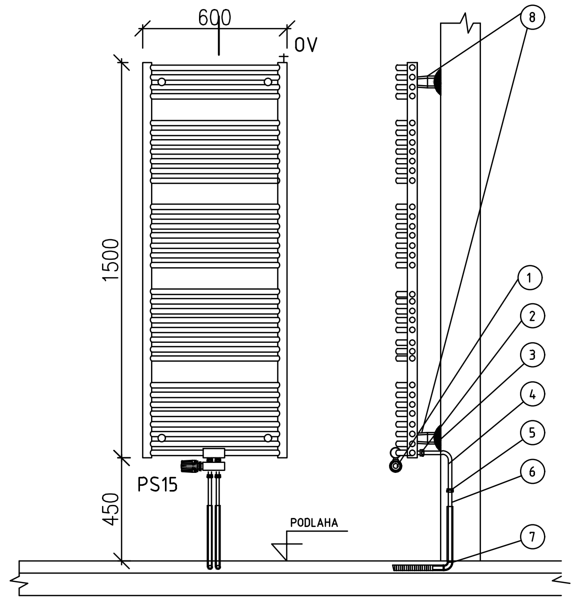

LEGENDA:

1 Stredové pripojenie vykurovacieho telesa, rozteč H=50mm
2 Svorková spojka
3 Krycia rozeta
4 Pripojovacia garnitúra s upevňovacím
5 Násuvná objímka
6 Vykurovacia rúrka
7 Vodiaci oblúk 90°
8 Stenová konzola

DETAIL ZAPOJENIA VYKUROVACÍCH TELIES
DOSKOVÉ VYKUROVACIE TELESO

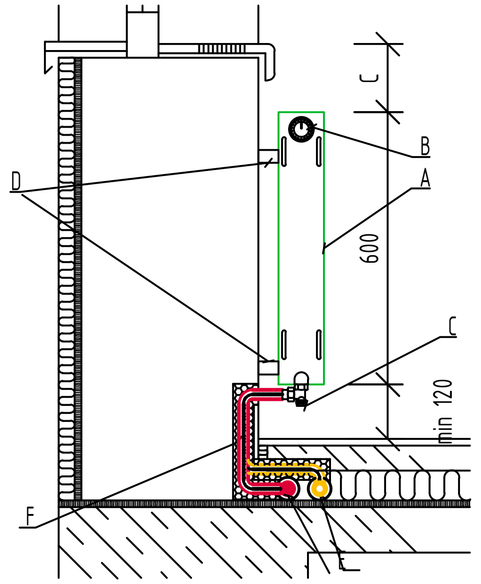

DETAIL OSADENIA VYK. TELESA
NA ROZVODY ÚK

A VYKUROVACIE TELESO
B TERMOSTATICKÁ HLAVICA
C ROHOVÁ PRIPOJOVACIA ARMATÚRA
D DRŽIAK
E ROZVODY ÚSTREDNÉHO KÚRENIA
F TRUBICOVÁ IZOLÁCIA

- 2.02 -	
Detska izba 1	
19.2 m2	47.0 m3
22 °C	488 W

- 2.03 -	
Detska izba 2	
16.8 m2	42.1 m3
22 °C	468 W

- 2.04 -	
Kupelna + wc	
6.1 m2	15.3 m3
24 °C	221 W

SYSTÉM	Elektrické vyhrievacie fólie KS
tep. výkon fólie	330 W
plocha fólie	3,0 m2

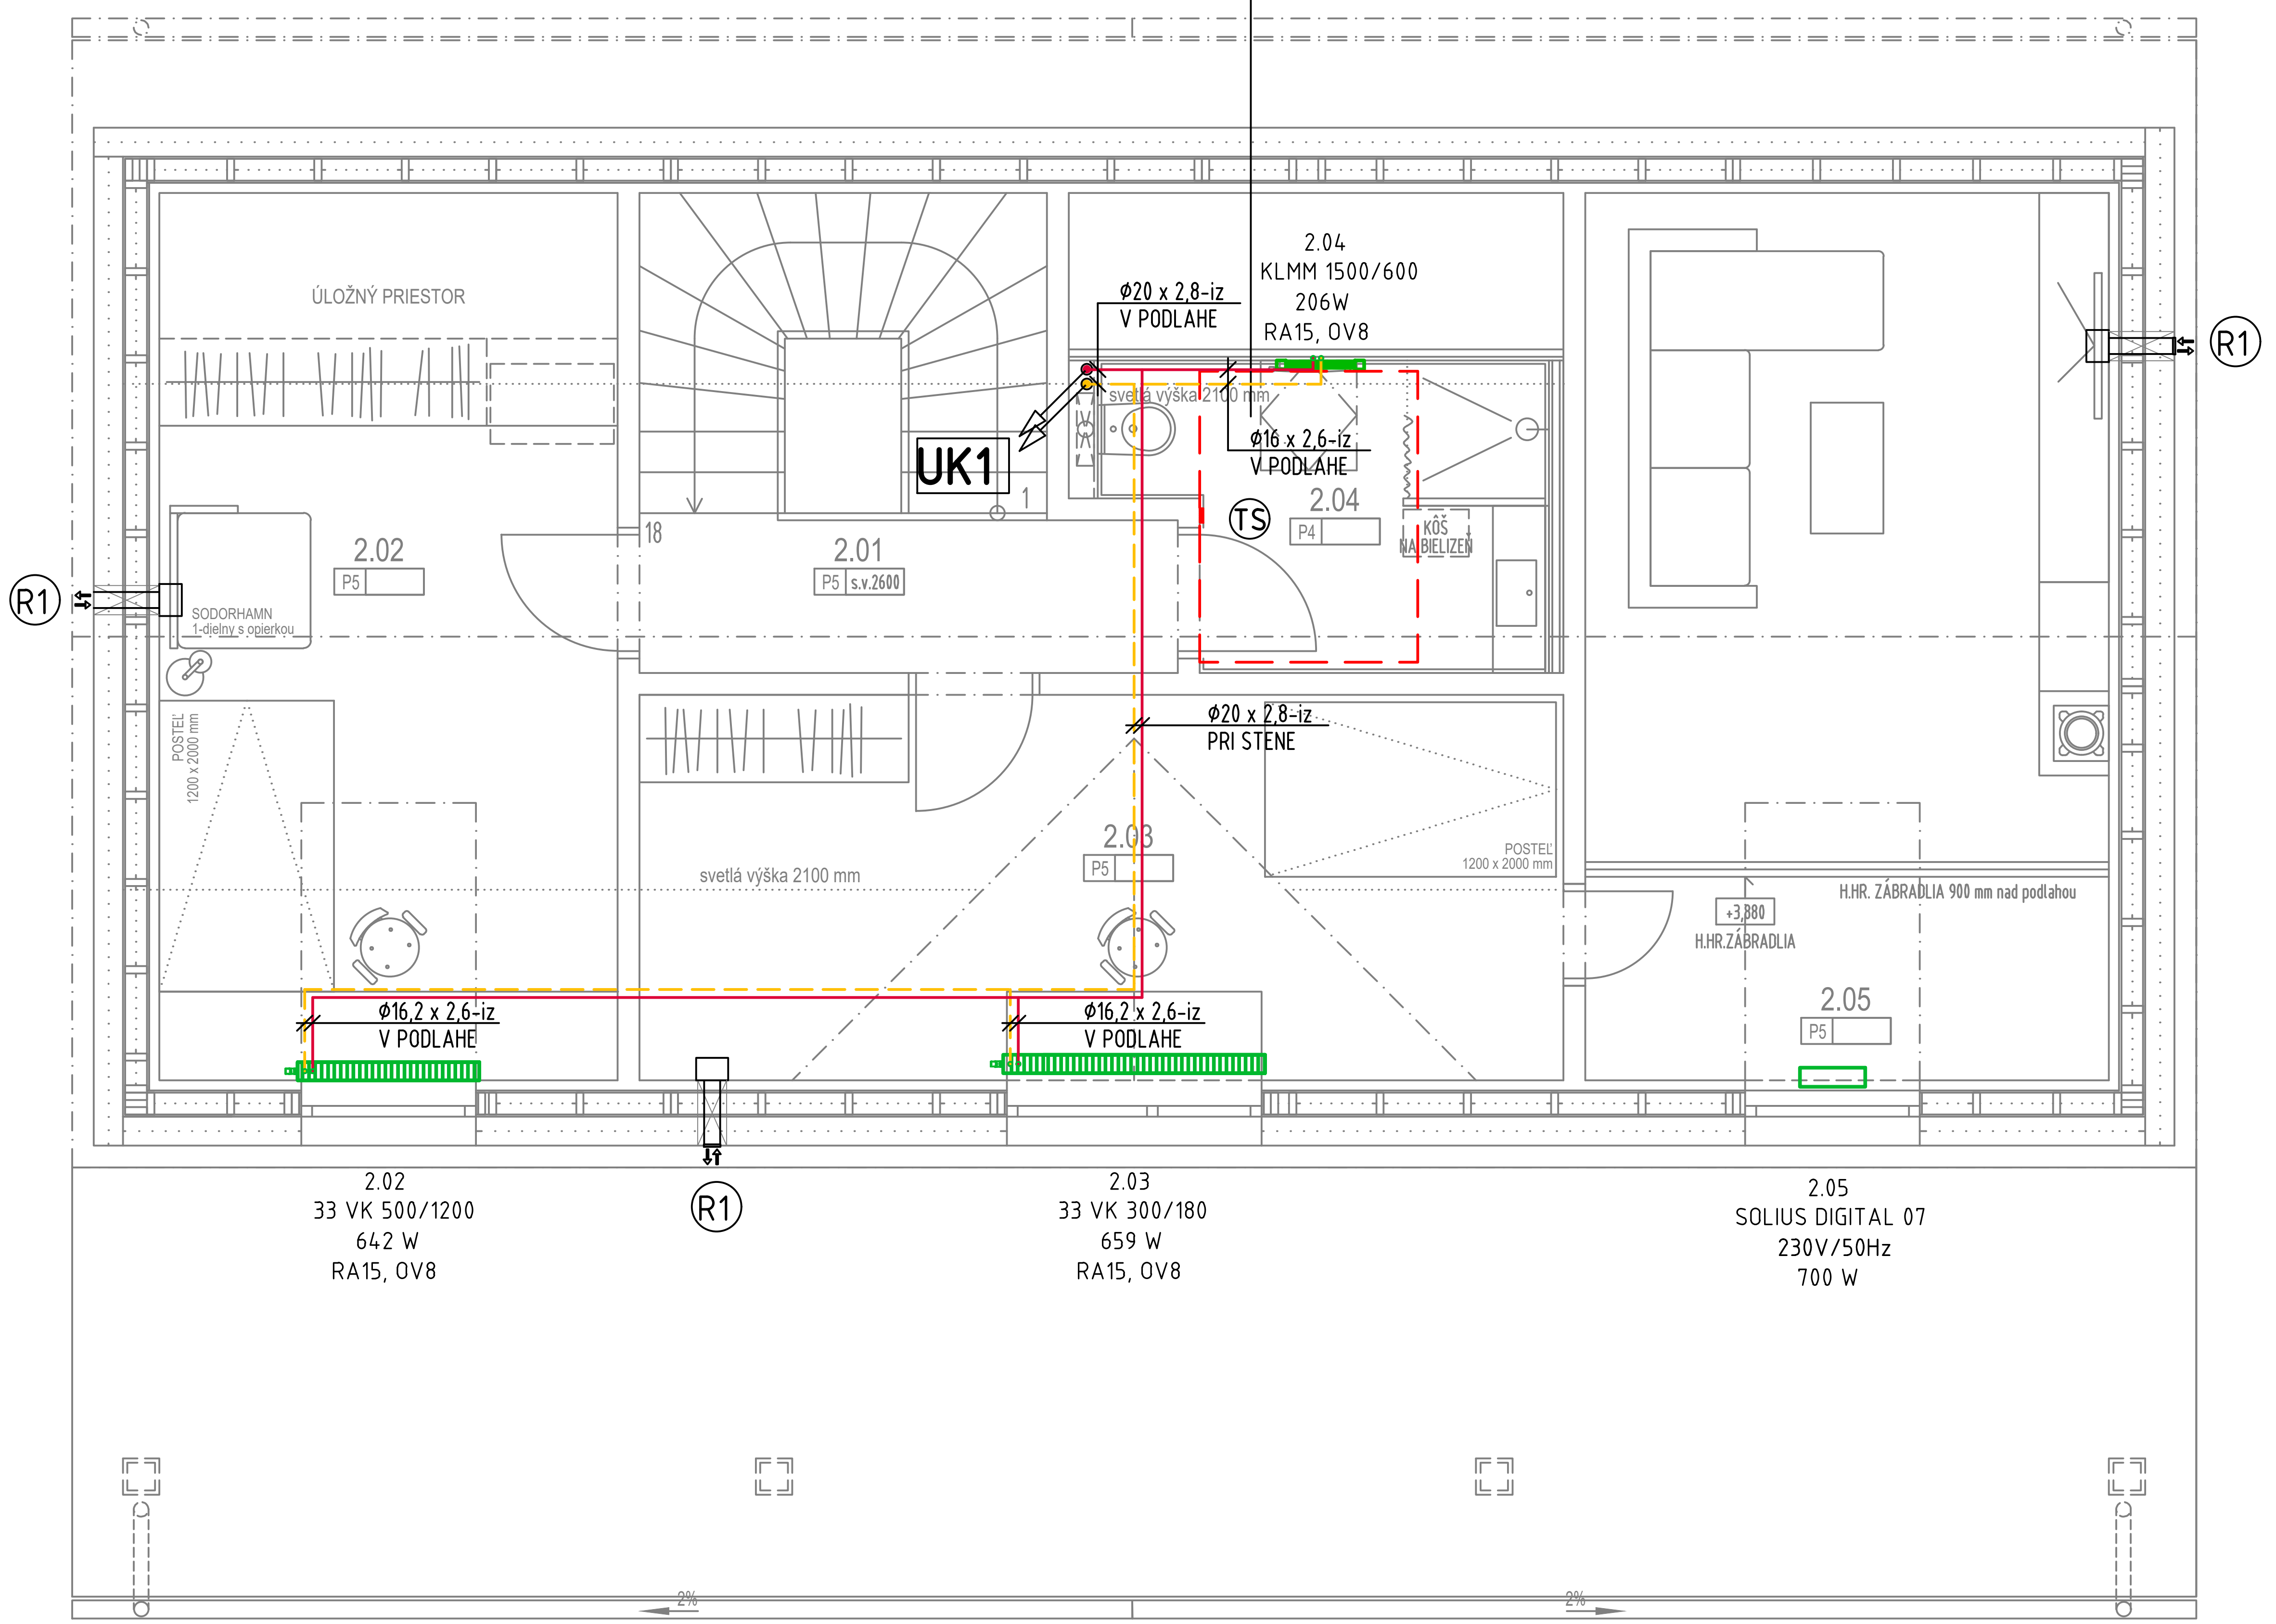

LEGENDA VYKUROVACÍCH TELIES:

▥ OCEĽOVÉ DOSKOVÉ VYKUROVACIE TELESO RADIK
SPÔSOB ZNAČENIA — TYP RADIK, SO SPODNÝM PRIPOJENÍM

33 VK 900 /900
- 900 (druhé) — STAVEBNÁ DĹŽKA V MILIMETROCH
- 900 (prvé) — STAVEBNÁ VÝŠKA V MILIMETROCH
- VK — PREVEDENIE VENTIL KOMPAKT - SO SPODNÝM PRIPOJENÍM
- 33 — TYP DVOJRADOVÝ

🟩 REBRÍKOVÉ VYKUROVACIE TELESO
TYP KORALUX LINEAR MAX-M, FY. KORADO

🟥 FÓLIOVÁ TECHNOLÓGIA SYSTÉMU VYHRIEVANIA NA ZÁKLADE DLHOVLNNÉHO
INFRAČERVENÉHO ŽIARENIA

LEGENDA POTRUBIA:

POTRUBIE - PLASTHLINNÍKOVÁ RURKA PE-Xa/AL/PE napr. RAUTITAN Stabil REHAU
SPÁJANÉ LISOVANÍM, IZOLOVANÉ POTRUBIE, TEPLOTNÝ SPÁD 45/35°C. PRE PODLAHOVÉ VYKUROVANIE

POTRUBIE - PLASTHLINNÍKOVÁ RURKA PE-Xa/AL/PE napr. RAUTITAN Stabil REHAU
SPÁJANÉ LISOVANÍM, IZOLOVANÉ POTRUBIE, TEPLOTNÝ SPÁD 45/35°C.

ROZVOD ÚK PRE PRIMÁRNY OKRUH TEPELNÉHO ČERPADLA
PRE OKRUHY KONVEKČNÉHO VYKUROVANIA, PRÍVOD A SPATOČKA
MATERIÁL MEĎ

LEGENDA ZARIADENÍ A ARMATÚR :

1a	VNÚTORNÁ JEDNOTKA TEPELNÉHO ČERPADLA BRILON ELCO AEROTOP SPLIT 08.2 M-CR 1Z
1b	VONKAJ.JEDNOTKA BRILON ELCO AEROTOP SPLIT 08.2 M-CR 1Z MAX.VÝSTUPNÁ TEPLOTA 60°C,TEPELNY VYKON 8kW A7/W35, 3f-400V
03	AKUMULAČNÍ ZÁSOBNÍK VYKUROVACEJ VODY WPPS 130, Objem 130l
04	UZAVRETÁ TLAKOVÁ EXPANZNÁ NÁDOBA VIESSMANN C35 OBJEM 35L, 3bar
TP	TERMOSTAT PRIESTOROVÝ REMOCON PLUS 2
TE	SNÍMAČ VONKAJŠEJ TEPLOTY
R1	LOKÁLNA REKUPERAČNÁ JEDNOTKA TYPU NAPR. VIESSMANN VITOVENT 100-D
TS	PRIESTOROVÝ REGULÁTOR TEPLOTY PRE ELEKTRICKÉ PODLAHOVÉ VYKUROVANIE

- PRÍPADNÉ ZMENY PROJEKTU JE NUTNÉ PRED ICH REALIZÁCIOU PREKONZULTOVAŤ S AUTOROM PROJEKTU, ICH REALIZÁCIA JE MOŽNÁ NA ZÁKLADE JEHO PÍSOMNÉHO SÚHLASU !
- PRÍPADNÉ NEJASNOSTI V PROJEKTE JE NUTNÉ BEZODKLADNE OZNÁMIŤ ZODPOVEDNÉMU PROJEKTANTOVI !
- PROJEKTOVANÉ ROZMERY STAVEBNÝCH VÝROBKOV A KONŠTRUKCIÍ JE NUTNÉ PRED ICH ZADANÍM DO VÝROBY OVERIŤ PREMERANÍM PRIAMO NA STAVBE !

±0,000 = 300 mm nad

AUTOR PROJEKTU	
ZODPOVEDNÝ PRO	
INVESTOR	
MIESTO STAVBY	
PROFESIA	
DRUH STAVBY	
NÁZOV VÝKRESU	
OZNAČENIE VÝKRE	