

ELEKTRO A MaR.:

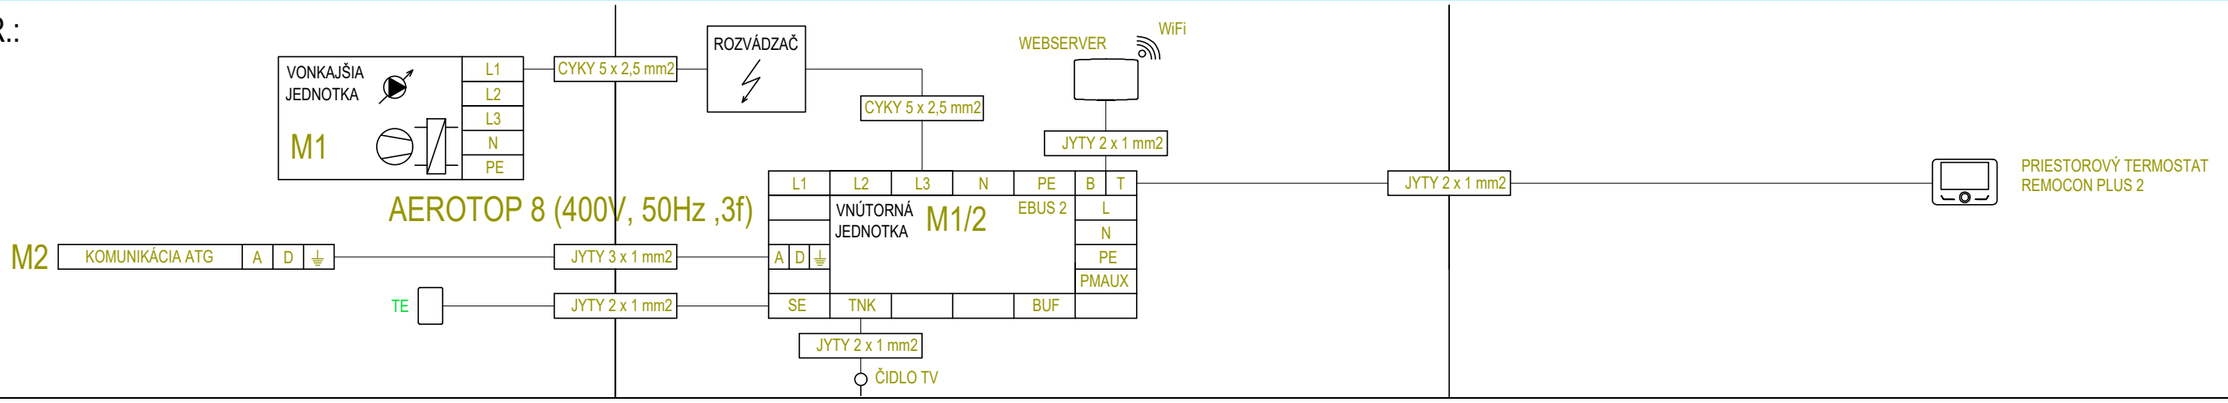

LEGENDA:

EK	ELEKTRO OHRIEVAČ	PV	POISTNÝ VENTIL
F	MAGNETICKÝ FILTER	OV	ODVZDUŠŇOVACÍ VENTIL
E	EXPANZNÁ NÁDOBA	T	TEPLOMER
3V	TROJCESTNÝ VENTIL	P	MANOMETER
GK	GULOVÝ KOHÚT	TE	VONKAJSÍ SNÍMAČ TEPLOTY
MK	EXPANZNÁ ARMATÚRA	OC	OBEHOVÉ ČERPADLO

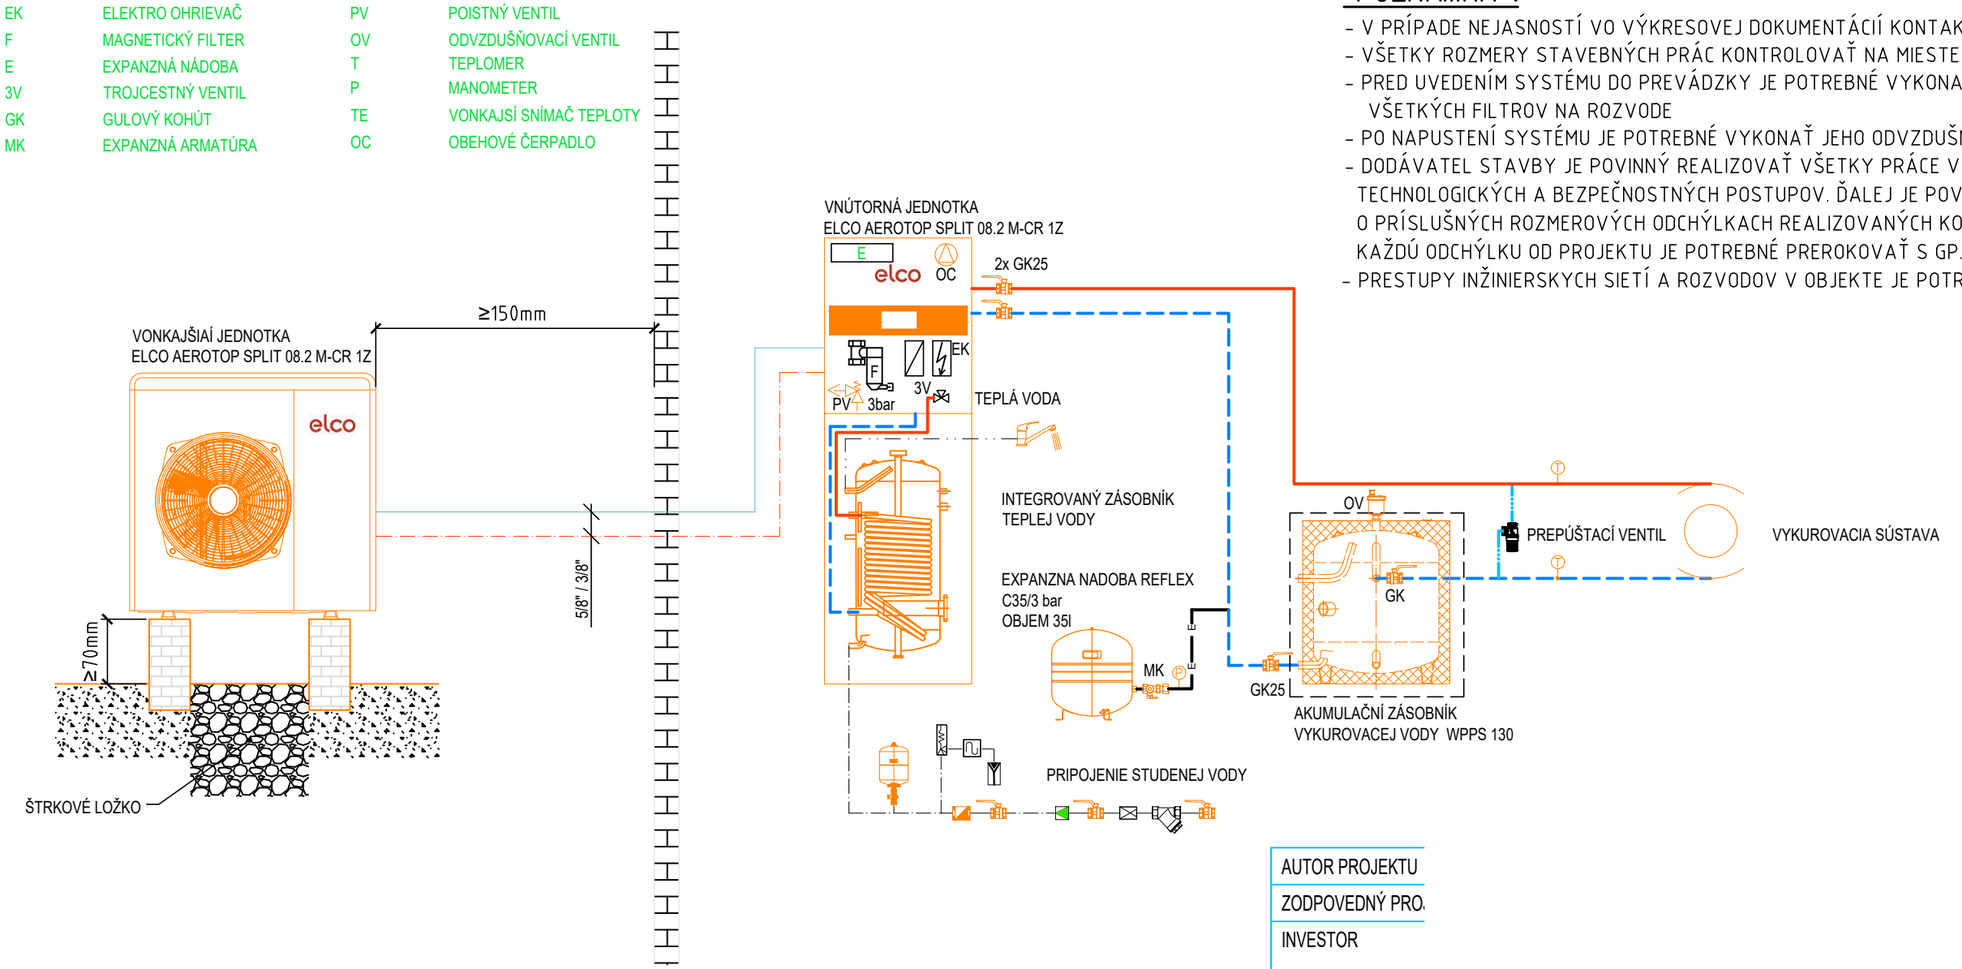

POZNÁMKA :

- V PRÍPADE NEJASNOSTÍ VO VÝKRESOVEJ DOKUMENTÁCII KONTAKTOVAŤ ZODPOVEDNÉHO PROJEKTANTA
- VŠETKY ROZMERY STAVEBNÝCH PRÁC KONTROLOVAŤ NA MIESTE STAVBY
- PRED UVEDENÍM SYSTÉMU DO PREVÁDZKY JE POTREBNÉ VYKONAŤ DÔKLADNÝ PREPLACH SYSTÉMU S VYČISTENÍM VŠETKÝCH FILTROV NA ROZVODE
- PO NAPUSTENÍ SYSTÉMU JE POTREBNÉ VYKONAŤ JEHO ODVZDUŠNENIE
- DODÁVATEL STAVBY JE POVINNÝ REALIZOVAŤ VŠETKY PRÁCE V ZMYSLE PLATNÝCH STN EN S DODRŽANÍM TECHNOLOGICKÝCH A BEZPEČNOSTNÝCH POSTUPOV. ĎALEJ JE POVINNÝ REŠPEKTOVAŤ USTANOVENIÁ STN 730421 O PRÍSLUŠNÝCH ROZMEROVÝCH ODCHÝLKACH REALIZOVANÝCH KONŠTRUKCIÍ PROTI PROJEKTOVANÉMU STAVU. KAŽDÚ ODCHÝLKU OD PROJEKTU JE POTREBNÉ PREROKOVAŤ S GP.
- PRESTUPY INŽINIERSKYCH SIETÍ A ROZVODOV V OBJEKTE JE POTREBNÉ VYNECHAŤ PRI REALIZÁCII STAVBY.

- TEPELNÉ ČERPADLO — ELCO AEROTOP SPLIT 08.2 M-CR 1Z
- AKUMULAČNÝ ZÁSOBNÍK — WPPS 130
- ZÁSOBNÍK TEPLEJ VODY — INTEGROVANÝ 180 L
- 1 VYKUROVACÍ OKRUH

Elco Aerotop Split			
Model	Chladivo	Plyn/kapalina - vnější Ø	
		mm	"
05.2	R32	**15,9 / 9,52**	**5/8 / 3/8**
08.2	R32	**15,9 / 9,52**	**5/8 / 3/8**
12.2	R32	**15,9 / 9,52**	**5/8 / 3/8**
15.2	R32	**15,9 / 9,52**	**5/8 / 3/8**

PRÍVODNÉ POTRUBIE
VRATNÉ POTRUBIE
EXPANZNÉ POTRUBIE
KOMUNIK. VEDENIE
CHLADIVO

AUTOR PROJEKTU	
ZODPOVEDNÝ PRO.	
INVESTOR	
MIESTO STAVBY	
PROFESIA	
DRUH STAVBY	
NÁZOV VÝKRESU	
OZNAČENIE VÝKRE.	