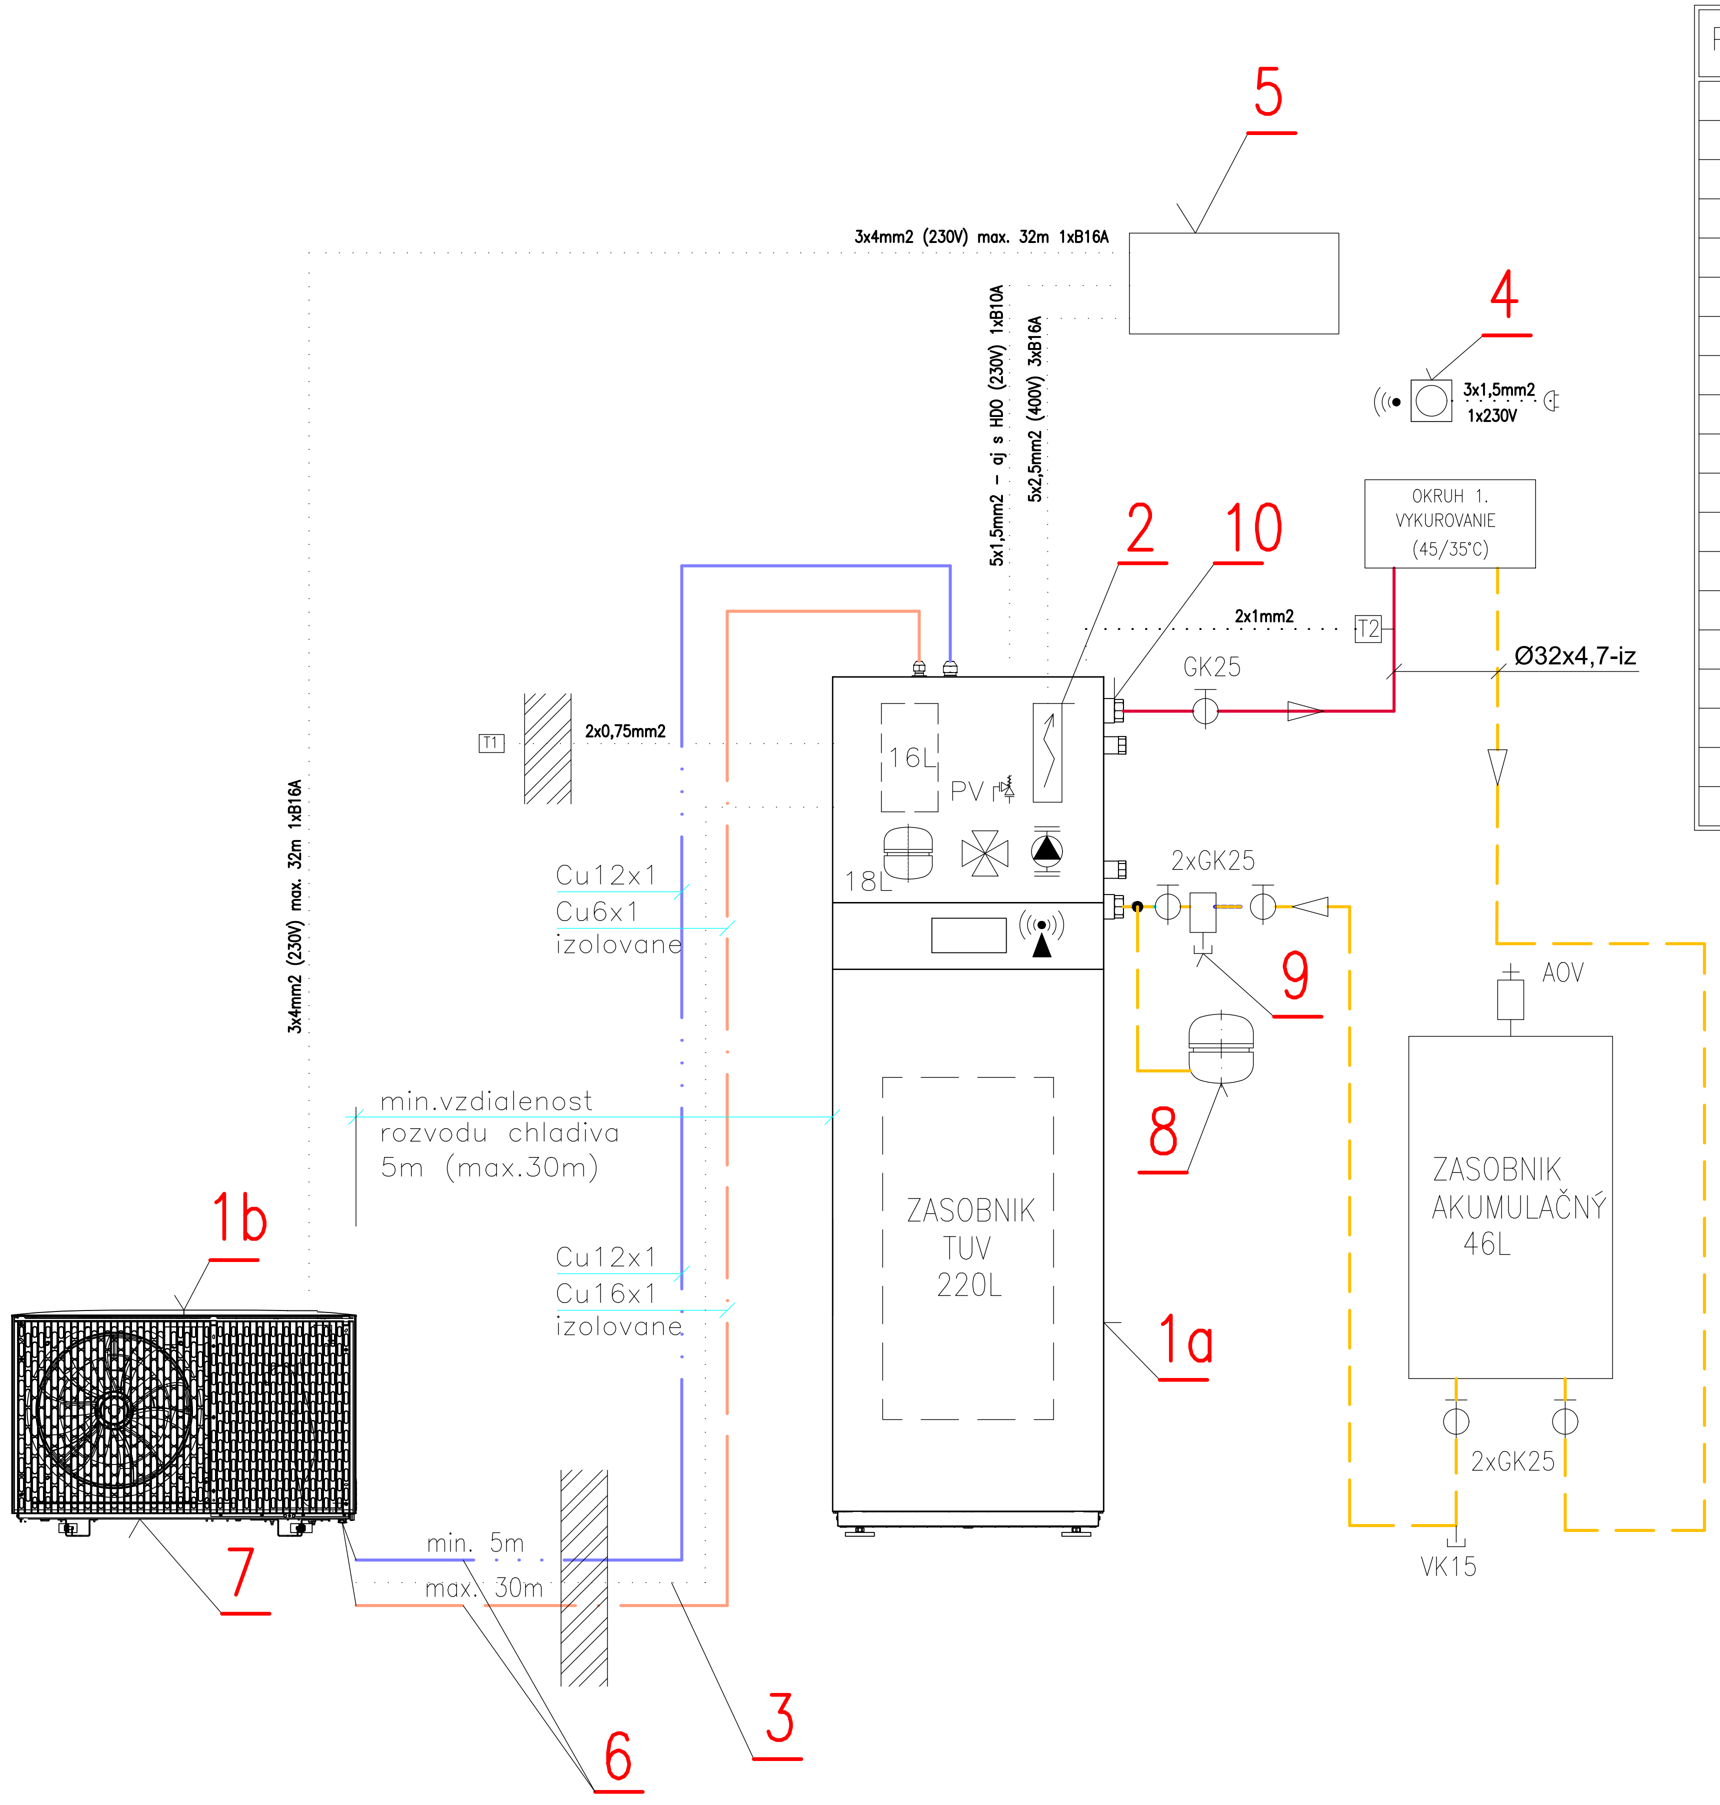

## LEGENDA ZARIADENÍ:

| POZ. | NÁZOV, ROZMER | P. KS |
|---|---|---|
| 1a | VNUT. JEDNOTKA napr. VITOCAL 222–S AWBT–M–E–AC 221.C08 | 1 |
| 1b | VON. JEDNOTKA napr. VITOCAL 222–S AWBT–M–E–AC 221.C08 (230V) | 1 |
| | MAX.VÝSTUPNÁ TEPLOTA 60°C,TEPELNY VYKON 3,5–7,5kW A7/W35 | |
| | EKOLOGICKE CHLADIVO R410A, REGULÁCIA ONE–BASE,WIFI | |
| 2 | ELEKTRIC.PRIETOKOVY OHRIEVAC 8kW –v rozsahu dodavky pol.1a | 1 |
| 3 | CANBUS KOMUNIKACNY KABEL MEDZI JEDNOTKY 15m | 1 |
| 4 | BEZDROTOVÉ DIALKOVE OVLADANIE VITOTROL 300–E | 1 |
| 5 | ELEKTRICKY ROZVADZAC OBJEKTU | 1 |
| 6 | INSTALAC.SADA 12/6 NA ZEM+KONZOLA – 12,5M RURY | 1 |
| 7 | ELEKTRIC.VYHREVNY PAS PRE VANU KONDENZATU 2,5m | 1 |
| 8 | EXPANZNA NADOBA N25 OBJEM 25L, 4bar BIELA | 1 |
| | NASTENNY DRZIAK PRE N25 | 1 |
| 9 | ODKALOVAC S MAGNETOM A IZOLACIOU VITOTRAP 28mm | 1 |
| 10 | PRIPOJOVACIA SADA NA OMIETKU | 1 |
| | | |
| | | |
| T1 | SNIMAC VONKAJSEJ TEPLOTY – v rozsahu dodavky tep.cerpadla | 1 |
| T2 | SNIMAC ROSNEHO BODU – VLHKOSTI | 1 |
| | | |

## LEGENDA POTRUBÍ:

| | |
|---|---|
| 🟥 | Plasthliníkové potrubie materiál: PE-Xa/AL/PE napr. Rautitan Stabil, zaizolované potrubie, teplotný spád 45/35 °C. |
| 🟦 | Medené potrubie primárneho okruhu tepelného čerpadla: Cu ϕ12×1, 6×1-iz. |

## LEGENDA ARMATÚR :

| | |
|---|---|
| GK | Guľový kohút so závitom |
| PV | Poistný ventil so závitom |

## POZNÁMKY :

- V prípade akýchkoľvek nejasností v projektovej dokumentácii je nutné kontaktovať zodpovedného projektanta.
- Všetky stavebné rozmery a prestupy je potrebné overiť priamo na mieste realizácie.
- Pred samotným spustením systému do prevádzky sa musí vykonať dôkladný preplach rozvodov a vyčistenie všetkých inštalovaných filtrov.
- Po napustení vykurovacej sústavy médiom je nevyhnutné zabezpečiť jej postupné odvzdušnenie.
- Zhotoviteľ je povinný postupovať v súlade s platnými normami STN EN a dodržiavať technologické aj bezpečnostné predpisy. Zároveň musí rešpektovať ustanovenia STN 730421 o rozmerových odchýlkach. Každú zmenu oproti projektu je nutné vopred skonzultovať s HIP.
- Otvory pre prestupy inžinierskych sietí a potrubných rozvodov v objekte je potrebné pripraviť počas realizácie hrubej stavby.
- Táto dokumentácia nenahrádza realizačnú dokumentáciu stavby!
-Výšková úroveň ±0,000 v projekte zodpovedá úrovni finálnej nášľapnej vrstvy podlahy.

TABUĽKA REVÍZIÍ

| | | | |
|---|---|---|---|
| | | | |
| | | | |
| | | | |
| ČÍSLO REVÍZIE | DÁTUM | POPIS ZMENY | VYPRACOVAL |

0,000=+0,300 nad korunou komunikácie m n. m.

| | |
|---|---|
| AUTOR PROJEKTU: | Ing. arch Pavel Vojtek, Ing. arch Ivor Mečiar, ArtD. |
| H.I.P.: | Ing. arch Ivor Mečiar, ArtD. |
| ZODP. PROJEKTANT: | Ing. Ján Bátor |
| VYPRACOVAL: | Bc. Viktor Lahovský |

GENERÁLNY PROJEKTANT:
**Alla s.r.o.**
Riazanská 70/683
831 02 Bratislava
tel.: +421 907 693 679
email: ateliar@alla.sk

| | |
|---|---|
| INVESTOR: | Ing. |
| NÁZOV PROJEKTU: | **RD** |
| MIESTO STAVBY: | Hvie |
| OBSAH VÝKRESU: | **SC**<br>**ZA** |
| STAVEBNÝ OBJEKT: | **SO** |
| ID STAVBY: -- | STUPEŇ PD: PSP |
| NÁZOV VÝKRESU V ELEKTRONICKEJ POD | |