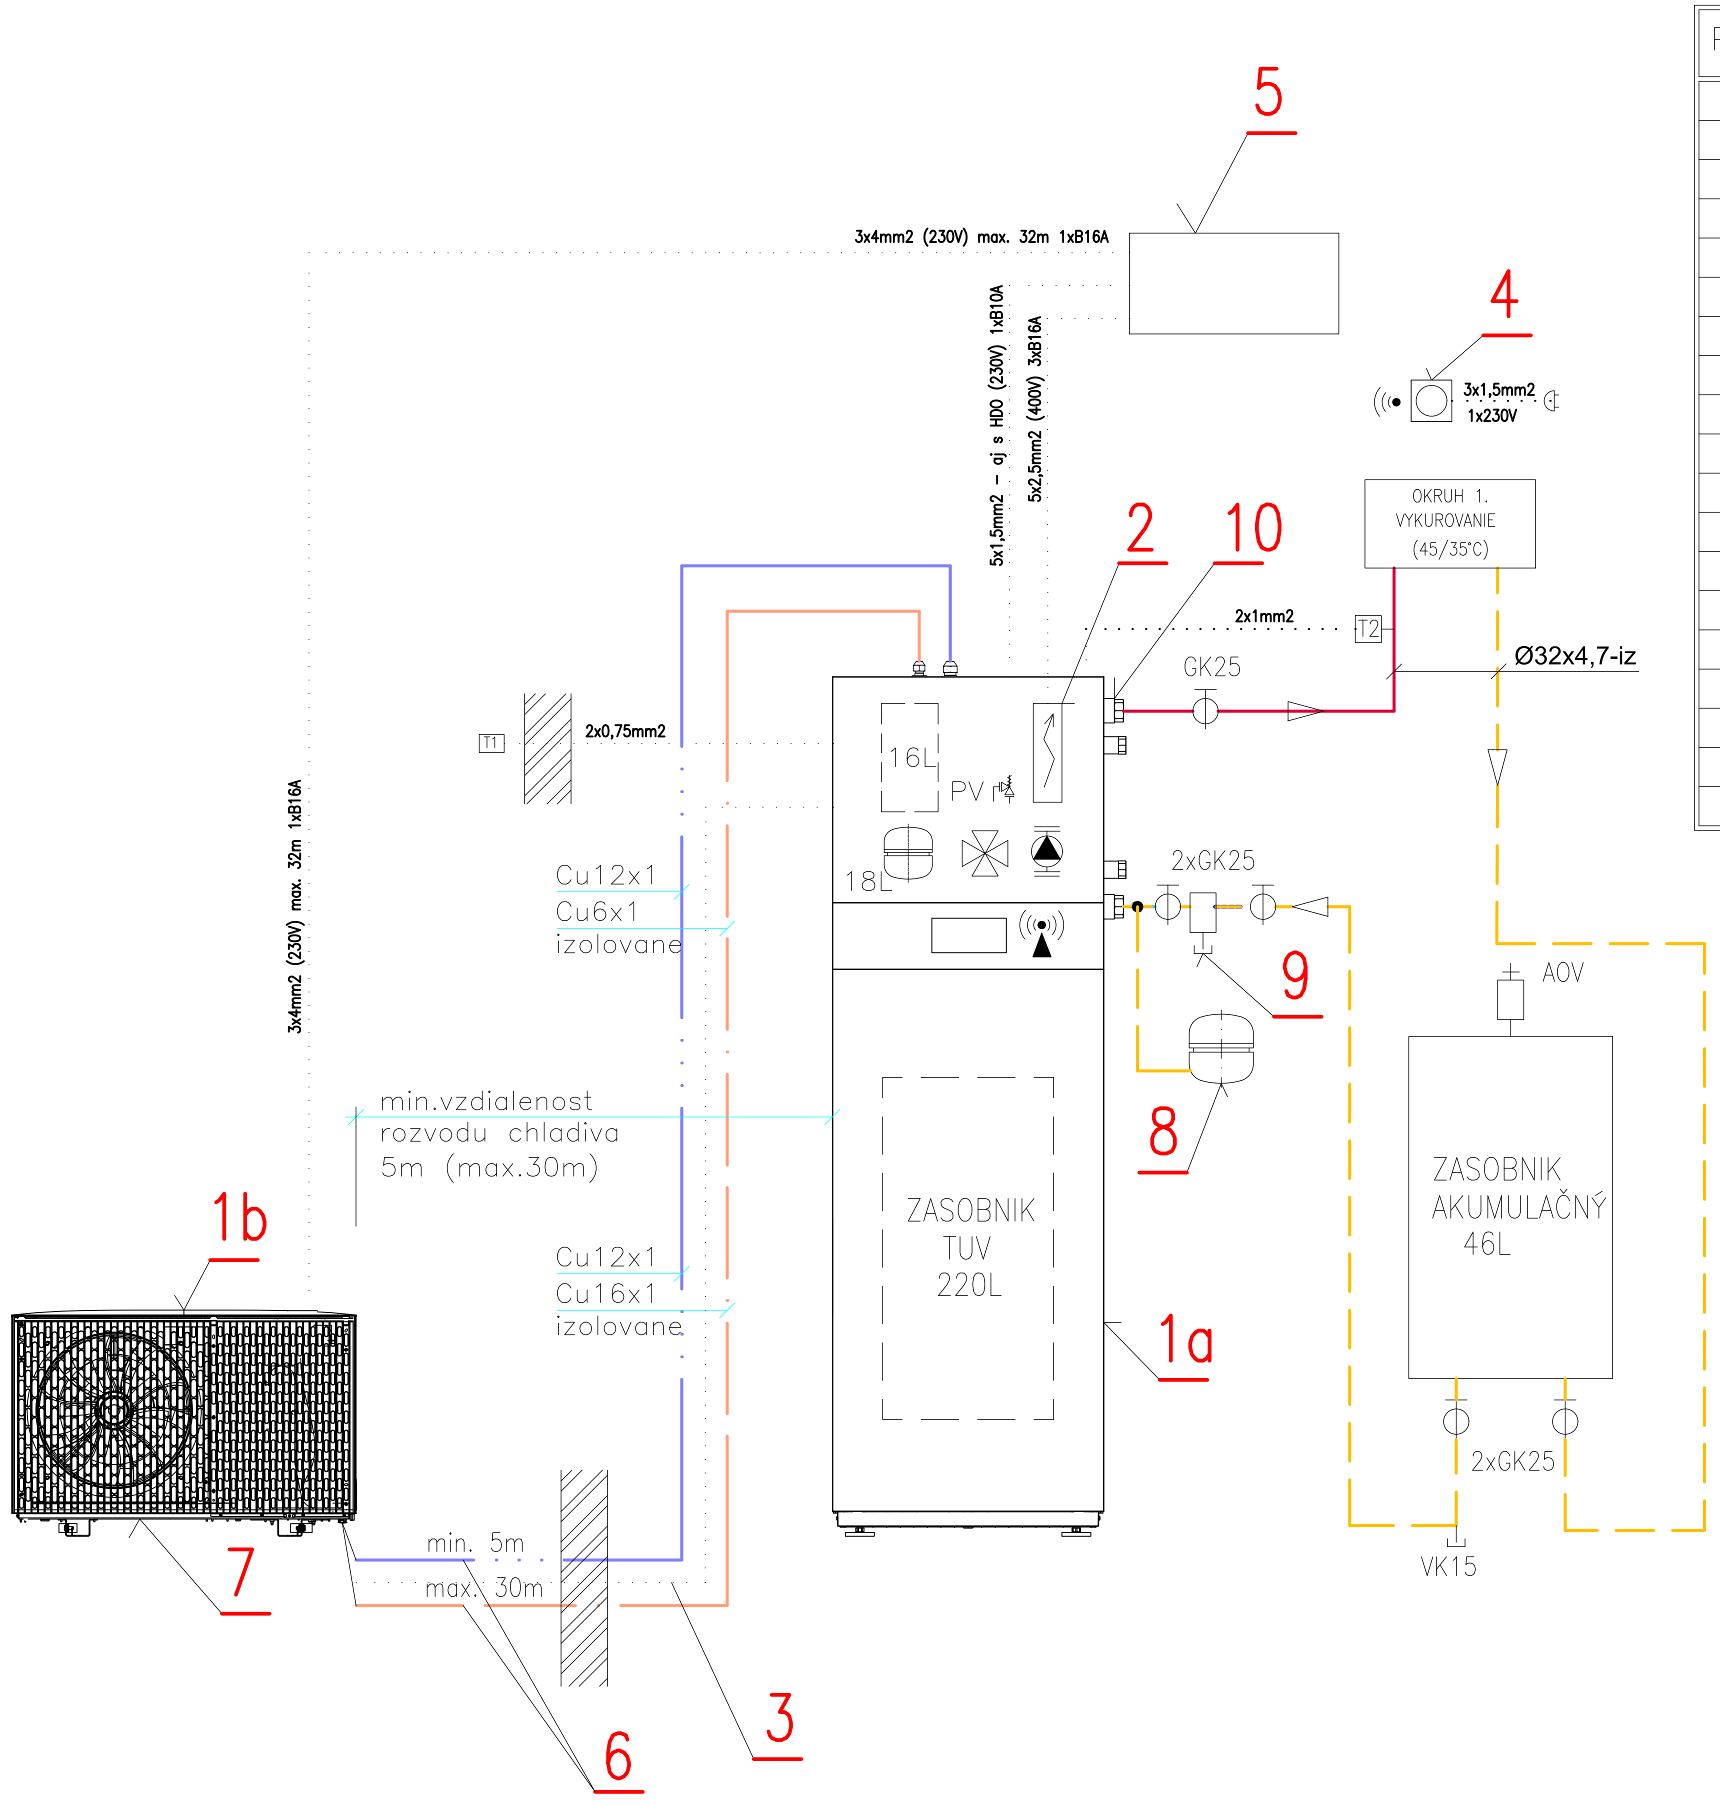

LEGENDA ZARIADENÍ:

POZ.	NÁZOV, ROZMER	P. KS
1a	VNUT. JEDNOTKA napr. VITOCAL 222–S AWBT–M–E–AC 221.C08	1
1b	VON. JEDNOTKA napr. VITOCAL 222–S AWBT–M–E–AC 221.C08 (230V)	1
	MAX.VÝSTUPNÁ TEPLOTA 60°C,TEPELNY VYKON 3,5–7,5kW A7/W35	
	EKOLOGICKE CHLADIVO R410A, REGULÁCIA ONE–BASE,WIFI	
2	ELEKTRIC.PRIETOKOVY OHRIEVAC 8kW –v rozsahu dodavky pol.1a	1
3	CANBUS KOMUNIKACNY KABEL MEDZI JEDNOTKY 15m	1
4	BEZDROTOVÉ DIALKOVE OVLADANIE VITOTROL 300–E	1
5	ELEKTRICKY ROZVADZAC OBJEKTU	1
6	INSTALAC.SADA 12/6 NA ZEM+KONZOLA – 12,5M RURY	1
7	ELEKTRIC.VYHREVNY PAS PRE VANU KONDENZATU 2,5m	1
8	EXPANZNA NADOBA N25 OBJEM 25L, 4bar BIELA	1
	NASTENNY DRZIAK PRE N25	1
9	ODKALOVAC S MAGNETOM A IZOLACIOU VITOTRAP 28mm	1
10	PRIPOJOVACIA SADA NA OMIETKU	1
T1	SNIMAC VONKAJSEJ TEPLOTY – v rozsahu dodavky tep.cerpadla	1
T2	SNIMAC ROSNEHO BODU – VLHKOSTI	1

LEGENDA POTRUBÍ:

Plasthliníkové potrubie materiál: PE-Xa/AL/PE napr. Rautitan Stabil, zaizolované potrubie, teplotný spád 45/35 °C.

Medené potrubie primárneho okruhu tepelného čerpadla: Cu ϕ12×1, 6×1-iz.

LEGENDA ARMATÚR :

GK	Guľový kohút so závitom
PV	Poistný ventil so závitom

POZNÁMKY :

- V prípade akýchkoľvek nejasností v projektovej dokumentácii je nutné kontaktovať zodpovedného projektanta.
- Všetky stavebné rozmery a prestupy je potrebné overiť priamo na mieste realizácie.
- Pred samotným spustením systému do prevádzky sa musí vykonať dôkladný preplach rozvodov a vyčistenie všetkých inštalovaných filtrov.
- Po napustení vykurovacej sústavy médiom je nevyhnutné zabezpečiť jej postupné odvzdušnenie.
- Zhotoviteľ je povinný postupovať v súlade s platnými normami STN EN a dodržiavať technologické aj bezpečnostné predpisy. Zároveň musí rešpektovať ustanovenia STN 730421 o rozmerových odchýlkach. Každú zmenu oproti projektu je nutné vopred skonzultovať s HIP.
- Otvory pre prestupy inžinierskych sietí a potrubných rozvodov v objekte je potrebné pripraviť počas realizácie hrubej stavby.
- Táto dokumentácia nenahrádza realizačnú dokumentáciu stavby!
-Výšková úroveň ±0,000 v projekte zodpovedá úrovni finálnej nášľapnej vrstvy podlahy.

TABUĽKA REVÍZIÍ

ČÍSLO REVÍZIE	DÁTUM	POPIS ZMENY	VYPRACOVAL

0,000=+0,300 nad korunou komunikácie m n. m.

AUTOR PROJEKTU:	Ing. arch Pavel Vojtek, Ing. arch Ivor Me čiar, ArtD.	GENERÁLNY PROJEKTANT: **Alla s.r.o.** Riazanská 70/683 831 02 Bratislava tel.: +421 907 693 679 email: ateliar@alla.sk
H.I.P.:	Ing. arch Ivor Me čiar, ArtD.	
ZODP. PROJEKTANT:	Ing. Ján Bátor	
VYPRACOVAL:	Bc. Viktor Labovský	

INVESTOR:	Ing.
NÁZOV PROJEKTU:	**RD**
MIESTO STAVBY:	Hvie
OBSAH VÝKRESU:	**SC** **ZA**
STAVEBNÝ OBJEKT:	SO

ID STAVBY:	STUPEŇ PD:
--	PSP

NÁZOV VÝKRESU V ELEKTRONICKEJ POD