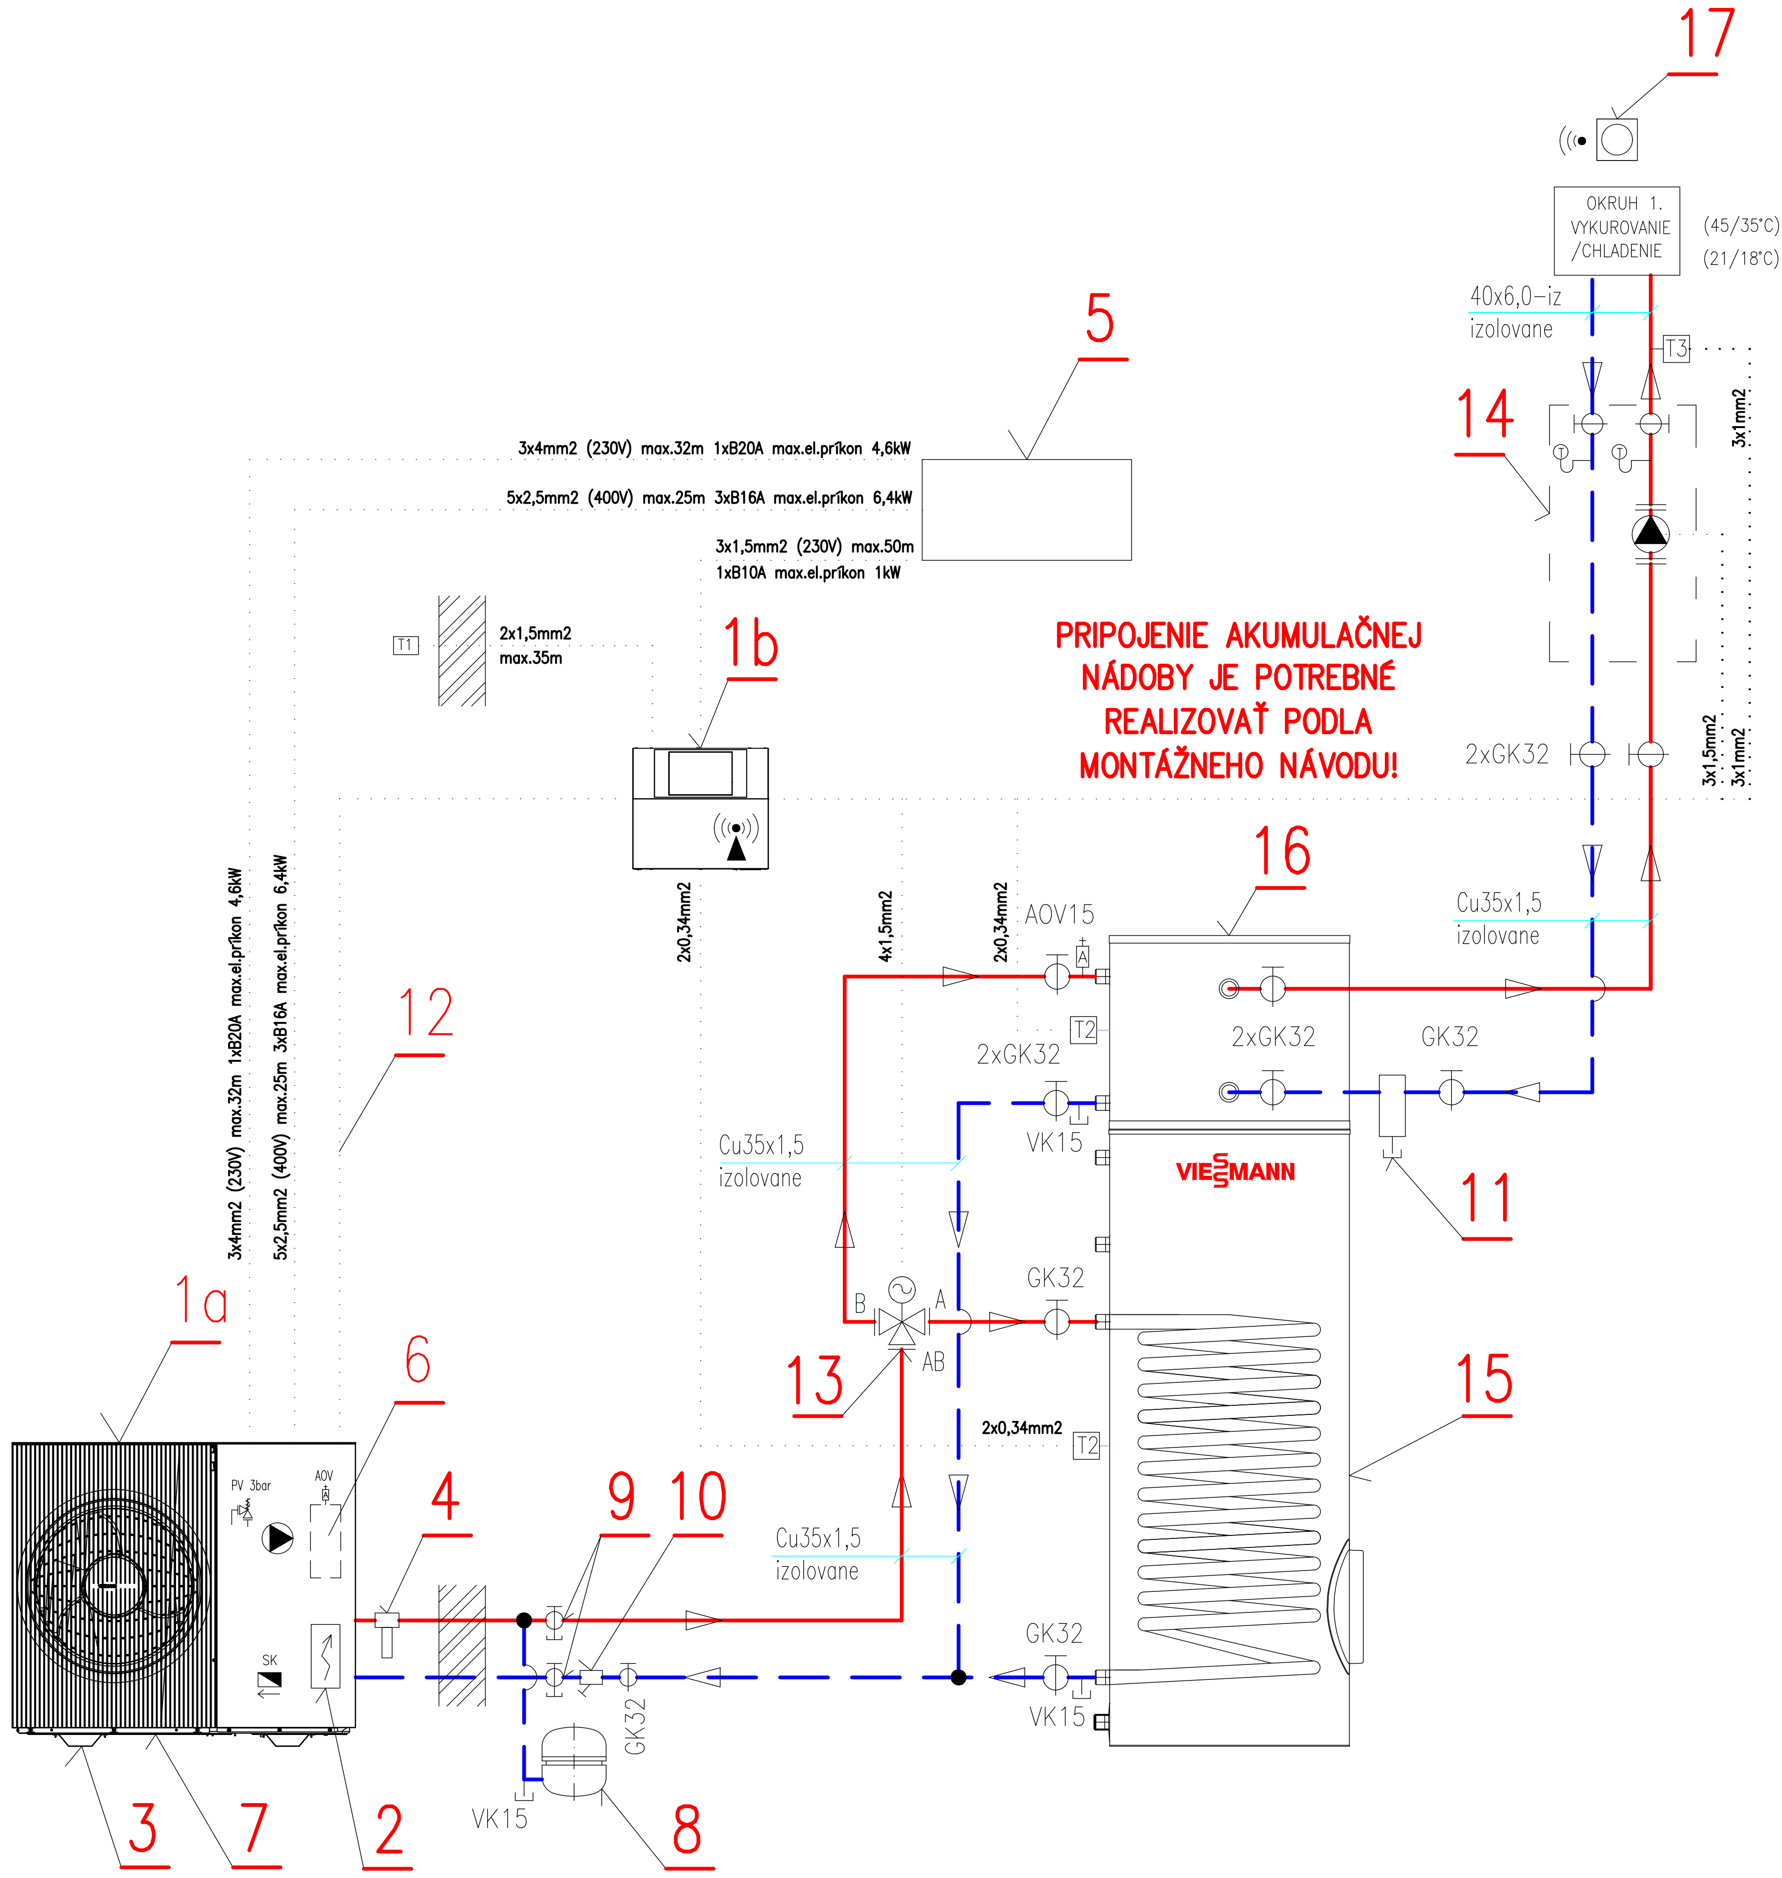
17
OKRUH 1. VYKUROVANIE /CHLADENIE
(45/35°C)
(21/18°C)
40x6,0–iz
izolovane
T3
3x1mm2
14
2xGK32
3x1,5mm2
3x1mm2
5
3x4mm2 (230V) max.32m 1xB20A max.el.príkon 4,6kW
5x2,5mm2 (400V) max.25m 3xB16A max.el.príkon 6,4kW
3x1,5mm2 (230V) max.50m
1xB10A max.el.príkon 1kW
T1
2x1,5mm2
max.35m
1b
2x0,34mm2
4x1,5mm2
2x0,34mm2
AOV15
16
Cu35x1,5
izolovane
T2
2xGK32
2xGK32
GK32
VK15
VIESSMANN
11
12
Cu35x1,5
izolovane
B
A
AB
13
GK32
15
2x0,34mm2
T2
Cu35x1,5
izolovane
GK32
VK15
1a
6
PV 3bar
AOV
SK
4
9
10
GK32
VK15
3
7
2
8

PRIPOJENIE AKUMULAČNEJ NÁDOBY JE POTREBNÉ REALIZOVAŤ PODLA MONTÁŽNEHO NÁVODU!

LEGENDA ZARIADENÍ:

POZ.	NÁZOV, ROZMER	P. KS
1a	VONKAJŠIA JEDNOTKA VITOCAL 200–A ie B12 230 V123	1
	MAX.VÝSTUPNÁ TEPLOTA 75°C, TEPELNÝ VÝKON 3,6–12,8kW A7/W35	1
	CHLADIVO R290 GWP3, ONE–BASE INTELIGENCE, WIFI (Z034465)	
1b	VNÚTORNÁ NÁSTENNÁ REGULÁCIA IDU–Controller – dodávka pol.1a	1
2	ELEKTRICKÝ PRIETOKOVÝ OHRIEVAČ 6,4kW – dodávka pol.1a	1
3	KONZOLA POD VONKAJŠIU JEDNOTKU–MONTÁŽ NA ZEM (3210409)	1
4	TERMOSTATICKÝ VENTIL PROTI ZAMRZNUTIU DN25 (ZR00220)	1
5	ELEKTRICKÝ ROZVÁDZAČ OBJEKTU	1
6	BEZPEČNOSTNÝ PLAVÁKOVÝ ODVZDUŠŇOVACÍ VENTIL–dodávka pol.1a	1
7	ELEKTRICKÝ VYHREVNÝ PÁS + VAŇA KONDENZÁTU (3210415)	1
8	EXPANZNA NADOBA N35 OBJEM 35L, 3bar BIELA (7938083)	1
	PRIPOJOVACI VENTIL PRE N35 (9572213)	1
9	SADA GULOV.KOHUTOV PRE PLNENIE A ODVZDUSNENIE (ZK06057)	1
10	GULOVY KOHUT S MAGNETICKYM FILTROM DN32 – dodávka pol.1a	1
11	ODKALOVAC S MAGNETOM A IZOLACIOU VITOTRAP 5/4" (ZK04657)	1
12	CANBUS KOMUNIKACNY KABEL MEDZI JEDNOTKY 15m (7973123)	1
13	TROJCESTNY PREPINACI VENTIL DN25 230V (7814924)	1
14	RMS BEZ ZMIESAVACA GDA211 DN32 Wilo Para 25/8 (7140702)	1
15	ZÁSOBNÍK TV VITOCELL 100–V TYP CVWC OBJEM 300L (Z026456)	1
16	AKUMULACNY ZASOBNIK VITOCELL 100–E TYP MSCA 50L 1(Z026457)	1
17	BEZDRATOVÉ DIALKOVE OVLADANIE VITOTROL 100–EH (7979559)	1
T1	SNIMAC VONKAJSEJ TEPLOTY – dodávka pol.1b	1
T2	SNIMAC TEPLOTY ZASOBNIKA – ponorny (7438702)	2
T3	SNIMAC ROSNEHO BODU 230V – VLHKOSTI (7452646)	1

LEGENDA POTRUBÍ:

PLASTHLINÍKOVÉ POTRUBIE MATERIÁL: PE-XA/AL/PE NAPR. RAUTITAN STABIL, ZAIZOLOVANÉ POTRUBIE, TEPLOTNÝ SPÁD 45/35 °C.

MEDENÉ POTRUBIE PRIMÁRNEHO OKRUHU TEPELNÉHO ČERPADLA: CU Φ12×1, 6×1-IZ.

LEGENDA ARMATÚR :

GK	GUĽOVÝ KOHÚT SO ZÁVITOM
AOV	AUTOMATICKÝ ODVZDUŠŇOVACÍ VENTIL S UZATVÁRACOU ARMATÚROU
PV	POISTNÝ VENTIL SO ZÁVITOM

POZNÁMKY :

- V PRÍPADE AKÝCHKOĽVEK NEJASNOSTÍ V PROJEKTOVEJ DOKUMENTÁCII JE NUTNÉ KONTAKTOVAŤ ZODPOVEDNÉHO PROJEKTANTA.
- VŠETKY STAVEBNÉ ROZMERY A PRESTUPY JE POTREBNÉ OVERIŤ PRIAMO NA MIESTE REALIZÁCIE.
- PRED SAMOTNÝM SPUSTENÍM SYSTÉMU DO PREVÁDZKY SA MUSÍ VYKONAŤ DÔKLADNÝ PREPLACH ROZVODOV A VYČISTENIE VŠETKÝCH INŠTALOVANÝCH FILTROV.
- PO NAPUSTENÍ VYKUROVACEJ SÚSTAVY MÉDIOM JE NEVYHNUTNÉ ZABEZPEČIŤ JEJ POSTUPNÉ ODVZDUŠNENIE.
- ZHOTOVITEĽ JE POVINNÝ POSTUPOVAŤ V SÚLADE S PLATNÝMI NORMAMI STN EN A DODRŽIAVAŤ TECHNOLOGICKÉ AJ BEZPEČNOSTNÉ PREDPISY. ZÁROVEŇ MUSÍ REŠPEKTOVAŤ USTANOVENIA STN 730421 O ROZMEROVÝCH ODCHÝLKACH. KAŽDÚ ZMENU OPROTI PROJEKTU JE NUTNÉ VOPRED SKONZULTOVAŤ S HIP.
- OTVORY PRE PRESTUPY INŽINIERSKYCH SIETÍ A POTRUBNÝCH ROZVODOV V OBJEKTE JE POTREBNÉ PRIPRAVIŤ POČAS REALIZÁCIE HRUBEJ STAVBY.
- TÁTO DOKUMENTÁCIA NENAHRÁDZA REALIZAČNÚ DOKUMENTÁCIU STAVBY!
-VÝŠKOVÁ ÚROVEŇ ±0,000 V PROJEKTE ZODPOVEDÁ ÚROVNI FINÁLNEJ NÁŠĽAPNEJ VRSTVY PODLAHY.

PROJEKTANT TZB:
TZB Smart Engineering s. r. o.
Karpatské námestie 7770/10A
831 06 Bratislava

TZB smart engineering

VYPRACOVAL:
ING. VIKTOR Labovský

ZODPOVEDNÝ PROJEKTANT
ING. JÁN BÁTOR

+0,000 = 170,90 m n.m. - ÚROVEŇ 1. NP

PROJEKTANT: