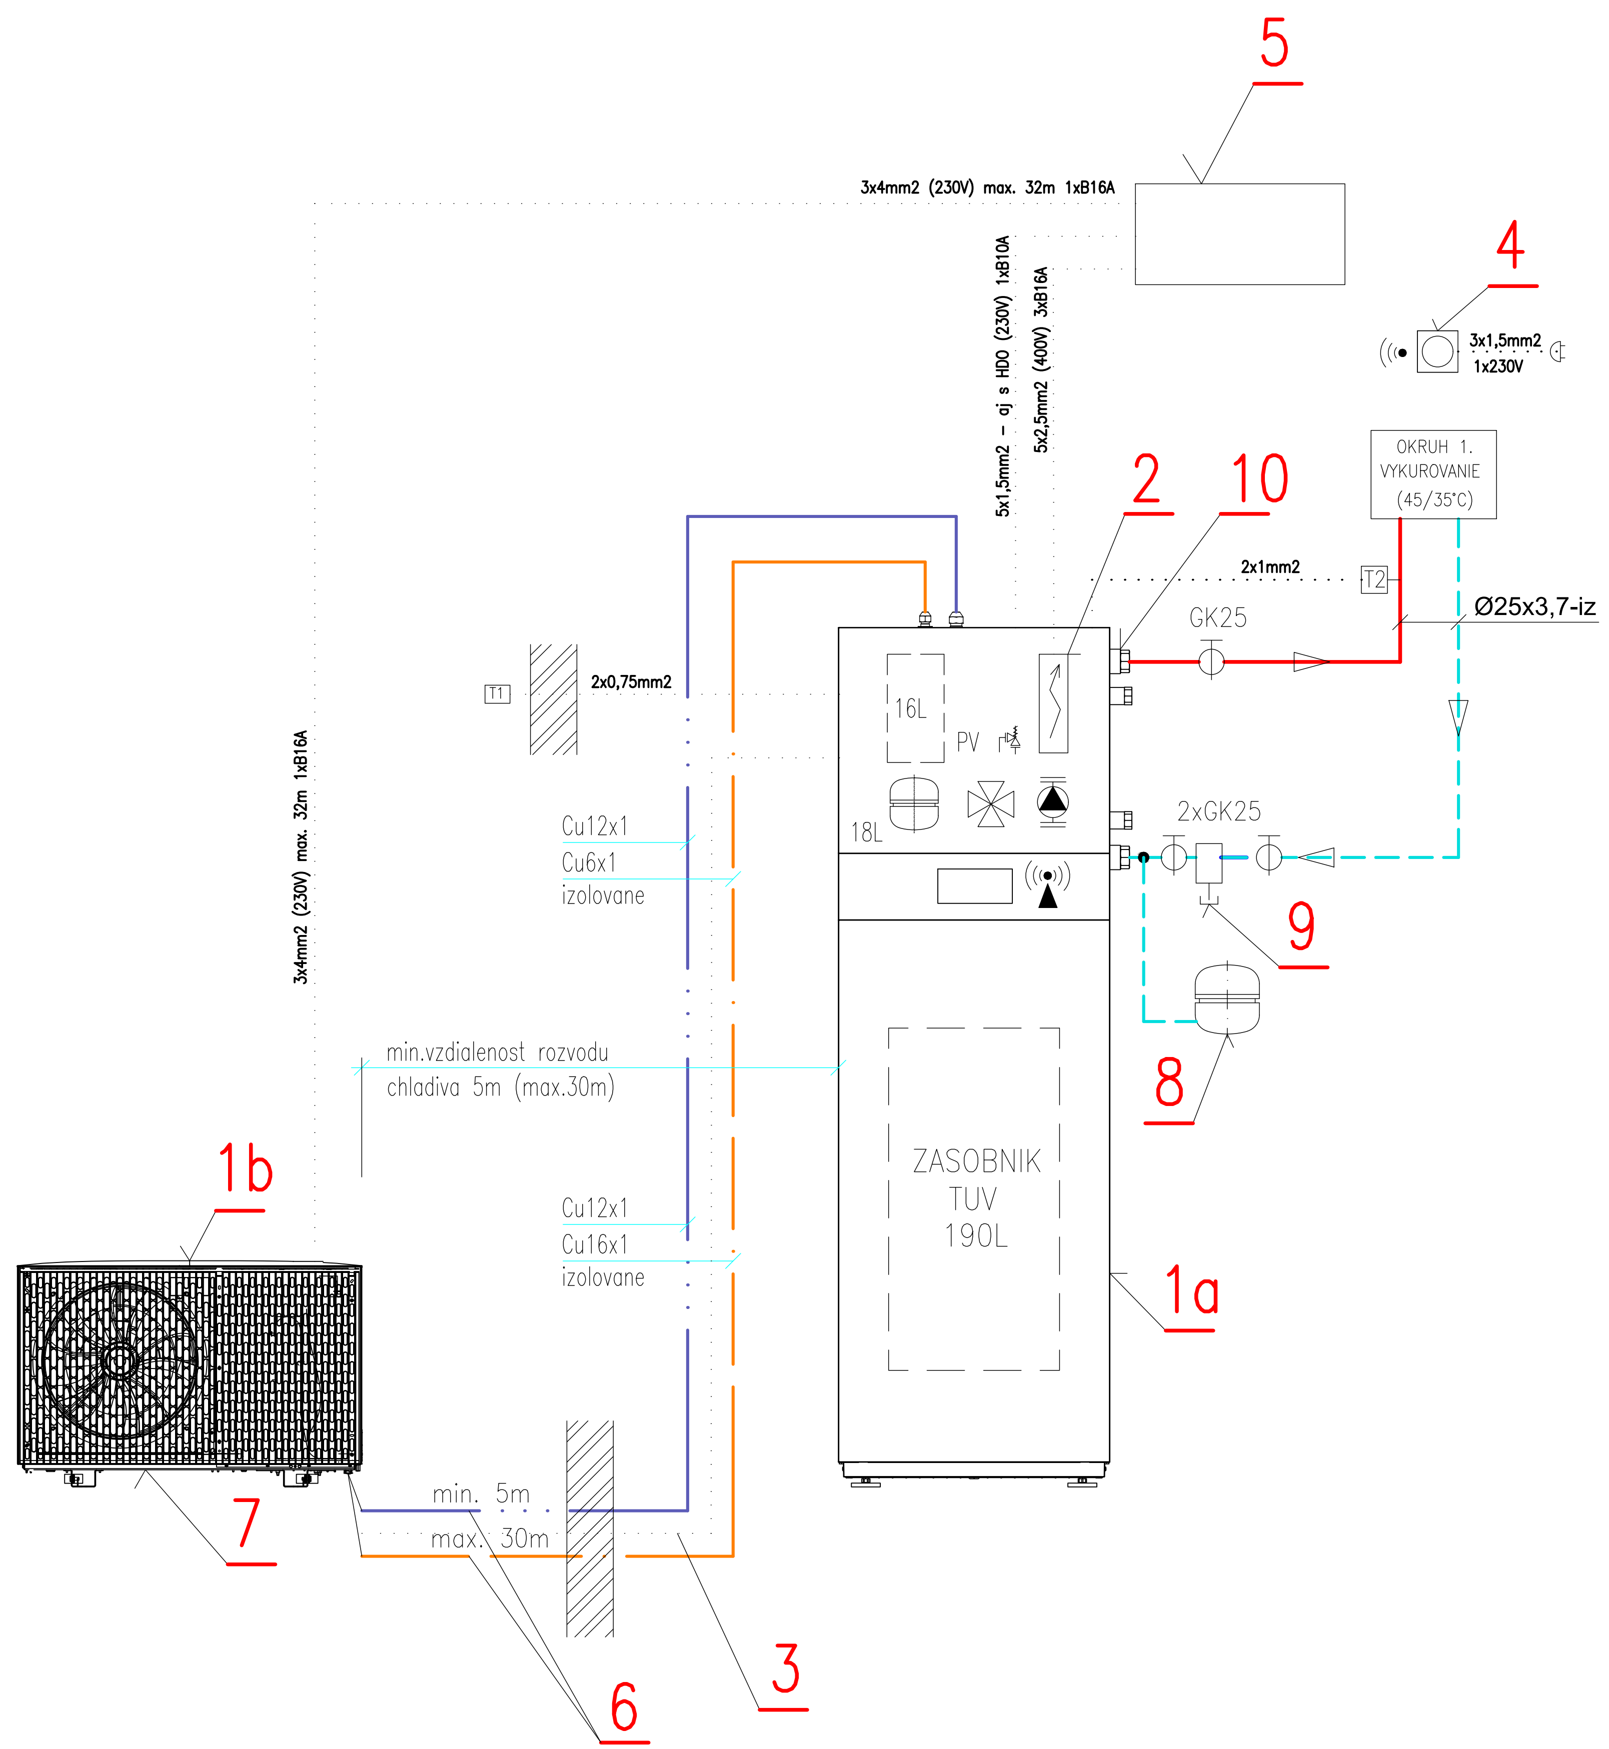

LEGENDA ZARIADENÍ:

POZ.	NÁZOV, ROZMER	P. KS
1a	VNUT. JEDNOTKA napr. VITOCAL 222-S AWBT-M-E-AC 221.E06	1
1b	VON. JEDNOTKA napr. VITOCAL 222-S AWBT-M-E-AC 221.E06 (230V)	1
	MAX.VÝSTUPNÁ TEPLOTA 60°C,TEPELNY VYKON 2,6-7,5kW A7/W35	
	EKOLOGICKE CHLADIVO R32, REGULÁCIA ONE-BASE,WIFI (Z022720)	
2	ELEKTRIC.PRIETOKOVY OHRIEVAC 8kW -v rozsahu dodavky pol.1a	1
3	CANBUS KOMUNIKACNY KABEL MEDZI JEDNOTKY 15m (ZK06217)	1
4	BEZDROTOVÉ DIALKOVE OVLADANIE VITOTROL 300-E (7959522)	1
5	ELEKTRICKY ROZVADZAC OBJEKTU	1
6	INSTALAC.SADA 12/6 NA ZEM+KONZOLA - 12,5M RURY (ZK06312)	1
7	ELEKTRIC.VYHREVNY PAS PRE VANU KONDENZATU 2,5m (ZK04098)	1
8	EXPANZNA NADOBA N25 OBJEM 25L, 3bar BIELA (7938081)	1
	NASTENNY DRZIAK PRE N25 (9572216)	1
9	ODKALOVAC S MAGNETOM A IZOLACIOU VITOTRAP 28mm (ZK04654)	1
10	PRIPOJOVACIA SADA NA OMIETKU-SPRAVA (ZK06403)-treba upresnit	1
T1	SNIMAC VONKAJSEJ TEPLOTY - v rozsahu dodavky tep.cerpadla	1
T2	SNIMAC ROSNEHO BODU - VLHKOSTI (7181418)	1

LEGENDA POTRUBÍ:

PLASTHLINÍKOVÉ POTRUBIE MATERIÁL: PE-XA/AL/PE NAPR. RAUTITAN STABIL, ZAIZOLOVANÉ POTRUBIE, TEPLOTNÝ SPÁD 45/35 °C.

MEDENÉ POTRUBIE PRIMÁRNEHO OKRUHU TEPELNÉHO ČERPADLA: CU Φ12×1, 6×1-IZ.

LEGENDA ARMATÚR :

GK	GUĽOVÝ KOHÚT SO ZÁVITOM
AOV	AUTOMATICKÝ ODVZDUŠŇOVACÍ VENTIL S UZATVÁRACOU ARMATÚROU
PV	POISTNÝ VENTIL SO ZÁVITOM

POZNÁMKY :

- V PRÍPADE AKÝCHKOĽVEK NEJASNOSTÍ V PROJEKTOVEJ DOKUMENTÁCII JE NUTNÉ KONTAKTOVAŤ ZODPOVEDNÉHO PROJEKTANTA.
- VŠETKY STAVEBNÉ ROZMERY A PRESTUPY JE POTREBNÉ OVERIŤ PRIAMO NA MIESTE REALIZÁCIE.
- PRED SAMOTNÝM SPUSTENÍM SYSTÉMU DO PREVÁDZKY SA MUSÍ VYKONAŤ DÔKLADNÝ PREPLACH ROZVODOV A VYČISTENIE VŠETKÝCH INŠTALOVANÝCH FILTROV.
- PO NAPUSTENÍ VYKUROVACEJ SÚSTAVY MÉDIOM JE NEVYHNUTNÉ ZABEZPEČIŤ JEJ POSTUPNÉ ODVZDUŠNENIE.
- ZHOTOVITEĽ JE POVINNÝ POSTUPOVAŤ V SÚLADE S PLATNÝMI NORMAMI STN EN A DODRŽIAVAŤ TECHNOLOGICKÉ AJ BEZPEČNOSTNÉ PREDPISY. ZÁROVEŇ MUSÍ REŠPEKTOVAŤ USTANOVENIA STN 730421 O ROZMEROVÝCH ODCHÝLKACH. KAŽDÚ ZMENU OPROTI PROJEKTU JE NUTNÉ VOPRED SKONZULTOVAŤ S HIP.
- OTVORY PRE PRESTUPY INŽINIERSKYCH SIETÍ A POTRUBNÝCH ROZVODOV V OBJEKTE JE POTREBNÉ PRIPRAVIŤ POČAS REALIZÁCIE HRUBEJ STAVBY.
- TÁTO DOKUMENTÁCIA NENAHRÁDZA REALIZAČNÚ DOKUMENTÁCIU STAVBY!
-VÝŠKOVÁ ÚROVEŇ ±0,000 V PROJEKTE ZODPOVEDÁ ÚROVNI FINÁLNEJ NÁŠĽAPNEJ VRSTVY PODLAHY.

TABUĽKA REVÍZIÍ

ČÍSLO REVÍZIE	DÁTUM	POPIS ZMENY	VYPRACOVAL

0,000=223,560 m n. m.

AUTOR PROJEKTU:	Ing. arch. Ivor Mečiar, Matúš Sorokáč
H.I.P.:	Ing. arch. Ivor Mečiar, ArtD.
ZODP. PROJEKTANT:	Ing. Ján Bátor
VYPRACOVAL:	

GENERÁLNY PROJEKTANT:
Alla s.r.o.
Riazanská 70/683
831 02 Bratislava
tel.: +421 907 693 679

INVESTOR:
NÁZOV PROJEKTU:
MIESTO STAVBY:
OBSAH VÝKRESU:
STAVEBNÝ OBJEKT:

ID STAVBY:	STUPEŇ PD:
---	PSI

NÁZOV VÝKRESU V ELEKTRONICK