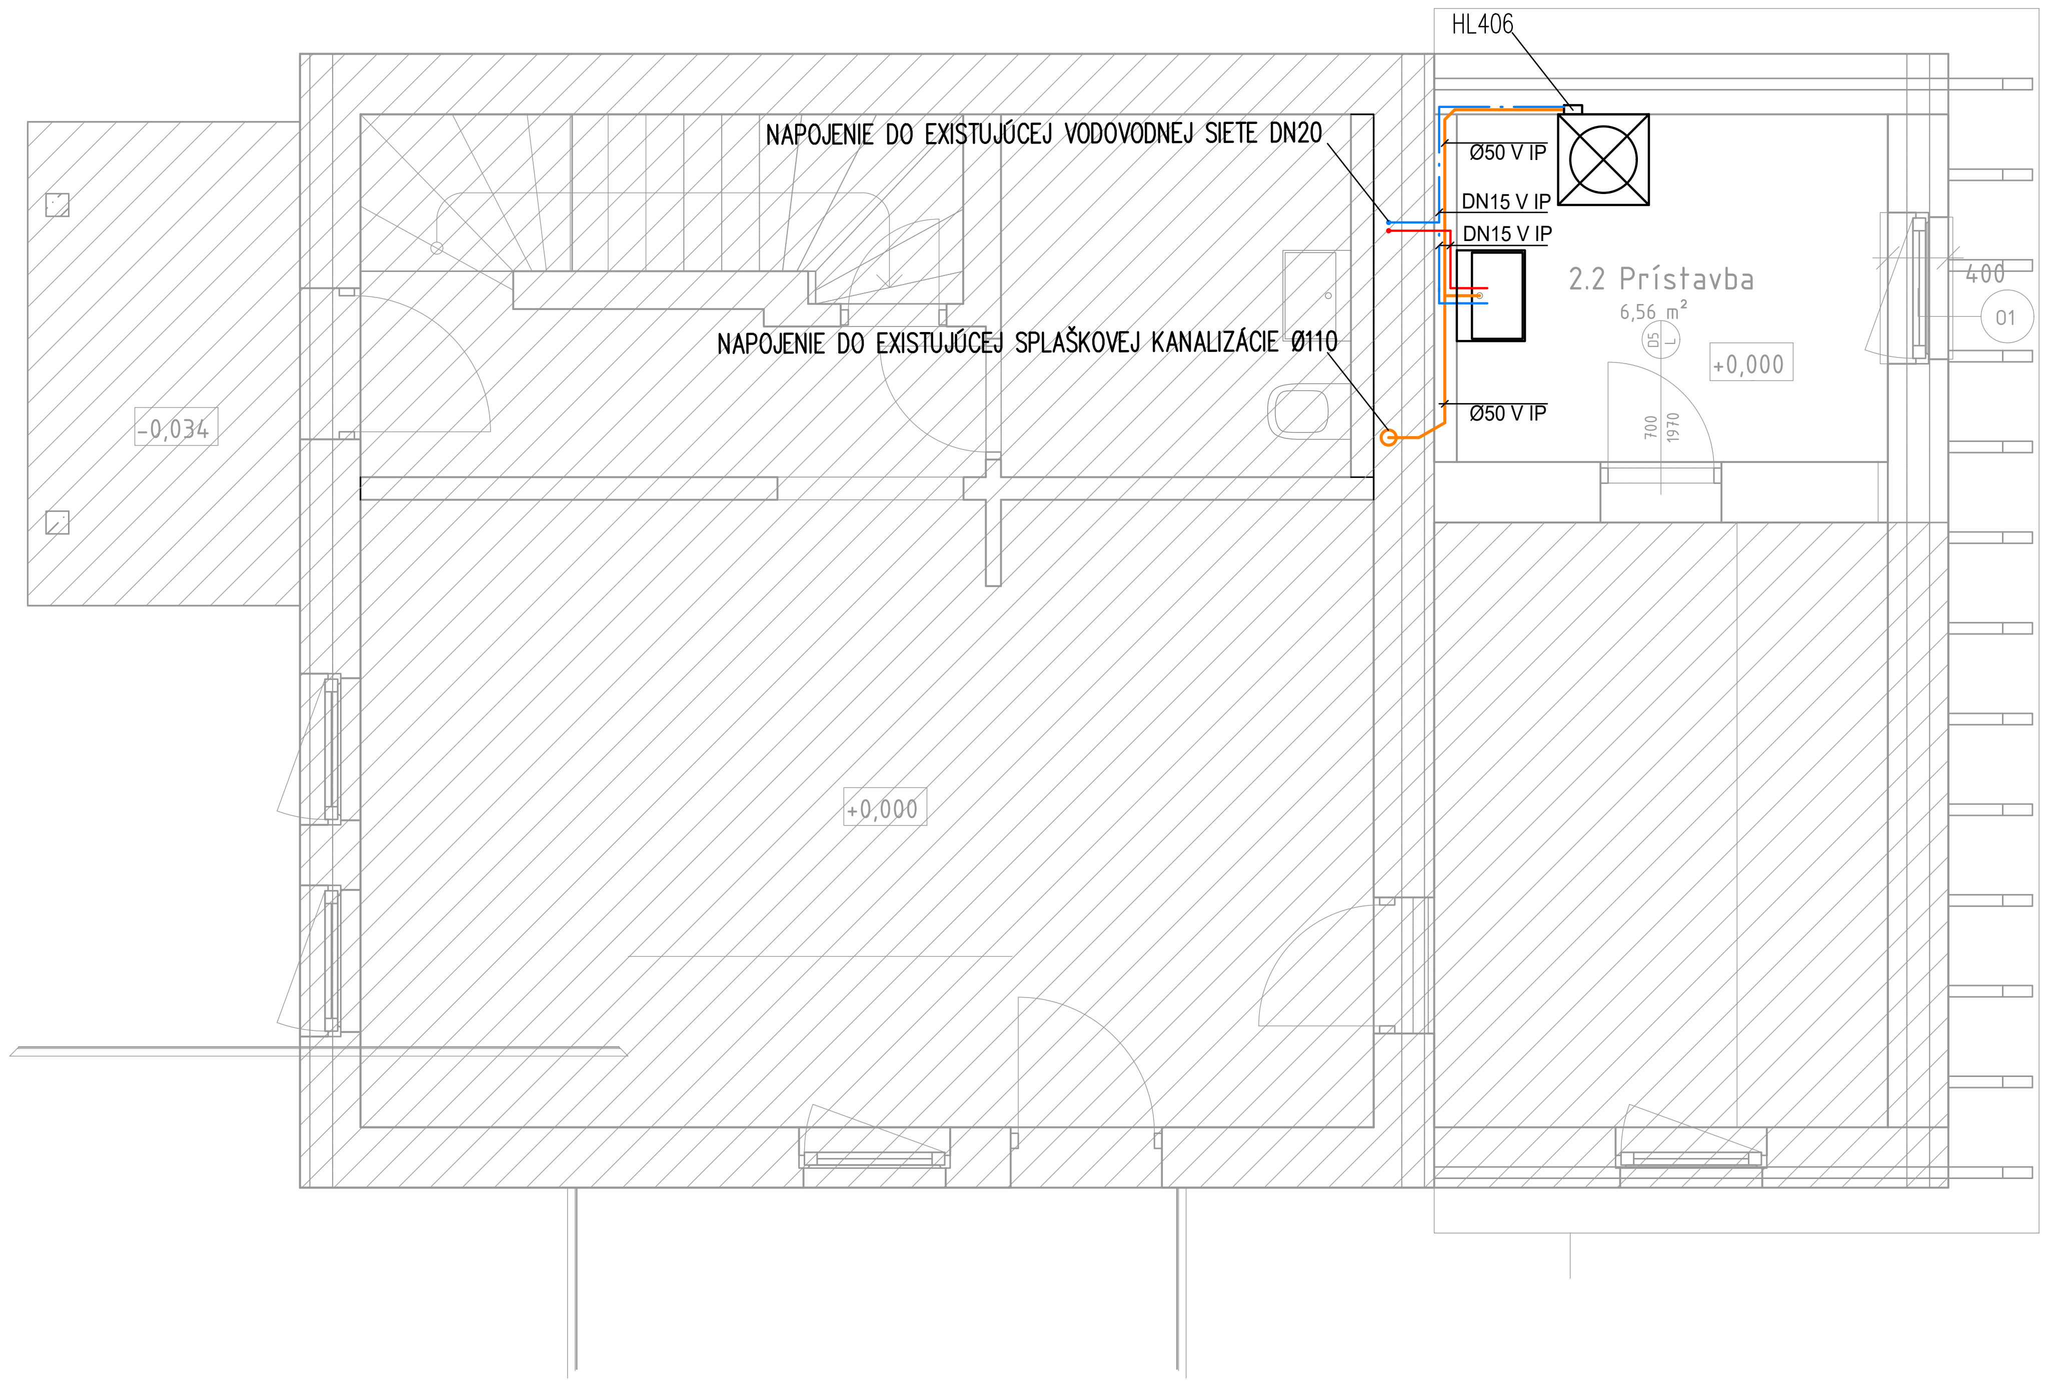
HL406
NAPOJENIE DO EXISTUJÚCEJ VODOVODNEJ SIETE DN20
Ø50 V IP
DN15 V IP
DN15 V IP
2.2 Prístavba
6,56 m²
NAPOJENIE DO EXISTUJÚCEJ SPLAŠKOVEJ KANALIZÁCIE Ø110
Ø50 V IP
+0,000
700
1970
400
01
-0,034
+0,000

LEGENDA

POTRUBIE HDPE–Al–PEXb napr. GEBERIT MEPLA – STUDENÁ VODA
+ PLASTOVÁ TEPELNÁ IZOLÁCIA napr. MIRELON

SPÁJANÉ LISOVANÍM, IZOLOVANÉ POTRUBIE
+ PLASTOVÁ TEPELNÁ IZOLÁCIA napr. MIRELON

POTRUBIE ODPADOVÉ HRDLOVÉ Z PP RÚR PRE VNÚTORNÚ KANALIZÁCIU
+ odporúčané vyhotoviť z odhlučneného potrubia vrátane objímok
napr. MASTER3, Geberit silent

U UMÝVADLO DITURVITOVÉ + PÁKOVÁ BATÉRIA STOJÁNKOVÁ
+ 2 x ROHOVÝ VENTIL DN 15

AP AUTOMATICKÁ PRÁČKA, HL406.1

POZNÁMKA :

- V PRÍPADE NEJASNOSTÍ VO VÝKRESOVEJ DOKUMENTÁCIÍ KONTAKTOVAŤ ZODPOVEDNÉHO PROJEKTANTA
- VŠETKY ROZMERY STAVEBNÝCH PRÁC KONTROLOVAŤ NA MIESTE STAVBY
- PRED UVEDENÍM SYSTÉMU DO PREVÁDZKY JE POTREBNÉ VYKONAŤ DÔKLADNÝ PREPLACH SYSTÉMU S VYČISTENÍM VŠETKÝCH FILTROV NA ROZVODE
- PO NAPUSTENÍ SYSTÉMU JE POTREBNÉ VYKONAŤ JEHO ODVZDUŠNENIE
- DODÁVATEL STAVBY JE POVINNÝ REALIZOVAŤ VŠETKY PRÁCE V ZMYSLE PLATNÝCH STN EN S DODRŽANÍM TECHNOLOGICKÝCH A BEZPEČNOSTNÝCH POSTUPOV. ĎALEJ JE POVINNÝ REŠPEKTOVAŤ USTANOVENIÁ STN 730421 O PRÍSLUŠNÝCH ROZMEROVÝCH ODCHÝLKACH REALIZOVANÝCH KONŠTRUKCIÍ PROTI PROJEKTOVANÉMU STAVU. KAŽDÚ ODCHÝLKU OD PROJEKTU JE POTREBNÉ PREROKOVAŤ S GP.
- PRESTUPY INŽINIERSKYCH SIETÍ A ROZVODOV V OBJEKTE JE POTREBNÉ VYNECHAŤ PRI REALIZÁCII STAVBY.
- DOKUMENTÁCIA SLÚŽI VÝHRADNE AKO PROJEKT PRE STAVEBNÝ ZÁMER A OVERENIE PROJEKTU STAVBY

TABULKA REVIZIÍ

ČÍSLO REVÍZIE	DÁTUM	POPIS ZMENY	VYPRACOVAL

0,000=132,6 m n. m.

AUTOR PROJEKTU:	Ing. arch. Ivor Mečiar ArtD.	GENERÁLNY PROJEKTANT: Alla s.r.o. Riazanská 70/683
H.I.P.:	Ing. arch. Ivor Mečiar ArtD.	
ZODP. PROJEKTANT		
VYPRACOVAL:		

INVESTOR:
NÁZOV PROJEKTU:
MIESTO STAVBY:
OBSAH VÝKRESU:
STAVEBNÝ OBJEKT:
ID STAVBY:
STUP
SZ
NÁZOV VÝKRESU V