LEGENDA MIESTNOSTI

M.č.	NÁZOV	PLOCHA (m2)	Teplota (°C)
A_1.01	Obývačka	41,32 m^2	
A_1.02	Vstup	16,25 m^2	
A_1.03	Izba	12,58 m^2	
A_1.04	Komora	2,83 m^2	
A_1.05	Technická miestnosť	3,32 m^2	
A_1.06	WC	1,63 m^2	
A_1.07	Izba	12,61 m^2	
A_1.08	Kúpeľňa	6,86 m^2	
A_1.09	Spálňa	13,36 m^2	
A_1.10	Izba	12,50 m^2	
A_1.11	Kúpeľňa	5,70 m^2	

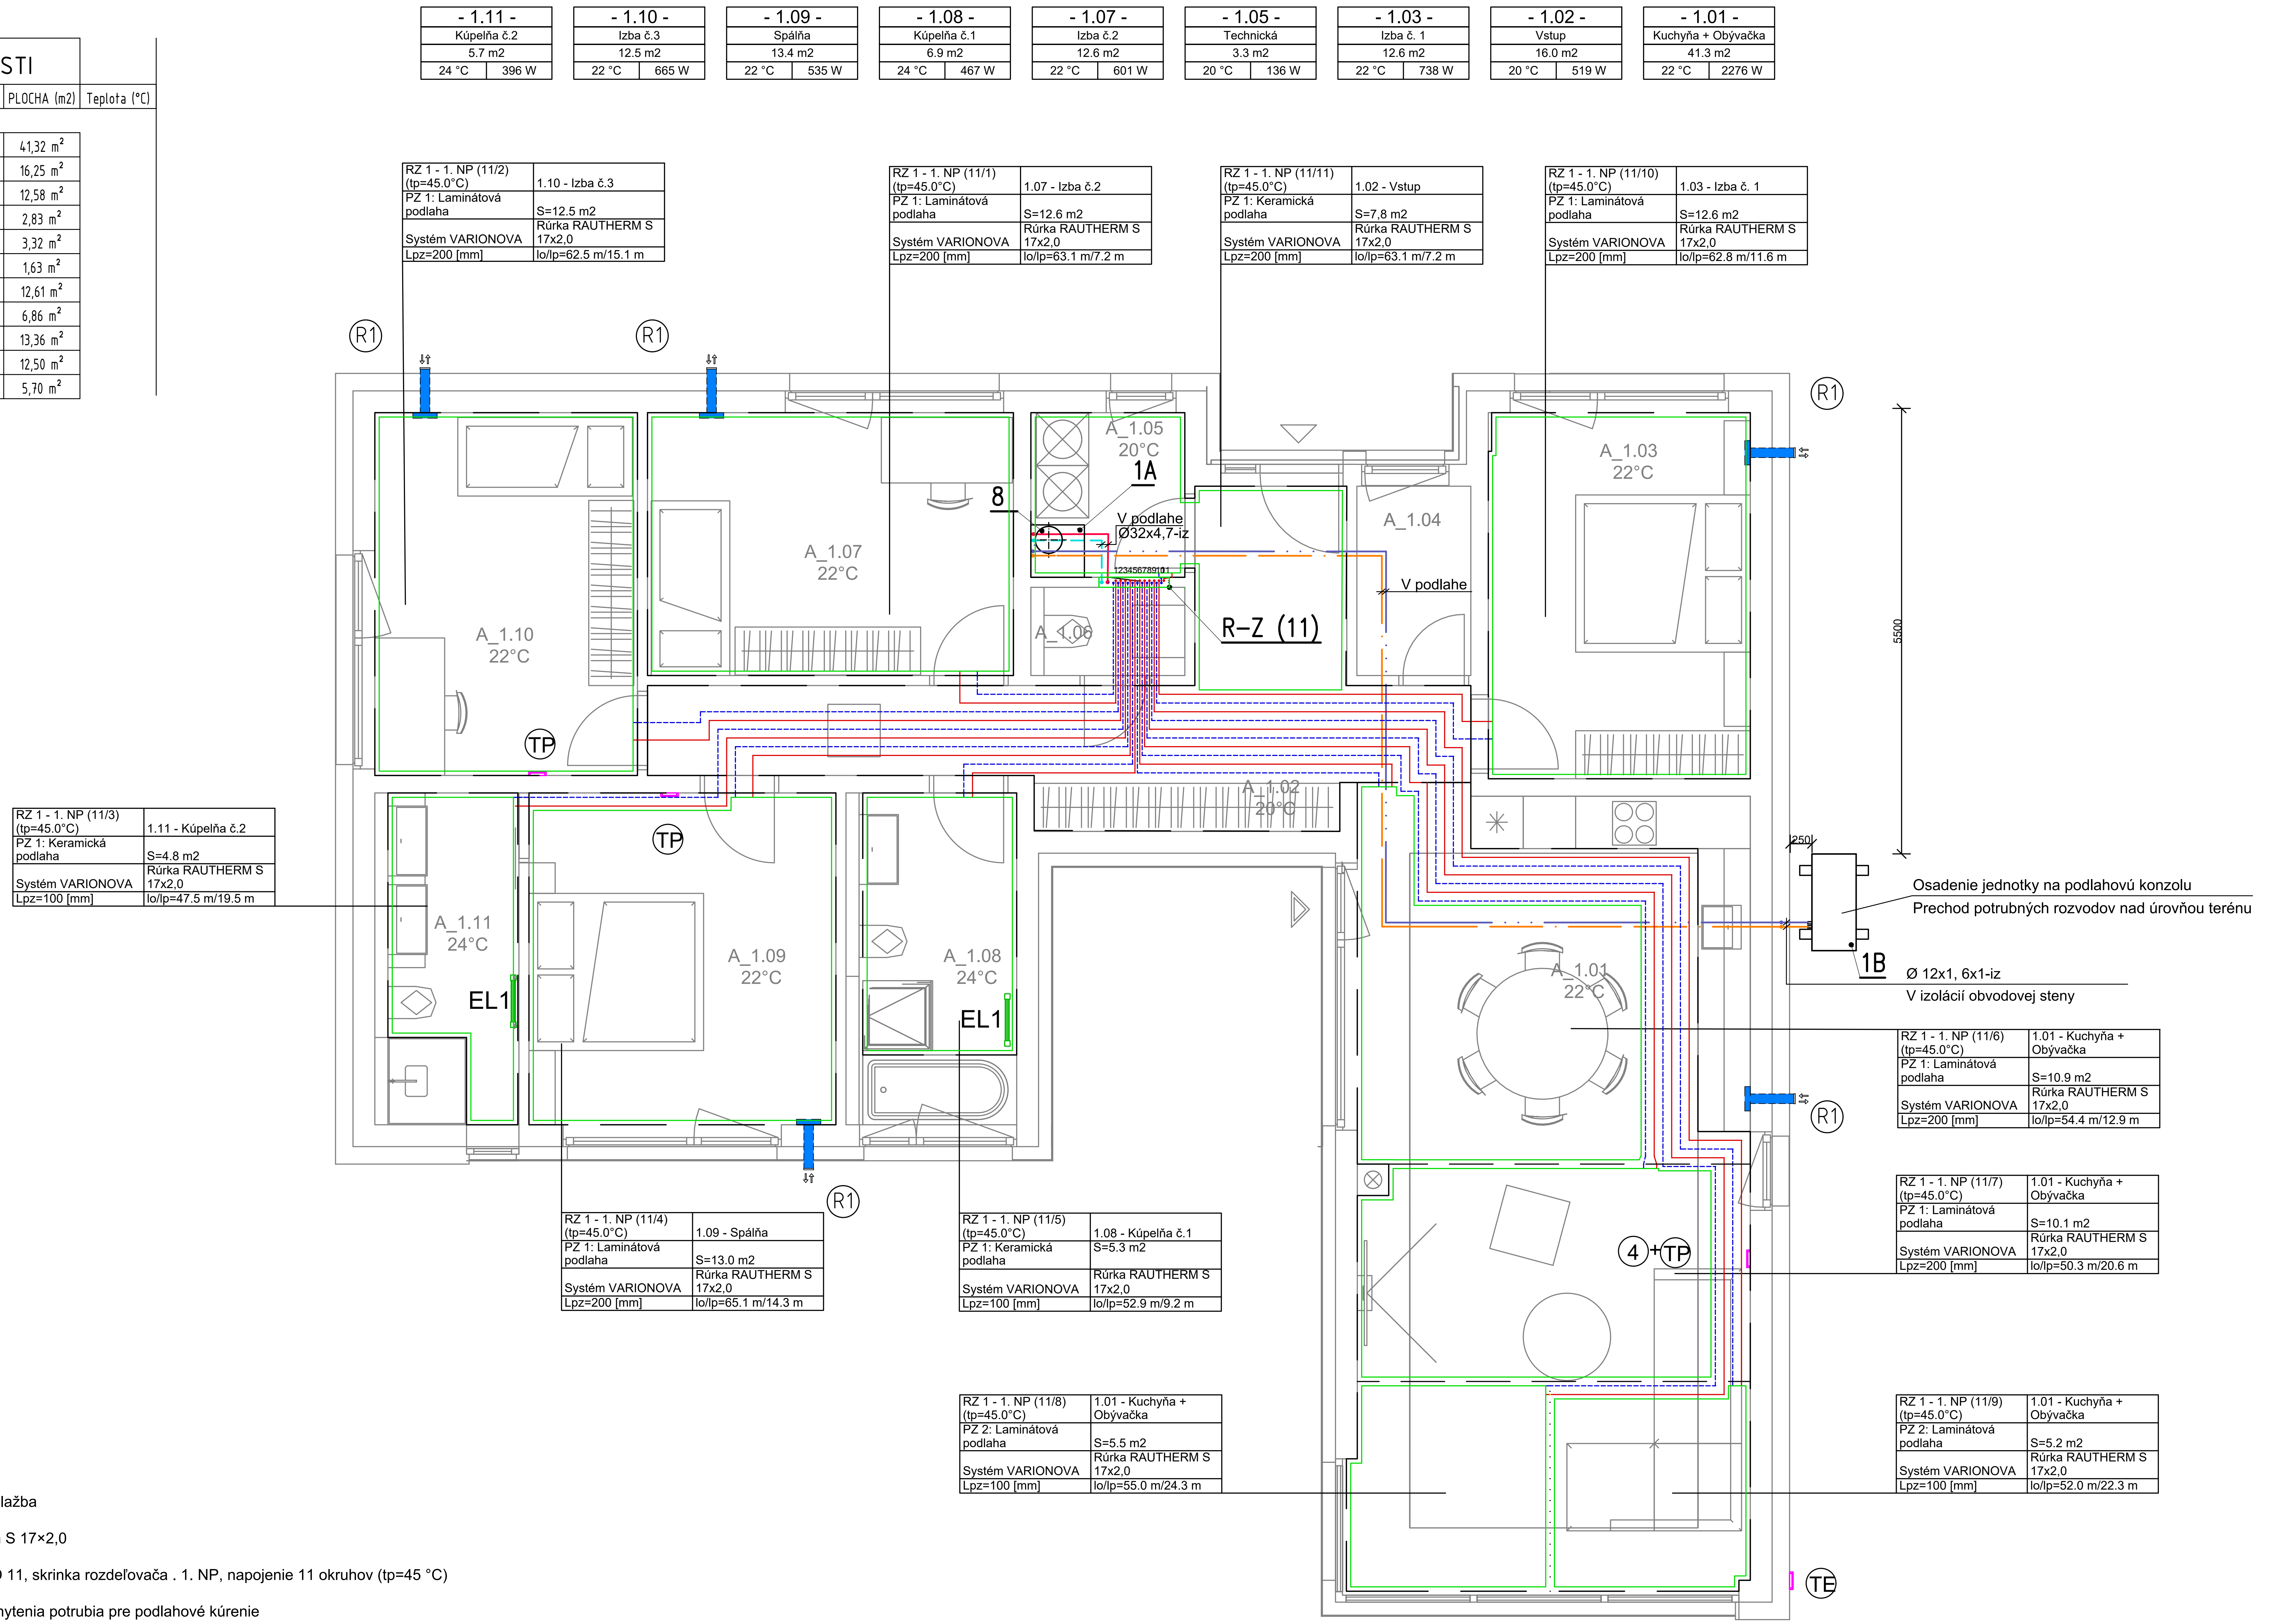

▭

Podlahové vykurovanie Rehau

Vykurovacia plocha: S=4.2 m²

Typ nášľapnej vrstvy (PX): Keramická dlažba

Typ vykurovacej rúrky: Rúrka Rautherm S 17×2,0

Rozdeľovač: Rozdeľovač Rehau HKV-D 11, skrinka rozdeľovača . 1. NP, napojenie 11 okruhov (tp=45 °C)

Systém uchytenia: Varionova – typ prichytenia potrubia pre podlahové kúrenie

LEGENDA POTRUBÍ:

🟥 🟦	Plasthliníkové potrubie napr. Rautherm S 17×2,0 Rehau pre podlahové vykurovanie, teplotný spád 45/35 °C, vedené v podlahe.
🟥 🟦	Plasthliníkové potrubie materiál: PE-Xa/AL/PE napr. Rautitan Stabil, zaizolované potrubie, teplotný spád 45/35 °C.
🟪 🟧	Medené potrubie primárneho okruhu tepelného čerpadla: Cu ϕ12×1, 6×1-iz.

LEGENDA ZARIADENÍ:

1A	Tepelné čerpadlo (vnútorná jednotka) napr.: Viessmann Vitocal 222-S (AWBT-M-E-AC 221.E06). Integrovaný zásobník na TV (190 l), napájanie 230V/50Hz. Hmotnosť: 188 kg.
1B	Tepelné čerpadlo (vonkajšia jednotka) napr.: Vitocal 222-S (vzduch-voda). Výkon (A7/W35): 2,6 – 7,5 kW, COP 4,95. Chladivo R32.
4	Ovládanie: Bezdrôtový diaľový ovládač napr. Vitotrol 300-E.
8	Expanzná nádoba napr: Viessmann N25 (objem 25 l, max. tlak 3 bar).
TP	Izbový regulátor napr.: REHAU Nea Smart 2.0 (meranie teploty).
TE	Snímač teploty exteriéru.
EL1	Elektrické vykurovacie teleso (rebrík) do kúpeľne, min. výkon 300 W (konkrétny model podľa výberu architekta).
R1	Lokálna rekuperačná jednotka napr.: korado korasmart tube 2400
R-Z	Zostava rozdeľovača podlahového vykurovania (teplotný spád 45/35 °C)

12-okruhový rozdeľovač napr. REHAU HKV-D 11, skrinka (rozmer 805 x 730 x 130 mm).
Ďiaľkové ovládanie termostatov napr. REHAU NEA (230V)

5 ks priestrový termostat napr. REHAU NEA (230V)

12 ks elektrický servo-pohon (230V)

POZNÁMKY :

- V prípade akýchkoľvek nejasností v projektovej dokumentácii je nutné kontaktovať zodpovedného projektanta.

- Všetky stavebné rozmery a prestupy je potrebné overiť priamo na mieste realizácie.

- Pred samotným spustením systému do prevádzky sa musí vykonať dôkladný preplach rozvodov a vyčistenie všetkých inštalovaných filtrov.

- Po napustení vykurovacej sústavy médiom je nevyhnutné zabezpečiť jej postupné odvzdušnenie.

- Zhotoviteľ je povinný postupovať v súlade s platnými normami STN EN a dodržiavať technologické aj bezpečnostné predpisy. Zároveň musí rešpektovať ustanovenia STN 730421 o rozmerových odchýlkach. Každú zmenu oproti projektu je nutné vopred skonzultovať s HIP.

- Otvory pre prestupy inžinierskych sietí a potrubných rozvodov v objekte je potrebné pripraviť počas realizácie hrubej stavby.

- Táto dokumentácia nenahrádza realizačnú dokumentáciu stavby!

-Výšková úroveň ±0,000 v projekte zodpovedá úrovni finálnej nášľapnej vrstvy podlahy.

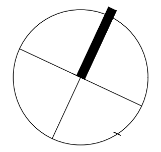

TABUĽKA REVÍZIÍ

ČÍSLO REVÍZIE	DÁTUM	POPIS ZMENY	VYPRACOVAL

0,000=+0,300 nad korunou komunikácie m n. m.

AUTOR PROJEKTU:	Ing. arch. Karol Kallay	GENERÁLNY PROJEKTANT: **Alla s.r.o.** Riazanská 70/683 831 02 Bratislava
H.I.P.:	Ing. arch Ivor Mečiar, ArtD.	
ZODP. PROJEKTANT:	Ing. Lukáš Skalík, PhD.	
VYPRACOVAL:	Bc.	

INVESTOR:	Tor
NÁZOV PROJEKTU:	**RI**
MIESTO STAVBY:	Cho
OBSAH VÝKRESU:	**PÔ**
STAVEBNÝ OBJEKT:	SO
ID STAVBY: --	STUPEŇ PD: PSP
NÁZOV VÝKRESU V ELEKTRONICKEJ POD	