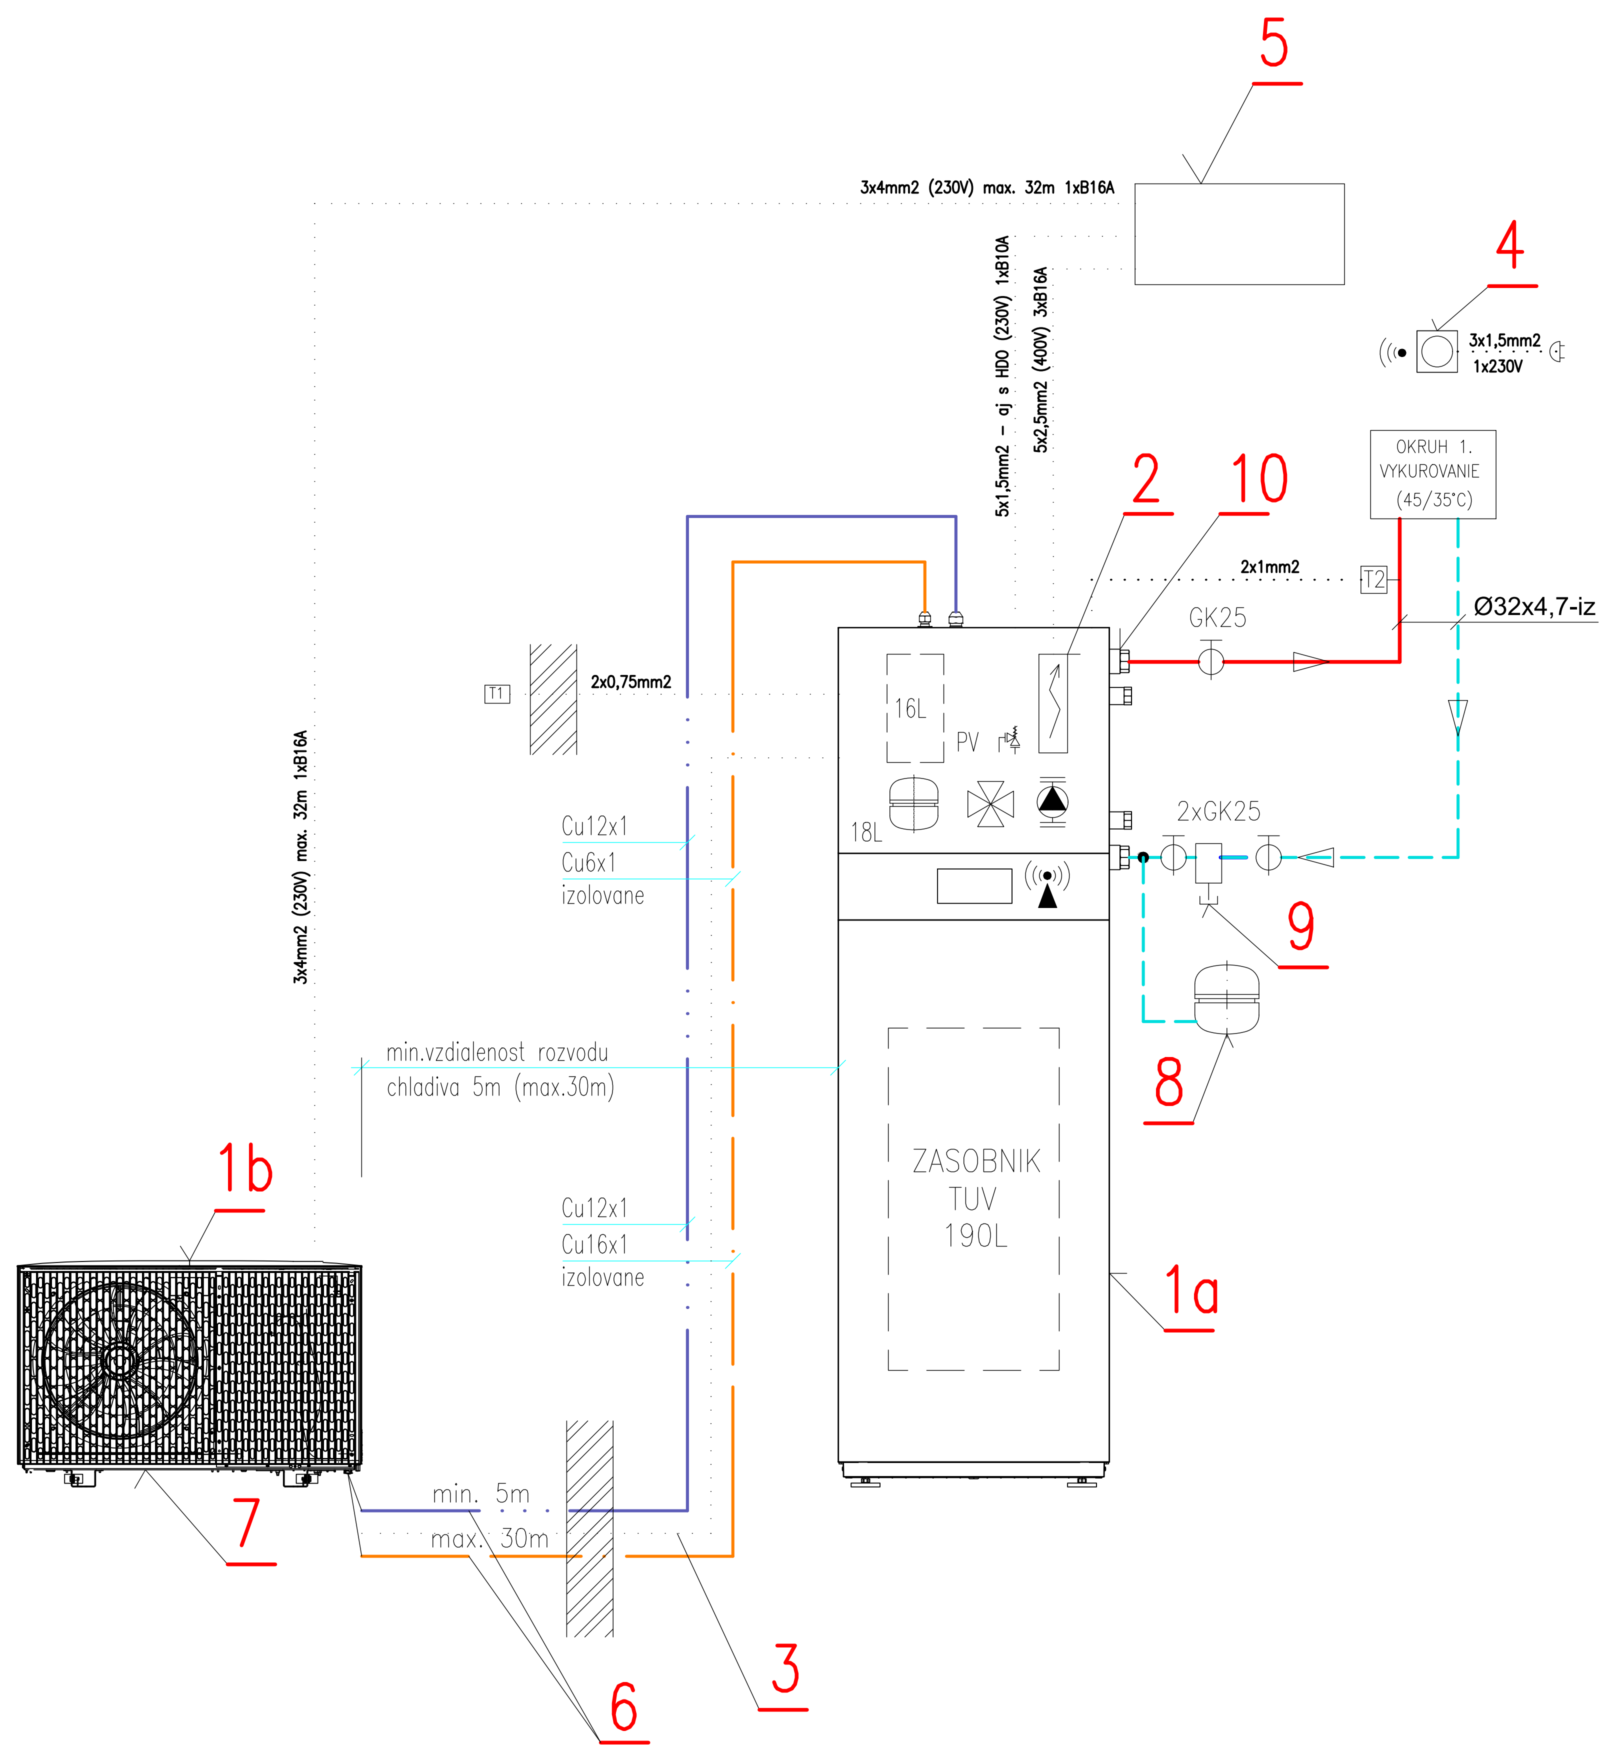
5
3x4mm2 (230V) max. 32m 1xB16A
5x1,5mm2 – aj s HDO (230V) 1xB10A
5x2,5mm2 (400V) 3xB16A
4
3x1,5mm2
1x230V
OKRUH 1. VYKUROVANIE (45/35°C)
2
10
2x1mm2
T2
GK25
Ø32x4,7-iz
T1
2x0,75mm2
16L
PV
18L
2xGK25
9
8
Cu12x1
Cu6x1
izolovane
3x4mm2 (230V) max. 32m 1xB16A
min.vzdialenost rozvodu
chladiva 5m (max.30m)
ZASOBNIK
TUV
190L
1b
1a
Cu12x1
Cu16x1
izolovane
min. 5m
max. 30m
7
6
3

LEGENDA ZARIADENÍ:

POZ.	NÁZOV, ROZMER	P. KS
1a	VNUT. JEDNOTKA napr. VITOCAL 222–S AWBT–M–E–AC 221.E06	1
1b	VON. JEDNOTKA napr. VITOCAL 222–S AWBT–M–E–AC 221.E06 (230V)	1
	MAX.VÝSTUPNÁ TEPLOTA 60°C,TEPELNY VYKON 2,6–7,5kW A7/W35	
	EKOLOGICKE CHLADIVO R32, REGULÁCIA ONE–BASE,WIFI (Z022720)	
2	ELEKTRIC.PRIETOKOVY OHRIEVAC 8kW –v rozsahu dodavky pol.1a	1
3	CANBUS KOMUNIKACNY KABEL MEDZI JEDNOTKY 15m (ZK06217)	1
4	BEZDROTOVÉ DIALKOVE OVLADANIE VITOTROL 300–E (7959522)	1
5	ELEKTRICKY ROZVADZAC OBJEKTU	1
6	INSTALAC.SADA 12/6 NA ZEM+KONZOLA – 12,5M RURY (ZK06312)	1
7	ELEKTRIC.VYHREVNY PAS PRE VANU KONDENZATU 2,5m (ZK04098)	1
8	EXPANZNA NADOBA N25 OBJEM 25L, 3bar BIELA (7938081)	1
	NASTENNY DRZIAK PRE N25 (9572216)	1
9	ODKALOVAC S MAGNETOM A IZOLACIOU VITOTRAP 28mm (ZK04654)	1
10	PRIPOJOVACIA SADA NA OMIETKU–SPRAVA (ZK06403)–treba upresnit	1
T1	SNIMAC VONKAJSEJ TEPLOTY – v rozsahu dodavky tep.cerpadla	1
T2	SNIMAC ROSNEHO BODU – VLHKOSTI (7181418)	1

LEGENDA POTRUBÍ:

▬ ▬ ▬	Plasthliníkové potrubie materiál: PE-Xa/AL/PE napr. Rautitan Stabil, zaizolované potrubie, teplotný spád 45/35 °C.
▬ · ▬	Medené potrubie primárneho okruhu tepelného čerpadla: Cu ϕ12×1, 6×1-iz.

LEGENDA ARMATÚR :

GK	Guľový kohút so závitom
AOV	Automatický odvzdušňovací ventil s uzatváracou armatúrou
PV	Poistný ventil so závitom

POZNÁMKY :

- V prípade akýchkoľvek nejasností v projektovej dokumentácii je nutné kontaktovať zodpovedného projektanta.

- Všetky stavebné rozmery a prestupy je potrebné overiť priamo na mieste realizácie.

- Pred samotným spustením systému do prevádzky sa musí vykonať dôkladný preplach rozvodov a vyčistenie všetkých inštalovaných filtrov.

- Po napustení vykurovacej sústavy médiom je nevyhnutné zabezpečiť jej postupné odvzdušnenie.

- Zhotoviteľ je povinný postupovať v súlade s platnými normami STN EN a dodržiavať technologické aj bezpečnostné predpisy. Zároveň musí rešpektovať ustanovenia STN 730421 o rozmerových odchýlkach. Každú zmenu oproti projektu je nutné vopred skonzultovať s HIP.

- Otvory pre prestupy inžinierskych sietí a potrubných rozvodov v objekte je potrebné pripraviť počas realizácie hrubej stavby.

- Táto dokumentácia nenahrádza realizačnú dokumentáciu stavby!

-Výšková úroveň ±0,000 v projekte zodpovedá úrovni finálnej nášľapnej vrstvy podlahy.

0,000=+0,300 nad korunou komunikácie m n. m.

AUTOR PROJEKTU: Ing. arch. Karol Kallay
H.I.P.: Ing. arch Ivor Mečiar, ArtD.
ZODP. PROJEKTANT: Ing. Lukáš Skalík, PhD.
VYPRACOVAL:

GENERÁLNY PROJEKTANT:
Alla s.r.o.
Riazanská 70/683
831 02 Bratislava
tel.: +421 907 693 679

INVESTOR:
NÁZOV PROJEKTU:
MIESTO STAVBY:
OBSAH VÝKRESU:
STAVEBNÝ OBJEKT:
ID STAVBY: --
STUPEŇ PD: PSP
NÁZOV VÝKRESU V ELEKTRONICKE

[redacted]