LEGENDA MIESTNOSTI

M.č.	NÁZOV	PLOCHA (m2)	Teplota (°C)
A_1.01	Obývačka	41,32 m^2	
A_1.02	Vstup	16,25 m^2	
A_1.03	Izba	12,58 m^2	
A_1.04	Komora	2,83 m^2	
A_1.05	Technická miestnosť	3,32 m^2	
A_1.06	WC	1,63 m^2	
A_1.07	Izba	12,61 m^2	
A_1.08	Kúpeľňa	6,86 m^2	
A_1.09	Spálňa	13,36 m^2	
A_1.10	Izba	12,50 m^2	
A_1.11	Kúpeľňa	5,70 m^2	

- 1.11 -	- 1.10 -	- 1.09 -	- 1.08 -	- 1.07 -	- 1.05 -	- 1.03 -	- 1.02 -	- 1.01 -
Kúpelňa č.2	Izba č.3	Spálňa	Kúpelňa č.1	Izba č.2	Technická	Izba č. 1	Vstup	Kuchyňa + Obývačka
5.7 m2	12.5 m2	13.4 m2	6.9 m2	12.6 m2	3.3 m2	12.6 m2	16.0 m2	41.3 m2
24 °C / 396 W	22 °C / 665 W	22 °C / 535 W	24 °C / 467 W	22 °C / 601 W	20 °C / 136 W	22 °C / 738 W	20 °C / 519 W	22 °C / 2276 W

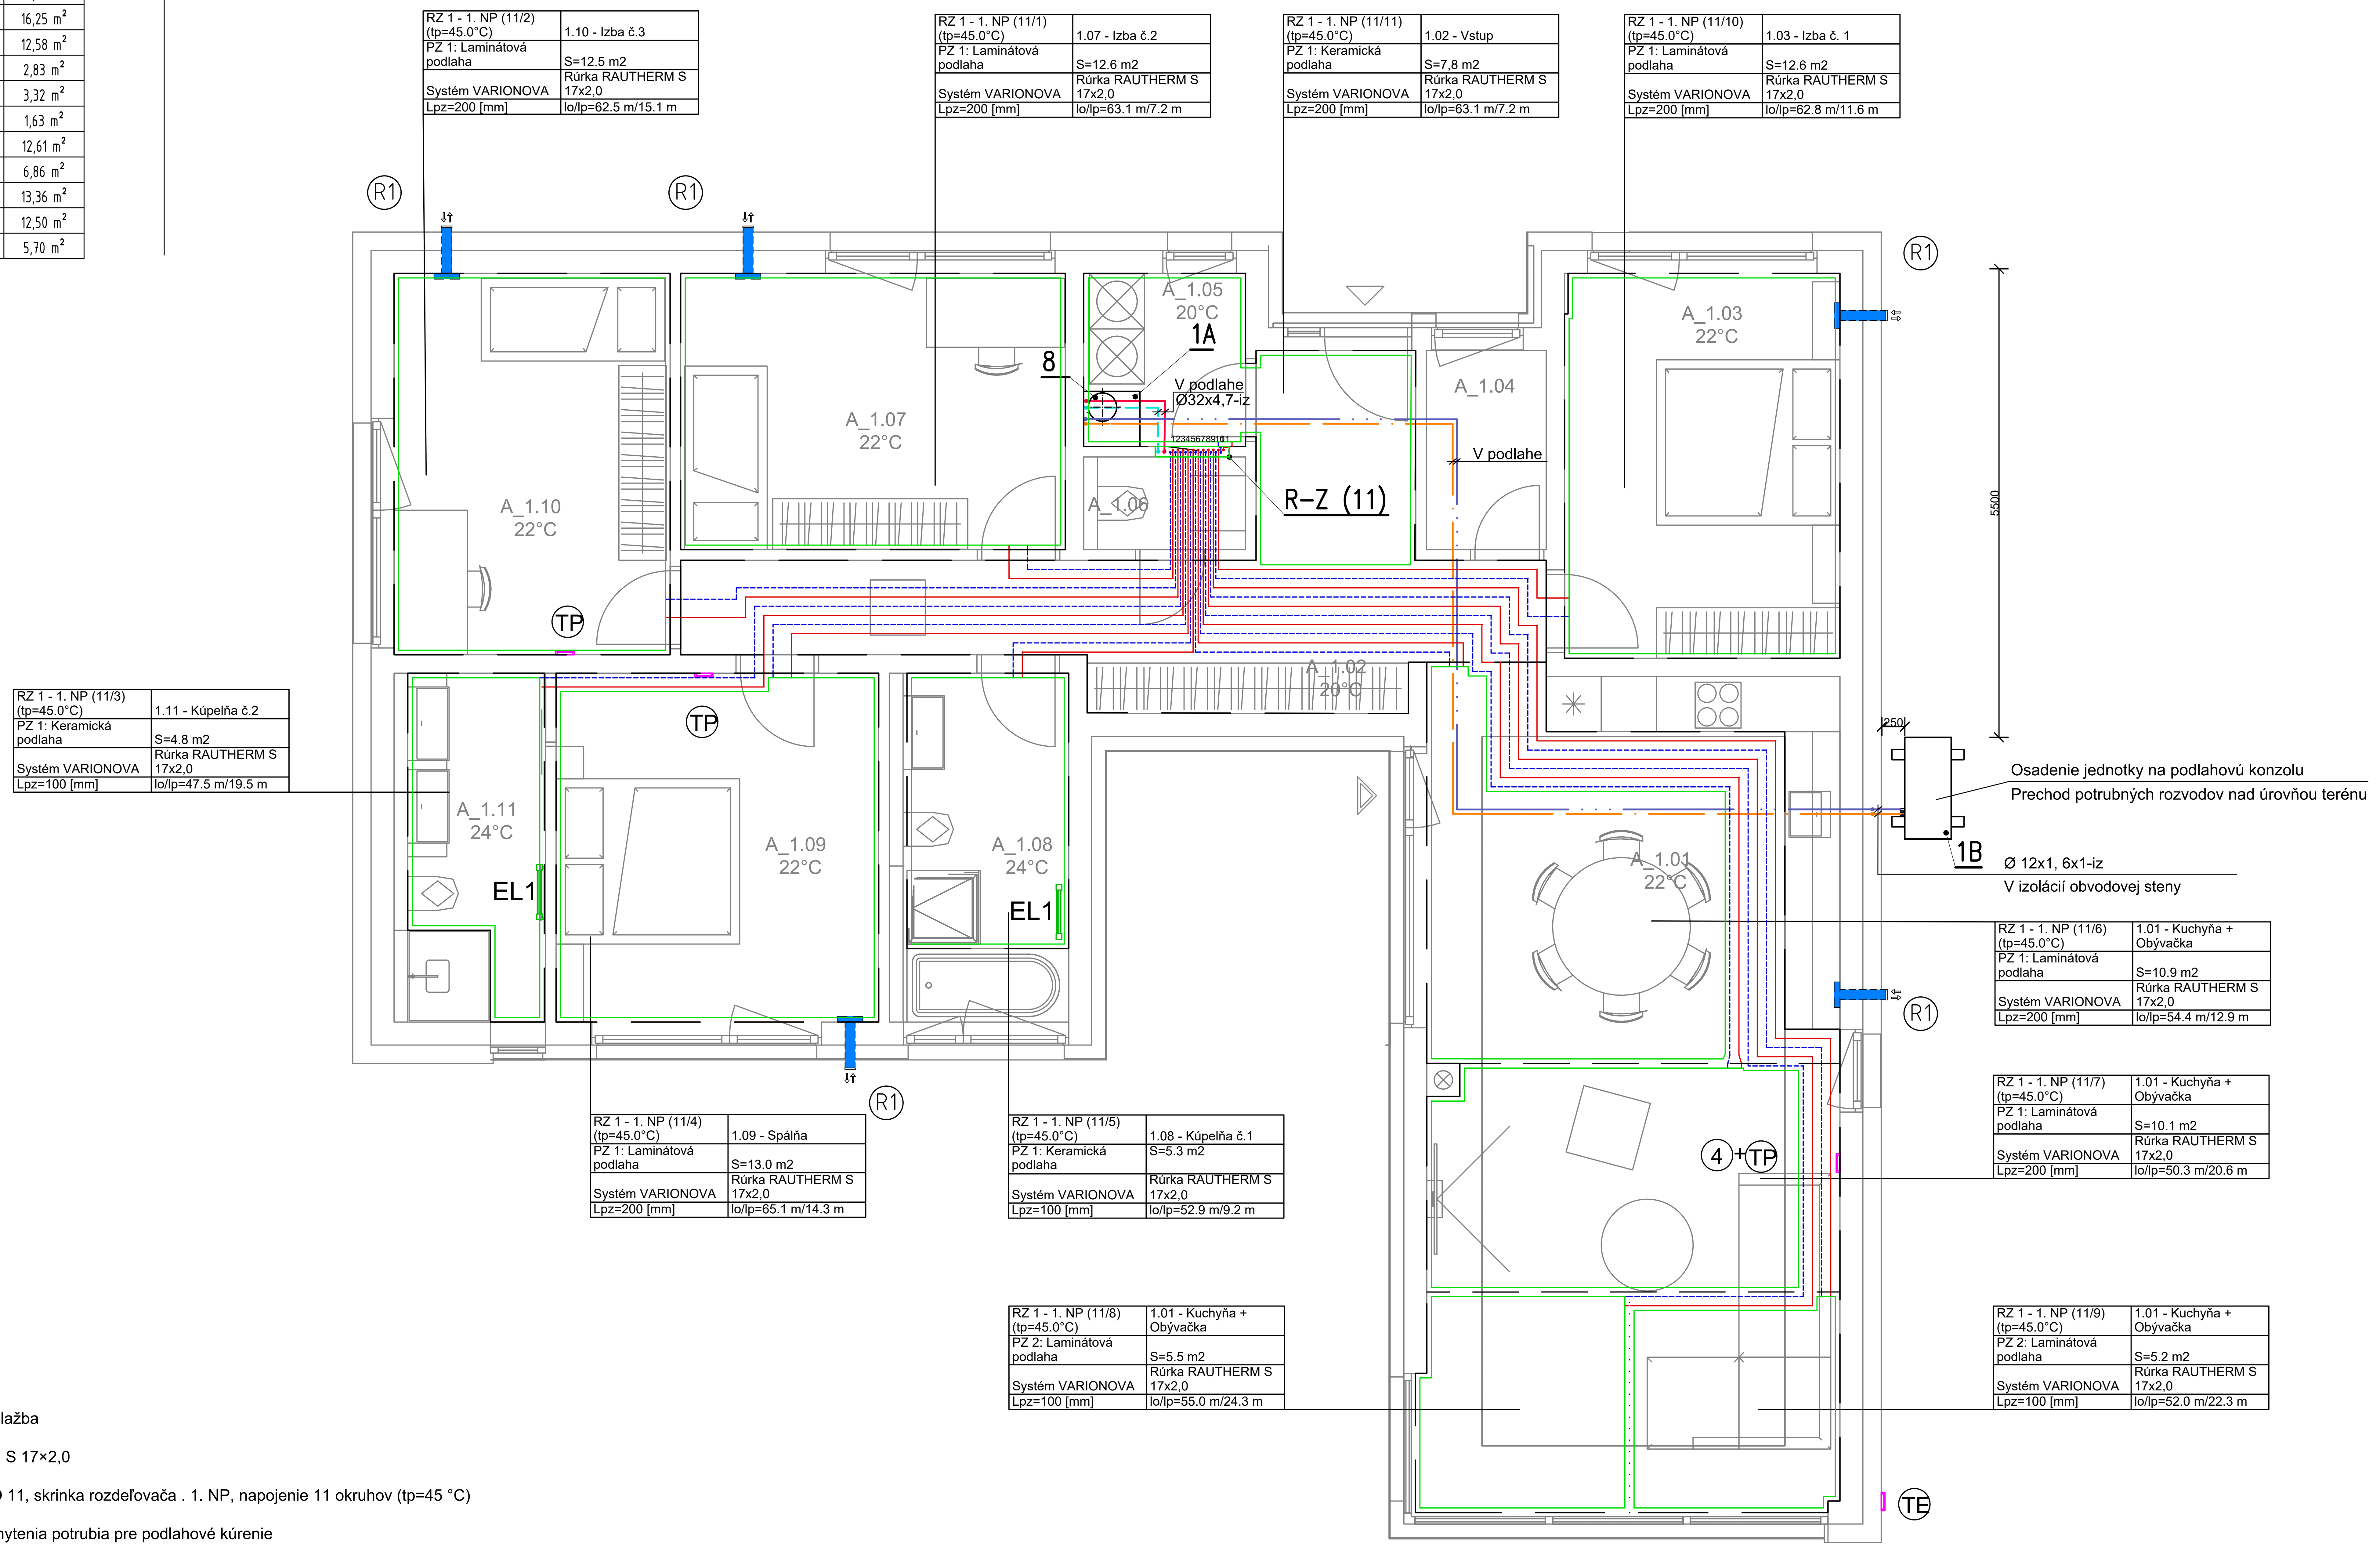

RZ 1 - 1. NP (11/2) (tp=45.0°C)	1.10 - Izba č.3
PZ 1: Laminátová podlaha	S=12.5 m2
Systém VARIONOVA	Rúrka RAUTHERM S 17x2,0
Lpz=200 [mm]	lo/lp=62.5 m/15.1 m

RZ 1 - 1. NP (11/1) (tp=45.0°C)	1.07 - Izba č.2
PZ 1: Laminátová podlaha	S=12.6 m2
Systém VARIONOVA	Rúrka RAUTHERM S 17x2,0
Lpz=200 [mm]	lo/lp=63.1 m/7.2 m

RZ 1 - 1. NP (11/11) (tp=45.0°C)	1.02 - Vstup
PZ 1: Keramická podlaha	S=7,8 m2
Systém VARIONOVA	Rúrka RAUTHERM S 17x2,0
Lpz=200 [mm]	lo/lp=63.1 m/7.2 m

RZ 1 - 1. NP (11/10) (tp=45.0°C)	1.03 - Izba č. 1
PZ 1: Laminátová podlaha	S=12.6 m2
Systém VARIONOVA	Rúrka RAUTHERM S 17x2,0
Lpz=200 [mm]	lo/lp=62.8 m/11.6 m

RZ 1 - 1. NP (11/3) (tp=45.0°C)	1.11 - Kúpelňa č.2
PZ 1: Keramická podlaha	S=4.8 m2
Systém VARIONOVA	Rúrka RAUTHERM S 17x2,0
Lpz=100 [mm]	lo/lp=47.5 m/19.5 m

RZ 1 - 1. NP (11/6) (tp=45.0°C)	1.01 - Kuchyňa + Obývačka
PZ 1: Laminátová podlaha	S=10.9 m2
Systém VARIONOVA	Rúrka RAUTHERM S 17x2,0
Lpz=200 [mm]	lo/lp=54.4 m/12.9 m

RZ 1 - 1. NP (11/4) (tp=45.0°C)	1.09 - Spálňa
PZ 1: Laminátová podlaha	S=13.0 m2
Systém VARIONOVA	Rúrka RAUTHERM S 17x2,0
Lpz=200 [mm]	lo/lp=65.1 m/14.3 m

RZ 1 - 1. NP (11/5) (tp=45.0°C)	1.08 - Kúpelňa č.1
PZ 1: Keramická podlaha	S=5.3 m2
Systém VARIONOVA	Rúrka RAUTHERM S 17x2,0
Lpz=100 [mm]	lo/lp=52.9 m/9.2 m

RZ 1 - 1. NP (11/7) (tp=45.0°C)	1.01 - Kuchyňa + Obývačka
PZ 1: Laminátová podlaha	S=10.1 m2
Systém VARIONOVA	Rúrka RAUTHERM S 17x2,0
Lpz=200 [mm]	lo/lp=50.3 m/20.6 m

RZ 1 - 1. NP (11/8) (tp=45.0°C)	1.01 - Kuchyňa + Obývačka
PZ 2: Laminátová podlaha	S=5.5 m2
Systém VARIONOVA	Rúrka RAUTHERM S 17x2,0
Lpz=100 [mm]	lo/lp=55.0 m/24.3 m

RZ 1 - 1. NP (11/9) (tp=45.0°C)	1.01 - Kuchyňa + Obývačka
PZ 2: Laminátová podlaha	S=5.2 m2
Systém VARIONOVA	Rúrka RAUTHERM S 17x2,0
Lpz=100 [mm]	lo/lp=52.0 m/22.3 m

Podlahové vykurovanie Rehau

Vykurovacia plocha: S=4.2 m²

Typ nášľapnej vrstvy (PX): Keramická dlažba

Typ vykurovacej rúrky: Rúrka Rautherm S 17×2,0

Rozdeľovač: Rozdeľovač Rehau HKV-D 11, skrinka rozdeľovača . 1. NP, napojenie 11 okruhov (tp=45 °C)

Systém uchytenia: Varionova – typ prichytenia potrubia pre podlahové kúrenie

LEGENDA POTRUBÍ:

Plasthliníkové potrubie napr. Rautherm S 17×2,0 Rehau pre podlahové vykurovanie, teplotný spád 45/35 °C, vedené v podlahe.

Plasthliníkové potrubie materiál: PE-Xa/AL/PE napr. Rautitan Stabil, zaizolované potrubie, teplotný spád 45/35 °C.

Medené potrubie primárneho okruhu tepelného čerpadla: Cu ϕ12×1, 6×1-iz.

LEGENDA ZARIADENÍ:

1A	Tepelné čerpadlo (vnútorná jednotka) napr.: Viessmann Vitocal 222-S (AWBT-M-E-AC 221.E06). Integrovaný zásobník na TV (190 l), napájanie 230V/50Hz. Hmotnosť: 188 kg.
1B	Tepelné čerpadlo (vonkajšia jednotka) napr.: Vitocal 222-S (vzduch-voda). Výkon (A7/W35): 2,6 – 7,5 kW, COP 4,95. Chladivo R32.
4	Ovládanie: Bezdrôtový diaľový ovládač napr. Vitotrol 300-E.
8	Expanzná nádoba napr: Viessmann N25 (objem 25 l, max. tlak 3 bar).
TP	Izbový regulátor napr.: REHAU Nea Smart 2.0 (meranie teploty).
TE	Snímač teploty exteriéru.
EL1	Elektrické vykurovacie teleso (rebrík) do kúpeľne, min. výkon 300 W (konkrétny model podľa výberu architekta).
R1	Lokálna rekuperačná jednotka napr.: korado korasmart tube 2400
R-Z	Zostava rozdeľovača podlahového vykurovania (teplotný spád 45/35 °C)

12-okruhový rozdeľovač napr. REHAU HKV-D 11, skrinka (rozmer 805 x 730 x 130 mm).
Ďiaľkové ovládanie termostatov napr. REHAU NEA (230V)

5 ks priestrový termostat napr. REHAU NEA (230V)

12 ks elektrický servo-pohon (230V)

POZNÁMKY :

- V prípade akýchkoľvek nejasností v projektovej dokumentácii je nutné kontaktovať zodpovedného projektanta.
- Všetky stavebné rozmery a prestupy je potrebné overiť priamo na mieste realizácie.
- Pred samotným spustením systému do prevádzky sa musí vykonať dôkladný preplach rozvodov a vyčistenie všetkých inštalovaných filtrov.
- Po napustení vykurovacej sústavy médiom je nevyhnutné zabezpečiť jej postupné odvzdušnenie.
- Zhotoviteľ je povinný postupovať v súlade s platnými normami STN EN a dodržiavať technologické aj bezpečnostné predpisy. Zároveň musí rešpektovať ustanovenia STN 730421 o rozmerových odchýlkach. Každú zmenu oproti projektu je nutné vopred skonzultovať s HIP.
- Otvory pre prestupy inžinierskych sietí a potrubných rozvodov v objekte je potrebné pripraviť počas realizácie hrubej stavby.
- Táto dokumentácia nenahrádza realizačnú dokumentáciu stavby!
- -Výšková úroveň ±0,000 v projekte zodpovedá úrovni finálnej nášľapnej vrstvy podlahy.

TABUĽKA REVÍZIÍ

ČÍSLO REVÍZIE	DÁTUM	POPIS ZMENY	VYPRACOVAL

0,000=+0,300 nad korunou komunikácie m n. m.

AUTOR PROJEKTU:	Ing. arch. Karol Kallay	GENERÁLNY PROJEKTANT: **Alla s.r.o.** Riazanská 70/683 831 02 Bratislava
H.I.P.:	Ing. arch Ivor Mečiar, ArtD.	
ZODP. PROJEKTANT:	Ing. Lukáš Skalík, PhD.	
VYPRACOVAL:	Bc.	
INVESTOR:	Tor	
NÁZOV PROJEKTU:	**RI**	
MIESTO STAVBY:	Cho	
OBSAH VÝKRESU:	**PÔ**	
STAVEBNÝ OBJEKT:	SO	
ID STAVBY: --	STUPEŇ PD: PSP	
NÁZOV VÝKRESU V ELEKTRONICKEJ POD		