R-Z ZOSTAVA ROZDEĽOVAČA PODLAHOVÉHO VYKUROVANIA (TEPLOTNÝ SPÁD 45/32,5 °C)

14-OKRUHOVÝ ROZDEĽOVAČ NAPR. REHAU HKVD SX-AG 14, SKRINKA (ROZMER 620 X 1150 X 110 MM).
ĎIAĽKOVÉ OVLÁDANIE TERMOSTATOV NAPR. REHAU NEA (230V)

5 KS PRIESTROVÝ TERMOSTAT NAPR. REHAU NEA (230V)

14 KS ELEKTRICKÝ SERVO-POHON (230V)

TABUĽKA MIESTNOSTÍ 1.NP

Č. MIESTNOSTI	NÁZOV MIESTNOSTI	PLOCHA (m2)
1.01	VSTUPNÁ CHODBA	6,06
1.02	CHODBA	12,30
1.03	KÚPEĽŇA	6,13
1.04	KÚPEĽŇA	4,34
1.05	ŠATNÍK + CHODBA	10,13
1.06	SPÁLŇA	13,36
1.07	IZBA	10,95
1.08	IZBA	10,95
1.09	RELAX MIESTNOSŤ	19,71
1.10	TECH. MIESTNOSŤ	3,69
1.11	ŠPAJZ	3,68
1.12	KUCHYŇA	12,10
1.13	OBÝVACIA MIESTNOSŤ	32,00
1.14	TERASA	37,14
		182,52 m²

DETAIL NAPOJENIA VYKUROVACÍCH TELIES

REBRÍKOVÉ VYKUROVACIE TELESO

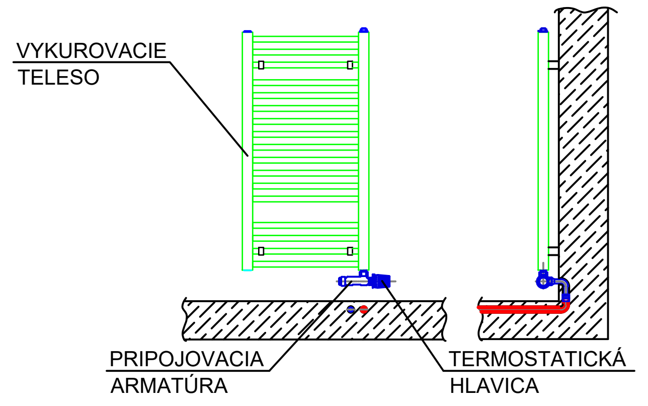
VYKUROVACIE TELESO
PRIPOJOVACIA ARMATÚRA
TERMOSTATICKÁ HLAVICA

Podlahové vykurovanie Rehau

Vykurovacia plocha: S=4.2 m²

Typ nášľapnej vrstvy (PX): Keramická dlažba

Typ vykurovacej rúrky: Rúrka Rautherm S 17×2,0

Rozdeľovač: Rozdeľovač Rehau , skrinka rozdeľovača 1. NP, napojenie 14 okruhov (tp=45 °C)

Systém uchytenia: Varionova – typ prichytenia potrubia pre podlahové kúrenie

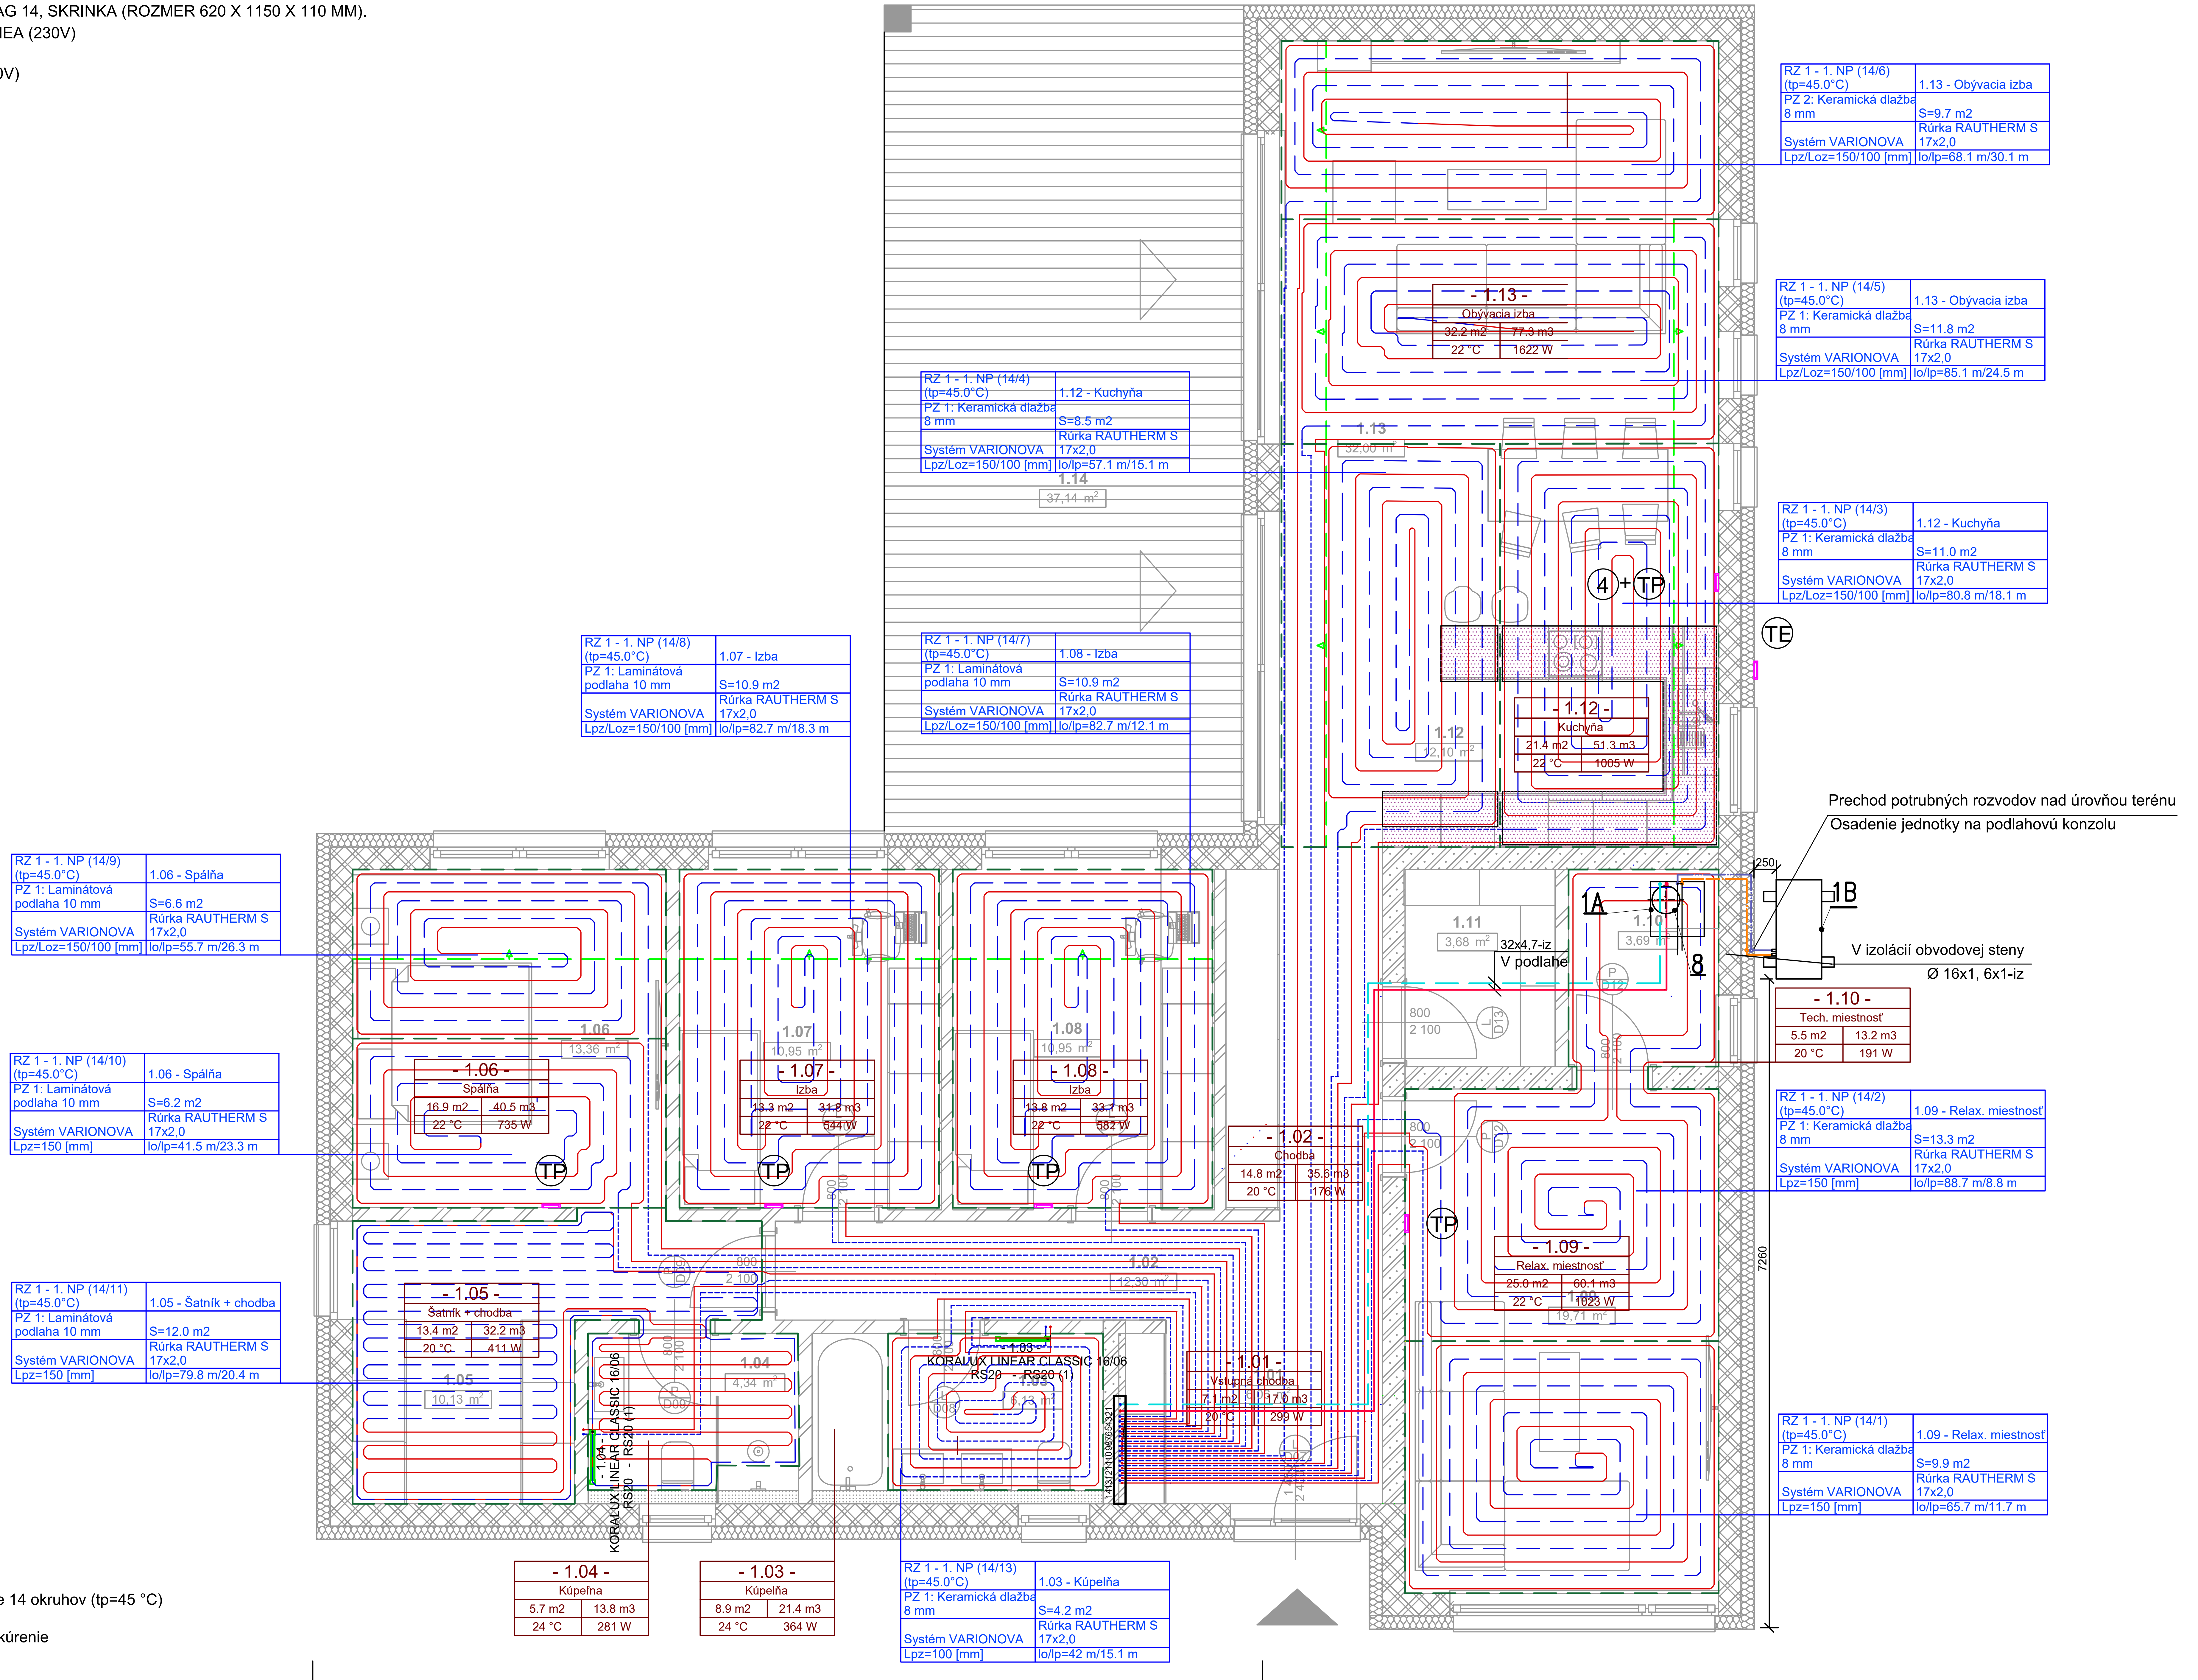
RZ 1 - 1. NP (14/6) (tp=45.0°C) | 1.13 - Obývacia izba | PZ 2: Keramická dlažba 8 mm | S=9.7 m2 | Systém VARIONOVA | Rúrka RAUTHERM S 17x2,0 | Lpz/Loz=150/100 [mm] | lo/lp=68.1 m/30.1 m
RZ 1 - 1. NP (14/5) (tp=45.0°C) | 1.13 - Obývacia izba | PZ 1: Keramická dlažba 8 mm | S=11.8 m2 | Systém VARIONOVA | Rúrka RAUTHERM S 17x2,0 | Lpz/Loz=150/100 [mm] | lo/lp=85.1 m/24.5 m
RZ 1 - 1. NP (14/4) (tp=45.0°C) | 1.12 - Kuchyňa | PZ 1: Keramická dlažba 8 mm | S=8.5 m2 | Systém VARIONOVA | Rúrka RAUTHERM S 17x2,0 | Lpz/Loz=150/100 [mm] | lo/lp=57.1 m/15.1 m
RZ 1 - 1. NP (14/3) (tp=45.0°C) | 1.12 - Kuchyňa | PZ 1: Keramická dlažba 8 mm | S=11.0 m2 | Systém VARIONOVA | Rúrka RAUTHERM S 17x2,0 | Lpz/Loz=150/100 [mm] | lo/lp=80.8 m/18.1 m
RZ 1 - 1. NP (14/8) (tp=45.0°C) | 1.07 - Izba | PZ 1: Laminátová podlaha 10 mm | S=10.9 m2 | Systém VARIONOVA | Rúrka RAUTHERM S 17x2,0 | Lpz/Loz=150/100 [mm] | lo/lp=82.7 m/18.3 m
RZ 1 - 1. NP (14/7) (tp=45.0°C) | 1.08 - Izba | PZ 1: Laminátová podlaha 10 mm | S=10.9 m2 | Systém VARIONOVA | Rúrka RAUTHERM S 17x2,0 | Lpz/Loz=150/100 [mm] | lo/lp=82.7 m/12.1 m
RZ 1 - 1. NP (14/9) (tp=45.0°C) | 1.06 - Spálňa | PZ 1: Laminátová podlaha 10 mm | S=6.6 m2 | Systém VARIONOVA | Rúrka RAUTHERM S 17x2,0 | Lpz/Loz=150/100 [mm] | lo/lp=55.7 m/26.3 m
RZ 1 - 1. NP (14/10) (tp=45.0°C) | 1.06 - Spálňa | PZ 1: Laminátová podlaha 10 mm | S=6.2 m2 | Systém VARIONOVA | Rúrka RAUTHERM S 17x2,0 | Lpz=150 [mm] | lo/lp=41.5 m/23.3 m
RZ 1 - 1. NP (14/11) (tp=45.0°C) | 1.05 - Šatník + chodba | PZ 1: Laminátová podlaha 10 mm | S=12.0 m2 | Systém VARIONOVA | Rúrka RAUTHERM S 17x2,0 | Lpz=150 [mm] | lo/lp=79.8 m/20.4 m
RZ 1 - 1. NP (14/13) (tp=45.0°C) | 1.03 - Kúpelňa | PZ 1: Keramická dlažba 8 mm | S=4.2 m2 | Systém VARIONOVA | Rúrka RAUTHERM S 17x2,0 | Lpz=100 [mm] | lo/lp=42 m/15.1 m
RZ 1 - 1. NP (14/2) (tp=45.0°C) | 1.09 - Relax. miestnosť | PZ 1: Keramická dlažba 8 mm | S=13.3 m2 | Systém VARIONOVA | Rúrka RAUTHERM S 17x2,0 | Lpz=150 [mm] | lo/lp=88.7 m/8.8 m
RZ 1 - 1. NP (14/1) (tp=45.0°C) | 1.09 - Relax. miestnosť | PZ 1: Keramická dlažba 8 mm | S=9.9 m2 | Systém VARIONOVA | Rúrka RAUTHERM S 17x2,0 | Lpz=150 [mm] | lo/lp=65.7 m/11.7 m
- 1.13 - Obývacia izba 32.2 m2 77.9 m3 22 °C 1622 W
- 1.12 - Kuchyňa 21.4 m2 51.3 m3 22 °C 1005 W
- 1.06 - Spálňa 16.9 m2 40.5 m3 22 °C 735 W
- 1.07 - Izba 13.3 m2 31.8 m3 20 °C 544 W
- 1.08 - Izba 13.8 m2 33.7 m3 22 °C 682 W
- 1.02 - Chodba 14.8 m2 35.5 m3 20 °C 176 W
- 1.05 - Šatník + chodba 13.4 m2 32.2 m3 20 °C 411 W
- 1.01 - Vstupná chodba 7.1 m2 17.0 m3 20 °C 299 W
- 1.09 - Relax. miestnosť 25.0 m2 60.1 m3 22 °C 1023 W
- 1.10 - Tech. miestnosť 5.5 m2 13.2 m3 20 °C 191 W
- 1.04 - Kúpeľna 5.7 m2 13.8 m3 24 °C 281 W
- 1.03 - Kúpelňa 8.9 m2 21.4 m3 24 °C 364 W
1.14 37,14 m²
KORALUX LINEAR CLASSIC 16/06 RS20 - RS20 (1)
4 TP TE 1A 1B 8
Prechod potrubných rozvodov nad úrovňou terénu
Osadenie jednotky na podlahovú konzolu
V izolácií obvodovej steny
Ø 16x1, 6x1-iz
32x4.7-iz V podlahe
250
7260

LEGENDA POTRUBÍ:

🟥	PLASTHLINÍKOVÉ POTRUBIE NAPR. RAUTHERM S 17×2,0 REHAU, TEPLOTNÝ SPÁD 45/32,5 °C, VEDENÉ V PODLAHE.
🟥	PLASTHLINÍKOVÉ POTRUBIE MATERIÁL: PE-XA/AL/PE NAPR. RAUTITAN STABIL, ZAIZOLOVANÉ POTRUBIE, TEPLOTNÝ SPÁD 45/32,5 °C.
🟧	MEDENÉ POTRUBIE PRIMÁRNEHO OKRUHU TEPELNÉHO ČERPADLA: CU Φ16×1, 6×1-IZ.

LEGENDA ZARIADENÍ:

1A	TEPELNÉ ČERPADLO (VNÚTORNÁ JEDNOTKA) NAPR.: VIESSMANN VITOCAL 222-S. INTEGROVANÝ ZÁSOBNÍK NA TV (190 L), NAPÁJANIE 230V/50HZ.
1B	TEPELNÉ ČERPADLO (VONKAJŠIA JEDNOTKA) NAPR.: VITOCAL 222-S. VÝKON (A7/W35): 2,6 – 10,4 KW.
4	OVLÁDANIE: BEZDRÔTOVÝ DIAĽOVÝ OVLÁDAČ NAPR. VITOTROL 300-E.
8	EXPANZNÁ NÁDOBA NAPR: VIESSMANN N25 (min. OBJEM 25 L, MAX. TLAK 4 BAR).
TP	IZBOVÝ REGULÁTOR NAPR.: REHAU NEA SMART 2.0 (MERANIE TEPLOTY).
TE	SNÍMAČ TEPLOTY EXTERIÉRU.
🟩	REBRÍKOVÉ VYKUROVACIE TELESO KORALUX LINEAR CLASSIC DOPLNENÉ O EL. VYKUROVACIU VLOŽKU 230V

POZNÁMKY :

- V PRÍPADE AKÝCHKOĽVEK NEJASNOSTÍ V PROJEKTOVEJ DOKUMENTÁCII JE NUTNÉ KONTAKTOVAŤ ZODPOVEDNÉHO PROJEKTANTA.
- VŠETKY STAVEBNÉ ROZMERY A PRESTUPY JE POTREBNÉ OVERIŤ PRIAMO NA MIESTE REALIZÁCIE.
- PRED SAMOTNÝM SPUSTENÍM SYSTÉMU DO PREVÁDZKY SA MUSÍ VYKONAŤ DÔKLADNÝ PREPLACH ROZVODOV A VYČISTENIE VŠETKÝCH INŠTALOVANÝCH FILTROV.
- PO NAPUSTENÍ VYKUROVACEJ SÚSTAVY MÉDIOM JE NEVYHNUTNÉ ZABEZPEČIŤ JEJ POSTUPNÉ ODVZDUŠNENIE.
- ZHOTOVITEĽ JE POVINNÝ POSTUPOVAŤ V SÚLADE S PLATNÝMI NORMAMI STN EN A DODRŽIAVAŤ TECHNOLOGICKÉ AJ BEZPEČNOSTNÉ PREDPISY. ZÁROVEŇ MUSÍ REŠPEKTOVAŤ USTANOVENIA STN 730421 O ROZMEROVÝCH ODCHÝLKACH. KAŽDÚ ZMENU OPROTI PROJEKTU JE NUTNÉ VOPRED SKONZULTOVAŤ S HIP.
- OTVORY PRE PRESTUPY INŽINIERSKYCH SIETÍ A POTRUBNÝCH ROZVODOV V OBJEKTE JE POTREBNÉ PRIPRAVIŤ POČAS REALIZÁCIE HRUBEJ STAVBY.
- TÁTO DOKUMENTÁCIA NENAHRÁDZA REALIZAČNÚ DOKUMENTÁCIU STAVBY!
-VÝŠKOVÁ ÚROVEŇ ±0,000 V PROJEKTE ZODPOVEDÁ ÚROVNI FINÁLNEJ NÁŠĽAPNEJ VRSTVY PODLAHY.

TABUĽKA REVÍZIÍ

ČÍSLO REVÍZIE	DÁTUM	POPIS ZMENY	VYPRACOVAL

0,000=123,200 m n. m.

AUTOR PROJEKTU:	Ing. arch. Ivor Mečiar, Matúš Sorokáč
H.I.P.:	Ing. arch. Ivor Mečiar, ArtD.
ZODP. PROJEKTANT:	Ing. Ján Bátor
VYPRACOVAL:	Ing. Viktor Labovský

GENERÁLNY PROJEKTANT:
Alla s.r.o.
Riazanská 70/683
831 02 Bratislava
tel.: +421 907 693 679
email: ateliar@alla.sk

INVESTOR:	Dc
NÁZOV PROJEKTU:	E
MIESTO STAVBY:	2(
OBSAH VÝKRESU:	F
STAVEBNÝ OBJEKT:	S
ID STAVBY: ---	STUPEŇ PD: PSP
NÁZOV VÝKRESU V ELEKTRONICKEJ F	