VETVA RADIATORY

4. NP 10.800
3. NP 7.200
2. NP 3.600
1. NP 0.000
RADIATORY
- 3.31 - KORAD 11VKP 6/04 TV15 (1) - VK-RS20 (6 Otv.) 176 W
- 3.20 - KORAD 22VKL 9/06 TV15 (3.00) - VK-RS20 (6 Otv.) 543 W
65
2xGK - DN 15 2x AUT. ODVZD.
PP
- 3.32 - KORAD 22VKP 6/14 TV15 (6.00) - VK-RS20 (6 Otv.) 1071 W
63
- 3.20 - KORAD 22VKP 9/14 - B TV15 (6.00) - VK-RS20 (6 Otv.) 1268 W
62
- 3.16 - KORAD 22VKL 6/06 TV15 (2.00) - VK-RS20 (6 Otv.) 459 W
64
- 2.31 - KORAD 11VKP 6/04 TV15 (1) - VK-RS20 (6 Otv.) 176 W
- 2.20 - KORAD 22VKL 9/06 TV15 (3.00) - VK-RS20 (6 Otv.) 543 W
- 2.38 - KORAD 22VKP 6/14 TV15 (6.00) - VK-RS20 (6 Otv.) 1071 W
- 2.20 - KORAD 22VKP 9/14 - B TV15 (6.00) - VK-RS20 (6 Otv.) 1268 W
- 2.14 - KORAD 22VKP 5/06 TV15 (2.00) - VK-RS20 (6 Otv.) 399 W
STRÖMAX-GM 2013(meranie) DN 50, Nastavenie 7.00 Prietok 7343.5 l/h Tlaková strata 4338 Pa
75x4,6
2xGK DN50
GK DN50
RTD DN 50 77.854 kPa 7343.5 l/h
2x AUT. ODVZD. 2xGK - DN 15
1F
Vetva RADIATORY Q=42216 W H=77821 Pa dt=45.0/40.0 °C
2F
3F
4F
5F
6F
7F
11F
26x3,0
20x2,0
16x2,0
32x3,0
40x3,5
50x4,0
63x4,5
- 1.21 - KORAD 22VKL 9/14 - A TV15 (6.00) - VK-RS20 (6 Otv.) 1268 W
- 1.32 - KORAD 22VKP 9/14 TV15 (8.00 Otv.) - VK-RS20 (6 Otv.) 1480 W
- 1.21 - KORAD 22VKP 9/14 TV15 (6.00) - VK-RS20 (6 Otv.) 1268 W
- 1.27 - KORAD 22VKL 9/20 TV15 (8 Otv.) - VK-RS20 (6 Otv.) 2114 W
- 1.08 - KORAD 22VKL 6/10 TV15 (4.00) - VK-RS20 (6 Otv.) 765 W
- 1.42 - KORAD 22VKP 6/20 - A TV15 (6.00) - VK-RS20 (6 Otv.) 1171 W
- 1.41 - KORAD 22VKL 6/06 TV15 (2.00) - VK-RS20 (6 Otv.) 459 W
- 1.42 - KORAD 22VKP 6/18 TV15 (6.00) - VK-RS20 (6 Otv.) 1054 W
- 1.43 - KORAD 22VKP 6/20 TV15 (8.00 Otv.) - VK-RS20 (6 Otv.) 1531 W
- 3.20 - KORAD 22VKL 9/20 - B TV15 (8 Otv.) - VK-RS20 (6 Otv.) 1812 W
66
- 2.20 - KORAD 22VKL 9/20 - B TV15 (8 Otv.) - VK-RS20 (6 Otv.) 1812 W
- 1.21 - KORAD 22VKL 9/20 TV15 (8 Otv.) - VK-RS20 (6 Otv.) 1812 W
- 3.20 - KORAD 22VKL 9/20 - A TV15 (8 Otv.) - VK-RS20 (6 Otv.) 1812 W
67
- 2.20 - KORAD 22VKL 9/20 - A TV15 (8 Otv.) - VK-RS20 (6 Otv.) 1812 W
- 1.21 - KORAD 22VKL 9/20 TV15 (8 Otv.) - VK-RS20 (6 Otv.) 1812 W
- 1.42 - KORAD 22VKP 6/20 - B TV15 (6.00) - VK-RS20 (6 Otv.) 1171 W
- 1.44 - KORAD 22VKP 9/14 TV15 (6.00) - VK-RS20 (6 Otv.) 1268 W
- 1.45 - KORAD 22VKP 6/08 TV15 (3.00) - VK-RS20 (6 Otv.) 612 W
- 1.48 - KORAD 22VKL 6/14 TV15 (6.00) - VK-RS20 (6 Otv.) 1071 W
- 1.47 - KORAD 22VKP 6/08 TV15 (3.00) - VK-RS20 (6 Otv.) 612 W
- 1.39 - KORAD 22VKP 6/16 TV15 (6.00) - VK-RS20 (6 Otv.) 1049 W
- 1.46 - KORAD 22VKP 6/08 TV15 (3.00) - VK-RS20 (6 Otv.) 612 W
- 1.30 - KORAD 11VKP 6/06 TV15 (1) - VK-RS20 (6 Otv.) 264 W
- 3.20 - KORAD 22VKP 9/06 TV15 (3.00) - VK-RS20 (6 Otv.) 543 W
68
- 2.20 - KORAD 22VKP 9/06 TV15 (3.00) - VK-RS20 (6 Otv.) 543 W
- 1.21 - KORAD 22VKP 9/06 TV15 (3.00) - VK-RS20 (6 Otv.) 543 W
- 1.29 - KORAD 11VKP 6/06 TV15 (1) - VK-RS20 (6 Otv.) 264 W
- 3.20 - KORAD 22VKP 9/14 - A TV15 (6.00) - VK-RS20 (6 Otv.) 1268 W
69
- 2.20 - KORAD 22VKP 9/14 - A TV15 (6.00) - VK-RS20 (6 Otv.) 1268 W
- 1.21 - KORAD 22VKL 9/14 - B TV15 (6.00) - VK-RS20 (6 Otv.) 1268 W
- 3.10 - KORAD 11VKP 3/06 TV15 (1) - VK-RS20 (6 Otv.) 151 W
61
- 1.11 - KORAD 22VKP 6/08 TV15 (2.00) - VK-RS20 (6 Otv.) 468 W
- 3.08 - KORAD 11VKP 3/06 TV15 (1) - VK-RS20 (6 Otv.) 151 W
60
- 1.10 - KORAD 11VKL 4/04 TV15 (1) - VK-RS20 (6 Otv.) 127 W

VETVA 4.NP

4. NP 10.800
3. NP 7.200
2. NP 3.600
1. NP 0.000
AOV
- 4.43 - FANCOLOVÁ PARAPETNÁ JEDNOTKA FWL02DTN VÝKON - Qchl=1350 W, Qvyk=976 W TEPLOTNÝ SPÁD - chl: 7/12°C, vyk: 45/40°C PRIETOK - 169.8 l/h
- 4.28 - FANCOLOVÁ PARAPETNÁ JEDNOTKA FWL04DTN VÝKON - Qchl=2470 W, Qvyk=1998 W TEPLOTNÝ SPÁD - chl: 7/12°C, vyk: 45/40°C PRIETOK - 347.6 l/h
- 4.21 - FANCOLOVÁ PARAPETNÁ JEDNOTKA FWL04DTN VÝKON - Qchl=3000 W, Qvyk=1771 W TEPLOTNÝ SPÁD - chl: 7/12°C, vyk: 45/40°C PRIETOK - 308.1 l/h
- 4.19 - FANCOLOVÁ PARAPETNÁ JEDNOTKA FWL02DTN VÝKON - Qchl=1750 W, Qvyk=1024 W TEPLOTNÝ SPÁD - chl: 7/12°C, vyk: 45/40°C PRIETOK - 178.1 l/h
- 4.17 - FANCOLOVÁ PARAPETNÁ JEDNOTKA FWL04DTN VÝKON - Qchl=2470 W, Qvyk=1389 W TEPLOTNÝ SPÁD - chl: 7/12°C, vyk: 45/40°C PRIETOK - 169.8 l/h
- 4.15 - FANCOLOVÁ PARAPETNÁ JEDNOTKA FWL04DTN VÝKON - Qchl=2600 W, Qvyk=1791 W TEPLOTNÝ SPÁD - chl: 7/12°C, vyk: 45/40°C PRIETOK - 311.5 l/h
HERZ 7217 V (1.10) DN 15
HERZ 7217 V (1.20) DN 20
HERZ 7217 V (3.80) DN 15
HERZ 7217 V (1.00) DN 20
HERZ 7217 V (0.70) DN 20
HERZ 7217 V (1.60) DN 15
HERZ 7217 V (1.40) DN 15
HERZ 7217 V (0.70) DN 20
HERZ 7217 V (1.40) DN 15
HERZ 7217 V (1.10) DN 20
GK s pákovým ovládačom DN 15
GK s pákovým ovládačom DN 20
3 CESTNÝ VENTIL K FWL-DTN (DODÁVKA VZT S FANCOILOM)
- 4.27 - FANCOLOVÁ PARAPETNÁ JEDNOTKA FWL03DTN VÝKON - Qchl=2100 W, Qvyk=1584 W TEPLOTNÝ SPÁD - chl: 7/12°C, vyk: 45/40°C PRIETOK - 275.5 l/h
- 4.20 - FANCOLOVÁ PARAPETNÁ JEDNOTKA FWL04DTN VÝKON - Qchl=2470 W, Qvyk=1387 W TEPLOTNÝ SPÁD - chl: 7/12°C, vyk: 45/40°C PRIETOK - 169.8 l/h
- 4.18 - FANCOLOVÁ PARAPETNÁ JEDNOTKA FWL02DTN VÝKON - Qchl=1660 W, Qvyk=965 W TEPLOTNÝ SPÁD - chl: 7/12°C, vyk: 45/40°C PRIETOK - 167.9 l/h
- 4.16 - FANCOLOVÁ PARAPETNÁ JEDNOTKA FWL02DTN VÝKON - Qchl=1600 W, Qvyk=937 W TEPLOTNÝ SPÁD - chl: 7/12°C, vyk: 45/40°C PRIETOK - 163.0 l/h
- 4.38 - FANCOLOVÁ PARAPETNÁ JEDNOTKA FWL03DTN VÝKON - Qchl=2200 W, Qvyk=1064 W TEPLOTNÝ SPÁD - chl: 7/12°C, vyk: 45/40°C PRIETOK - 169.8 l/h
- 4.40 - FANCOLOVÁ PARAPETNÁ JEDNOTKA FWL03DTN VÝKON - Qchl=2300 W, Qvyk=1569 W TEPLOTNÝ SPÁD - chl: 7/12°C, vyk: 45/40°C PRIETOK - 272.9 l/h
- 4.37 - FANCOLOVÁ PARAPETNÁ JEDNOTKA FWL03DTN VÝKON - Qchl=2200 W, Qvyk=1057 W TEPLOTNÝ SPÁD - chl: 7/12°C, vyk: 45/40°C PRIETOK - 183.9 l/h
- 4.26 - FANCOLOVÁ PARAPETNÁ JEDNOTKA FWL03DTN VÝKON - Qchl=2100 W, Qvyk=1569 W TEPLOTNÝ SPÁD - chl: 7/12°C, vyk: 45/40°C PRIETOK - 272.9 l/h
- 4.24 - FANCOLOVÁ PARAPETNÁ JEDNOTKA FWL03DTN VÝKON - Qchl=2050 W, Qvyk=1510 W TEPLOTNÝ SPÁD - chl: 7/12°C, vyk: 45/40°C PRIETOK - 262.7 l/h
HERZ 7217 V (1.40) DN 15
HERZ 7217 V (1.40) DN 15
HERZ 7217 V (3.70) DN 15
HERZ 7217 V (2.50) DN 15
HERZ 7217 V (1.40) DN 15
HERZ 7217 V (1.40) DN 20
HERZ 7217 V (3.70) DN 15
HERZ 7217 V (1.00) DN 20
HERZ 7217 V (3.40) DN 15
HERZ 7217 V (3.40) DN 15
- 4.39 - FANCOLOVÁ PARAPETNÁ JEDNOTKA FWL03DTN VÝKON - Qchl=2200 W, Qvyk=1057 W TEPLOTNÝ SPÁD - chl: 7/12°C, vyk: 45/40°C PRIETOK - 183.9 l/h
- 4.41 - FANCOLOVÁ PARAPETNÁ JEDNOTKA FWL03DTN VÝKON - Qchl=2200 W, Qvyk=1322 W TEPLOTNÝ SPÁD - chl: 7/12°C, vyk: 45/40°C PRIETOK - 230.0 l/h
- 4.36 - FANCOLOVÁ PARAPETNÁ JEDNOTKA FWL04DTN VÝKON - Qchl=3000 W, Qvyk=2497 W TEPLOTNÝ SPÁD - chl: 7/12°C, vyk: 45/40°C PRIETOK - 434.4 l/h
- 4.25 - FANCOLOVÁ PARAPETNÁ JEDNOTKA FWL04DTN VÝKON - Qchl=2400 W, Qvyk=1775 W TEPLOTNÝ SPÁD - chl: 7/12°C, vyk: 45/40°C PRIETOK - 308.8 l/h
- 4.23 - FANCOLOVÁ PARAPETNÁ JEDNOTKA FWL03DTN VÝKON - Qchl=2000 W, Qvyk=1499 W TEPLOTNÝ SPÁD - chl: 7/12°C, vyk: 45/40°C PRIETOK - 260.8 l/h
- 4.13 - FANCOLOVÁ PARAPETNÁ JEDNOTKA FWL02DTN VÝKON - Qchl=1850 W, Qvyk=1418 W TEPLOTNÝ SPÁD - chl: 7/12°C, vyk: 45/40°C PRIETOK - 246.7 l/h
- 4.12 - FANCOLOVÁ PARAPETNÁ JEDNOTKA FWL01DTN VÝKON - Qchl=1100 W, Qvyk=921 W TEPLOTNÝ SPÁD - chl: 7/12°C, vyk: 45/40°C PRIETOK - 160.2 l/h
- 4.10 - FANCOLOVÁ PARAPETNÁ JEDNOTKA FWL02DTN VÝKON - Qchl=1660 W, Qvyk=1200 W TEPLOTNÝ SPÁD - chl: 7/12°C, vyk: 45/40°C PRIETOK - 208.7 l/h
- 4.09 - FANCOLOVÁ PARAPETNÁ VSTAVANÁ JEDNOTKA FWL04DTN VÝKON - Qchl=3000 W, Qvyk=1760 W TEPLOTNÝ SPÁD - chl: 7/12°C, vyk: 45/40°C PRIETOK - 306.2 l/h
- 4.03 - FANCOLOVÁ PARAPETNÁ VSTAVANÁ JEDNOTKA FWL02DTN VÝKON - Qchl=5300 W, Qvyk=1946 W TEPLOTNÝ SPÁD - chl: 7/12°C, vyk: 45/40°C PRIETOK - 338.5 l/h
HERZ 7217 V (3.00) DN 15
HERZ 7217 V (3.10) DN 15
HERZ 7217 V (1.40) DN 15
HERZ 7217 V (1.90) DN 15
HERZ 7217 V (2.30) DN 15
HERZ 7217 V (1.00) DN 20
HERZ 7217 V (1.10) DN 20
HERZ 7217 V (0.10) DN 15
HERZ 7217 V (5.90) DN 15
HERZ 7217 V (5.90) DN 15
- 4.13 - FANCOLOVÁ PARAPETNÁ JEDNOTKA FWL02DTN VÝKON - Qchl=1850 W, Qvyk=1418 W TEPLOTNÝ SPÁD - chl: 7/12°C, vyk: 45/40°C PRIETOK - 246.7 l/h
- 4.11 - FANCOLOVÁ PARAPETNÁ JEDNOTKA FWL02DTN VÝKON - Qchl=1500 W, Qvyk=1138 W TEPLOTNÝ SPÁD - chl: 7/12°C, vyk: 45/40°C PRIETOK - 198.0 l/h
- 4.09 - FANCOLOVÁ PARAPETNÁ JEDNOTKA FWL04DTN VÝKON - Qchl=3000 W, Qvyk=1760 W TEPLOTNÝ SPÁD - chl: 7/12°C, vyk: 45/40°C PRIETOK - 306.2 l/h
- 4.04 - FANCOLOVÁ PARAPETNÁ VSTAVANÁ JEDNOTKA FWL01DTN VÝKON - Qchl=1100 W, Qvyk=458 W TEPLOTNÝ SPÁD - chl: 7/12°C, vyk: 45/40°C PRIETOK - 79.7 l/h
- 4.03 - FANCOLOVÁ PARAPETNÁ VSTAVANÁ JEDNOTKA FWL02DTN VÝKON - Qchl=5300 W, Qvyk=1946 W TEPLOTNÝ SPÁD - chl: 7/12°C, vyk: 45/40°C PRIETOK - 338.5 l/h
- 4.01 - FANCOLOVÁ PODSTROPNÁ JEDNOTKA FVH04AT VÝKON - Qchl=4300 W, Qvyk=744 W TEPLOTNÝ SPÁD - chl: 7/12°C, vyk: 45/40°C PRIETOK - 129.4 l/h
- 4.01 - FANCOLOVÁ PODSTROPNÁ JEDNOTKA FVH04AT VÝKON - Qchl=4300 W, Qvyk=744 W TEPLOTNÝ SPÁD - chl: 7/12°C, vyk: 45/40°C PRIETOK - 129.4 l/h
HERZ 7217 V (1.00) DN20
GK s pákovým ovládačom DN20
3 CESTNÝ VENTIL K FWH-AT (DODÁVKA VZT S FANCOILOM)
- 4.01 - FANCOLOVÁ PODSTROPNÁ JEDNOTKA FVH04AT VÝKON - Qchl=4300 W, Qvyk=744 W TEPLOTNÝ SPÁD - chl: 7/12°C, vyk: 45/40°C PRIETOK - 129.4 l/h
- 4.01 - FANCOLOVÁ PODSTROPNÁ JEDNOTKA FVH04AT VÝKON - Qchl=4300 W, Qvyk=744 W TEPLOTNÝ SPÁD - chl: 7/12°C, vyk: 45/40°C PRIETOK - 129.4 l/h
69
2xGK - DN 15 2x AUT. ODVZD.
32x3,0
PP
59
29
75x4,6-iz
- 4.22 - FANCOLOVÁ PODSTROPNÁ JEDNOTKA FVH04AT VÝKON - Qchl=4000 W, Qvyk=3017 W TEPLOTNÝ SPÁD - chl: 7/12°C, vyk: 45/40°C PRIETOK - 524.8 l/h
- 4.29 - FANCOLOVÁ PODSTROPNÁ JEDNOTKA FVH04AT VÝKON - Qchl=4000 W, Qvyk=3017 W TEPLOTNÝ SPÁD - chl: 7/12°C, vyk: 45/40°C PRIETOK - 524.8 l/h
- 4.44 - FANCOLOVÁ PODSTROPNÁ JEDNOTKA FVH04AT VÝKON - Qchl=4500 W, Qvyk=3136 W TEPLOTNÝ SPÁD - chl: 7/12°C, vyk: 45/40°C PRIETOK - 545.5 l/h
- 4.45 - FANCOLOVÁ PODSTROPNÁ JEDNOTKA FVH04AT VÝKON - Qchl=4100 W, Qvyk=3080 W TEPLOTNÝ SPÁD - chl: 7/12°C, vyk: 45/40°C PRIETOK - 535.8 l/h
HERZ 7217 V (1.90) DN20
HERZ 7217 V (1.90) DN20
HERZ 7217 V (1.80) DN20
HERZ 7217 V (1.80) DN20
HERZ 7217 V (2.30) DN20
HERZ 7217 V (2.00) DN20
HERZ 7217 V (1.80) DN20
- 4.29 - FANCOLOVÁ PODSTROPNÁ JEDNOTKA FVH04AT VÝKON - Qchl=4000 W, Qvyk=3017 W TEPLOTNÝ SPÁD - chl: 7/12°C, vyk: 45/40°C PRIETOK - 524.8 l/h
- 4.46 - FANCOLOVÁ PODSTROPNÁ JEDNOTKA FVH04AT VÝKON - Qchl=1899 W, Qvyk=3000 W TEPLOTNÝ SPÁD - chl: 7/12°C, vyk: 45/40°C PRIETOK - 521.8 l/h
- 4.44 - FANCOLOVÁ PODSTROPNÁ JEDNOTKA FVH04AT VÝKON - Qchl=4500 W, Qvyk=3136 W TEPLOTNÝ SPÁD - chl: 7/12°C, vyk: 45/40°C PRIETOK - 545.5 l/h

LEGENDA:

▬ ▬	VYK. POTRUBIE NÍZKOUHLÍKOVÉ OCELOVÉ/PLASTOHLINÍKOVÉ POTRUBIE
▬ ▬	VYK. POTRUBIE NÍZKOUHLÍKOVÉ OCELOVÉ/PLASTOHLINÍKOVÉ POTRUBIE, RADIATOROVÉ
☰ PP	POŽIARNY PRESTUP

DETAIL NAPOJENIA KANÁLOVÉHO FANCOILU:

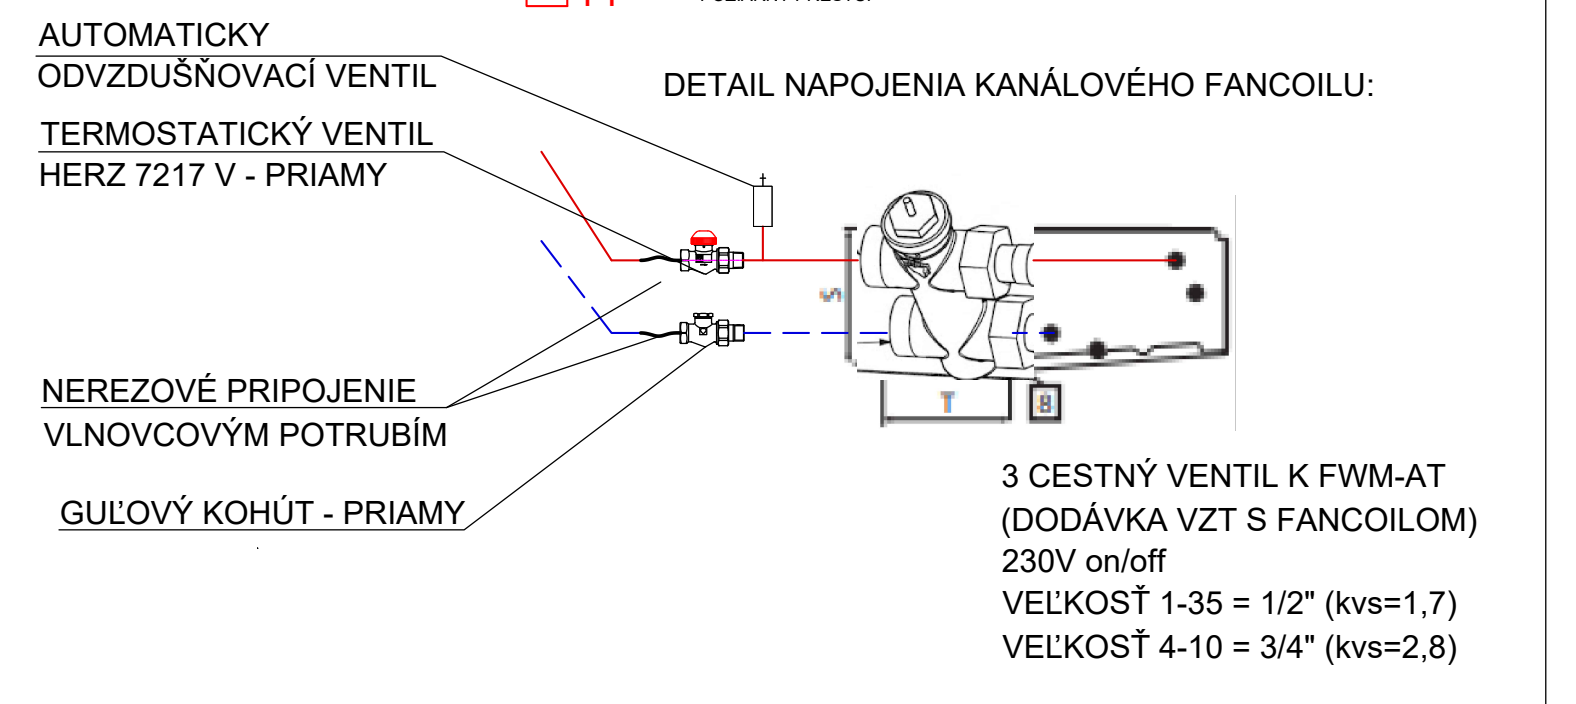
AUTOMATICKY ODVZDUŠŇOVACÍ VENTIL
TERMOSTATICKÝ VENTIL HERZ 7217 V - PRIAMY
NEREZOVÉ PRIPOJENIE VLNOVCOVÝM POTRUBÍM
GUĽOVÝ KOHÚT - PRIAMY
T
B

3 CESTNÝ VENTIL K FWM-AT
(DODÁVKA VZT S FANCOILOM)
230V on/off
VEĽKOSŤ 1-35 = 1/2" (kvs=1,7)
VEĽKOSŤ 4-10 = 3/4" (kvs=2,8)

DETAIL NAPOJENIA KAZETOVÉHO FANCOILU:

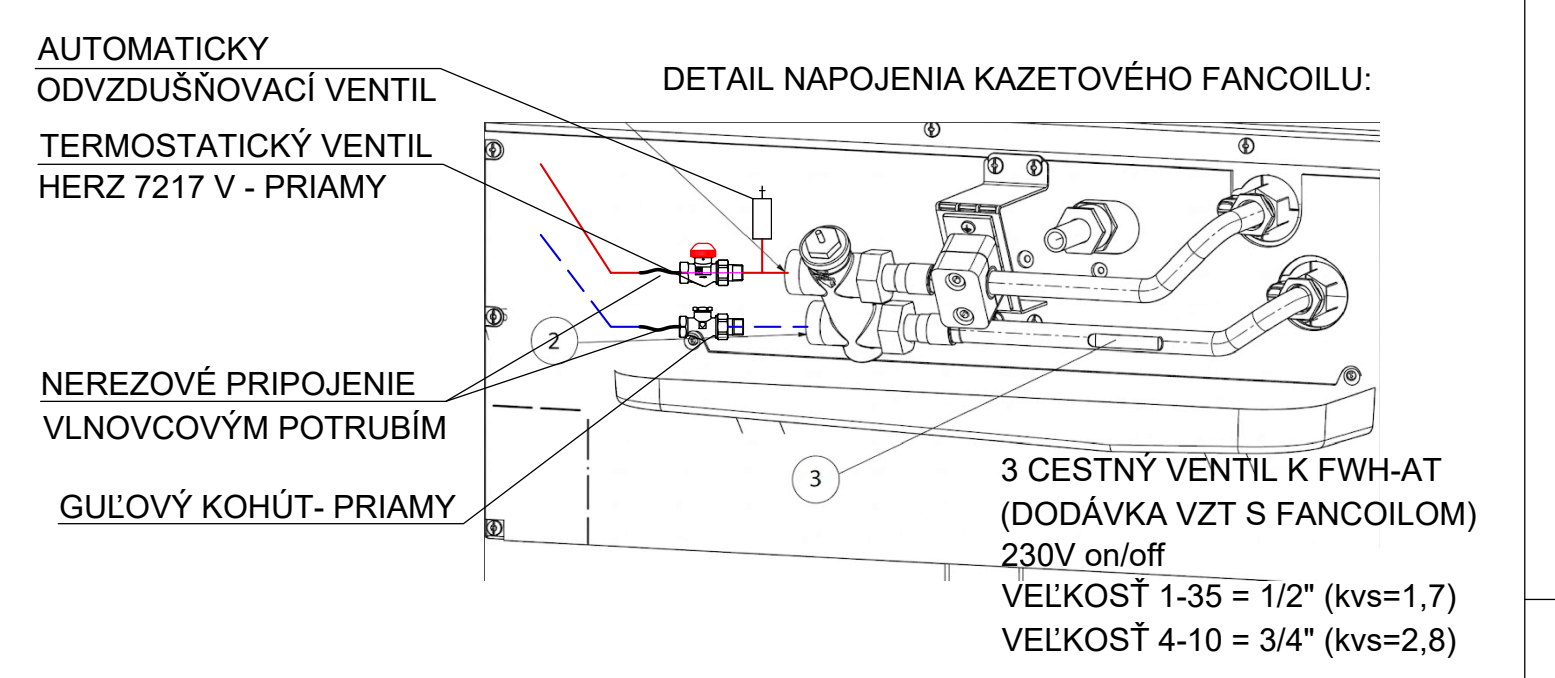
AUTOMATICKY ODVZDUŠŇOVACÍ VENTIL
TERMOSTATICKÝ VENTIL HERZ 7217 V - PRIAMY
NEREZOVÉ PRIPOJENIE VLNOVCOVÝM POTRUBÍM
GUĽOVÝ KOHÚT- PRIAMY
2
3

3 CESTNÝ VENTIL K FWH-AT
(DODÁVKA VZT S FANCOILOM)
230V on/off
VEĽKOSŤ 1-35 = 1/2" (kvs=1,7)
VEĽKOSŤ 4-10 = 3/4" (kvs=2,8)

DETAIL NAPOJENIA PARAPETNÉHO FANCOILU:

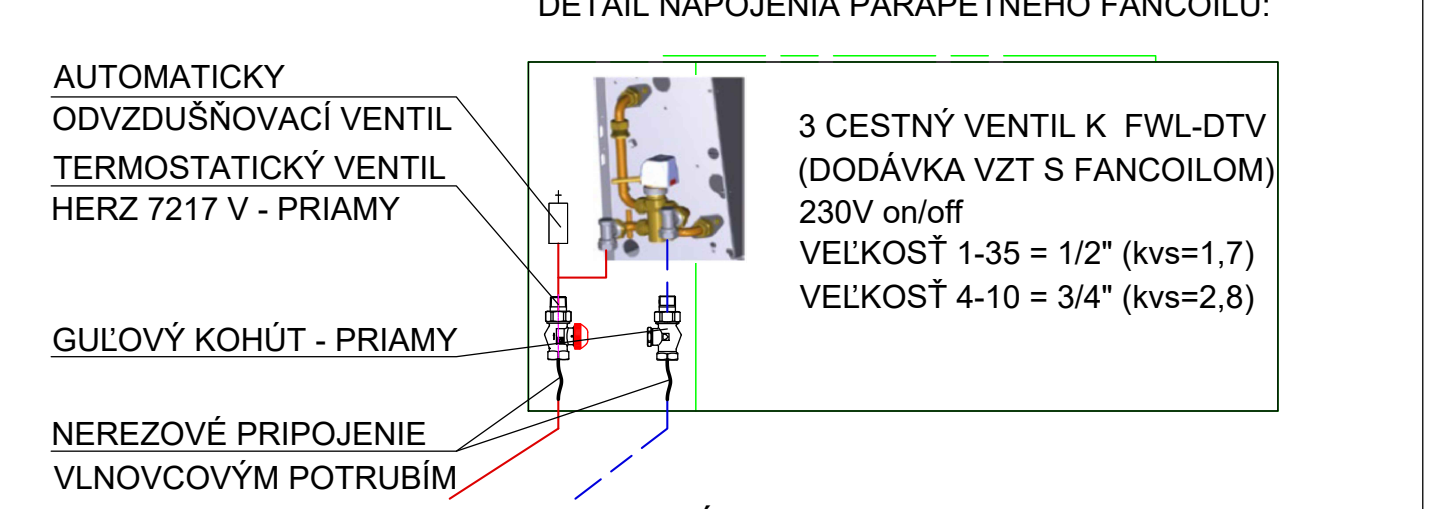
AUTOMATICKY ODVZDUŠŇOVACÍ VENTIL
TERMOSTATICKÝ VENTIL HERZ 7217 V - PRIAMY
GUĽOVÝ KOHÚT - PRIAMY
NEREZOVÉ PRIPOJENIE VLNOVCOVÝM POTRUBÍM

3 CESTNÝ VENTIL K FWL-DTV
(DODÁVKA VZT S FANCOILOM)
230V on/off
VEĽKOSŤ 1-35 = 1/2" (kvs=1,7)
VEĽKOSŤ 4-10 = 3/4" (kvs=2,8)

DOSKOVÉ VYKUROVACIE TELESO

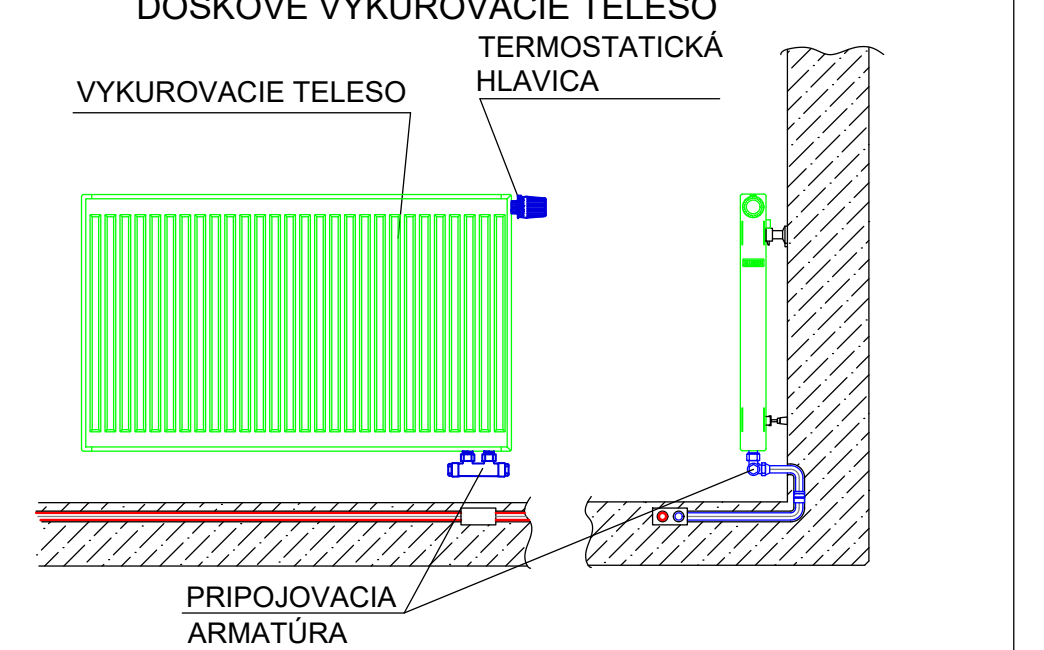

LEGENDA OSADENIA REGULÁCIE NA PÄTE STÚPAČKY:

GK - Guľový kohút
VK - Vypúšťací kohút DN15
RTD - Regulátor tlakovej diferencie
PTV - Partnerský vyvažovací ventil Herz Stromax GM 2013 - závit Rp

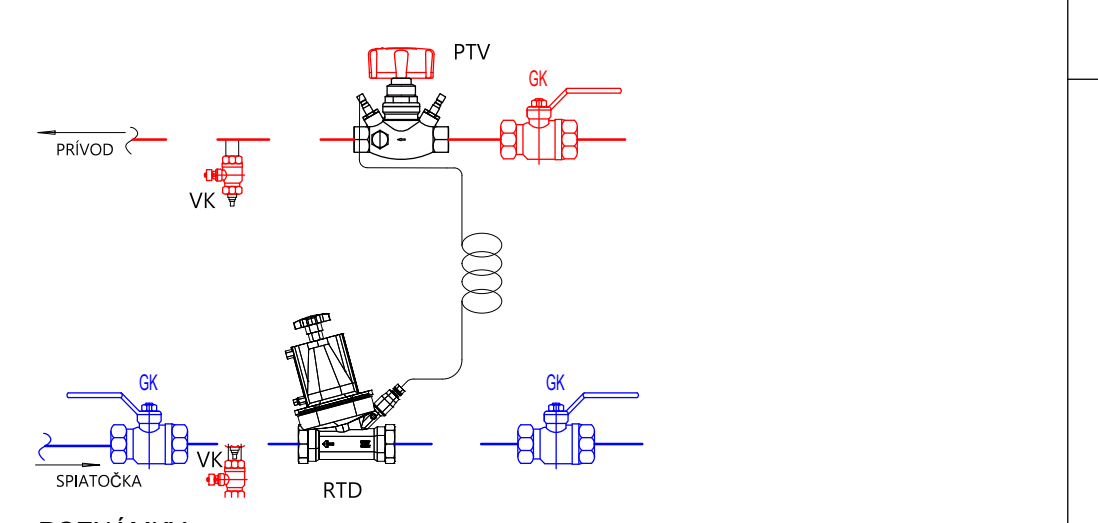

POZNÁMKY:

POTRUBIA A SPÁDOVANIE - Všetky potrubia ÚK a chladenia spádovať v smere prúdenia k najnižším bodom systému pod spádom min. 0,2 %. V najvyšších bodoch rozvodov osadiť automatické odvzdušňovacie ventily, v najnižších bodoch vypúšťacie kohúty s hadicovým nástavcom.

TEPELNÁ IZOLÁCIA POTRUBIA- Všetky potrubné rozvody tepla/chladu celoplošne a súvisle zaizolovať parotesnou elastomérnou izoláciou na báze syntetického kaučuku. Hrúbka izolácie musí byť dimenzovaná podľa priemeru potrubia v zmysle vyhlášky č. 14/2016 Z. z. (minimálne hrúbky pre vykurovanie) a zároveň musí bezpečne zabrániť vzniku kondenzátu v režime chladenia (min. hrúbka 13 mm pre DN 15–25, min. 19 mm pre DN 32 a väčšie, resp. podľa výpočtu pre dané prostredie).

FANCOILOVÉ JEDNOTKY A ZAPOJENIE - Pred montážou fancoilových jednotiek skontrolovať presný typ, výkon a orientáciu pripojenia podľa PD a dodávky stavby. Pripojenie fancoilu na pevné potrubné rozvody vyhotoviť pomocou nerezových vlnovcových potrubí z dôvodu eliminácie prenosu vibrácií a hluku do potrubnej siete. Pred každou fancoilovou jednotkou osadiť armatúry podľa PD.

SADA ČÍSLO

±0,000 = ÚROVEŇ PODLAHY 1.NP

Objednávateľ: Trenčiansky samosprávny kraj, K dolnej stanici 7282/20A, 911 01 Trenčín,
Tre
Generálny projekt
Kontroloval: Ing.
Kraj: Trenčiansky
Investor: Trenčian
Trenčian
Miesto stavby: k.ú
15
Stupeň PD:
Akcia:
Objekt: SO 20
Obsah: Schém