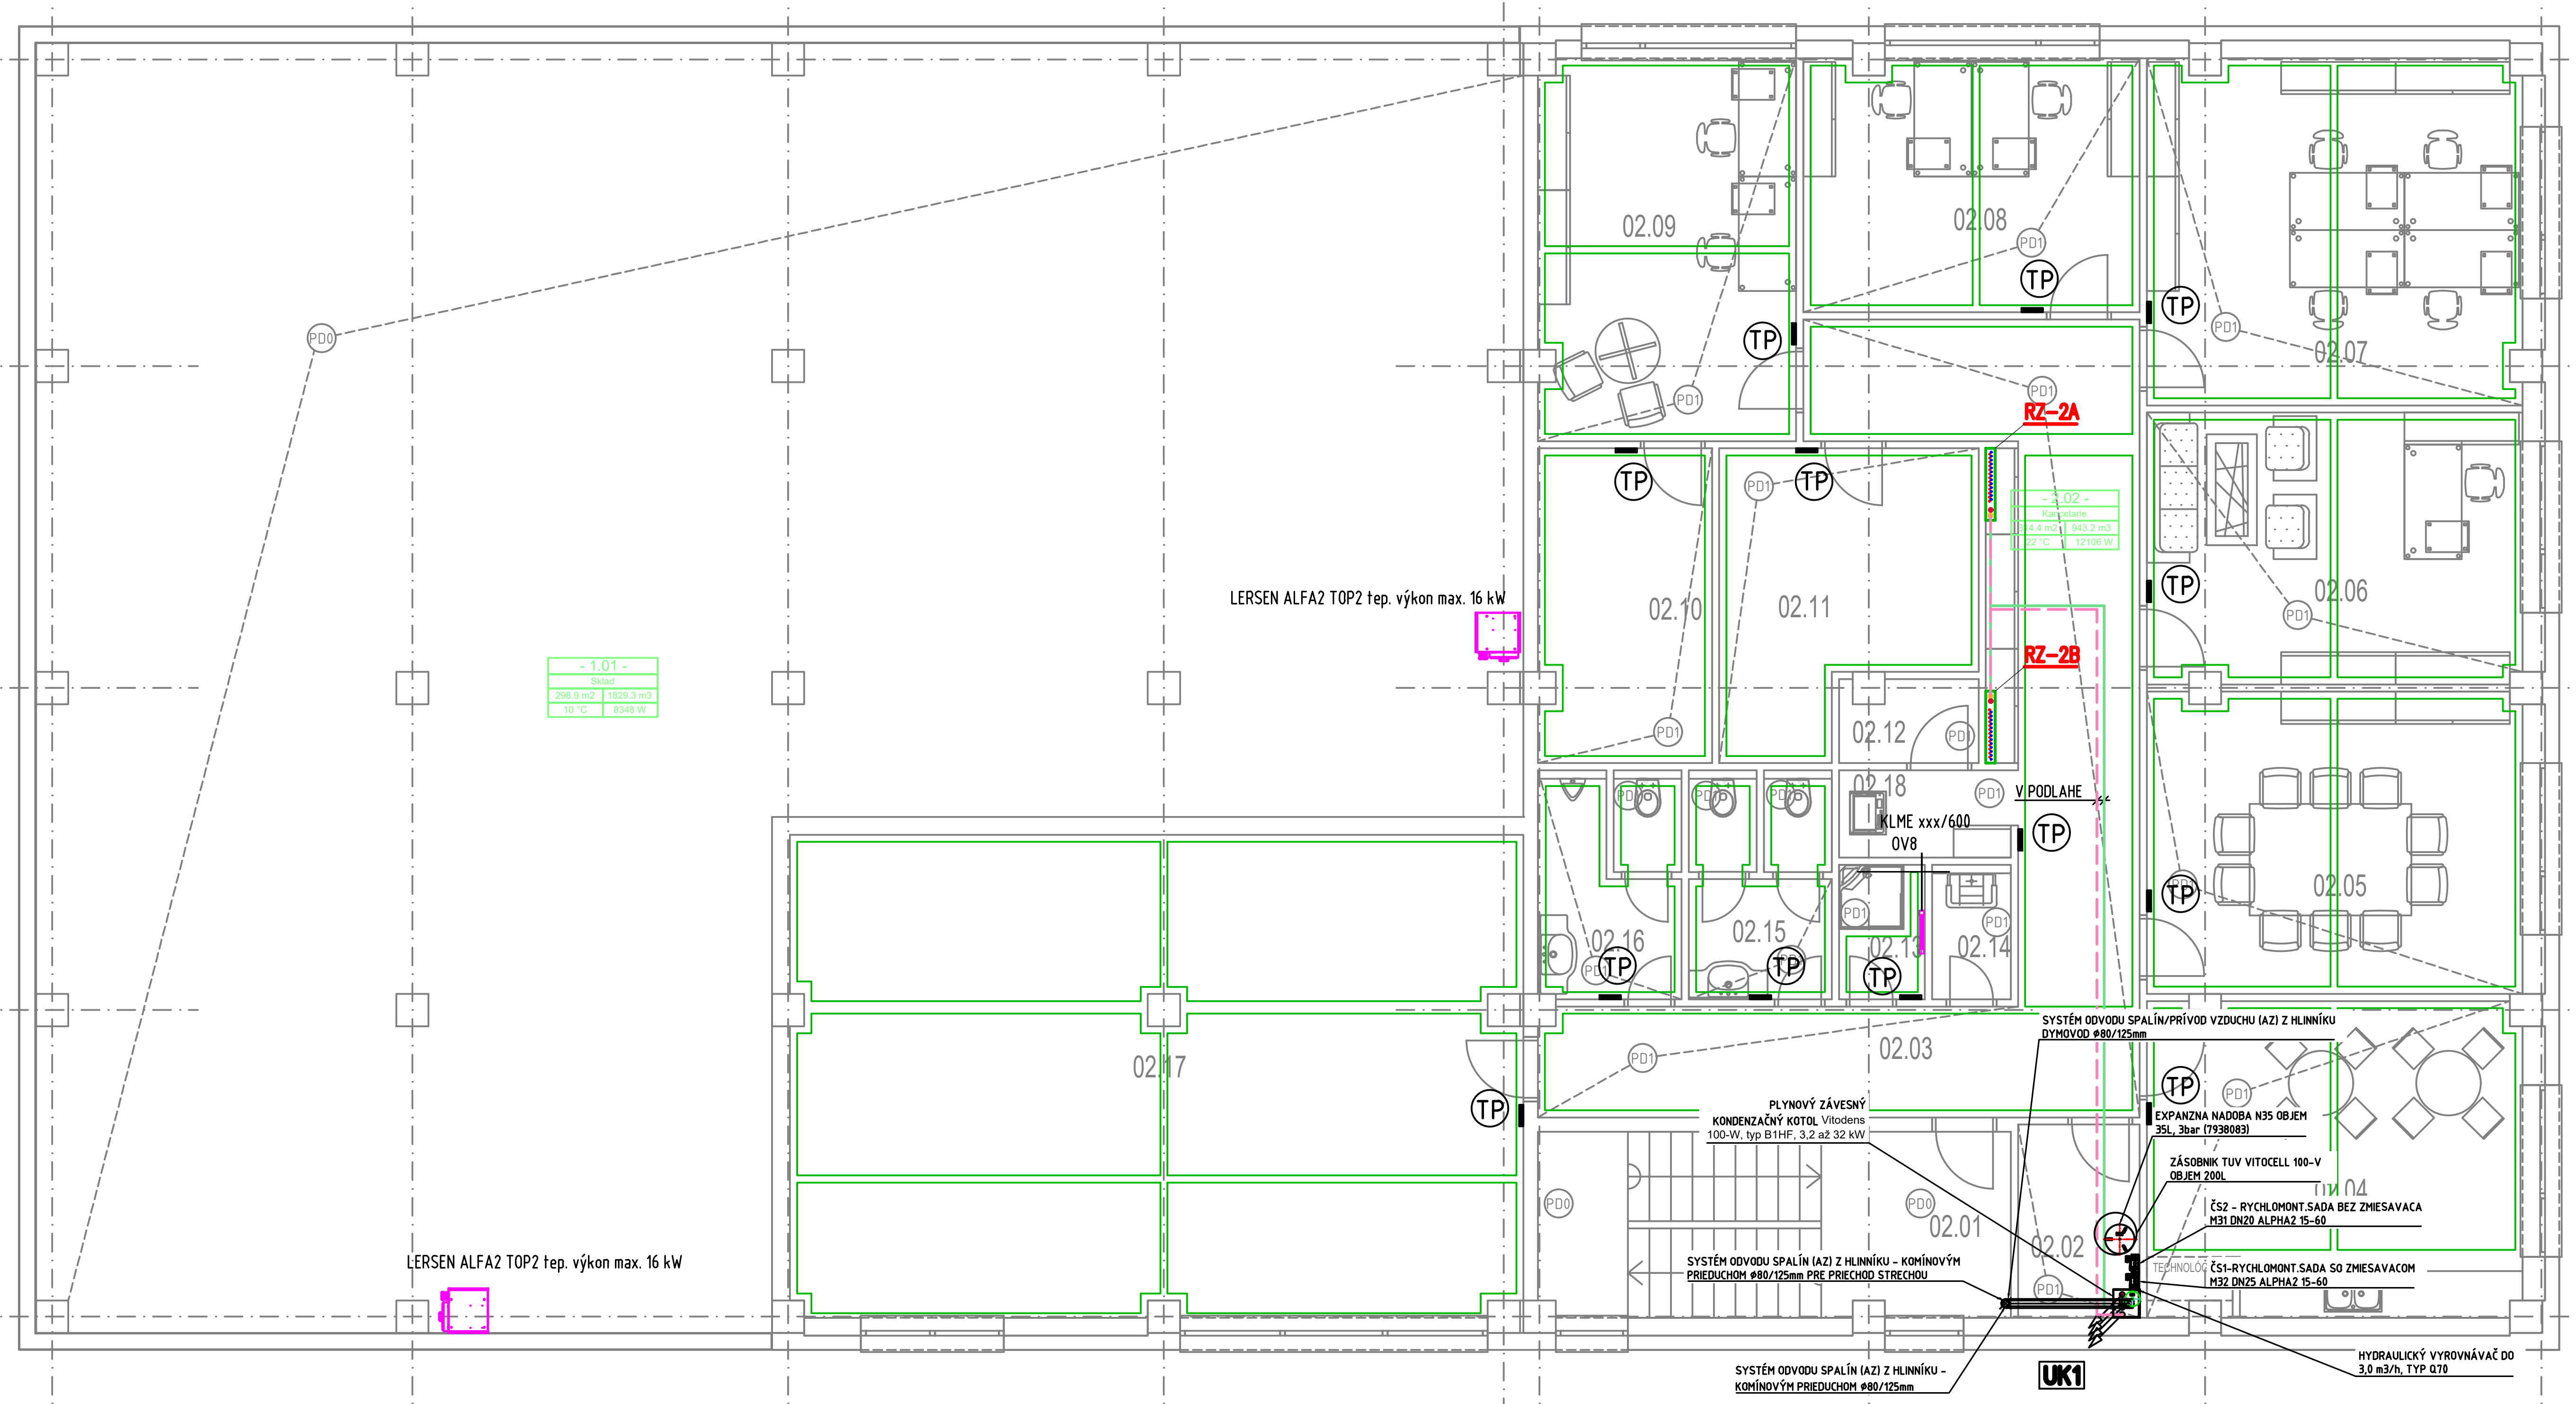
02.09
02.08
02.07
02.10
02.11
RZ-2A
RZ-2B
- 2.02 -
Kancelarie
314.4 m2
943.2 m3
22 °C
12106 W
02.06
02.12
02.18
V PODLAHE
KLME xxx/600
OV8
02.05
02.16
02.15
02.13
02.14
02.17
02.03
02.04
02.01
02.02
TP
PD1
PD0
LERSEN ALFA2 TOP2 tep. výkon max. 16 kW
LERSEN ALFA2 TOP2 tep. výkon max. 16 kW
SYSTÉM ODVODU SPALÍN/PRÍVOD VZDUCHU (AZ) Z HLINNÍKU DYMOVOD ø80/125mm
PLYNOVÝ ZÁVESNÝ KONDENZAČNÝ KOTOL Vitodens 100-W, typ B1HF, 3,2 až 32 kW
EXPANZNA NADOBA N35 OBJEM 35L, 3bar (7938083)
ZÁSOBNIK TUV VITOCELL 100-V OBJEM 200L
ČS2 - RYCHLOMONT.SADA BEZ ZMIESAVACA M31 DN20 ALPHA2 15-60
TECHNOLÓG
ČS1-RYCHLOMONT.SADA SO ZMIESAVACOM M32 DN25 ALPHA2 15-60
SYSTÉM ODVODU SPALÍN (AZ) Z HLINNÍKU - KOMÍNOVÝM PRIEDUCHOM ø80/125mm PRE PRIECHOD STRECHOU
SYSTÉM ODVODU SPALÍN (AZ) Z HLINNÍKU - KOMÍNOVÝM PRIEDUCHOM ø80/125mm
HYDRAULICKÝ VYROVNÁVAČ DO 3,0 m3/h, TYP Q70
UK1

LEGENDA ZARIADENÍ A ARMATÚR :

PS	PRIPÁJACÍ BLOK S INTEGROVANÝM TERMOSTATICKÝM VENTILOM TYP BB PRE VYKUROVACIE TELESÁ SO STREDOVÝM PRIPOJENÍM, ROHOVÉ, DN15, PRIPOJENIE RADIÁTORA VONKAJŠÍ ZÁVIT 1/2", PRIPOJENIE DO STENY VONKAJŠÍ ZÁVIT 3/4" S TERMOSTATICKOU HLAVICOU NAPR. THERA-4 KLASIK S KVAPAL. SNÍMAČOM
GV	GUĽOVÝ VENTIL ZÁVITOVÝ
RV	PREDNASTAVITEĽNÝ REGULAČNÝ VENTIL PRIAMY - STAD
VK	VYPÚŠŤACÍ KOHÚT
OV	ODVZDUŠŇOVACÍ VENTIL
TP	PRIESTOROVÝ REGULÁTOR NEA SMART 2.0 PRE MERANIE TEPLOTY V MIESTNOSTI, FY. REHAU
UK1	STÚPAČKA VYKUROVANIA
TS	Termostat SALUS týdenní programovatelný, 0-230V, 0,5°C, 5A, pro ALFA, SIGMA, ZETA, COMPACT
RZ	ROZDELOVACIA STANICA PRE VYKUROVACIE TELESÁ A PODLAHOVĚ VYKUROVANIE

LAVICOVÉ VYKUROVACIE TELESO KORALINE LDE 300/2000

OCEĽOVÉ DOSKOVÉ VYKUROVACIE TELESO RADIK VK
TYP VENTIL KOMPAKT, S PRAVÝM SPODNÝM PRIPOJENÍM

SPÔSOB ZNAČENIA
22 VK 600/ ...

- STAVEBNÁ DĹŽKA V MILIMETROCH
- STAVEBNÁ VÝŠKA V MILIMETROCH
- PREVEDENIE VENTIL-KOMAPKT
- TYP DVOJRADOVÝ

REBRÍKOVÉ VYKUROVACIE TELESO TYP KORALUX LINEAR MAX-E, FY. KORADO

PLYNOVÝ TEPLOVZDUŠNÝ OHRIEVAČ LERSEN ALFA2 TOP2 tep. výkon max. 16 kW

LEGENDA PODLAHOVÉHO VYKUROVANIA:

PODLAHOVÉ KÚRENIE REHAU

Rúrka RAUTHERM S 17x2,0 VARIONOVA	TYP VYKUROVACEJ RÚRKY SYSTÉM PODLAHOVÉHO VYKUROVANIA

DETAIL ZAPOJENIA VYKUROVACÍCH TELIES
DOSKOVÉ VYKUROVACIE TELESO

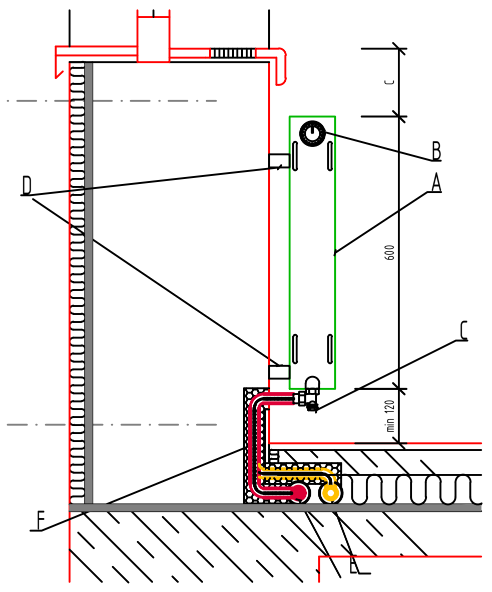
D
B
A
C
F
E
C
600
min 120

DETAIL OSADENIA VYK. TELESA
NA ROZVODY ÚK, M = 1:25

- A OCELOVÉ VYKUROVACIE TELESO TYP VK
- B TERMOSTATICKÁ HLAVICA
- C ROHOVÁ PRIPOJOVACIA ARMATÚRA PRE DVOJTRUBKOVÉ SYSTÉMY
- D DRŽIAK
- E ROZVODY ÚSTREDNÉHO KÚRENIA
- F TRUBICOVÁ IZOLÁCIA

DETAIL ZAPOJENIA VYKUROVACÍCH TELIES
REBRÍKOVÉ VYKUROVACIE TELESO

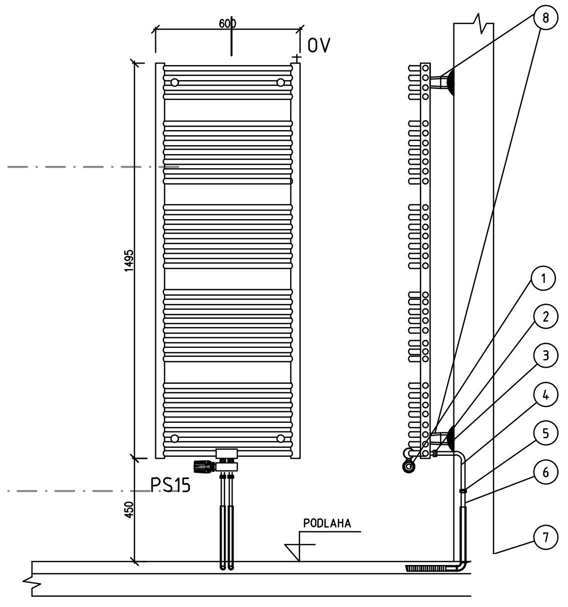
600
OV
1485
PS15
450
PODLAHA
1
2
3
4
5
6
7
8

LEGENDA:

1 Stredové pripojenie vykurovacieho telesa, roz
rohové, farbia biela
2 Svorková spojka
3 Krycia rozeta
4 Pripojovacia garnitúra s upevňovacím
5 Násuvná objímka
6 Vykurovacia rúrka
7 Vodiaci oblúk 90°
8 Stenová konzola

LEGENDA MIESTNOSTÍ 2.N.P

Č.M.	ÚČEL MIESTNOSTI	PLOCHA (m2)	POPIS POVRCHOVÝCH ÚPRAV		
			PODLAHA	STENY	STROPY
02.01	SCHODISKO	17,00	KERAMICKÁ DLAŽBA	SÁDROVÁ OMIETKA	SDK PODHĽAD - PLNÝ
02.02	ARCHÍV	4,59	VINYL	SÁDROVÁ OMIETKA	SDK PODHĽAD - PLNÝ
02.03	CHODBA	36,36	VINYL	SÁDROVÁ OMIETKA	SDK PODHĽAD - PLNÝ
02.04	KUCHYNKA	22,78	VINYL	SÁDROVÁ OMIETKA	SDK PODHĽAD - PLNÝ
02.05	ZASADAČKA	22,07	VINYL	SÁDROVÁ OMIETKA	SDK PODHĽAD - PLNÝ
02.06	KANCELÁRIA RIADITEĽ	19,84	VINYL	KERAM. OBKLAD	SDK PODHĽAD - PLNÝ
02.07	KANCELÁRIA	25,23	VINYL	SÁDROVÁ OMIETKA	SDK PODHĽAD - PLNÝ
02.08	KANCELÁRIA OBCHOD	16,58	VINYL	SÁDROVÁ OMIETKA	SDK PODHĽAD - PLNÝ
02.09	KANCELÁRIA EKONÓM	19,14	VINYL	SÁDROVÁ OMIETKA	SDK PODHĽAD - PLNÝ
02.10	ARCHÍV	10,60	VINYL	SÁDROVÁ OMIETKA	SDK PODHĽAD - PLNÝ
02.11	SKLAD	13,33	VINYL	SÁDROVÁ OMIETKA	SDK PODHĽAD - PLNÝ
02.12	SERVER	2,13	VINYL	SÁDROVÁ OMIETKA	SDK PODHĽAD - PLNÝ
02.13	SPRCHA	2,26	KERAMICKÁ DLAŽBA	SÁDROVÁ OMIETKA	SDK PODHĽAD - PLNÝ
02.14	UPRATOVAČKA	2,07	KERAMICKÁ DLAŽBA	SÁDROVÁ OMIETKA	SDK PODHĽAD - PLNÝ
02.15	WC ŽENY	6,40	KERAMICKÁ DLAŽBA	SÁDROVÁ OMIETKA	SDK PODHĽAD - PLNÝ
02.16	WC MUŽI	6,40	KERAMICKÁ DLAŽBA	SÁDROVÁ OMIETKA	SDK PODHĽAD - PLNÝ
02.17	VOĽNÝ PRIESTOR	68,60	VINYL	SÁDROVÁ OMIETKA	SDK PODHĽAD - PLNÝ
02.18	COPY POINT	3,00	VINYL	SÁDROVÁ OMIETKA	SDK PODHĽAD - PLNÝ

LEGENDA POTRUBIA:

POTRUBIE - PLASTHLINNÍKOVÁ RÚRKA NAPR. GEBERIT MEPLA
SPÁJANÉ LISOVANÍM, IZOLOVANÉ POTRUBIE, TEPLOTNÝ SPÁD 70/50°C
POTRUBIE VEDENÉ POD STROPOM, PRE RADIATORI, PRÍVOD A SPIATOČKA

POTRUBIE - PLASTHLINNÍKOVÁ RÚRKA NAPR. GEBERIT MEPLA
SPÁJANÉ LISOVANÍM, IZOLOVANÉ POTRUBIE, TEPLOTNÝ SPÁD 45/35°C
POTRUBIE VEDENÉ V PODLAHE, V ŠACHTE, PRE PODLAHOVÉ VYKUROVANIE, PRÍVOD A SPIATOČKA

POZNÁMKA :

- V PRÍPADE NEJASNOSTÍ VO VÝKRESOVEJ DOKUMENTÁCIÍ KONTAKTOVAŤ ZODPOVEDNÉHO PROJEKTANTA
- VŠETKY ROZMERY STAVEBNÝCH PRÁC KONTROLOVAŤ NA MIESTE STAVBY
- PRED UVEDENÍM SYSTÉMU DO PREVÁDZKY JE POTREBNÉ VYKONAŤ DÔKLADNÝ PREPLACH SYSTÉMU S VYČISTENÍM VŠETKÝCH FILTROV NA ROZVODE
- PO NAPUSTENÍ SYSTÉMU JE POTREBNÉ VYKONAŤ JEHO ODVZDUŠNENIE
- DODÁVATEL STAVBY JE POVINNÝ REALIZOVAŤ VŠETKY PRÁCE V ZMYSLE PLATNÝCH STN EN S DODRŽANÍM TECHNOLOGICKÝCH A BEZPEČNOSTNÝCH POSTUPOV. ĎALEJ JE POVINNÝ REŠPEKTOVAŤ USTANOVENIÁ STN 730421 O PRÍSLUŠNÝCH ROZMEROVÝCH ODCHÝLKACH REALIZOVANÝCH KONŠTRUKCIÍ PROTI PROJEKTOVANÉMU STAVU. KAŽDÚ ODCHÝLKU OD PROJEKTU JE POTREBNÉ PREROKOVAŤ S GP.
- PRESTUPY INŽINIERSKYCH SIETÍ A ROZVODOV V OBJEKTE JE POTREBNÉ VYNECHAŤ PRI REALIZÁCII STAVBY.
- PROJEKTOVÁ DOKUMENTÁCIA JE SPRACOVANÁ PRE ÚČEL VYDANIA STAVEBNÉHO POVOLENIA A NENAHRÁDZA REALIZAČNÝ PROJEKT